


План на відм. -3,300. Секція №1 по ГП, М 1:100

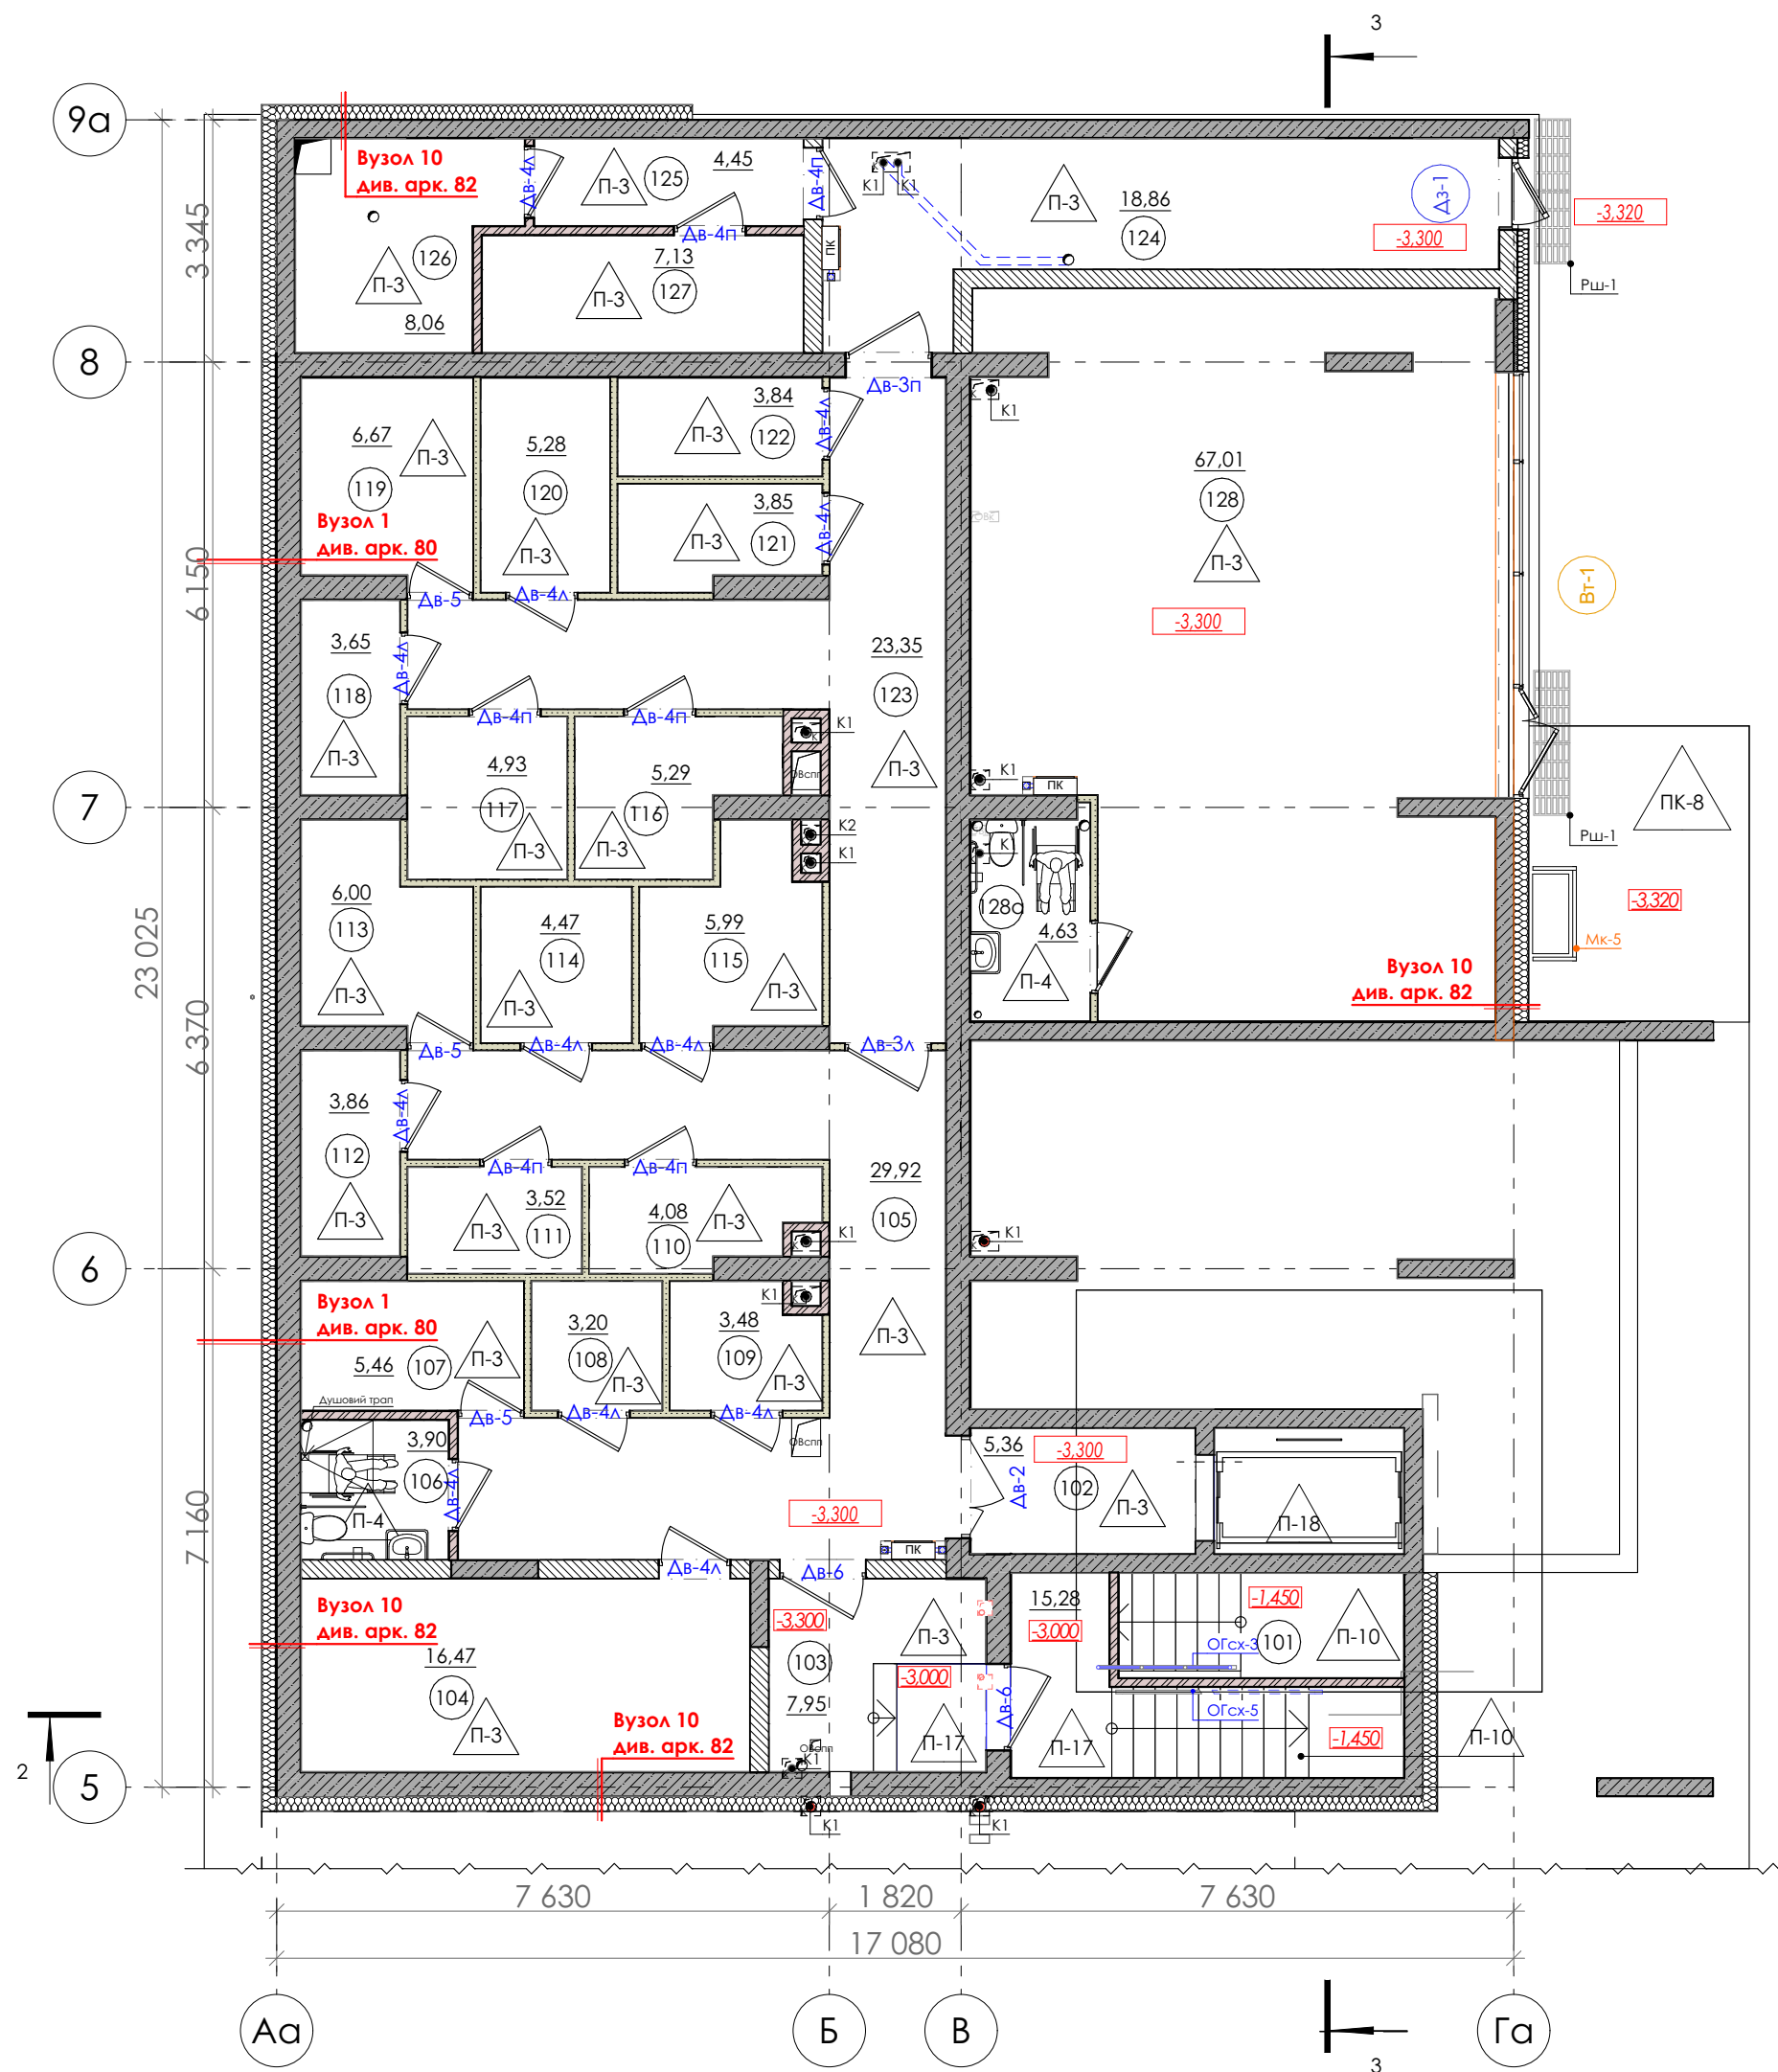


Умовні позначення:

- Монолітні з/б стіни, пілони, колони
- Стіни та перегородки з керамічного блоку 2НФ 2,12 - 250мм, 120мм
- Стіни та перегородки з цегли - 250мм, 120мм
- Стіни та перегородки з мучкоблоку - 250мм, 100мм
- Контури балок
- Вентканали
- Підключення до вентиляційного каналу
- Підключення до димоходу
- Підключення до К1
- Побутова каналізація
- Ливнева каналізація
- Відвід води від кондиціонерів
- Відмітка рівня підлоги
- Номер приміщення місць загального користування (МЗК) або нежитлового
- Номер приміщення квартири
- Тип підлоги/покрівлі
- Напрямі ухил стоку води
- Типи квартири
- Житлова площа квартири
- Площа квартири
- Загальна площа квартири
- Маркування зовнішніх/внутрішніх дверей
- Маркування вікон/балконних блоків
- Маркування ревізійних дверцят
- Маркування корзин кондиціонерів
- Маркування огороження балконів
- Маркування огороження сходів
- Маркування фасонних елементів
- Вузли


Експлікація приміщень цокольного поверху С1				
Тип	№ п.п.	Найменування	Площа	Прим.
1.1. Приміщення загального користування				
	101	Сходові клітки Н1	15,28	
	102	Ліфтовий хол	5,36	
	124	Коридор	18,86	
			39,50 м²	
1.2. СПП (190 осіб)				
	103	Тамбур	7,95	
	104	Фільтровентиляційне приміщення	16,47	
	105	Коридор	29,92	
	106	Сан. приміщення	3,90	
	107	Комора	5,46	
	108	Комора	3,20	
	109	Комора	3,48	
	110	Комора	4,08	
	111	Комора	3,52	
	112	Комора	3,86	
	113	Комора	6,00	
	114	Комора	4,47	
	115	Комора	5,99	
	116	Комора	5,29	
	117	Комора	4,93	
	118	Комора	3,65	
	119	Комора	6,67	
	120	Комора	5,28	
	121	Комора	3,85	
	122	Комора	3,84	
	123	Коридор	23,35	
			155,16 м²	
1.3. Комерційне приміщення				
	128	Торгівельне приміщення	67,01	
	128а	Санвузол	4,63	
			71,64 м²	
1.4. Приміщення технічні				
	125	Коридор	4,45	
	126	Технічне приміщення (вузол вводу)	8,06	
	127	Технічне приміщення (електрощитова)	7,13	
			19,64 м²	
			285,94 м²	

Блок-схема
Черга 1.
Пусковий комплекс №1.
Будинок №1

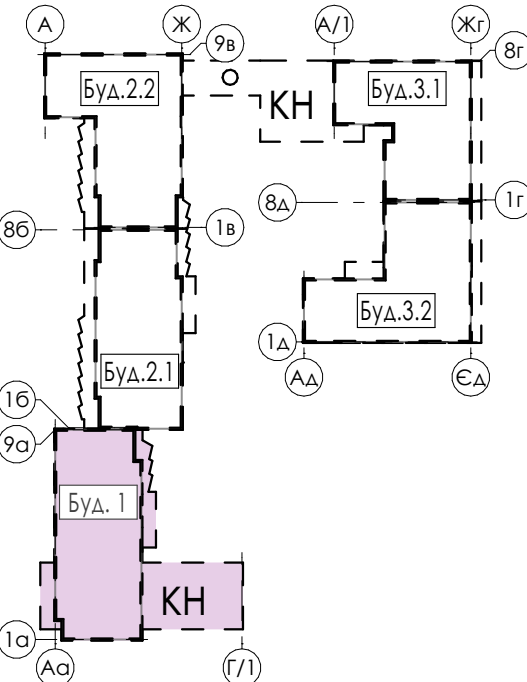

ТР Специфікація придверних решіток на відм. -3,300						
Марка	Найменування	Вигляд	Кількість	Розміри	Виробник	Примітки
РШ-1	Брудодісна решітка		4	1000 x 500	ACO Vario	Алюмінієва з гумовим покриттям

Маркувальний план на відм.+0,500. М 1:100

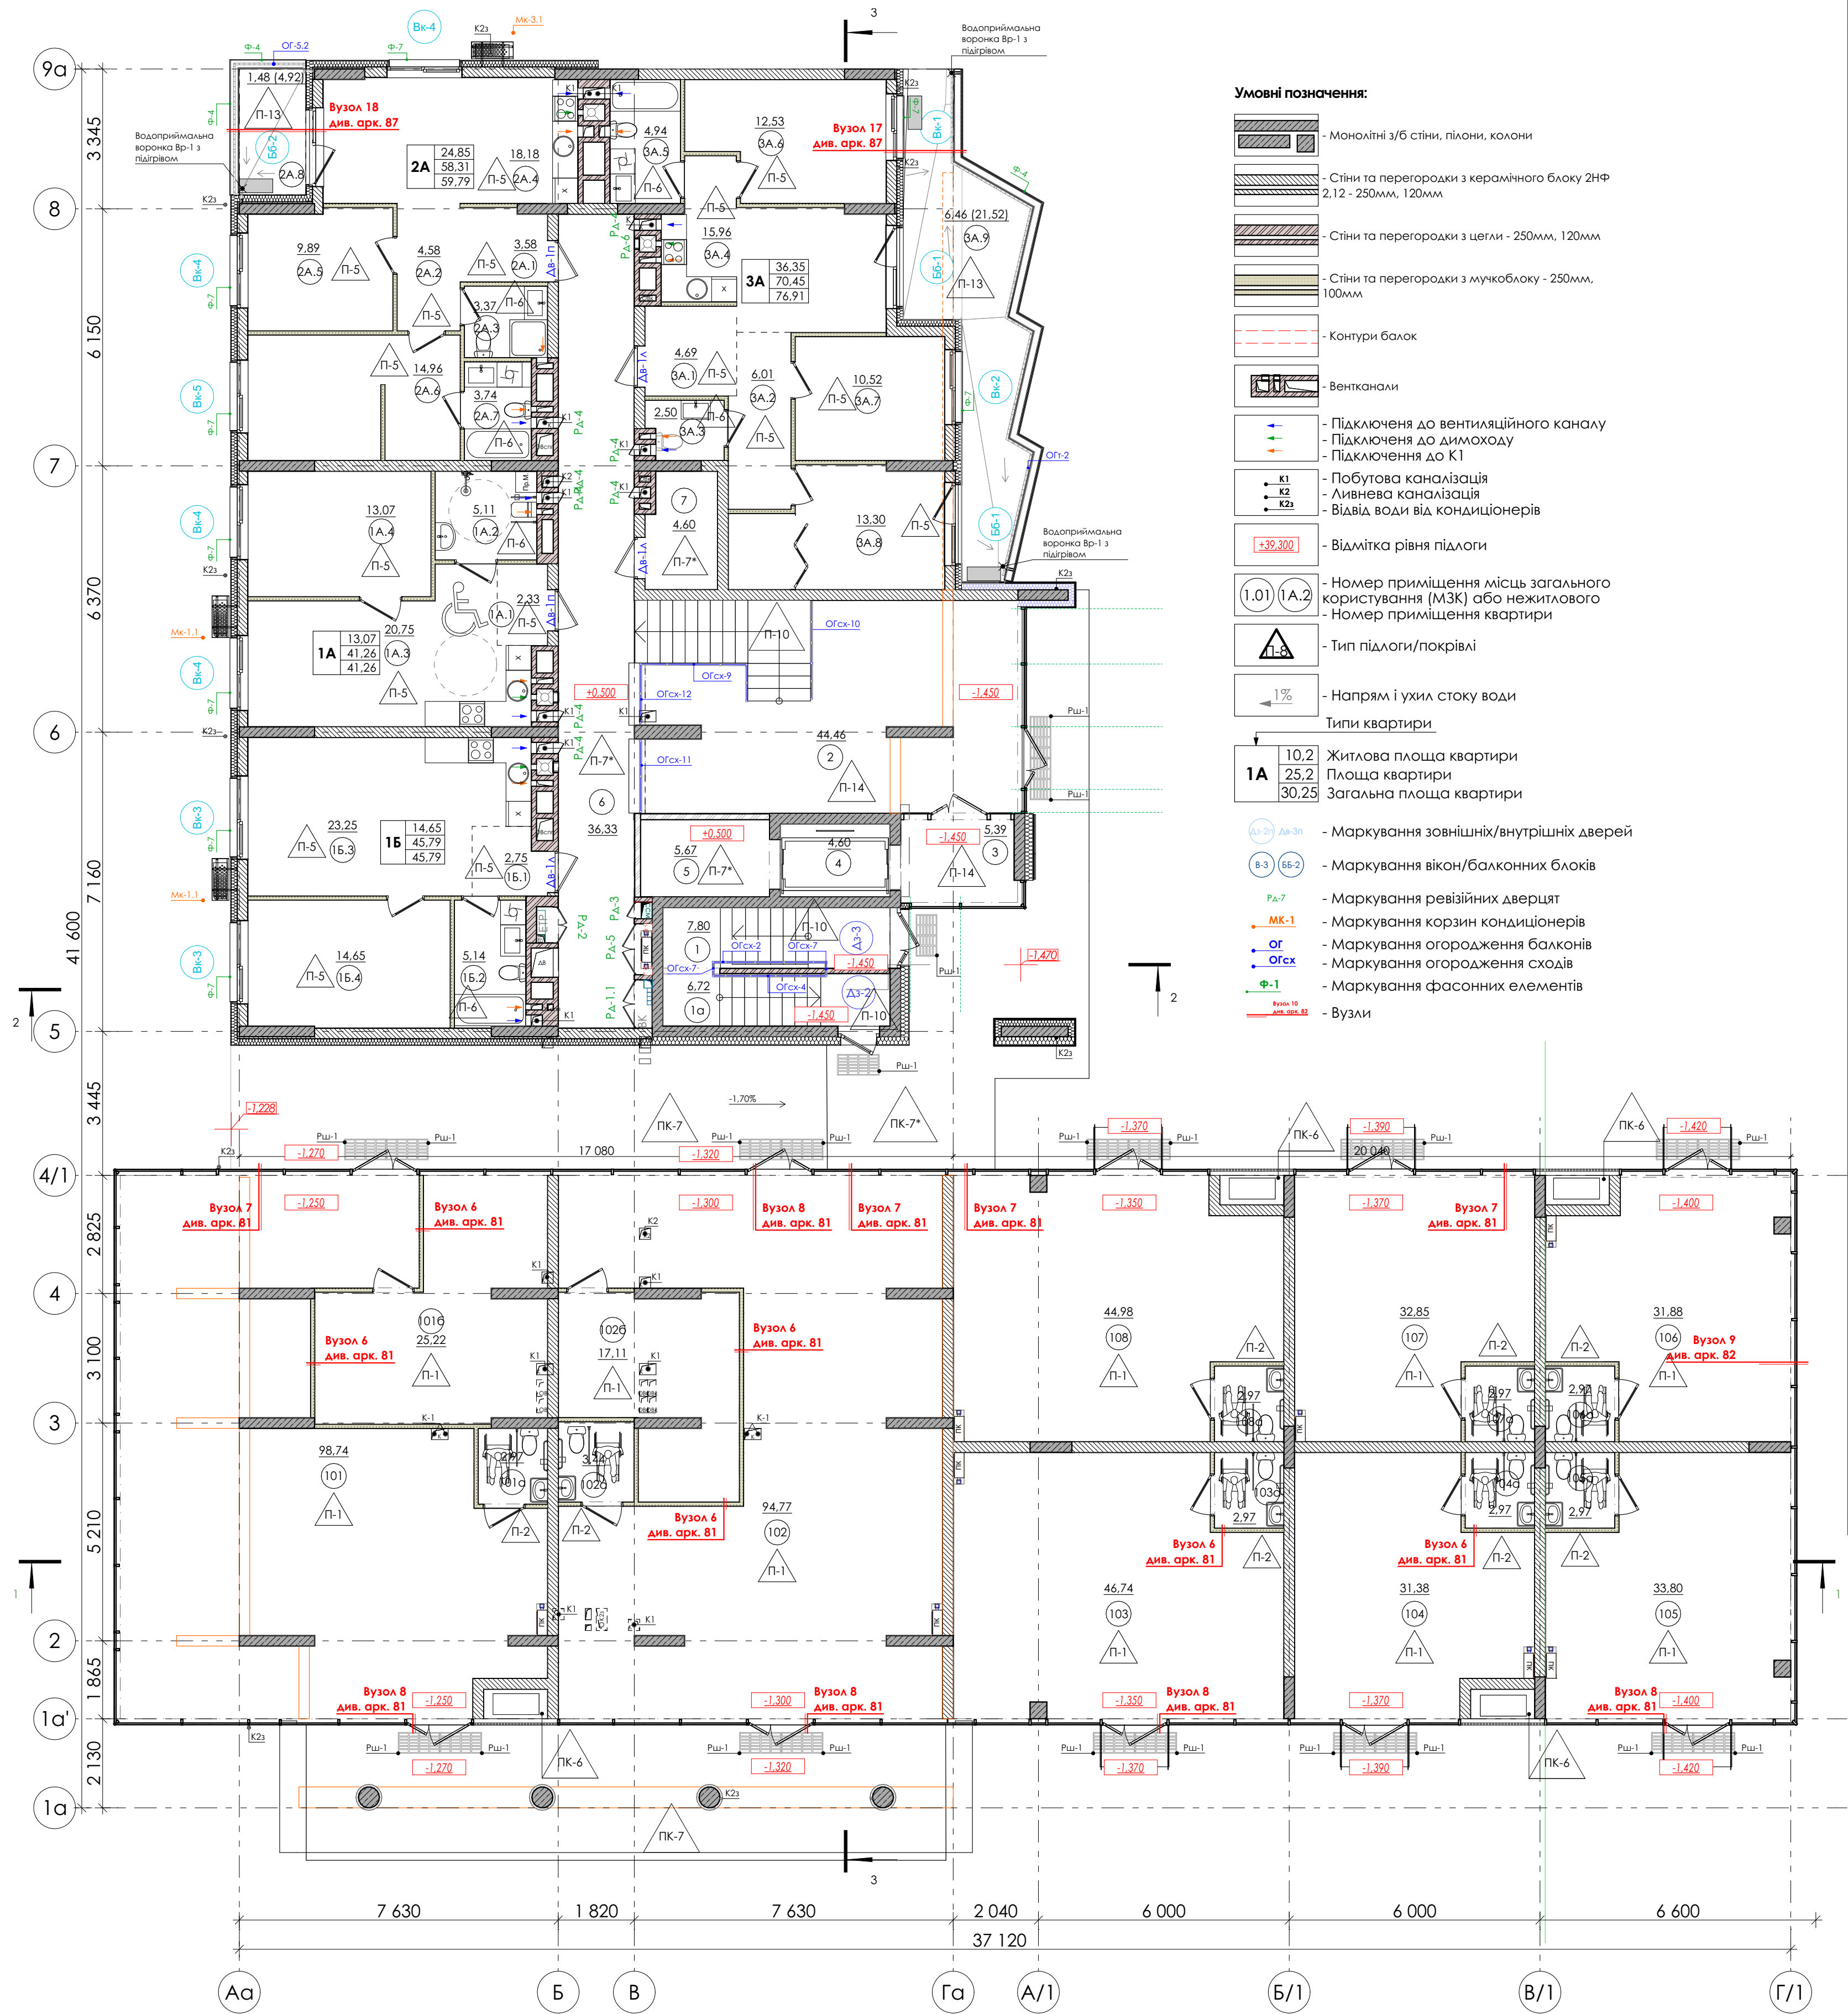


Умовні позначення:

- Монолітні з/б стіни, пілони, колони
- Стіни та перегородки з керамичного блоку 2НФ 2,12 - 250мм, 120мм
- Стіни та перегородки з цегли - 250мм, 120мм
- Стіни та перегородки з мукоблоку - 250мм, 100мм
- Контури балок
- Вентканалы
- Підключення до вентиляційного каналу
- Підключення до димоходу
- Підключення до К1
- Побутова каналізація
- Ливнева каналізація
- Відвід води від кондиціонерів
- Відмітка рівня підлоги
- Номер приміщення місць загального користування (МЗК) або нежитлового
- Номер приміщення квартири
- Тип підлоги/покрівлі
- Напрямок і ухил стоку води
- Типи квартири
- Житлова площа квартири
- Площа квартири
- Загальна площа квартири
- Маркування зовнішніх/внутрішніх дверей
- Маркування вікон/балконних блоків
- Маркування ревізійних дверцят
- Маркування корзин кондиціонерів
- Маркування огороження балконів
- Маркування огороження сходів
- Маркування фасонних елементів
- Вузли

Експлікація приміщень Секція 1 поверху С1				
Тип	№ п.п.	Найменування	Площа	Прим.
1.1. Приміщення загального користування				
	1	Сходово-каїтка Н1	7,80	
	1а	Сходово-каїтка	6,72	
	2	Хол	44,46	
	3	Ліфтовий хол	5,39	
	4	Ліфт	4,60	
	5	Ліфтовий хол	5,67	
	6	Коридор	36,33	
			110,97 м²	
1.2. Допоміжні приміщення				
	7	Допоміжне приміщення	4,60	
			4,60 м²	
1.3.1. Комерційне приміщення				
	101	Торгівельне приміщення	98,74	
	101а	Санвузол	2,97	
	101б	Допоміжне приміщення	25,22	
			126,93 м²	
1.3.2. Комерційне приміщення				
	102	Торгівельне приміщення	94,77	
	102а	Санвузол	3,44	
	102б	Допоміжне приміщення	17,11	
			115,32 м²	
1.3.3. Комерційне приміщення				
	103	Торгівельне приміщення	46,74	
	103а	Санвузол	2,97	
			49,71 м²	
1.3.4. Комерційне приміщення				
	104	Торгівельне приміщення	31,38	
	104а	Санвузол	2,97	
			34,35 м²	
1.3.5. Комерційне приміщення				
	105	Торгівельне приміщення	33,80	
	105а	Санвузол	2,97	
			36,77 м²	
1.3.6. Комерційне приміщення				
	106	Торгівельне приміщення	31,88	
	106а	Санвузол	2,97	
			34,85 м²	
1.3.7. Комерційне приміщення				
	107	Торгівельне приміщення	32,85	
	107а	Санвузол	2,97	
			35,82 м²	
1.3.8. Комерційне приміщення				
	108	Торгівельне приміщення	44,98	
	108а	Санвузол	2,97	
			47,95 м²	
1А (квартира для МГН)				
	1А.1	Передпокої	2,33	
	1А.2	Суміщений санвузол	5,11	
	1А.3	Кухня-їдальня	20,75	
	1А.4	Спальня	13,07	
			41,26 м²	
1Б				
	1Б.1	Передпокої	2,75	
	1Б.2	Суміщений санвузол	5,14	
	1Б.3	Кухня-їдальня	23,25	
	1Б.4	Спальня	14,65	
			45,79 м²	
2А				
	2А.1	Передпокої	3,58	
	2А.2	Коридор	4,58	
	2А.3	Туалет	3,37	
	2А.4	Кухня-їдальня	18,18	
	2А.5	Спальня	9,89	
	2А.6	Спальня	14,96	
	2А.7	Ванна кімната	3,74	
	2А.8	Балкон	1,48	
			59,78 м²	
3А				
	3А.1	Передпокої	4,69	
	3А.2	Коридор	6,01	
	3А.3	Туалет	2,50	
	3А.4	Кухня-їдальня	15,96	
	3А.5	Суміщений санвузол	4,94	
	3А.6	Спальня	12,53	
	3А.7	Спальня	10,52	
	3А.8	Спальня	13,30	
	3А.9	Балкон	6,46	
			76,91 м²	
			821,01 м²	


Блок-схема
Черга 1. Пусковий комплекс №1.
Будинок №1

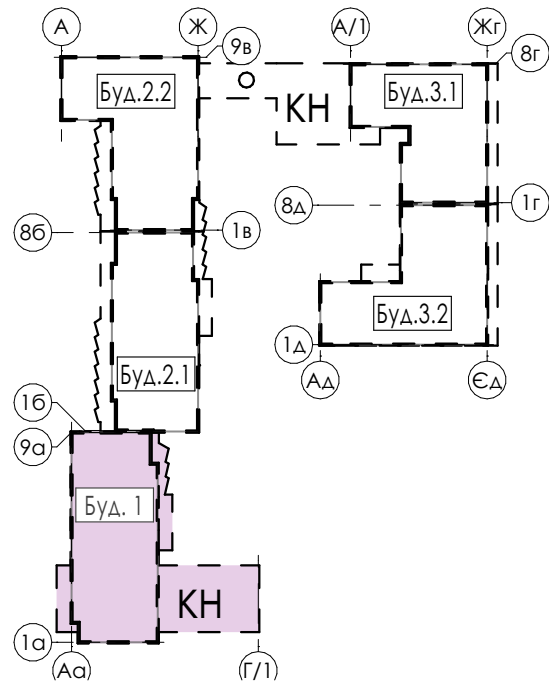

Специфікація воронки на відм. +0,500			
Марка	Найменування	Кількість	Примітки
Вр-1	Воронка водоприймальна з підгірвом	3	Див. розділ ВК


Специфікація брудочисних решіток на відм.+0,500						
Марка	Найменування	Вигляд	Кількість	Розміри	Виробник	Примітки
Рш-1	Брудочисна решітка		24	1000 x 500	ACO Vario	Алюмінієва з гумовим покриттям

Маркувальний план на відм.+3,500. М 1:100

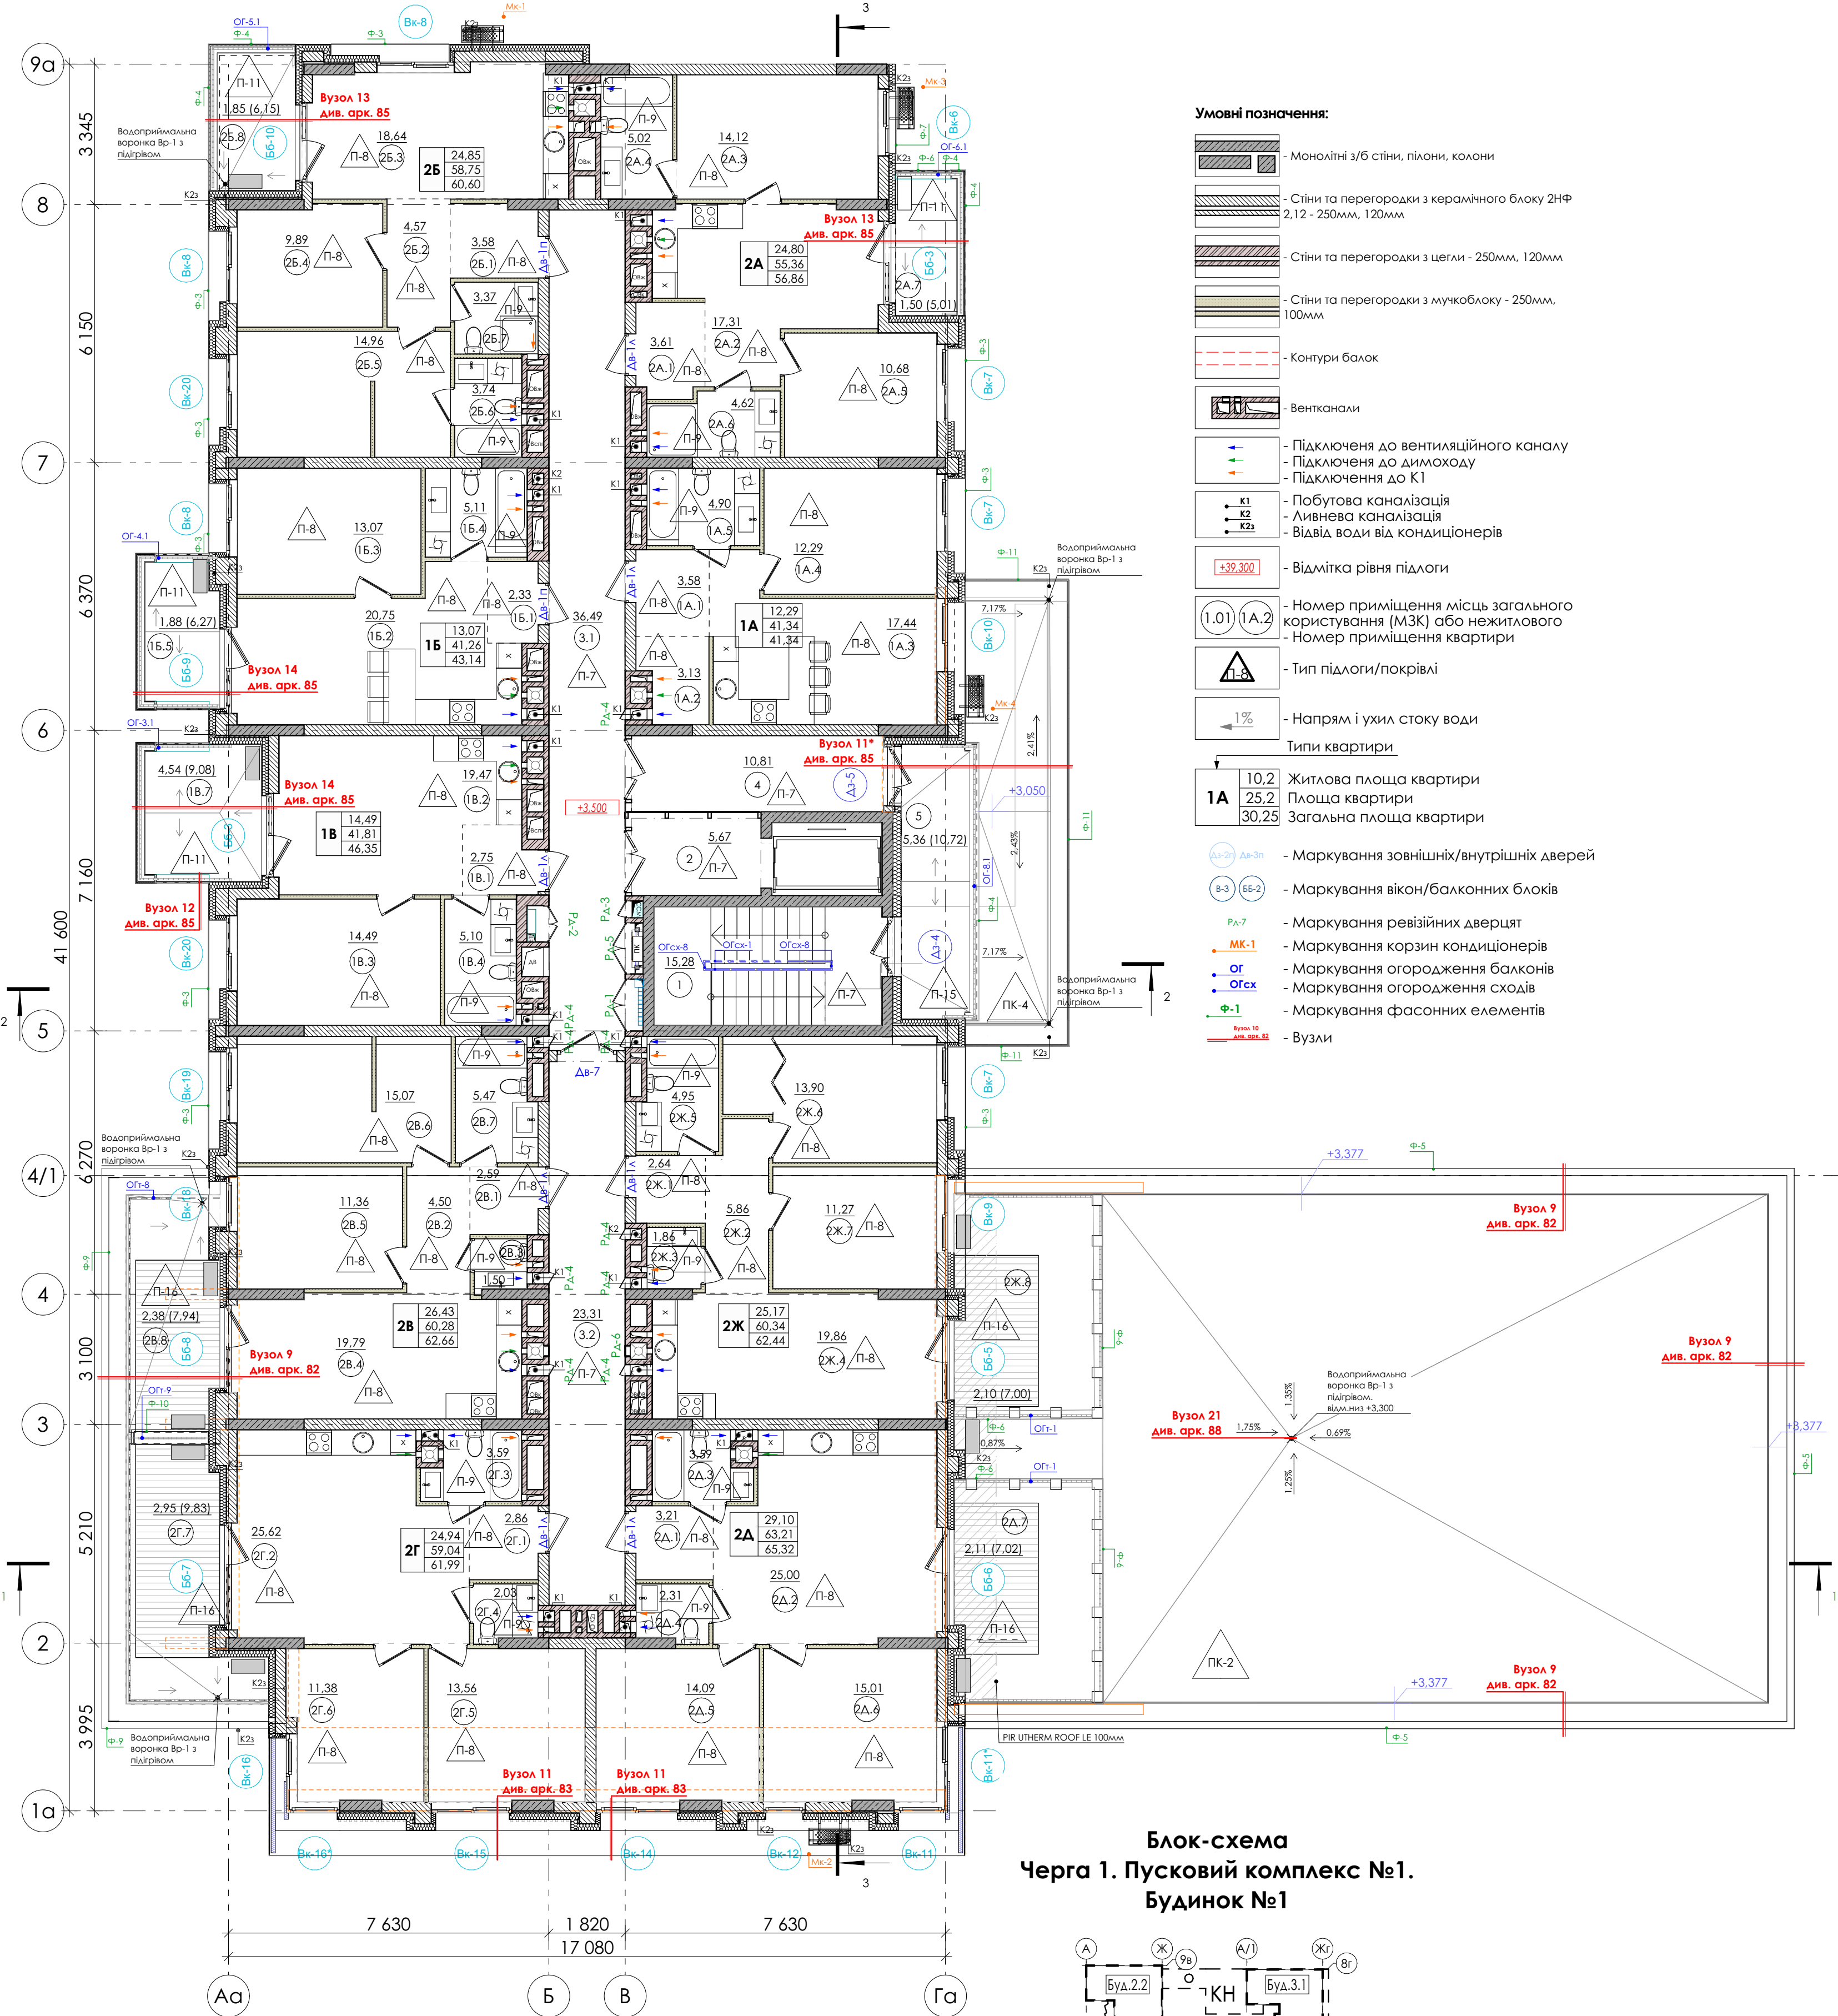

- Умовні позначення:
- Монолітні з/б стіни, пілони, колони
 - Стіни та перегородки з керамічного блоку 2НФ 2,12 - 250мм, 120мм
 - Стіни та перегородки з цегли - 250мм, 120мм
 - Стіни та перегородки з мушкету - 250мм, 100мм
 - Контури балок
 - Вентканалы
 - Підключення до вентиляційного каналу
 - Підключення до димоходу
 - Підключення до К1
 - Побутова каналізація
 - Ливнева каналізація
 - Відвід води від кондиціонерів
 - Відмітка рівня підлоги
 - Номер приміщення місць загального користування (МЗК) або нежитлового
 - Номер приміщення квартири
 - Тип підлоги/покрівлі
 - Напрямок і ухил стоку води
 - Типи квартири
 - Житлова площа квартири
 - Площа квартири
 - Загальна площа квартири
 - Маркування зовнішніх/внутрішніх дверей
 - Маркування вікон/балконних блоків
 - Маркування ревізійних дверцят
 - Маркування корзин кондиціонерів
 - Маркування огороження балконів
 - Маркування огороження сходів
 - Маркування фасонних елементів
 - Вузли

Блок-схема
Черга 1. Пусковий комплекс №1.
Будинок №1

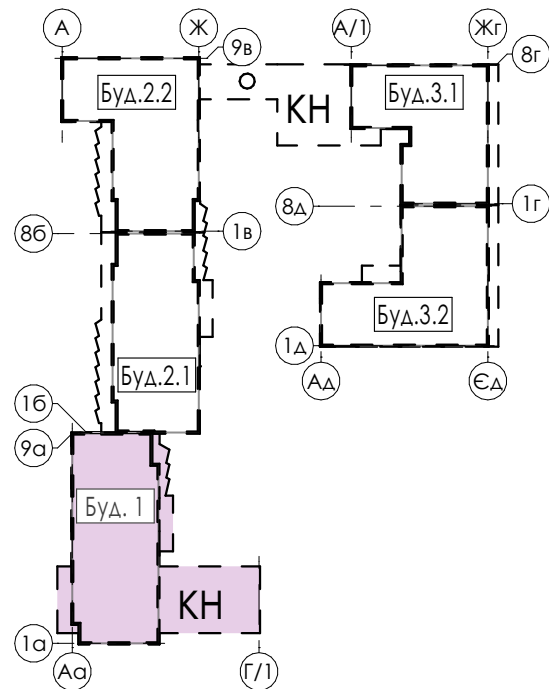

Е1 Експлікація приміщень Секція 1 2ий поверх				
Тип	№ п.п.	Найменування	Площа	Прим.
1. Приміщення загального користування				
	1	Сходово-каліткі Н1	15,28	
	2	Ліфтовий хол	5,67	
	3.1	Коридор	36,49	
	3.2	Коридор	23,31	
	4	Коридор	10,81	
	5	Лоджія	10,72	
			102,28 м²	
1А				
	1А.1	Передпокій	3,58	
	1А.2	Гардероб	3,13	
	1А.3	Кухня-їдальня	17,44	
	1А.4	Спальня	12,29	
	1А.5	Суміщений санвузол	4,90	
			41,34 м²	
1Б				
	1Б.1	Передпокій	2,33	
	1Б.2	Кухня-їдальня	20,75	
	1Б.3	Спальня	13,07	
	1Б.4	Суміщений санвузол	5,11	
	1Б.5	Балкон	1,88	
			43,14 м²	
1В				
	1В.1	Передпокій	2,75	
	1В.2	Кухня-їдальня	19,47	
	1В.3	Спальня	14,49	
	1В.4	Суміщений санвузол	5,10	
	1В.7	Лоджія	4,54	
			46,35 м²	
2А				
	2А.1	Передпокій	3,61	
	2А.2	Кухня-їдальня	17,31	
	2А.3	Спальня	14,12	
	2А.4	Суміщений санвузол	5,02	
	2А.5	Спальня	10,68	
	2А.6	Ванна кімната	4,62	
	2А.7	Балкон	2,50	
			57,86 м²	
2Б				
	2Б.1	Передпокій	3,58	
	2Б.2	Коридор	4,57	
	2Б.3	Кухня-їдальня	18,64	
	2Б.4	Спальня	9,89	
	2Б.5	Спальня	14,96	
	2Б.6	Ванна кімната	3,74	
	2Б.7	Туалет	3,37	
	2Б.8	Балкон	1,85	
			60,60 м²	
2Г				
	2Г.1	Передпокій	2,59	
	2Г.2	Коридор	4,50	
	2Г.3	Туалет	1,50	
	2Г.4	Кухня-їдальня	19,79	
	2Г.5	Спальня	11,36	
	2Г.6	Спальня	15,07	
	2Г.7	Суміщений санвузол	5,47	
	2Г.8	Балкон	2,38	
			62,66 м²	
2А				
	2А.1	Передпокій	3,21	
	2А.2	Кухня-їдальня	25,00	
	2А.3	Ванна кімната	3,59	
	2А.4	Туалет	2,31	
	2А.5	Спальня	14,09	
	2А.6	Спальня	15,01	
	2А.7	Балкон	2,11	
			65,32 м²	
2Ж				
	2Ж.1	Передпокій	2,64	
	2Ж.2	Коридор	5,86	
	2Ж.3	Туалет	1,86	
	2Ж.4	Кухня-їдальня	19,86	
	2Ж.5	Суміщений санвузол	4,95	
	2Ж.6	Спальня	13,90	
	2Ж.7	Спальня	11,27	
	2Ж.8	Балкон	2,10	
			62,44 м²	
			603,98 м²	

Специфікація водоприймальних ворон на відм.+3,500			
Марка	Найменування	Кількість	Примітки
Вр-1	Воронка водоприймальна з підігрівом	6	Див. розділ ВК

1	Підставка універсальна для кондиціонеру 1000x400x350h	1 шт.	До встановлення покрівлі встановити підставку для кондиціонеру.
---	---	-------	---




- 
 - Номер приміщення місць загального користування (МЗК) або нежитлового
 - Номер приміщення квартири
 - 
 - Тип підлоги/покрівлі
 - 
 - Напрямок і ухил стоку води
 - Типи квартири

1A	10,2
	25,2
	30,25

 - Житлова площа квартири
 - Площа квартири
 - Загальна площа квартири
 - 
 - Маркування зовнішніх/внутрішніх дверей
 - 
 - Маркування вікон/балконних блоків
 - 
 - Маркування ревізійних дверцят
 - 
 - Маркування корзин кондиціонерів
 - 
 - Маркування огороження балконів
 - 
 - Маркування огороження сходів
 - 
 - Маркування фасонних елементів
 - 
 - Вузли

Експлікація приміщень типового поверху С1				
Тип	№ п.п.	Найменування	Площа	Прим.
1. Приміщення загального користування				
	1	Сходово клітка Н1	15,28	
	2	Ліфтовий хол	5,69	
	3.1	Коридор	36,50	
	3.2	Коридор	23,29	
	4	Коридор	10,86	
	5	Лоджія	10,73	
			102,35 м²	
1А				
	1А.1	Передпокій	5,07	
	1А.2	Гардероб	2,90	
	1А.3	Суміщений санвузол	4,90	
	1А.4	Кухня-їдальня	15,96	
	1А.5	Спальня	12,29	
	1А.6	Балкон	1,46	
			42,58 м²	
1Б				
	1Б.1	Передпокій	2,33	
	1Б.2	Суміщений санвузол	5,11	
	1Б.3	Кухня-їдальня	20,75	
	1Б.4	Спальня	13,07	
	1Б.5	Балкон	1,88	
				43,14 м²
1В				
	1В.1	Передпокій	2,75	
	1В.2	Суміщений санвузол	5,10	
	1В.3	Кухня-їдальня	19,47	
	1В.5	Спальня	14,49	
	1В.7	Лоджія	4,54	
				46,35 м²
2А				
	2А.1	Передпокій	3,61	
	2А.2	Ванна кімната	4,62	
	2А.3	Кухня-їдальня	17,32	
	2А.4	Спальня	10,66	
	2А.5	Спальня	14,12	
	2А.6	Суміщений санвузол	5,02	
	2А.7	Балкон	1,50	
				56,85 м²
2Б				
	2Б.1	Передпокій	3,59	
	2Б.2	Коридор	4,57	
	2Б.3	Туалет	3,37	
	2Б.4	Кухня-їдальня	18,64	
	2Б.5	Спальня	9,88	
	2Б.6	Спальня	14,96	
	2Б.7	Ванна кімната	3,74	
	2Б.8	Балкон	1,85	
				60,60 м²
2В				
	2В.1	Передпокій	2,60	
	2В.2	Коридор	4,50	
	2В.3	Суміщений санвузол	5,47	
	2В.4	Туалет	1,51	
	2В.5	Кухня-їдальня	19,79	
	2В.6	Спальня	11,34	
	2В.7	Спальня	15,07	
	2В.8	Балкон	1,63	
				61,91 м²
2Г				
	2Г.1	Передпокій	2,86	
	2Г.2	Ванна кімната	3,59	
	2Г.3	Туалет	2,03	
	2Г.4	Кухня-їдальня	25,62	
	2Г.5	Спальня	13,56	
	2Г.6	Спальня	11,38	
	2Г.7	Балкон	1,95	
				60,99 м²
2Д				
	2Д.1	Передпокій	3,21	
	2Д.2	Ванна кімната	3,59	
	2Д.3	Туалет	2,31	
	2Д.4	Кухня-їдальня	25,00	
	2Д.5	Спальня	14,09	
	2Д.6	Спальня	15,01	
	2Д.7	Балкон	1,54	
				64,75 м²
2Ж				
	2Ж.1	Передпокій	2,64	
	2Ж.2	Коридор	5,86	
	2Ж.3	Суміщений санвузол	4,95	
	2Ж.4	Туалет	1,86	
	2Ж.5	Кухня-їдальня	19,86	
	2Ж.6	Спальня	13,90	
	2Ж.7	Спальня	11,27	
	2Ж.8	Балкон	1,43	
				61,77 м²
			601,29 м²	

Специфікація воронки типового поверху на відм.+6,500			
Марка	Найменування	Кількість	Примітки
Вр-1	Воронка водоприймальна з підірвом	1	Див. розділ ВК

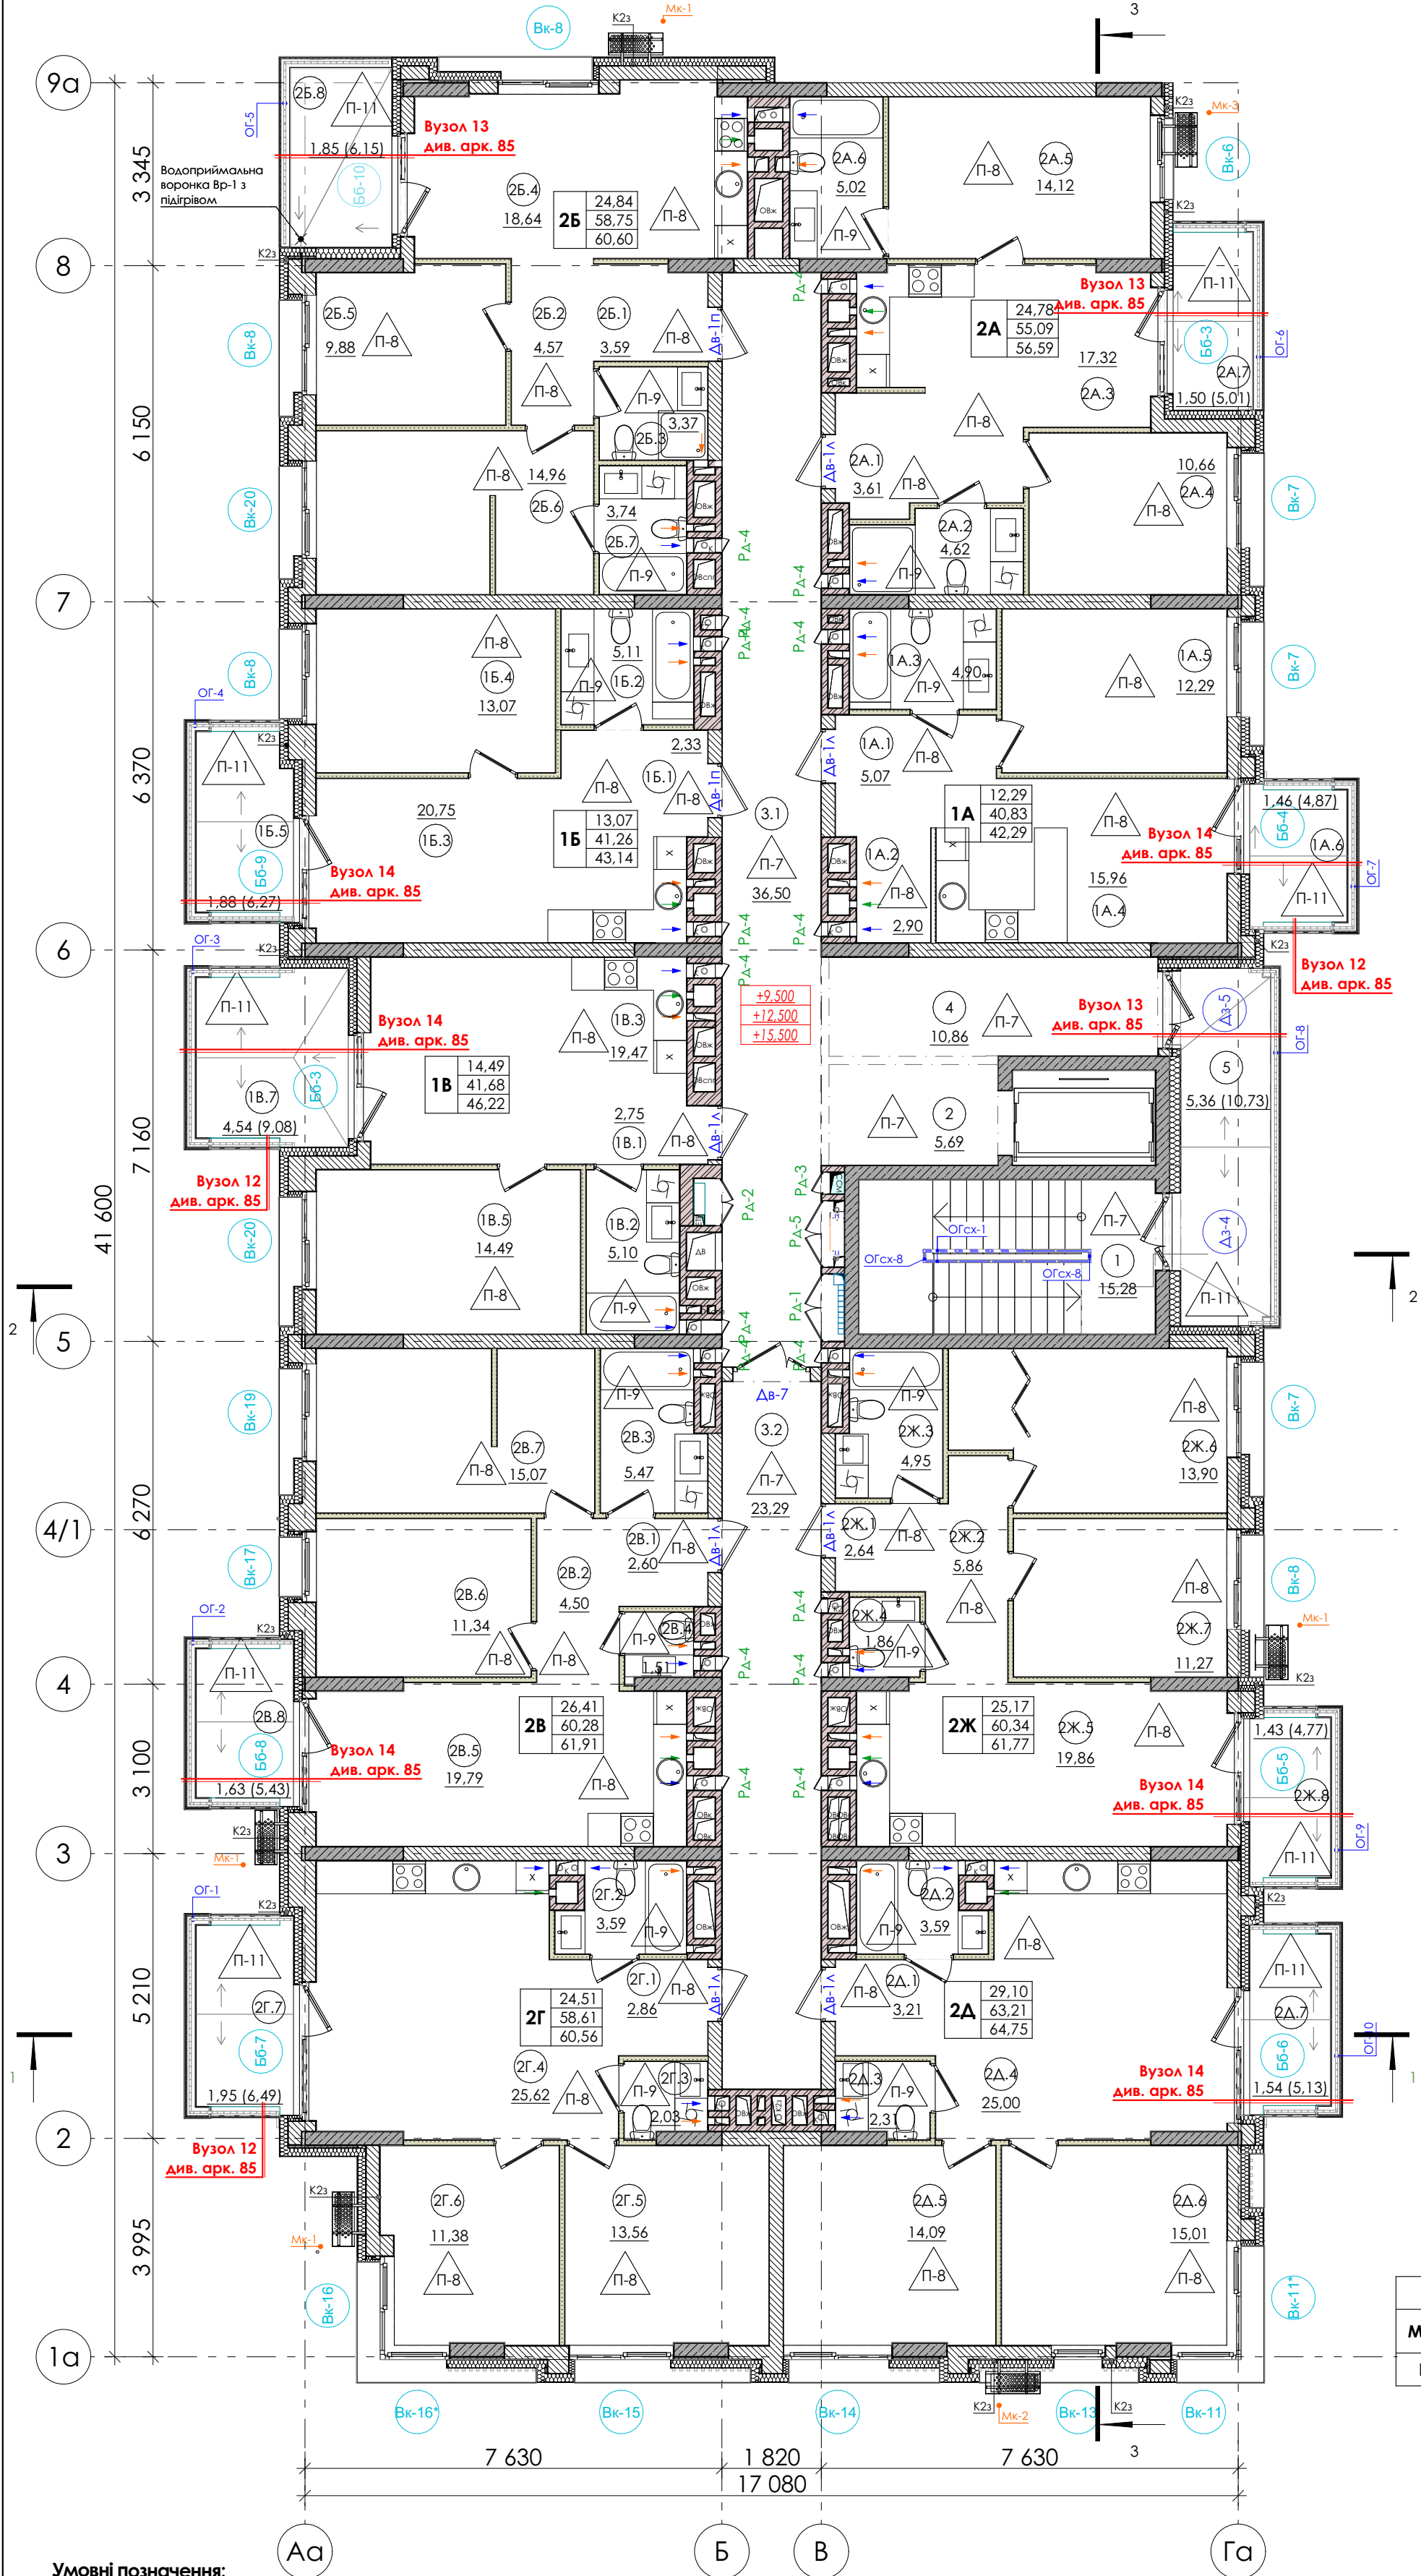

Експлікація приміщень типового поверху С1				
Тип	№ п.п.	Найменування	Площа	Прим.
1. Приміщення загального користування				
	1	Сходово-клітка Н1	15,28	
	2	Ліфтовий хол	5,69	
	3.1	Коридор	36,50	
	3.2	Коридор	23,29	
	4	Коридор	10,86	
	5	Лоджія	10,73	
			102,35 м²	
1А				
	1А.1	Передпокій	5,07	
	1А.2	Гардероб	2,90	
	1А.3	Суміщений санвузол	4,90	
	1А.4	Кухня-їдальня	15,96	
	1А.5	Спальня	12,29	
	1А.6	Балкон	1,46	
			42,58 м²	
1Б				
	1Б.1	Передпокій	2,33	
	1Б.2	Суміщений санвузол	5,11	
	1Б.3	Кухня-їдальня	20,75	
	1Б.4	Спальня	13,07	
	1Б.5	Балкон	1,88	
			43,14 м²	
1В				
	1В.1	Передпокій	2,75	
	1В.2	Суміщений санвузол	5,10	
	1В.3	Кухня-їдальня	19,47	
	1В.5	Спальня	14,49	
	1В.7	Лоджія	4,54	
			46,35 м²	
2А				
	2А.1	Передпокій	3,61	
	2А.2	Ванна кімната	4,62	
	2А.3	Кухня-їдальня	17,32	
	2А.4	Спальня	10,66	
	2А.5	Спальня	14,12	
	2А.6	Суміщений санвузол	5,02	
	2А.7	Балкон	1,50	
			56,85 м²	
2Б				
	2Б.1	Передпокій	3,59	
	2Б.2	Коридор	4,57	
	2Б.3	Туалет	3,37	
	2Б.4	Кухня-їдальня	18,64	
	2Б.5	Спальня	9,88	
	2Б.6	Спальня	14,96	
	2Б.7	Ванна кімната	3,74	
	2Б.8	Балкон	1,85	
			60,60 м²	
2В				
	2В.1	Передпокій	2,60	
	2В.2	Коридор	4,50	
	2В.3	Суміщений санвузол	5,47	
	2В.4	Туалет	1,51	
	2В.5	Кухня-їдальня	19,79	
	2В.6	Спальня	11,34	
	2В.7	Спальня	15,07	
	2В.8	Балкон	1,63	
			61,91 м²	
2Г				
	2Г.1	Передпокій	2,86	
	2Г.2	Ванна кімната	3,59	
	2Г.3	Туалет	2,03	
	2Г.4	Кухня-їдальня	25,62	
	2Г.5	Спальня	13,56	
	2Г.6	Спальня	11,38	
	2Г.7	Балкон	1,95	
			60,99 м²	
2Д				
	2Д.1	Передпокій	3,21	
	2Д.2	Ванна кімната	3,59	
	2Д.3	Туалет	2,31	
	2Д.4	Кухня-їдальня	25,00	
	2Д.5	Спальня	14,09	
	2Д.6	Спальня	15,01	
	2Д.7	Балкон	1,54	
			64,75 м²	
2Ж				
	2Ж.1	Передпокій	2,64	
	2Ж.2	Коридор	5,86	
	2Ж.3	Суміщений санвузол	4,95	
	2Ж.4	Туалет	1,86	
	2Ж.5	Кухня-їдальня	19,86	
	2Ж.6	Спальня	13,90	
	2Ж.7	Спальня	11,27	
	2Ж.8	Балкон	1,43	
			61,77 м²	
			601,29 м²	

Специфікація воронки типового поверху +9,500			
Марка	Найменування	Кількість	Примітки
Вр-1	Воронка водопримильна з підігрівом	1	Див. розділ ВК

Умовні позначення:

- Монолітні з/б стіни, пілони, колони
- Стіни та перегородки з керамічного блоку 2НФ 2,12 - 250мм, 120мм
- Стіни та перегородки з цегли - 250мм, 120мм
- Стіни та перегородки з мучкоблоку - 250мм, 100мм
- Контури балок
- Вентканалы
- Підключення до вентиляційного каналу
- Підключення до димоходу
- Підключення до КІ
- Побутова каналізація
- Ливнева каналізація
- Відвід води від кондиціонерів
- Відмітка рівня підлоги


- Номер приміщення місць загального користування (МЗК) або нежитлового
- Номер приміщення квартири
- Тип підлоги/покрівлі
- Напрямок і ухил стоку води
- Типи квартири
- Житлова площа квартири
- Площа квартири
- Загальна площа квартири
- Маркування зовнішніх/внутрішніх дверей
- Маркування вікон/балконних блоків
- Маркування ревізійних дверцят
- Маркування корзин кондиціонерів
- Маркування огороження балконів
- Маркування огороження сходів
- Маркування фасонних елементів
- Вузли

- 
 - Номер приміщення місць загального користування (МЗК) або нежитлового
 - Номер приміщення квартири
 - 
 - Тип підлоги/покрівлі
 - 
 - Напрямок і ухил стоку води
 - Типи квартири


1A	10,2
	25,2
	30,25

 - Житлова площа квартири
 - Площа квартири
 - Загальна площа квартири
 - 
 - Маркування зовнішніх/внутрішніх дверей
 - 
 - Маркування вікон/балконних блоків
 - 
 - Маркування ревізійних дверцят
 - 
 - Маркування корзин кондиціонерів
 - 
 - Маркування огороження балконів
 - 
 - Маркування огороження сходів
 - 
 - Маркування фасонних елементів
 - 
 - Вузли

Специфікація воронки поверху на відм.+27,50			
Марка	Найменування	Кількість	Примітки
Вр-1	Воронка водоприймальна з підігрівом	10	

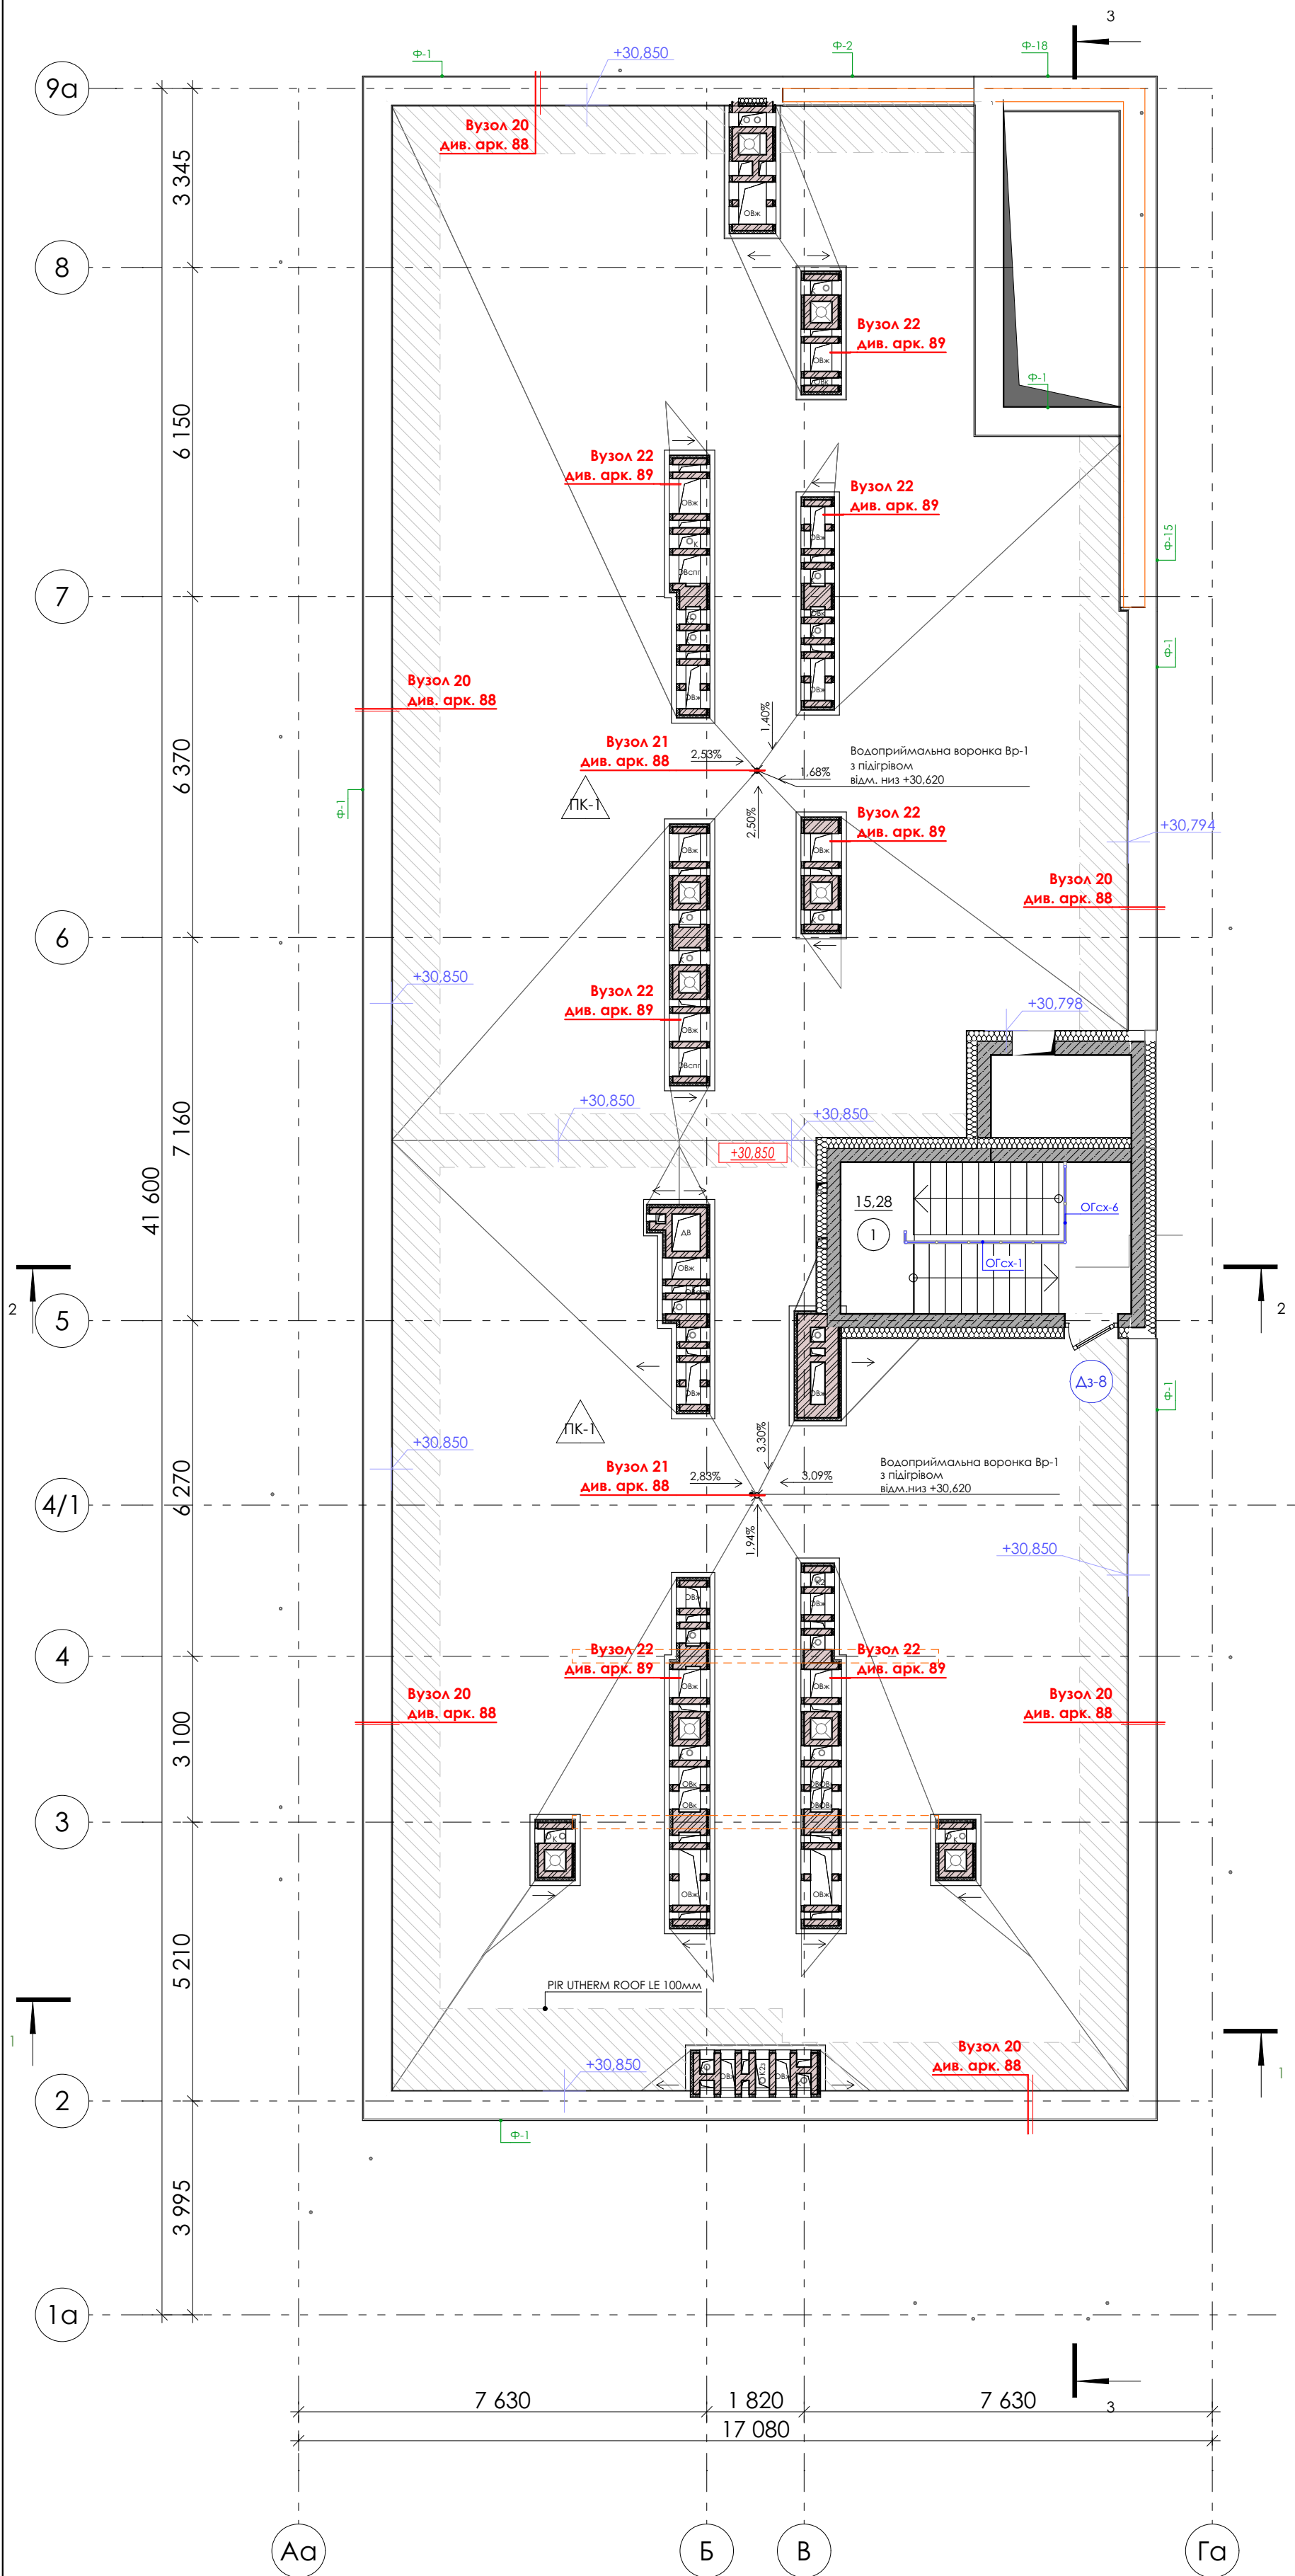

План покрівлі над сходовою.
Секція №1 по ГП, М 1:100

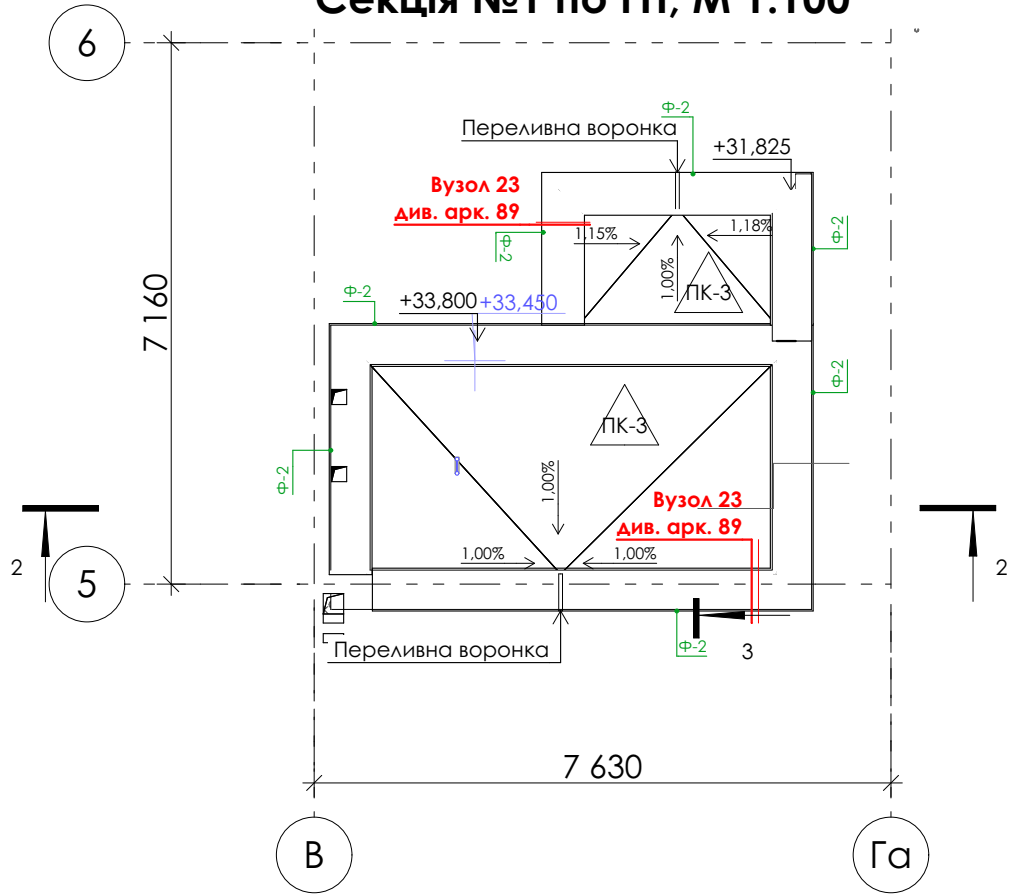

Експлікація приміщень покрівлі				
Тип	№ п.п.	Найменування	Площа	Прим.
1. Приміщення загального користування				
	1	Сходова клітка Н1	15,28	
			15,28 м²	

- Умовні позначення:
- Монолітні з/б стіни, пілони, колони
 - Стіни та перегородки з керамічного блоку 2НФ 2,12 - 250мм, 120мм
 - Стіни та перегородки з цегли - 250мм, 120мм
 - Стіни та перегородки з мучкоблоку - 250мм, 100мм
 - Відмітка рівня підлоги
 - Номер приміщення місць загального користування (МЗК) або нежитлового
 - Номер приміщення квартири
 - Тип підлоги/покрівлі
 - Напрямок і ухил стоку води
 - Маркування зовнішніх/внутрішніх дверей
 - Маркування огороження балконів
 - Маркування огороження сходів
 - Маркування фасонних елементів
 - Вузли
 - Відмітки покрівлі
 - Додатковий шар утеплення для полегшення конструкцій покрівлі

Специфікація воронок покрівлі			
Марка	Найменування	Кількість	Примітки
Вр-1	Воронка водоприймальна з підігрівом	2	Див. розділ ВК

Розріз 1-1 М 1:100



Розріз 2-2 М 1:100



Умовні позначення:







- +1,000 - Відмітки
- П-1 - Тип підлоги/покрівлі
- ОГСК-3 - Маркування огорожень
- 23 89 - Маркування вузлів

Розріз 3-3 М 1:100





Умовні позначення:





- +1,000 - Відмітки
- П-1 - Тип підлоги/покрівлі
- Огсх-3 - Маркування огорожень
- 23/89 - Маркування вузлів

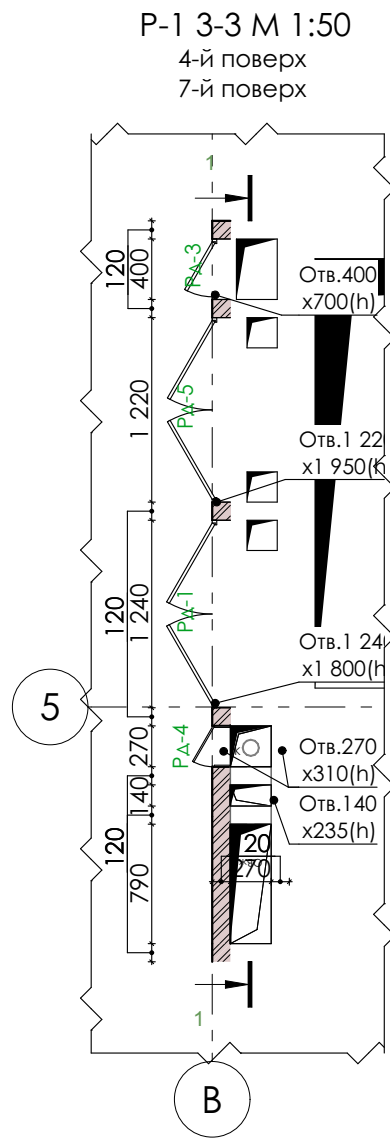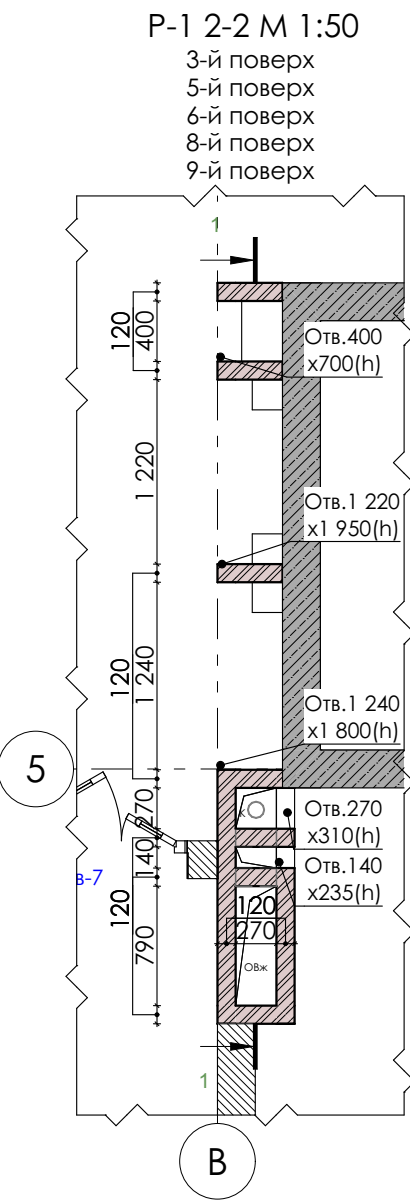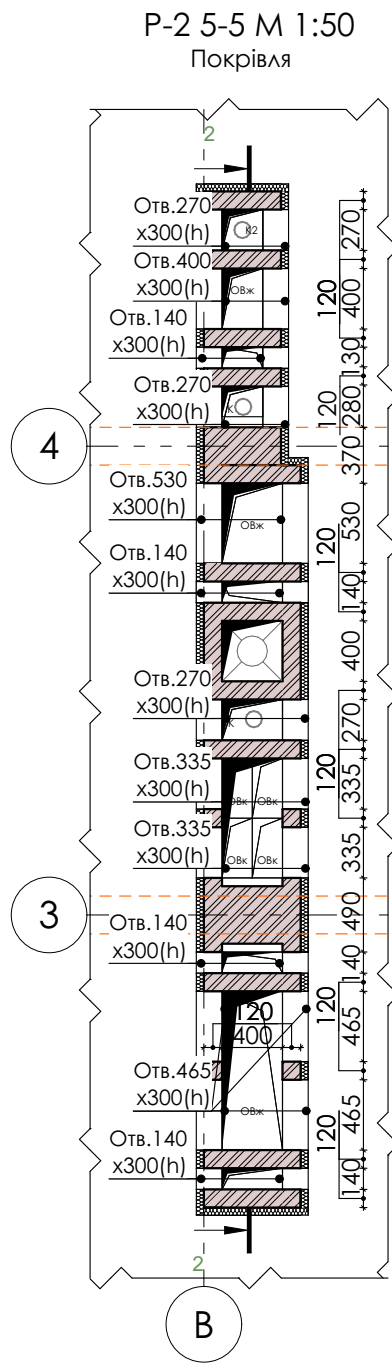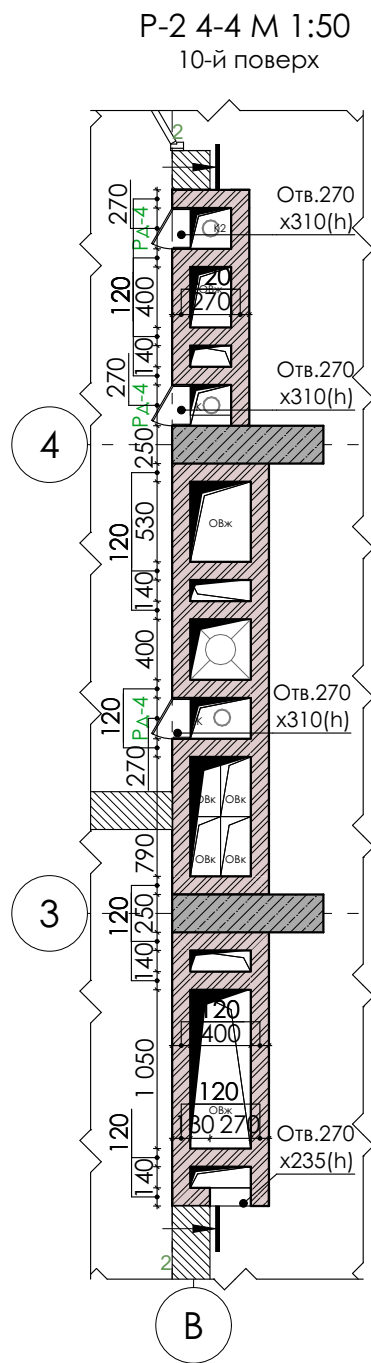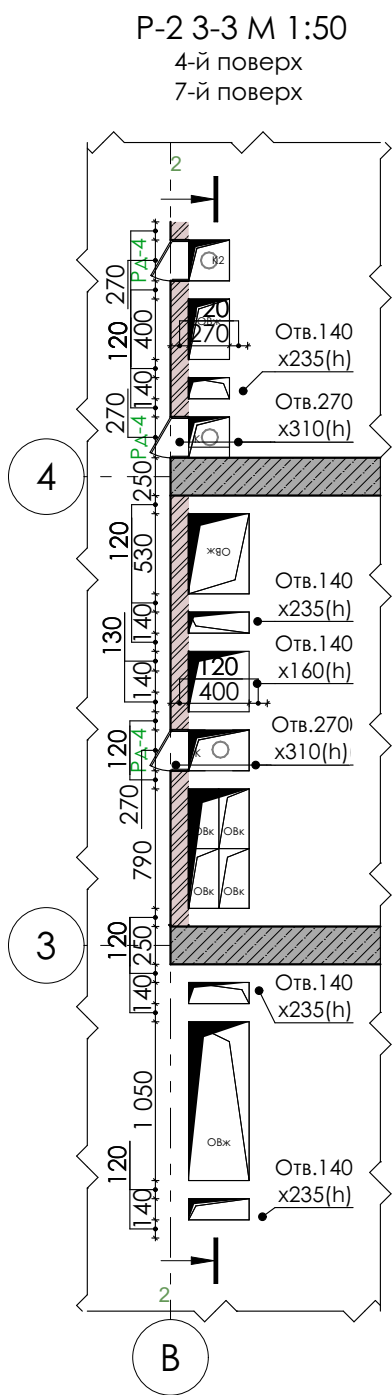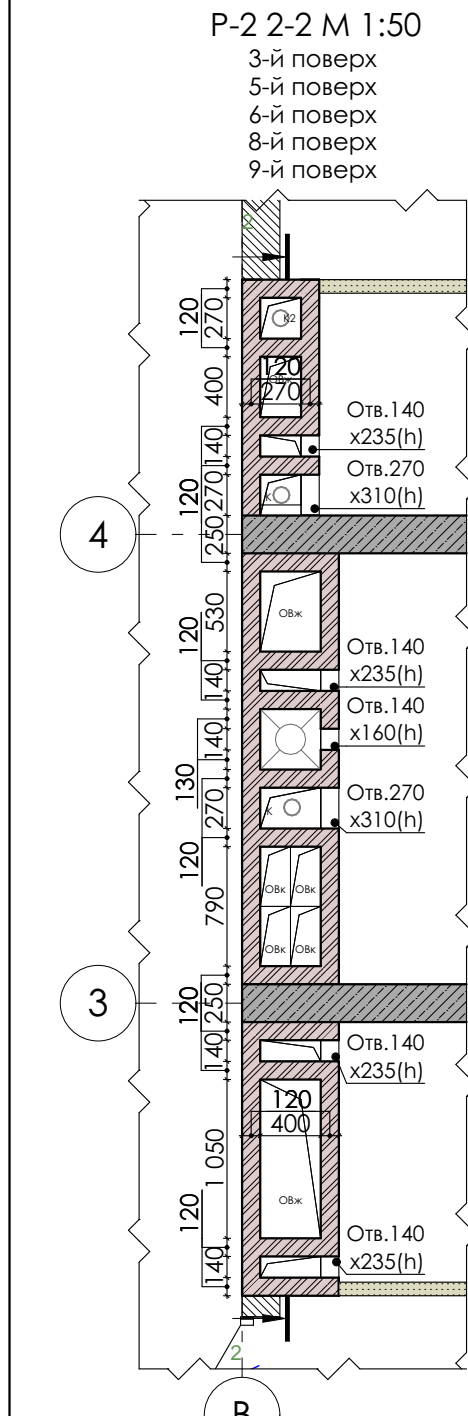


Розгортка вентканалу P-1 М 1:50

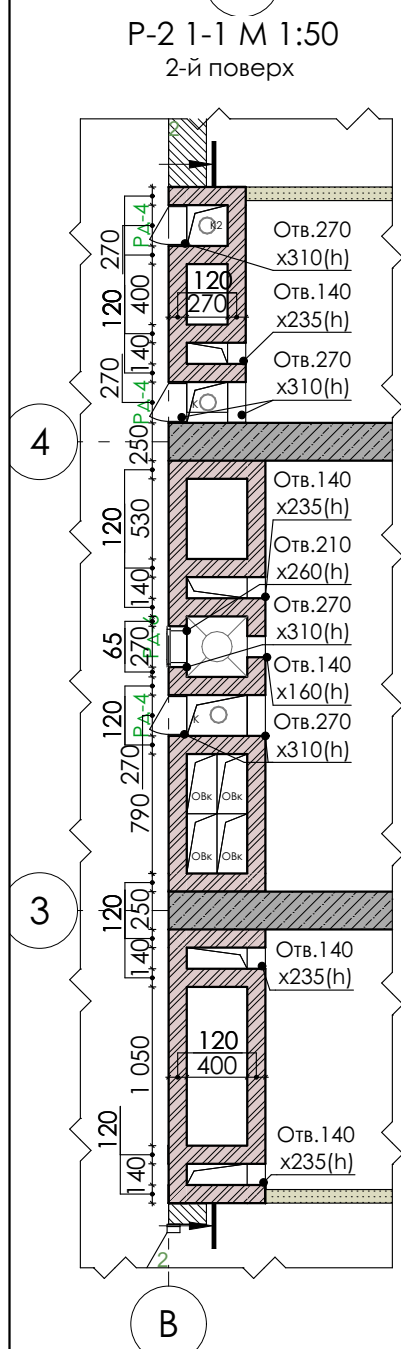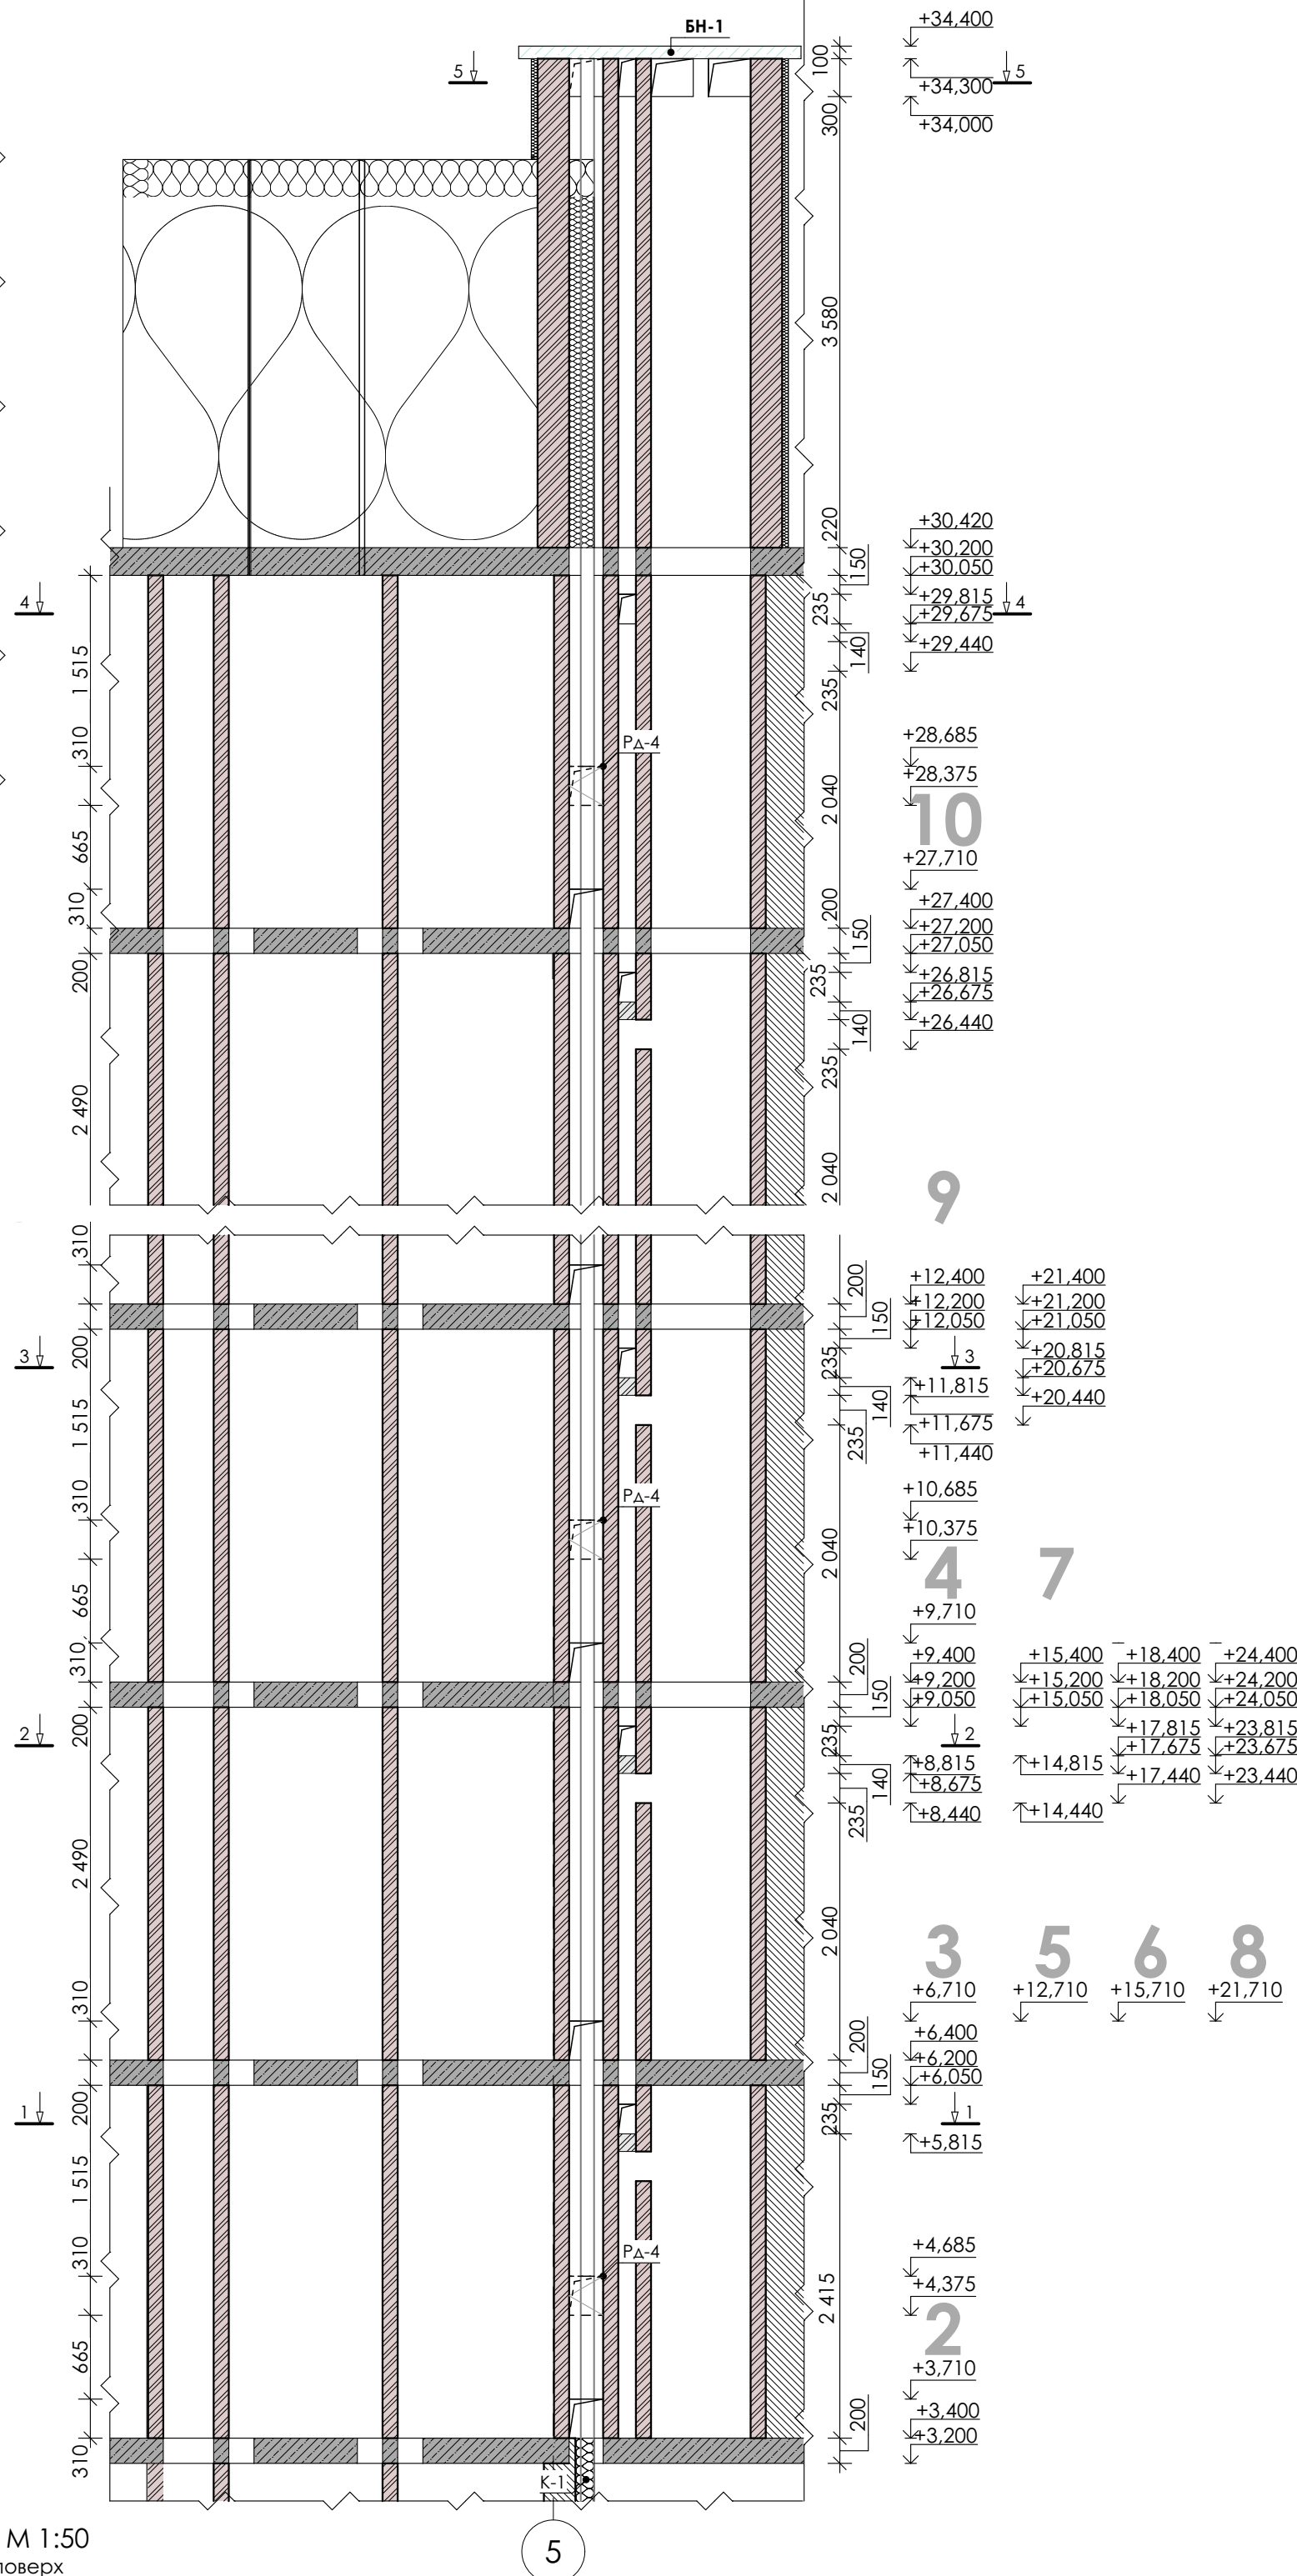

Розгортка вентканалу P-2 М 1:50

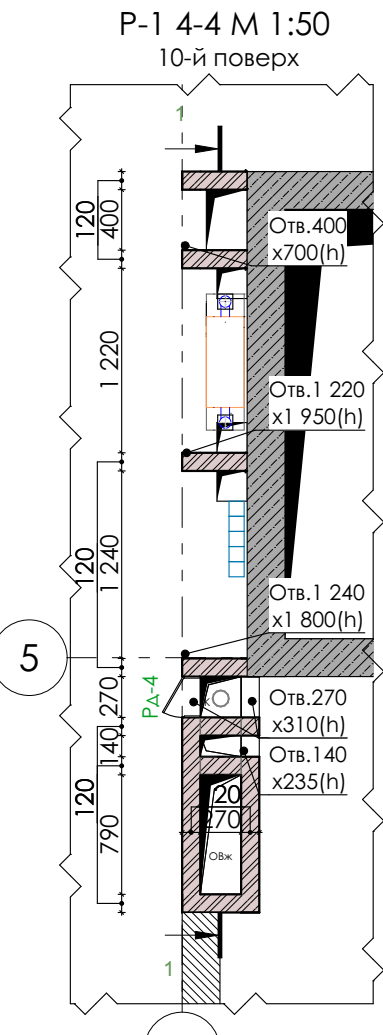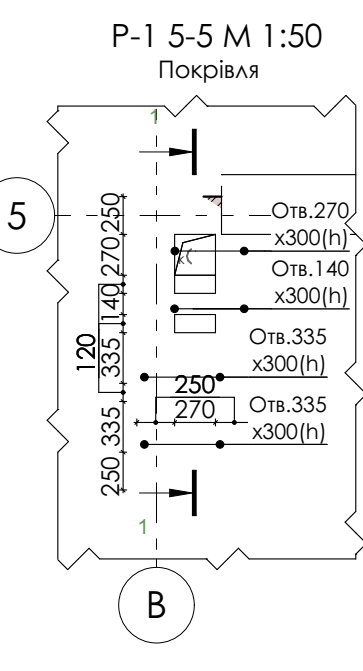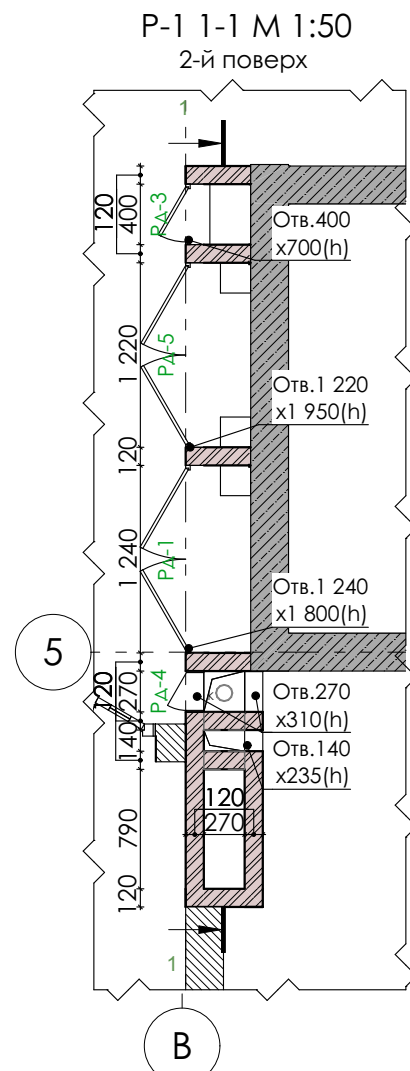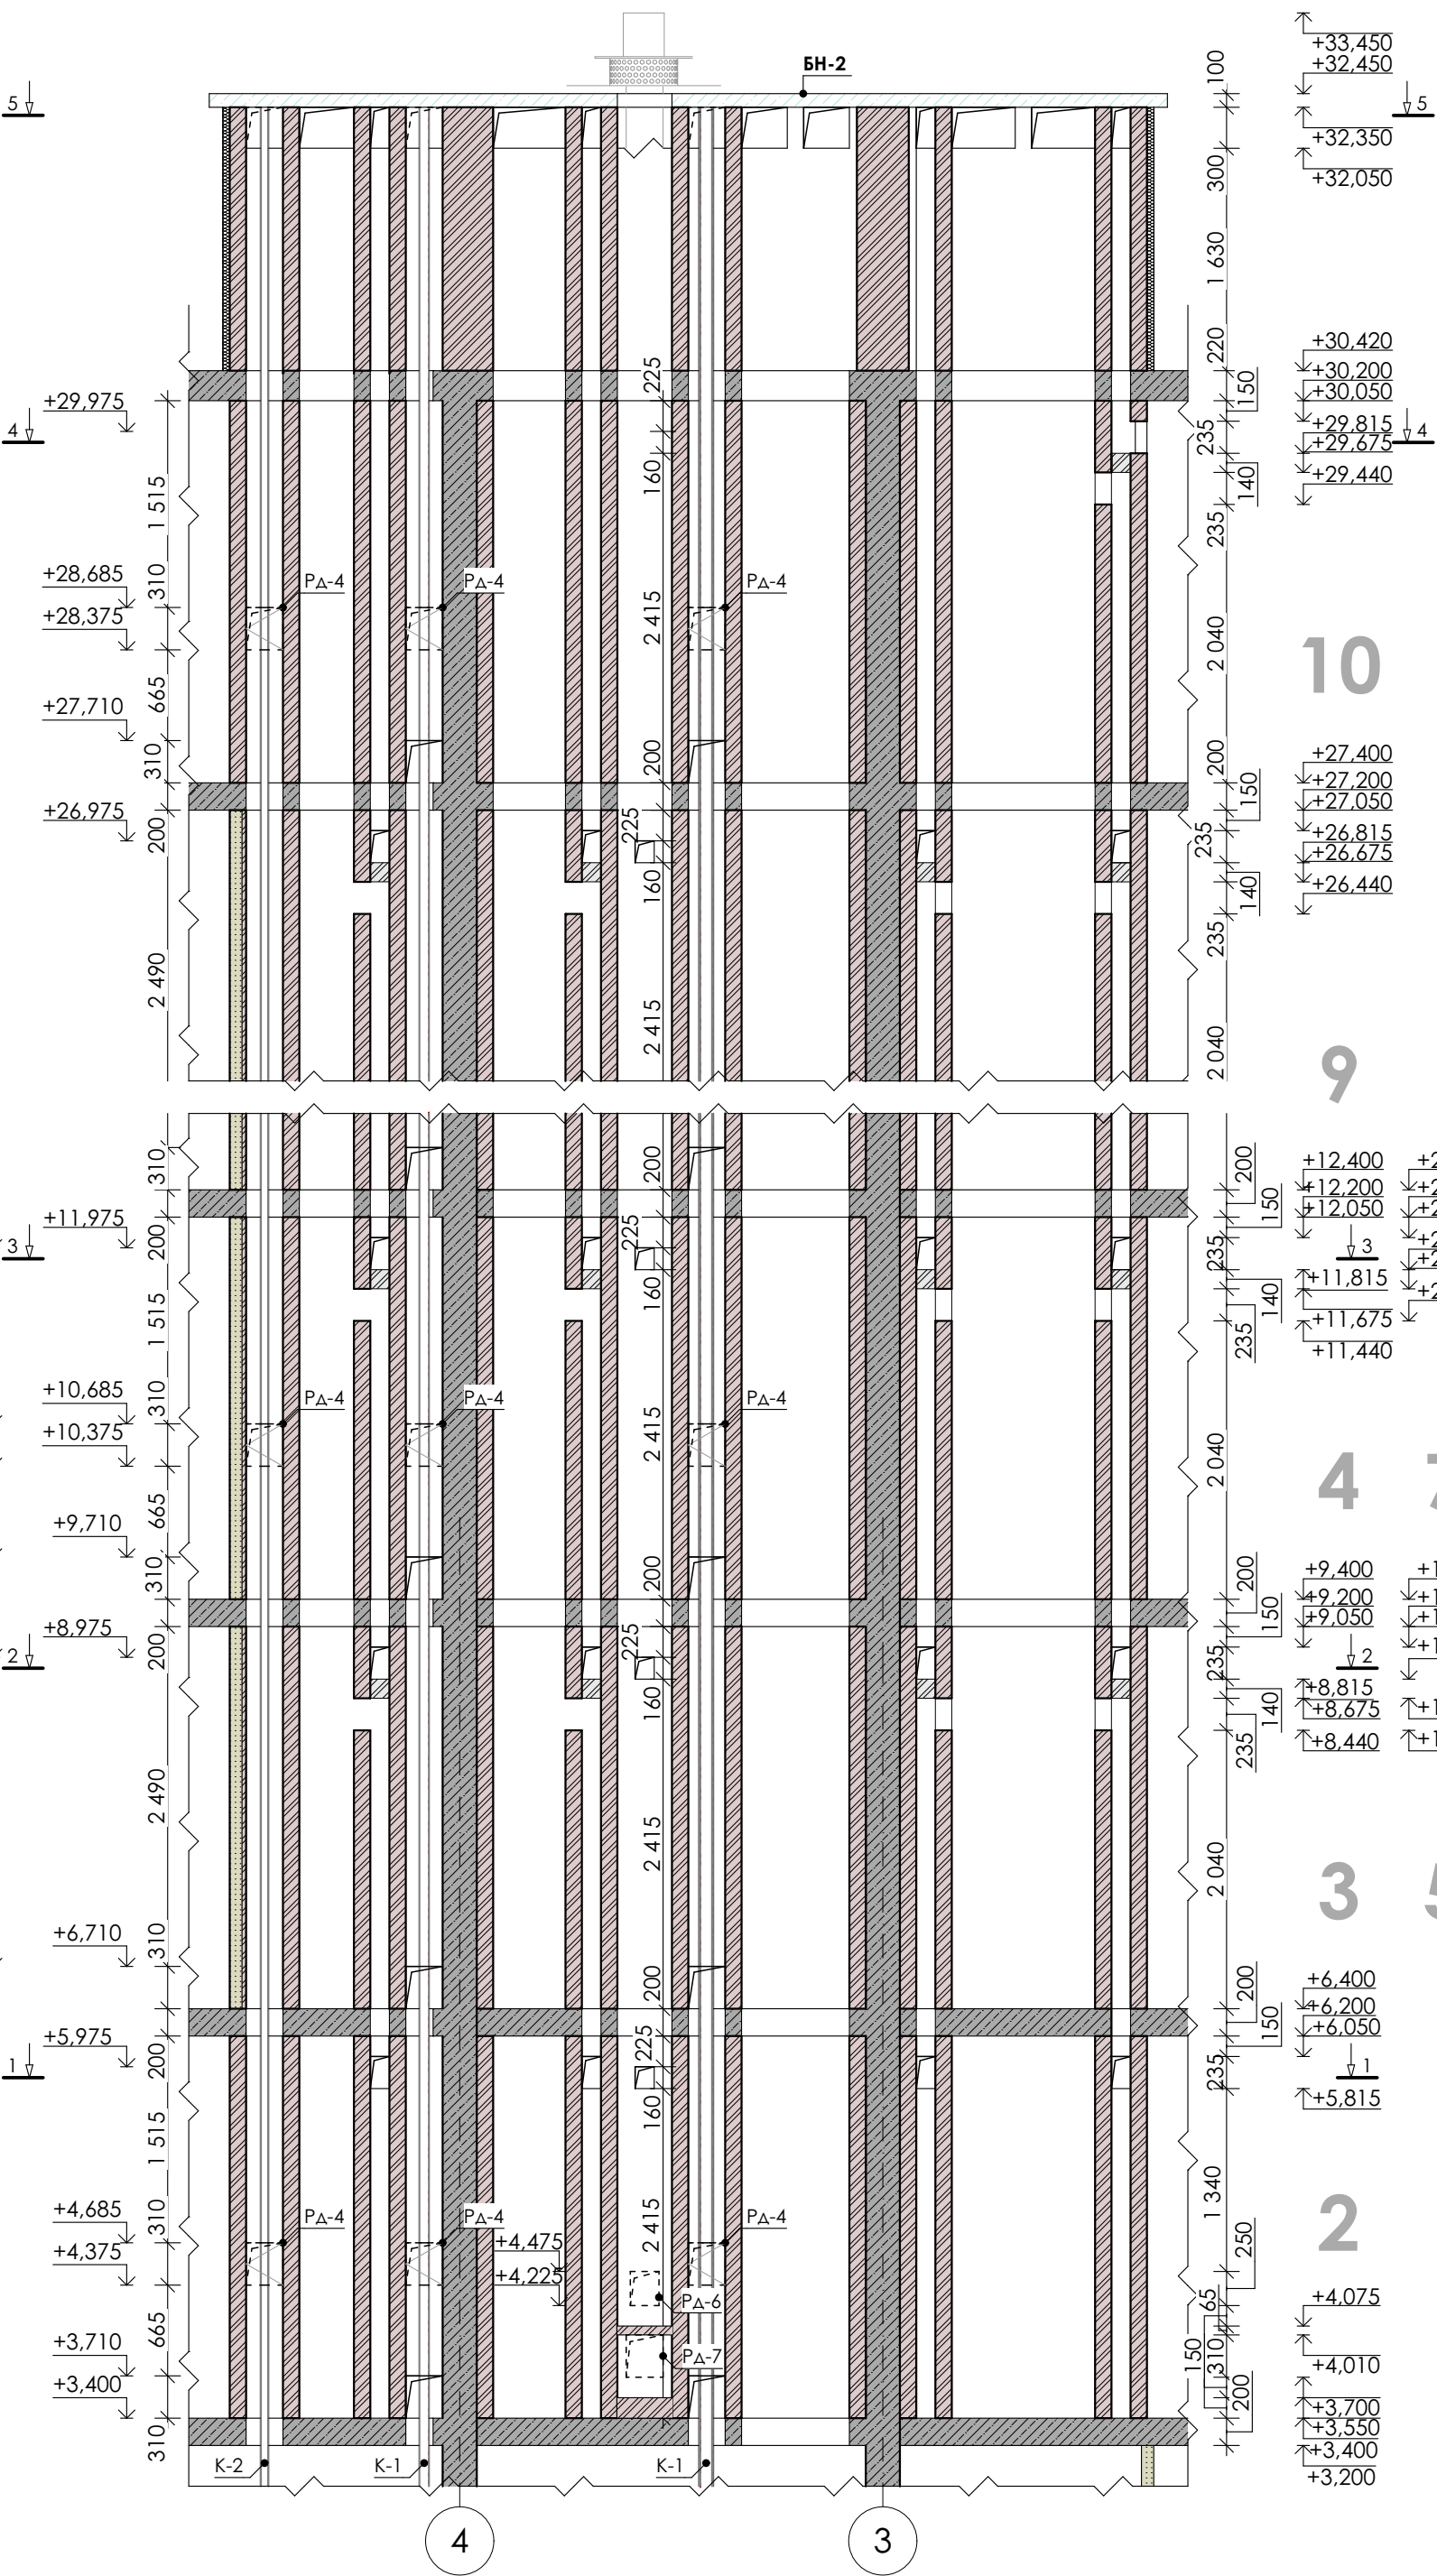

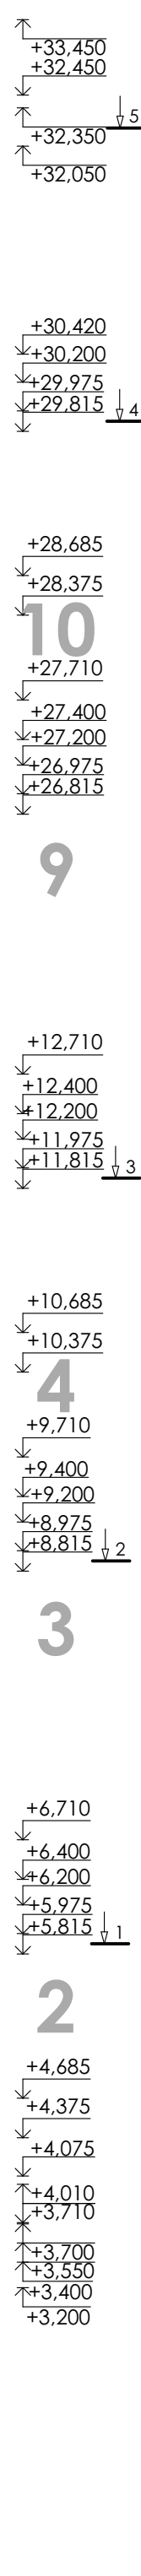[illegible]

Покрівля

3

120 130 140 270

Отв. 270 x300(h)

П-3 4-4 М 1:50

10-й поверх

3

120 130 140 270

Отв. 140 x160(h)

П-3 2-2 М 1:50

3-й поверх

5-й поверх

6-й поверх

8-й поверх

9-й поверх

3

120 130 140 270

Отв. 270 x310(h)

Отв. 140 x160(h)

00	+18,400	+24,400
00	+18,200	+24,200
75	+17,975	+23,975
5	+17,815	+23,815

6 8

П-3 3-3 М 1:50

4-й поверх

7-й поверх

3

120 130 140 270

Отв. 270 x310(h)

Отв. 140 x160(h)

П-2 1-1 М 1:50

2-й поверх

3



120 130 140 270

Отв. 270 x310(h)

Отв. 270 x310(h)

Отв. 140 x160(h)

Отв. 210 x250(h)

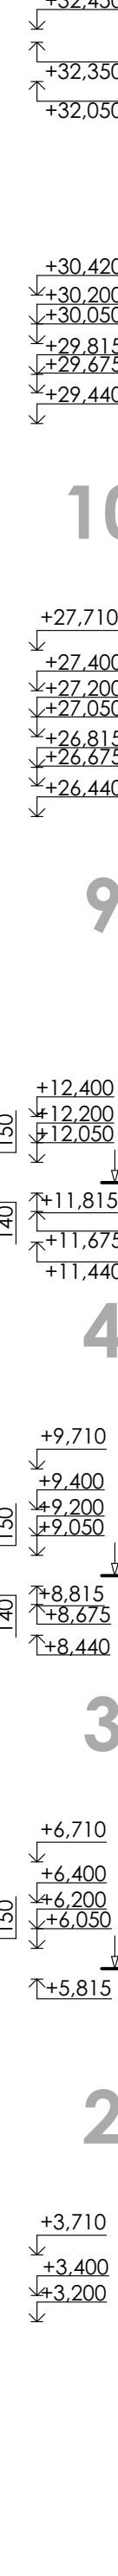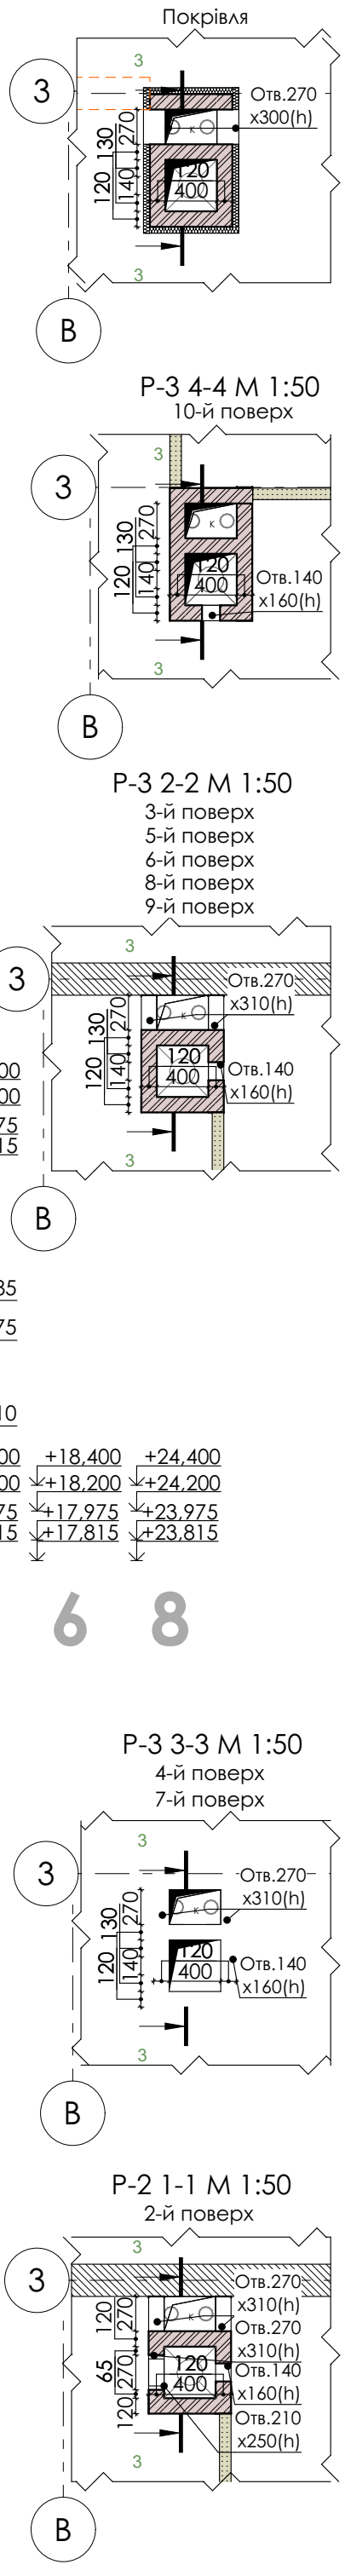

Покрівля

3

Отв. 270
x300(h)

120
400

5

270
120
140
120
130

Р-5 4-4 М 1:50
10-й поверх

3

Отв. 140
x160(h)

120
400

5

270
120
140
120
130

Р-5 2-2 М 1:50
3-й поверх
5-й поверх
6-й поверх
8-й поверх
9-й поверх

3

Отв. 270
x310(h)
Отв. 140
x160(h)

120
400

5

270
120
140
120
130

+21.400
+21.200
+21.050
+20.815
+20.675
+20.440

7

+15.400	+18.400	+24.400
+15.200	+18.200	+24.200
+15.050	+18.050	+24.050
+14.675	+17.815	+23.815
	+17.675	+23.675
+14.815	+17.440	+23.440
+14.440		

5 6 8

Р-5 3-3 М 1:50
4-й поверх
7-й поверх

3

Отв. 270
x310(h)
Отв. 140
x160(h)

120
400

5

270
120
140
120
130

Р-5 1-1 М 1:50
2-й поверх


3

Отв. 270
x310(h)
Отв. 140
x160(h)
Отв. 210
x250(h)
Отв. 270
x310(h)

120
400



5

270
120
140
120
130
65

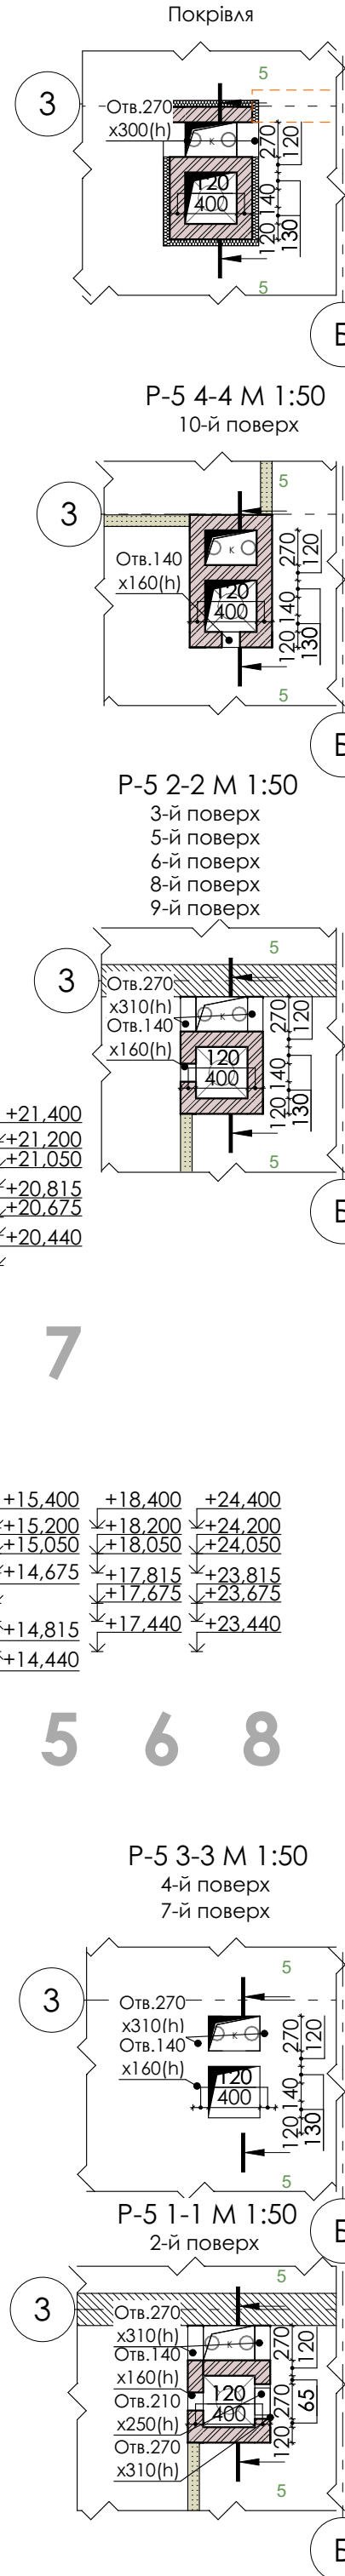

The drawing shows a vertical section of a building facade with three levels. The facade is composed of various materials, including brickwork and concrete. The levels are labeled 1, 2, and 3. The elevation data is as follows:

Level	Point	Elevation
Level 3	Top of Level 3	+33.450
	Top of Level 2	+32.450
	Top of Level 1	+32.350
	Top of Level 0	+32.050
	Top of Level -1	+30.420
	Top of Level -2	+30.200
	Top of Level -3	+29.975
	Top of Level -4	+29.815
	Top of Level -5	+28.685
	Top of Level -6	+28.375
Level 2	Top of Level 2	+27.710
	Top of Level 1	+27.400
	Top of Level 0	+27.200
	Top of Level -1	+26.975
	Top of Level -2	+26.815
	Top of Level -3	+12.710
	Top of Level -4	+12.400
	Top of Level -5	+12.200
	Top of Level -6	+11.975
	Top of Level -7	+11.815
Level 1	Top of Level 1	+10.685
	Top of Level 0	+10.375
	Top of Level -1	+9.710
	Top of Level -2	+9.400
	Top of Level -3	+8.975
	Top of Level -4	+8.815
	Top of Level -5	+6.710
	Top of Level -6	+6.400
	Top of Level -7	+6.200
	Top of Level -8	+5.975
Level 0	Top of Level 0	+4.685
	Top of Level -1	+4.375
	Top of Level -2	+4.075
	Top of Level -3	+4.010
	Top of Level -4	+3.710
	Top of Level -5	+3.700
	Top of Level -6	+3.550
	Top of Level -7	+3.400
	Top of Level -8	+3.200
	Top of Level -9	+3.000

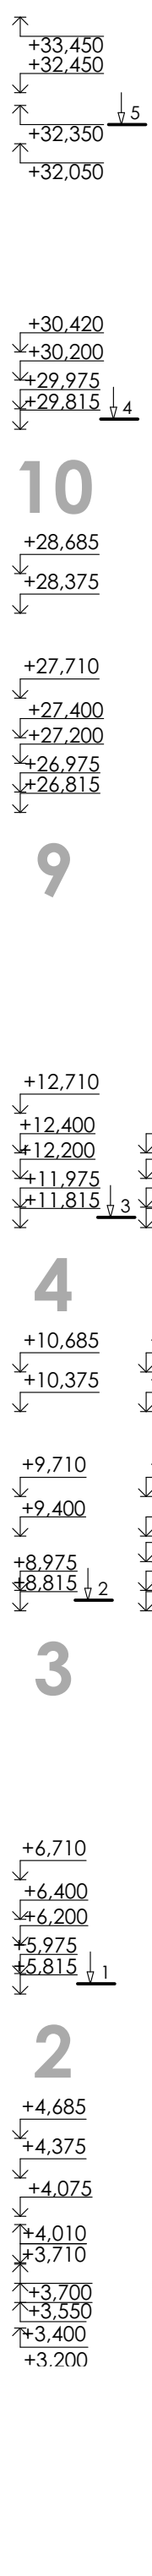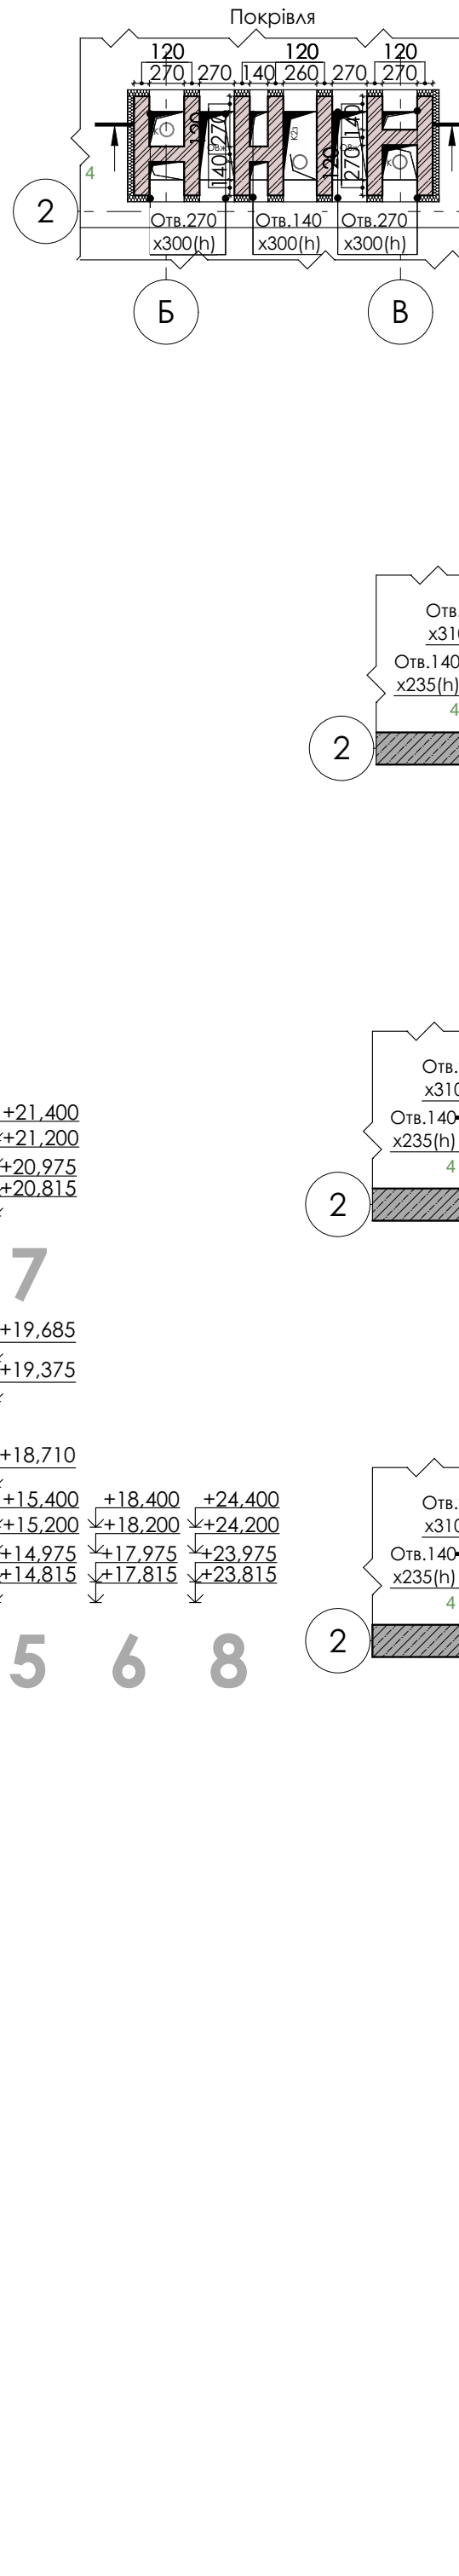[illegible]

10-й поверх

Отв. 270 x310(h)

Отв. 140 x235(h)

Отв. 270 x310(h)

Б В

П-4 2-2 М 1:50

3-й поверх

5-й поверх

6-й поверх

8-й поверх

9-й поверх

Отв. 270 x310(h)

Отв. 140 x235(h)

Отв. 270 x310(h)

Б В

П-4 3-3 М 1:50

4-й поверх

7-й поверх

Отв. 270 x310(h)

Отв. 140 x235(h)

Отв. 270 x310(h)

Б В

П-4 1-1 М 1:50


2-й поверх

Отв. 270 x310(h)

Отв. 140 x235(h)

Отв. 270 x310(h)

Б В

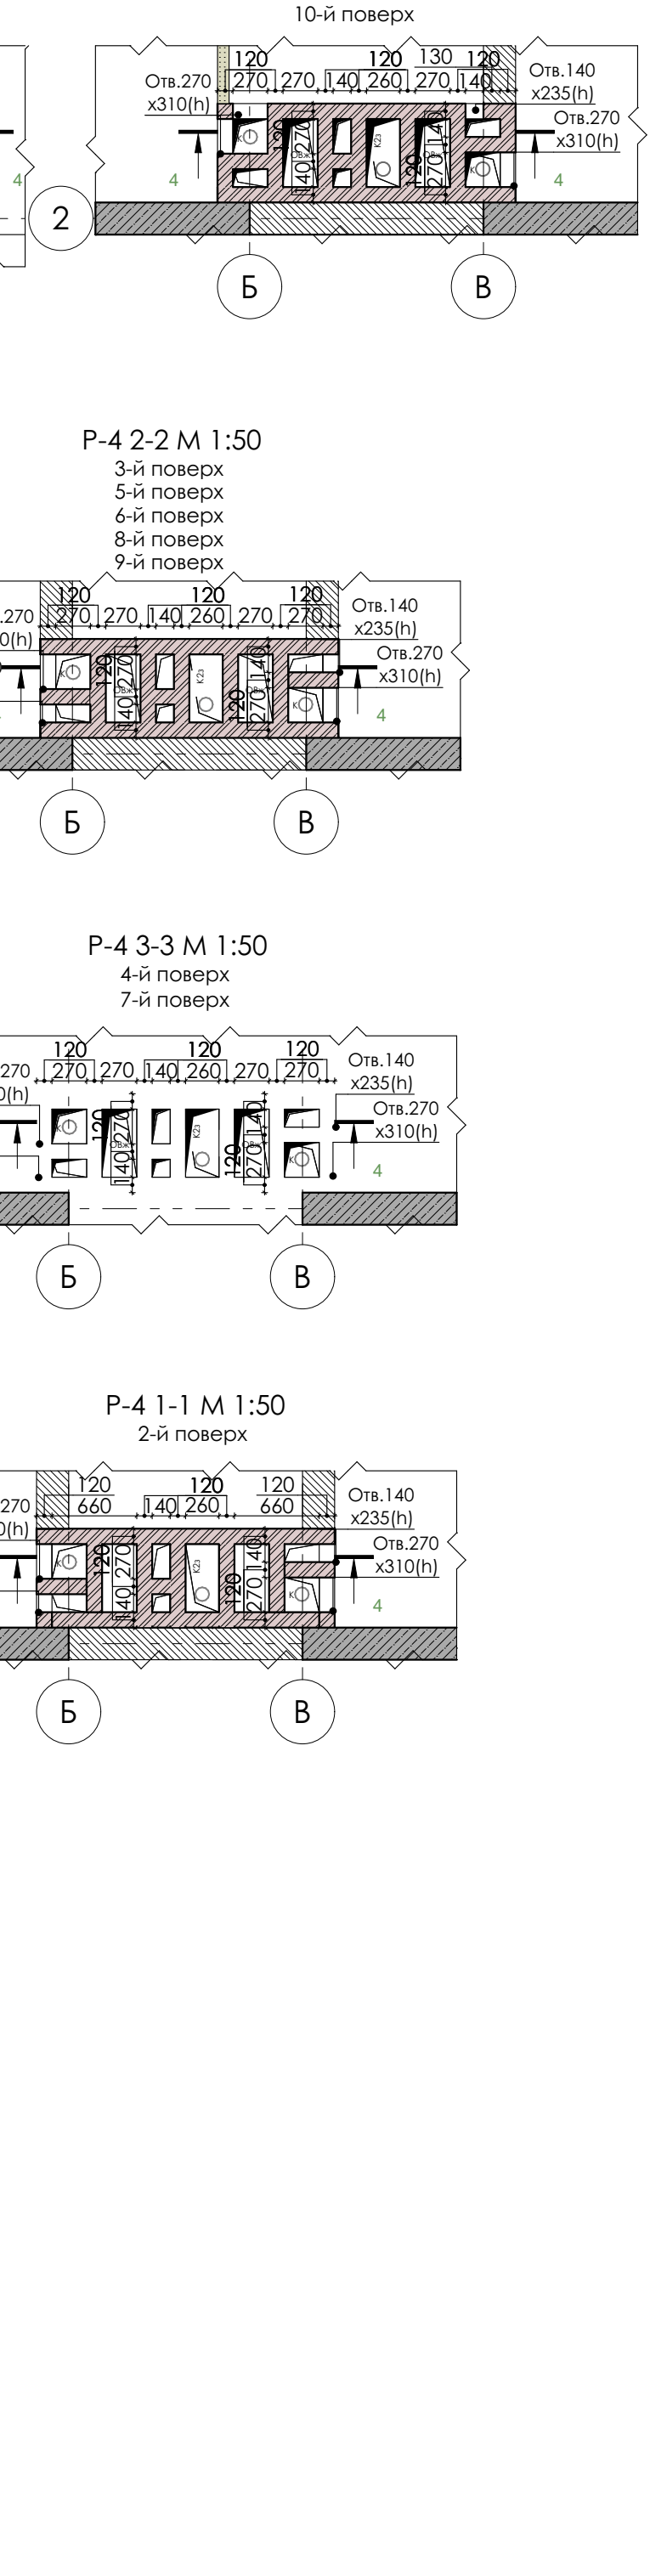

3-й поверх
5-й поверх
6-й поверх
8-й поверх
9-й поверх

Отв. 270
х 310 (h)


Отв. 140
х 235 (h)

Отв. 270
х 310 (h)

2

Б

В


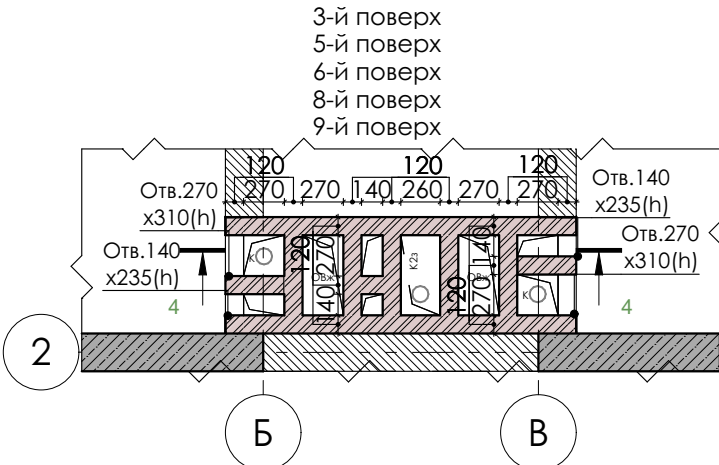












4-й этаж
7-й этаж


Отв. 270 x 310(h)
Отв. 140 x 235(h)
Отв. 140 x 235(h)
Отв. 270 x 310(h)



120 270 140 260 270 120

Б В

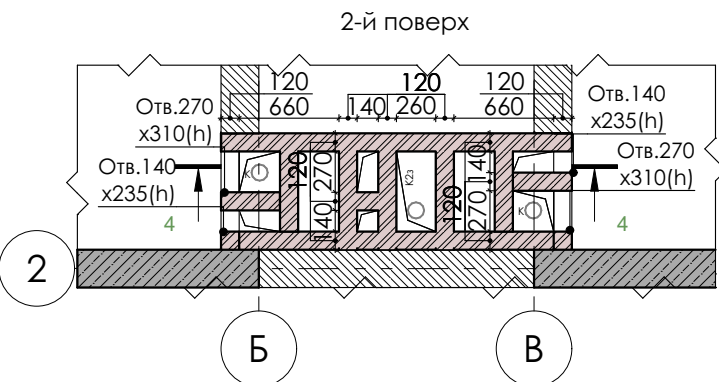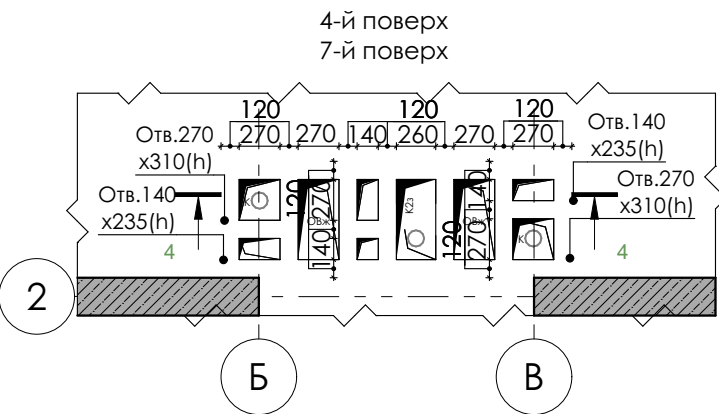

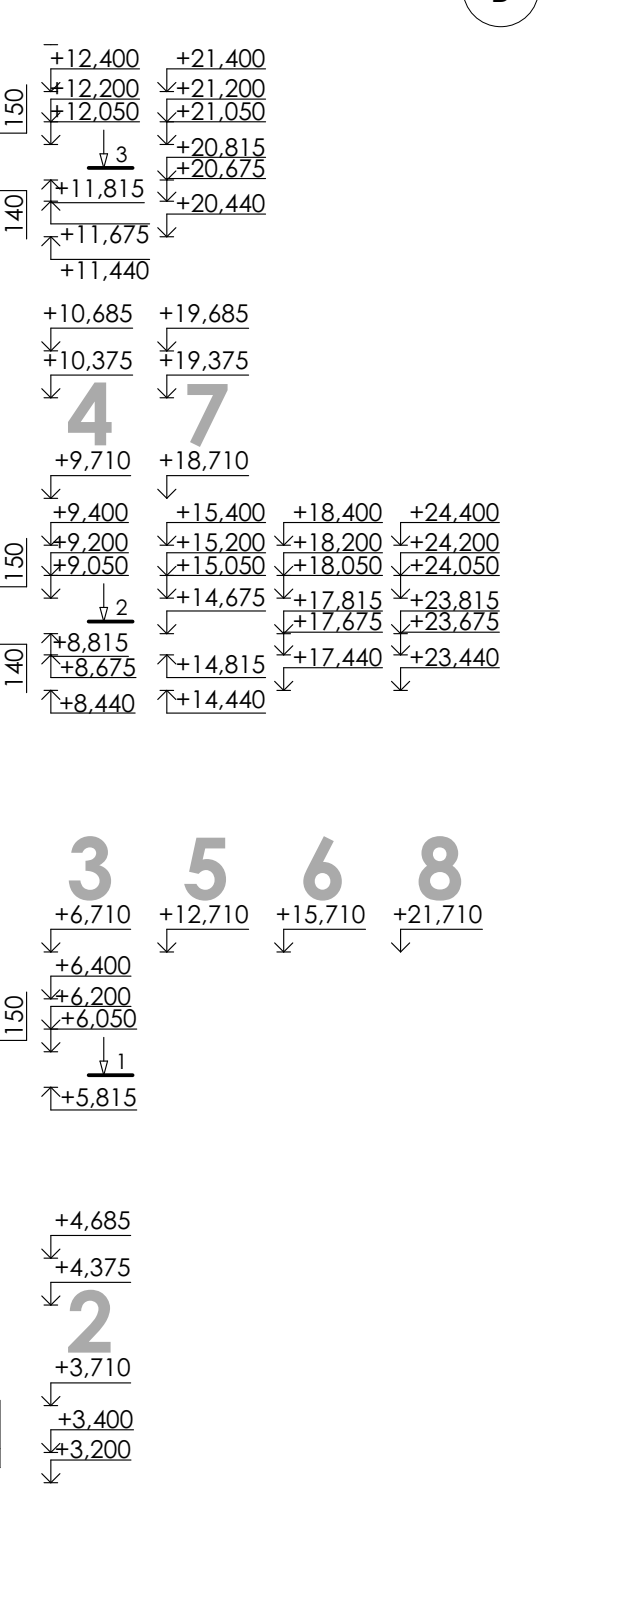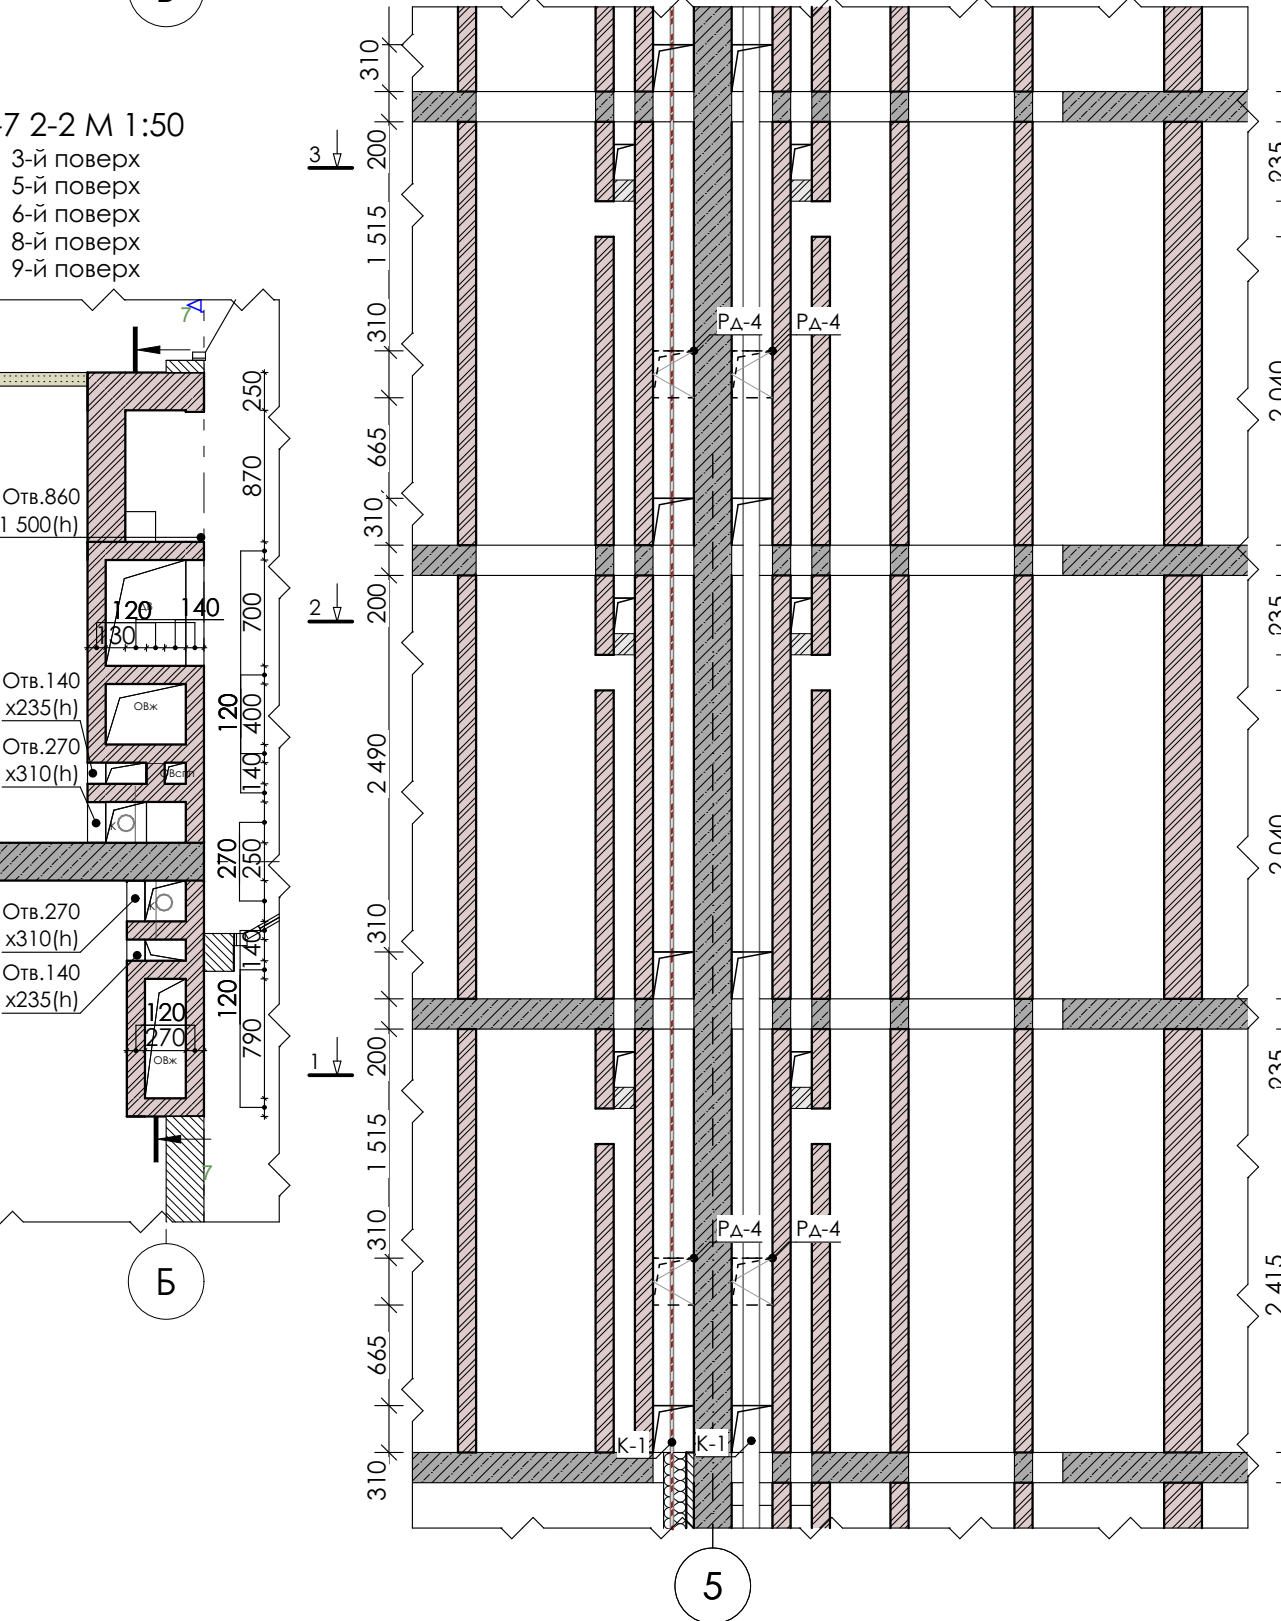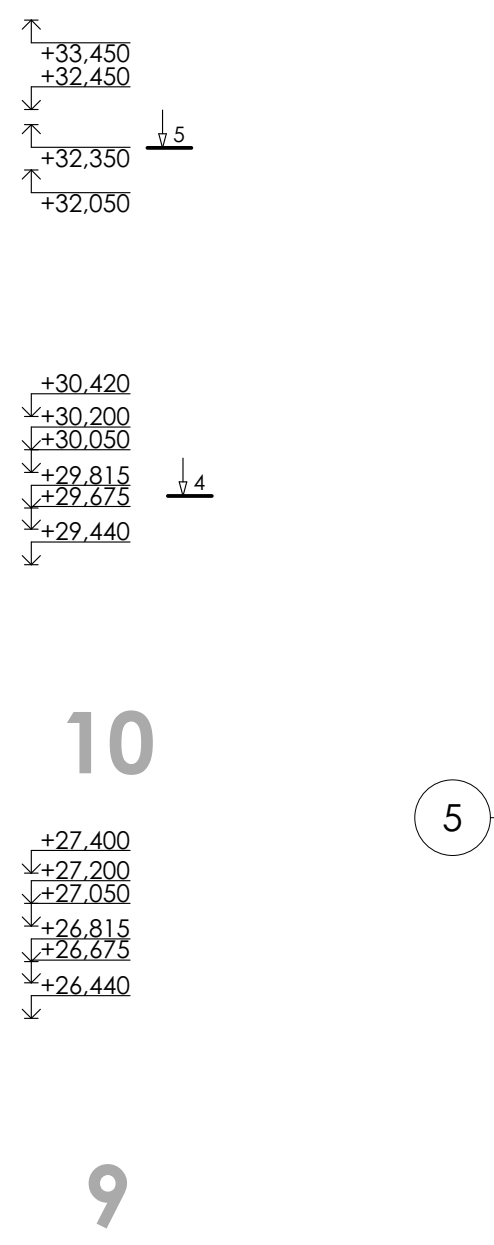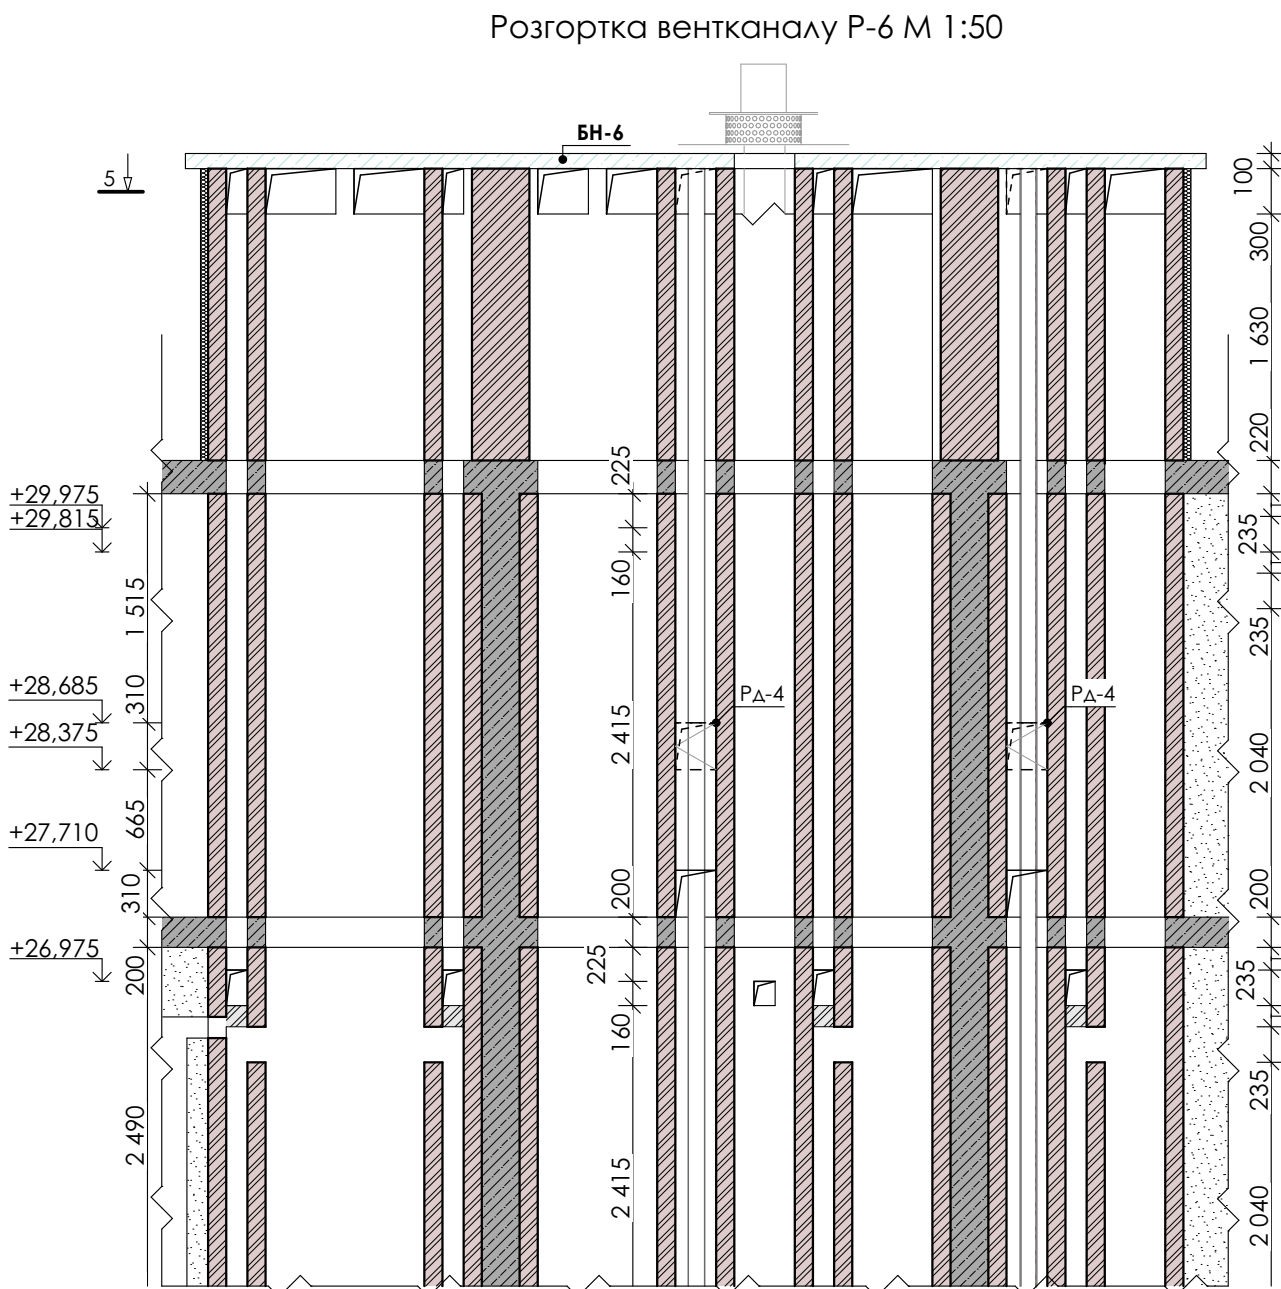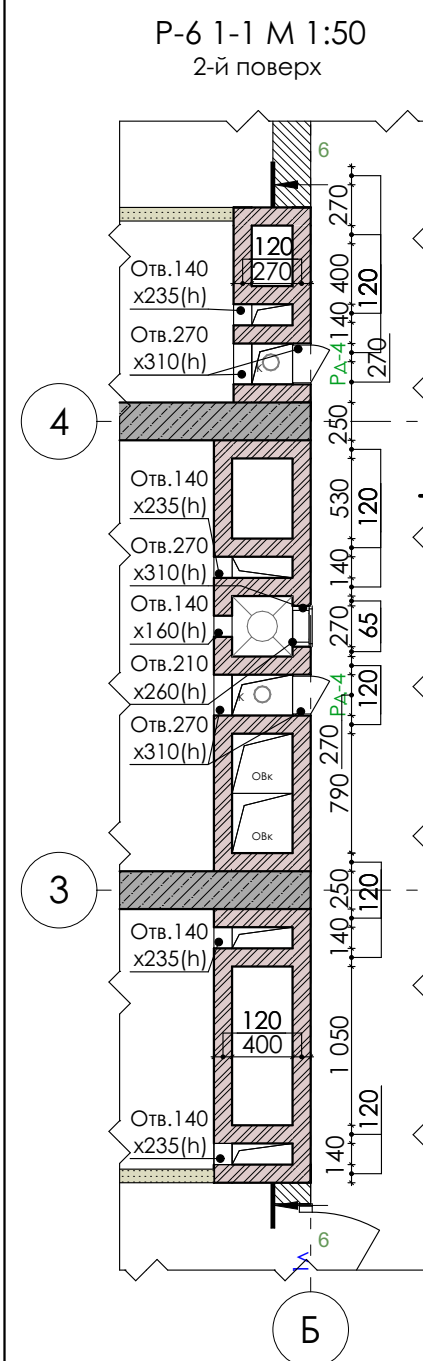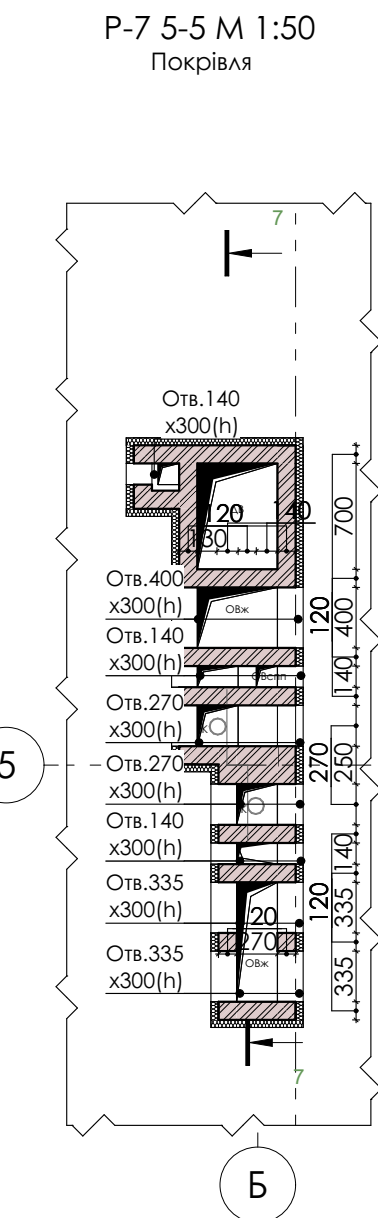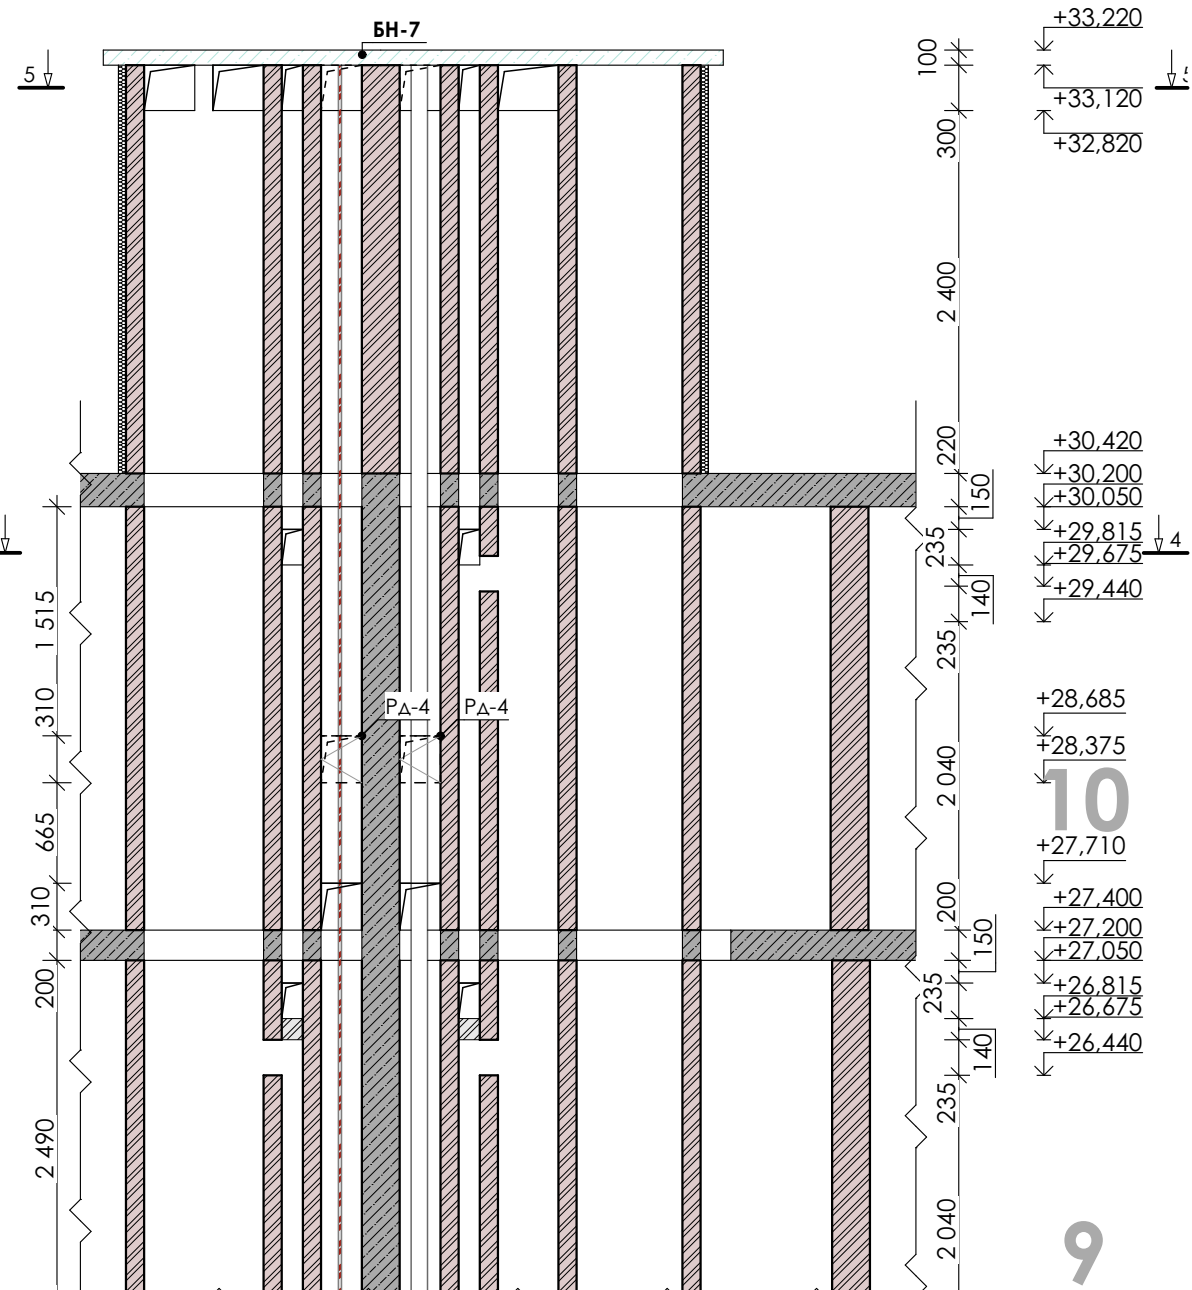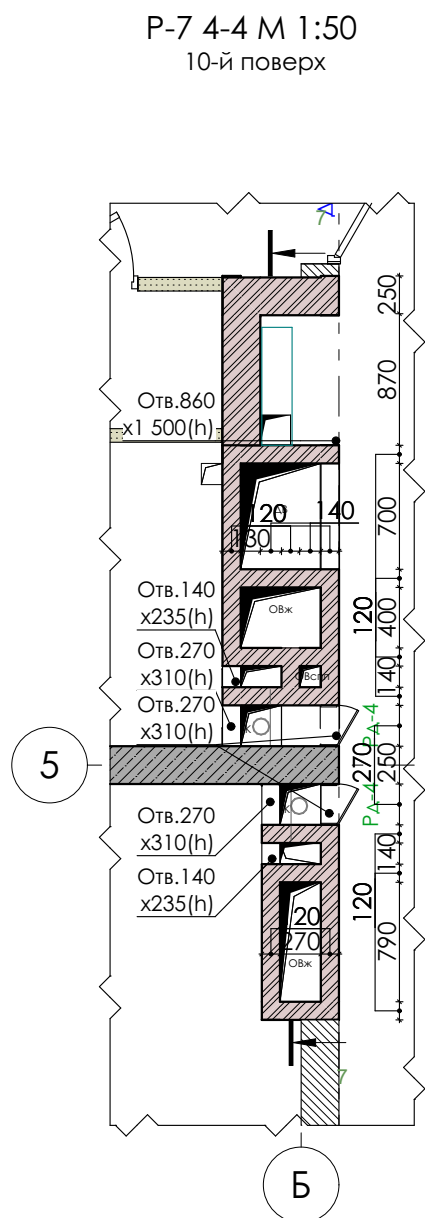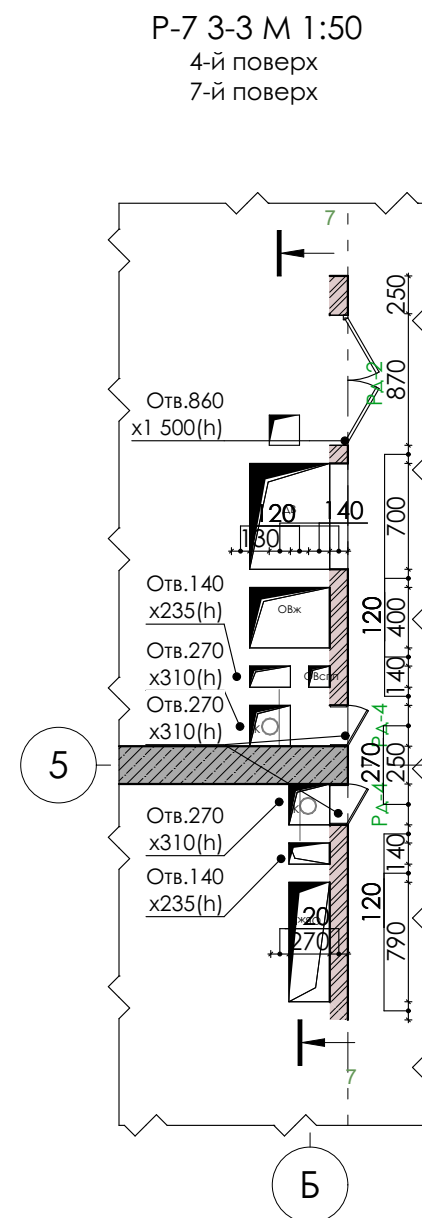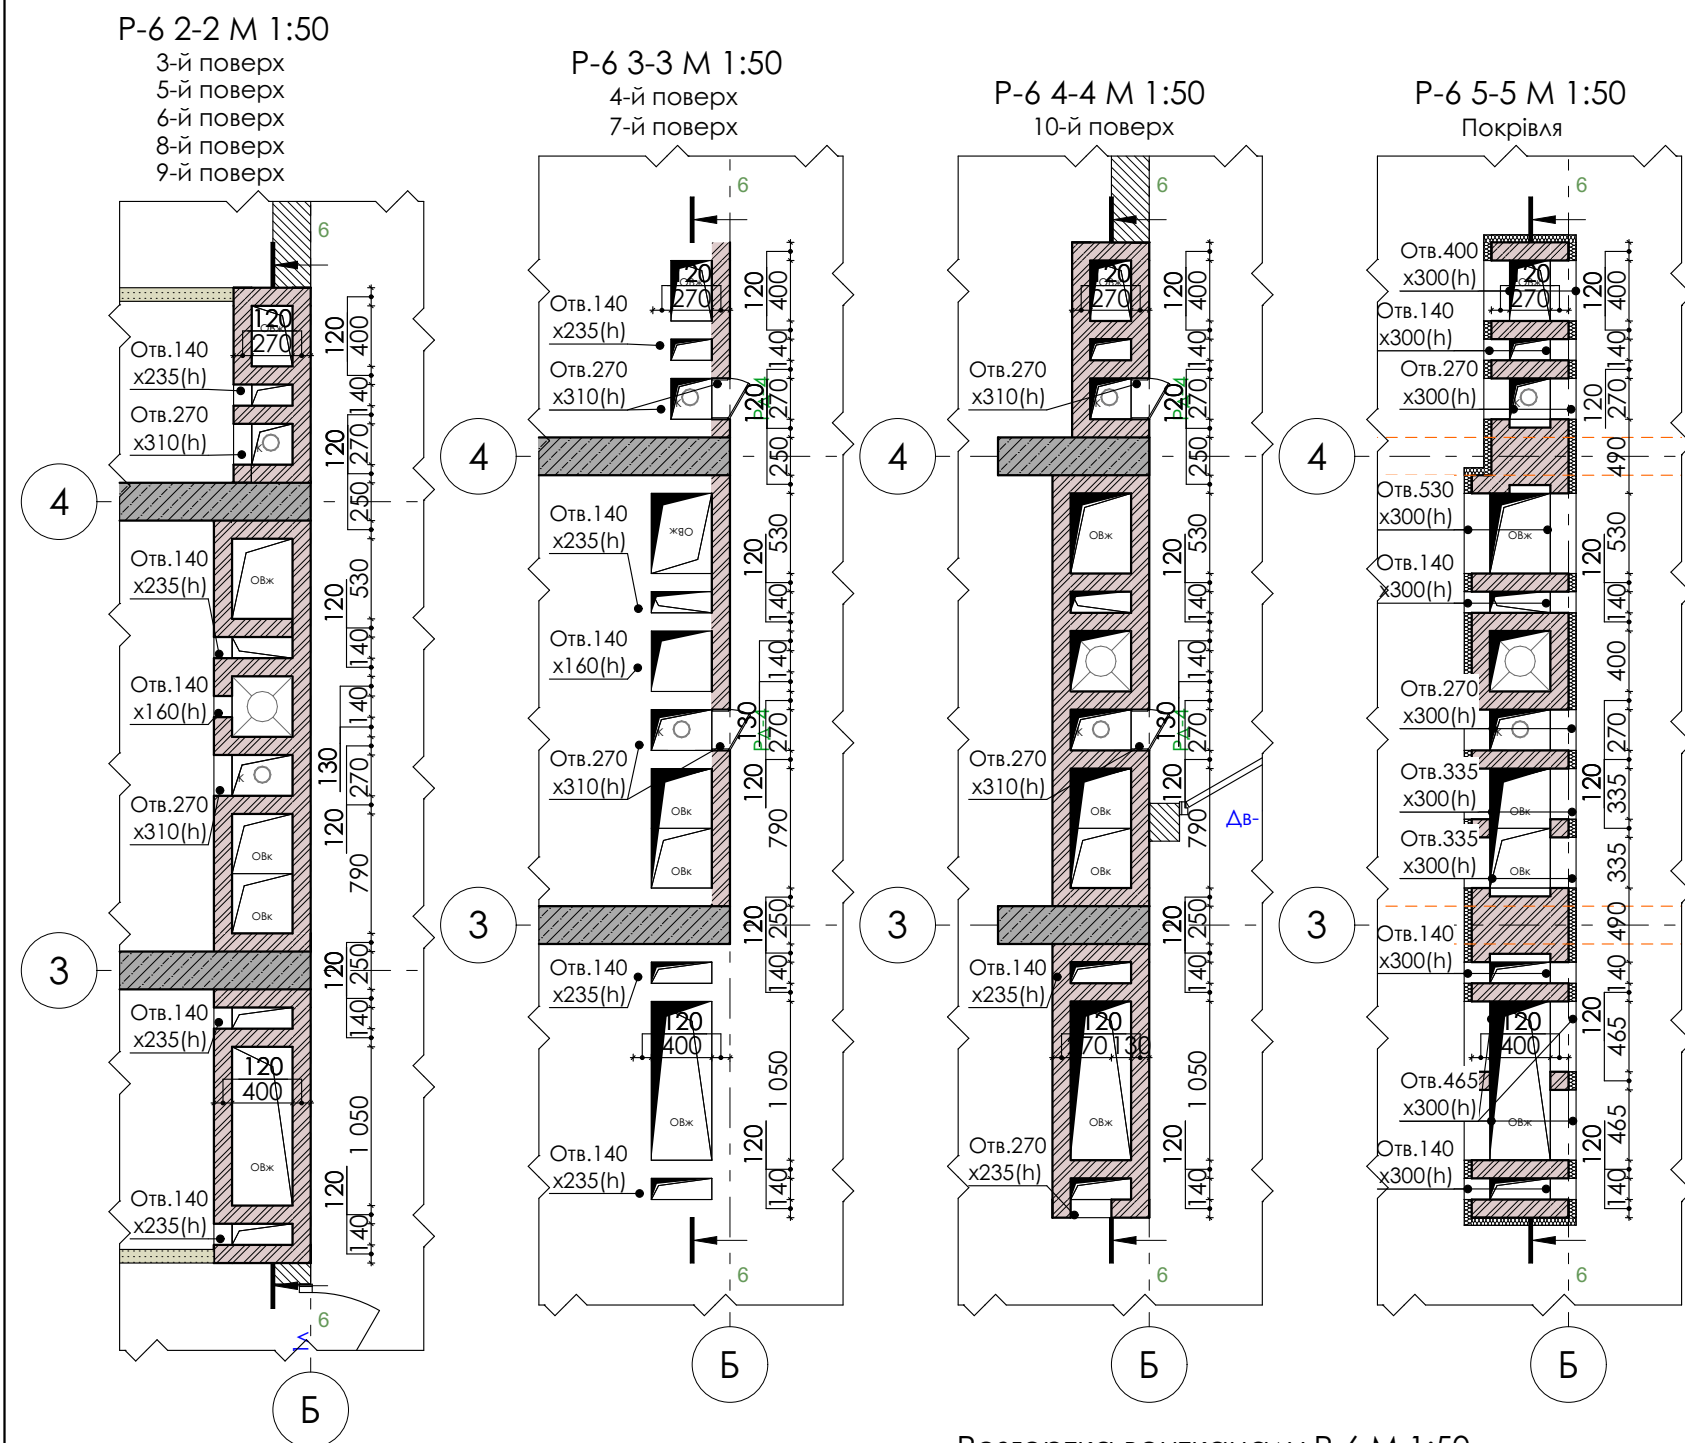

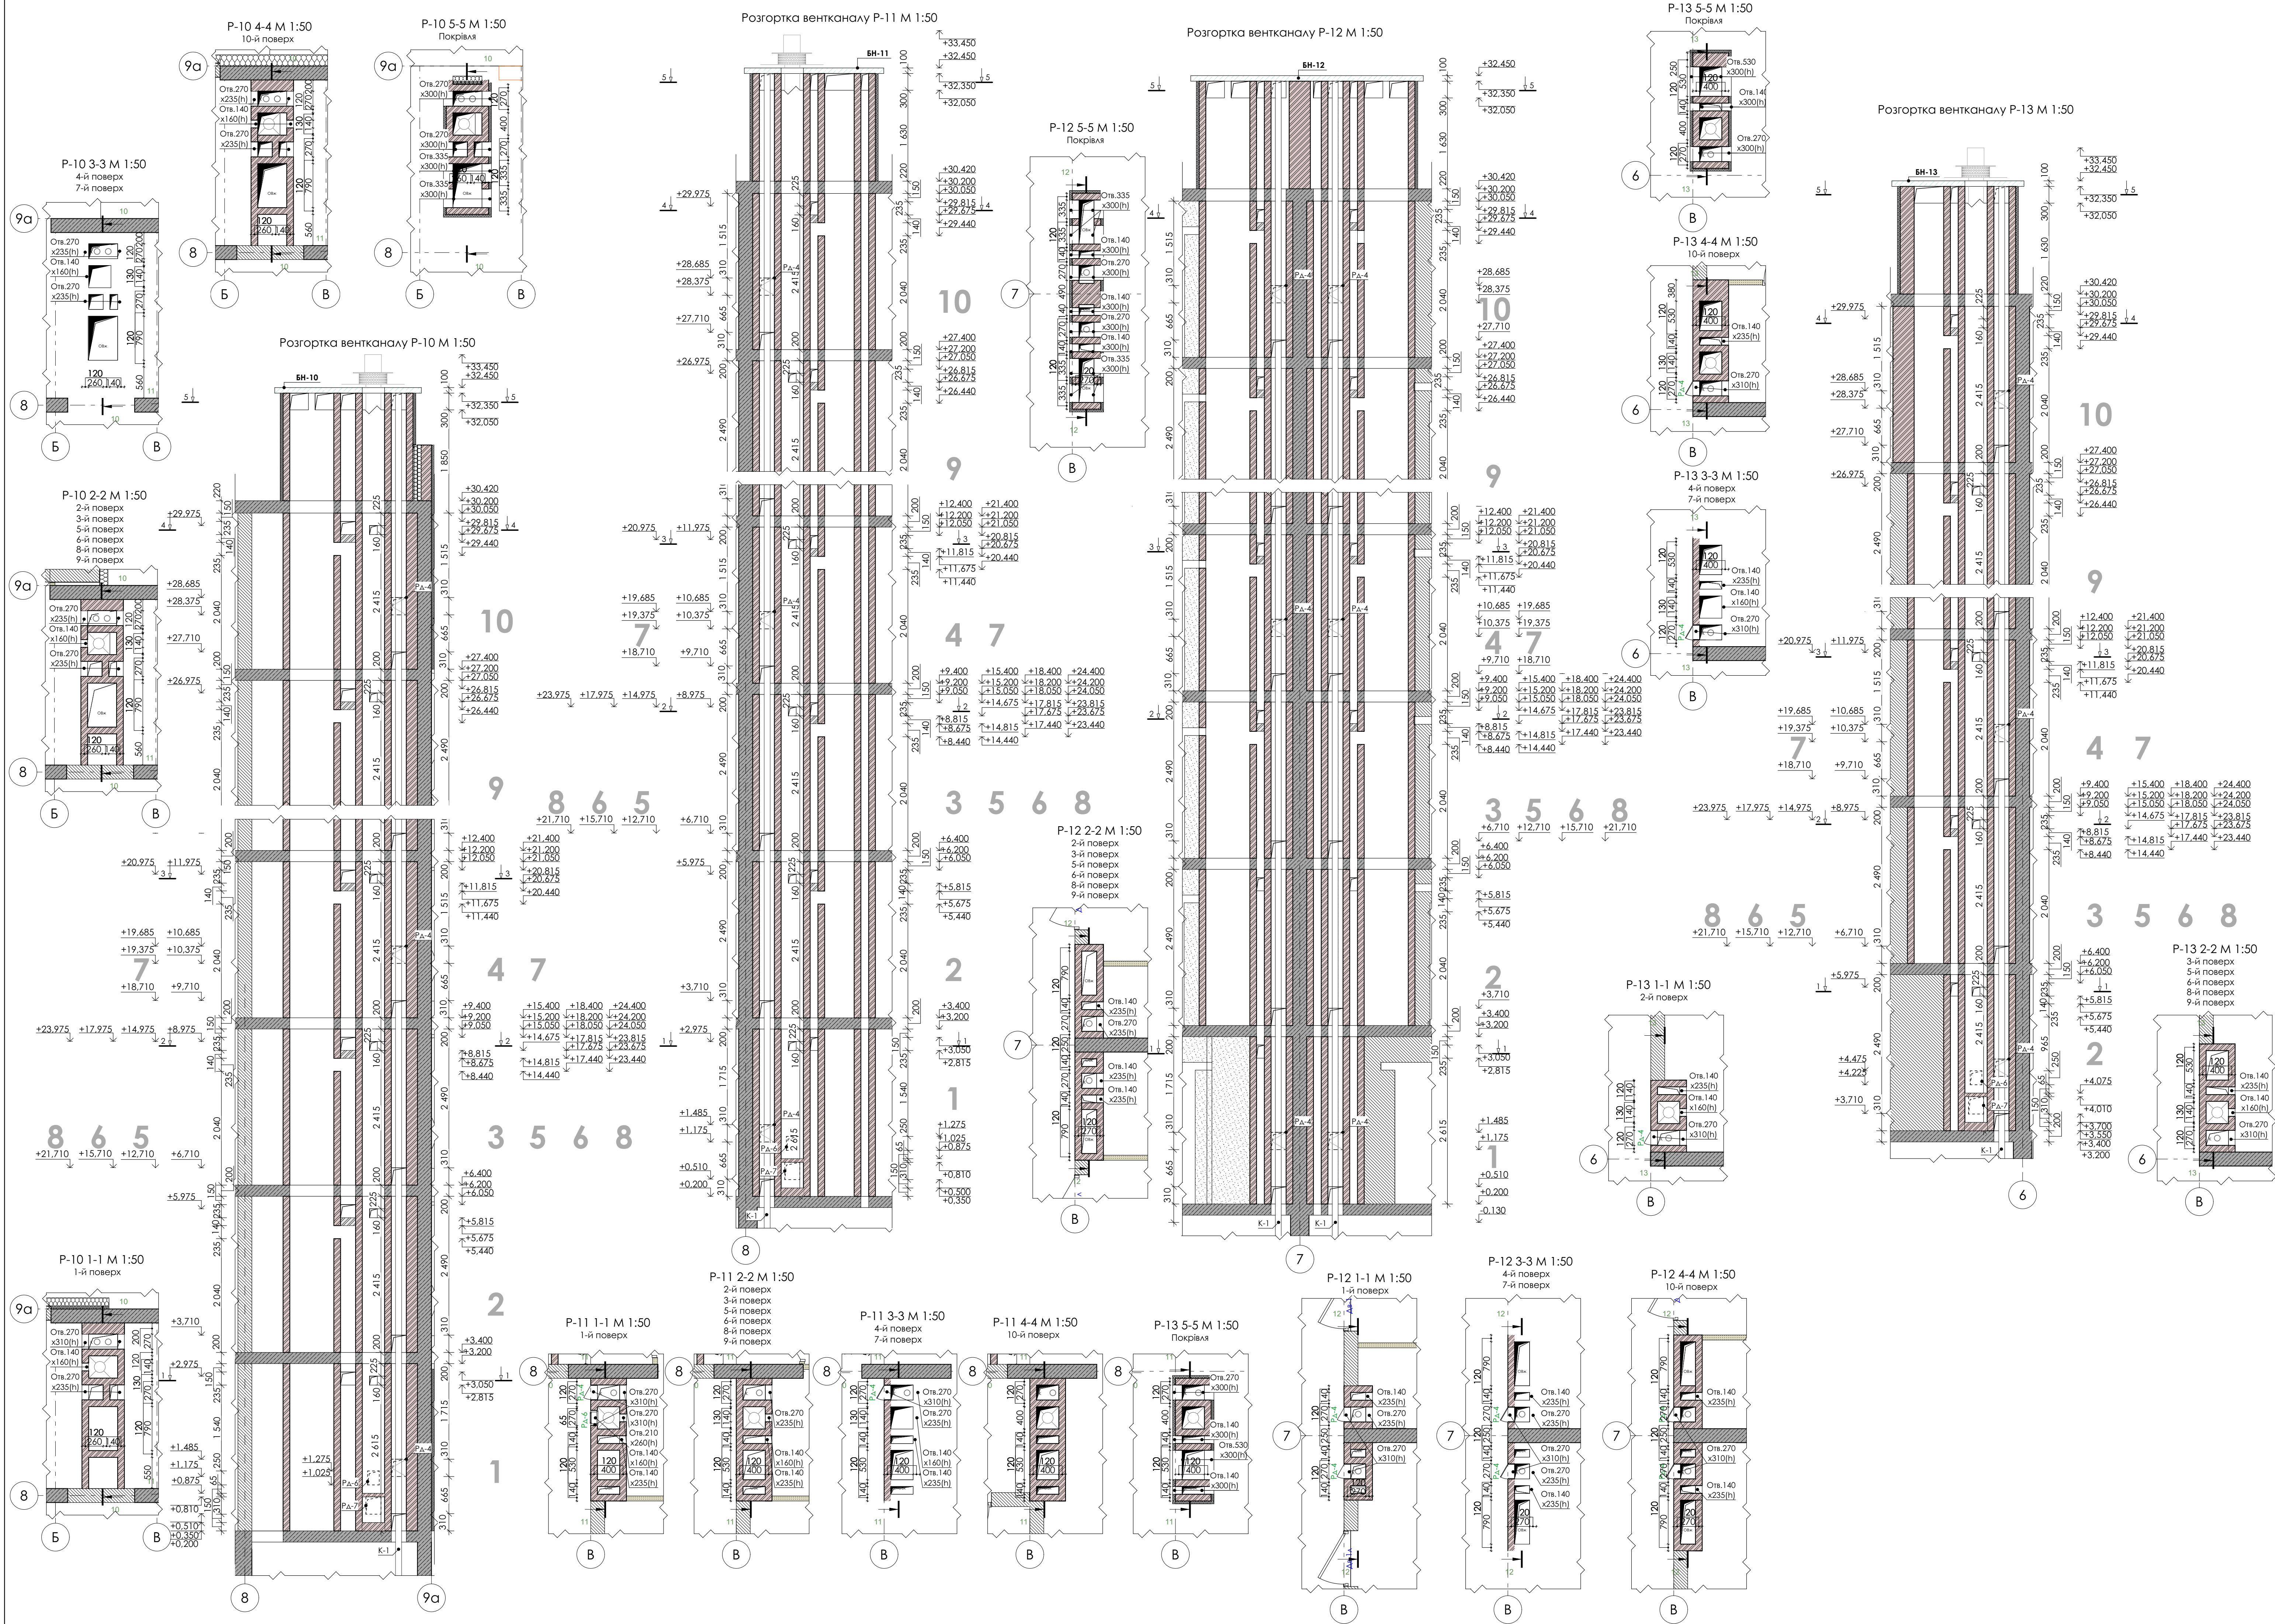


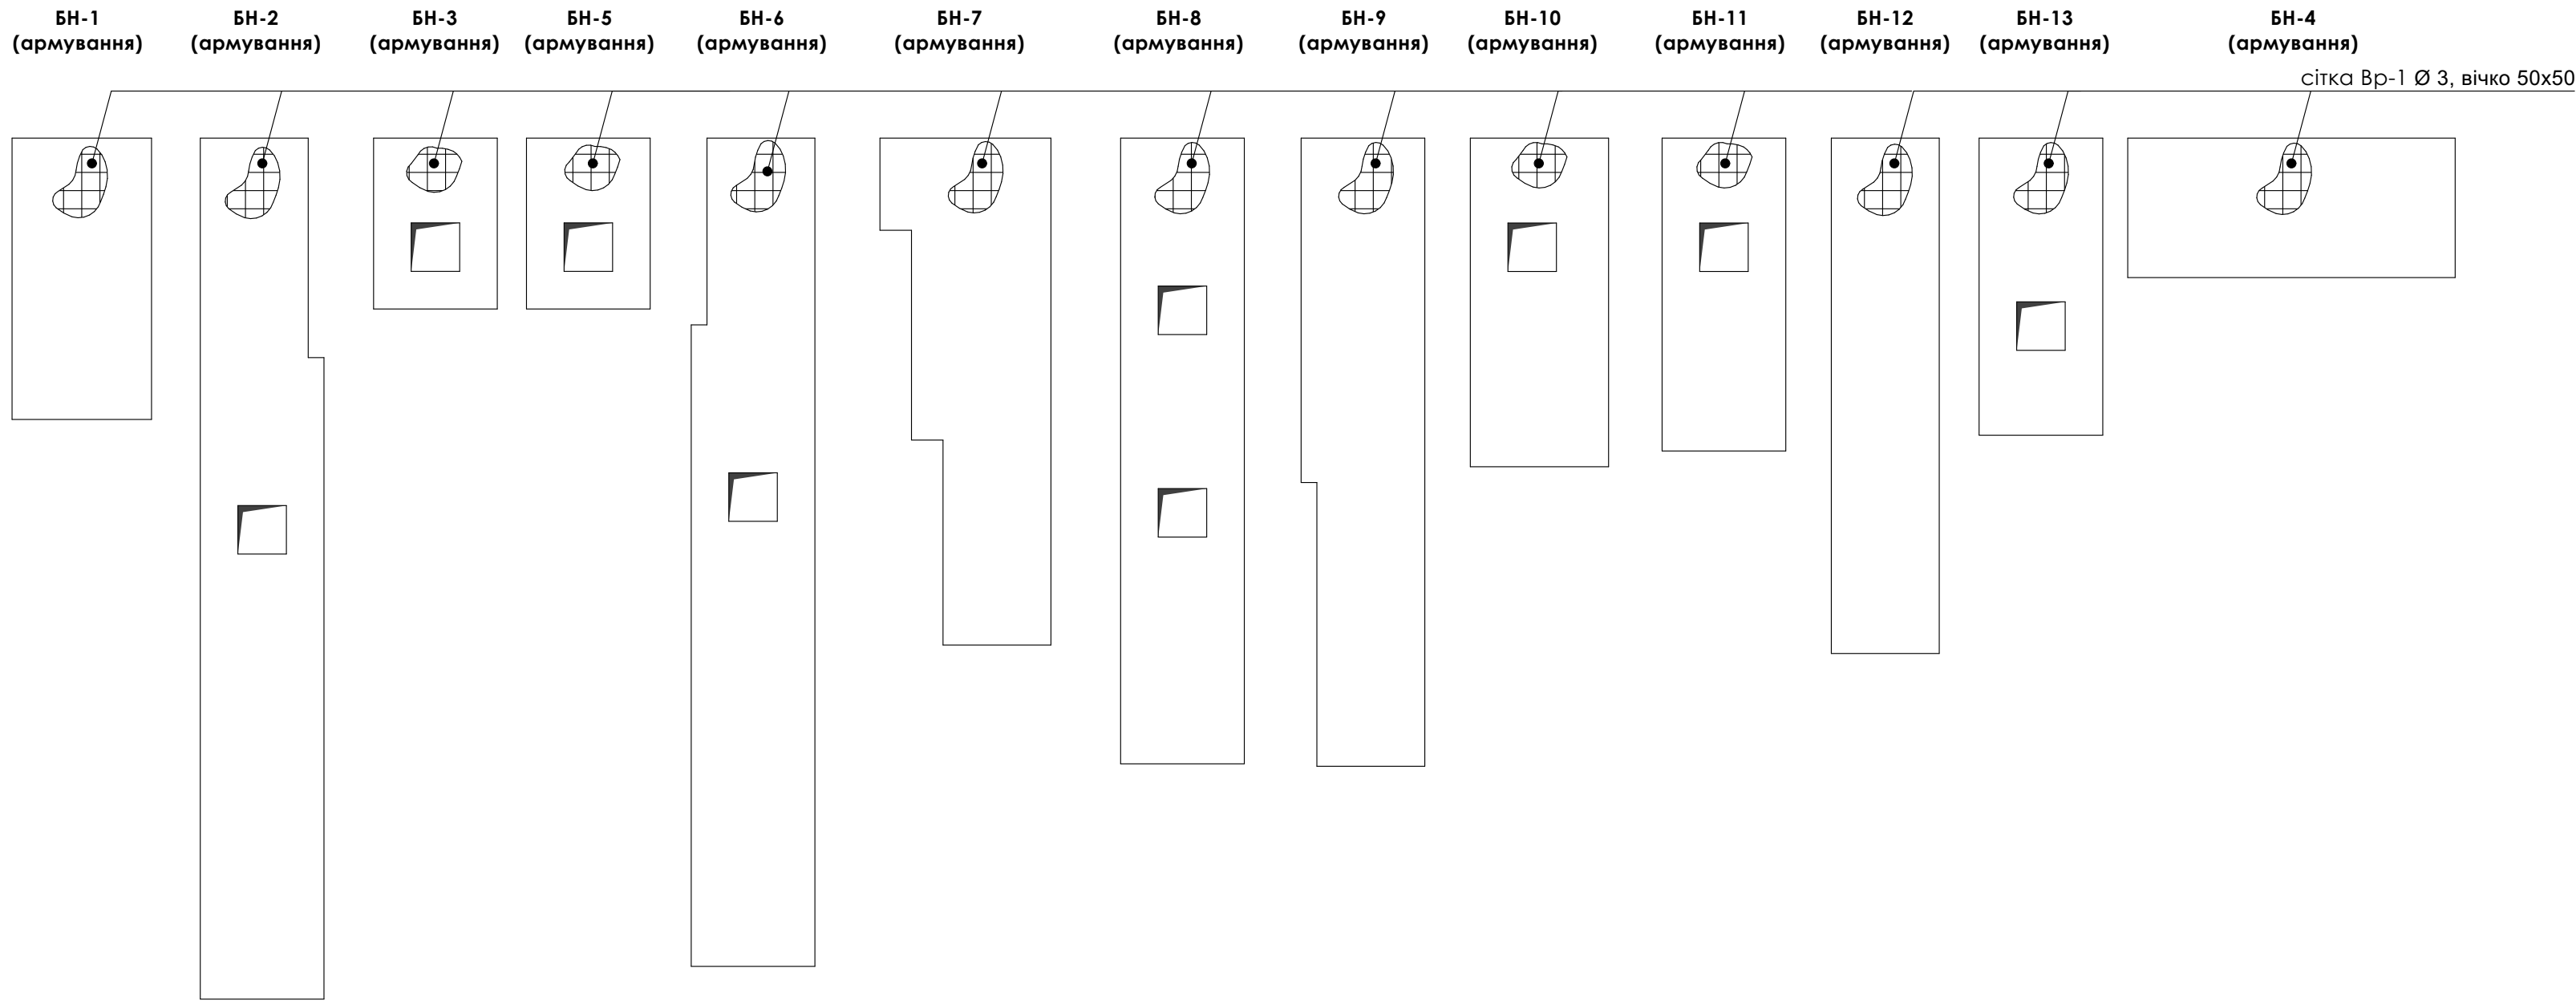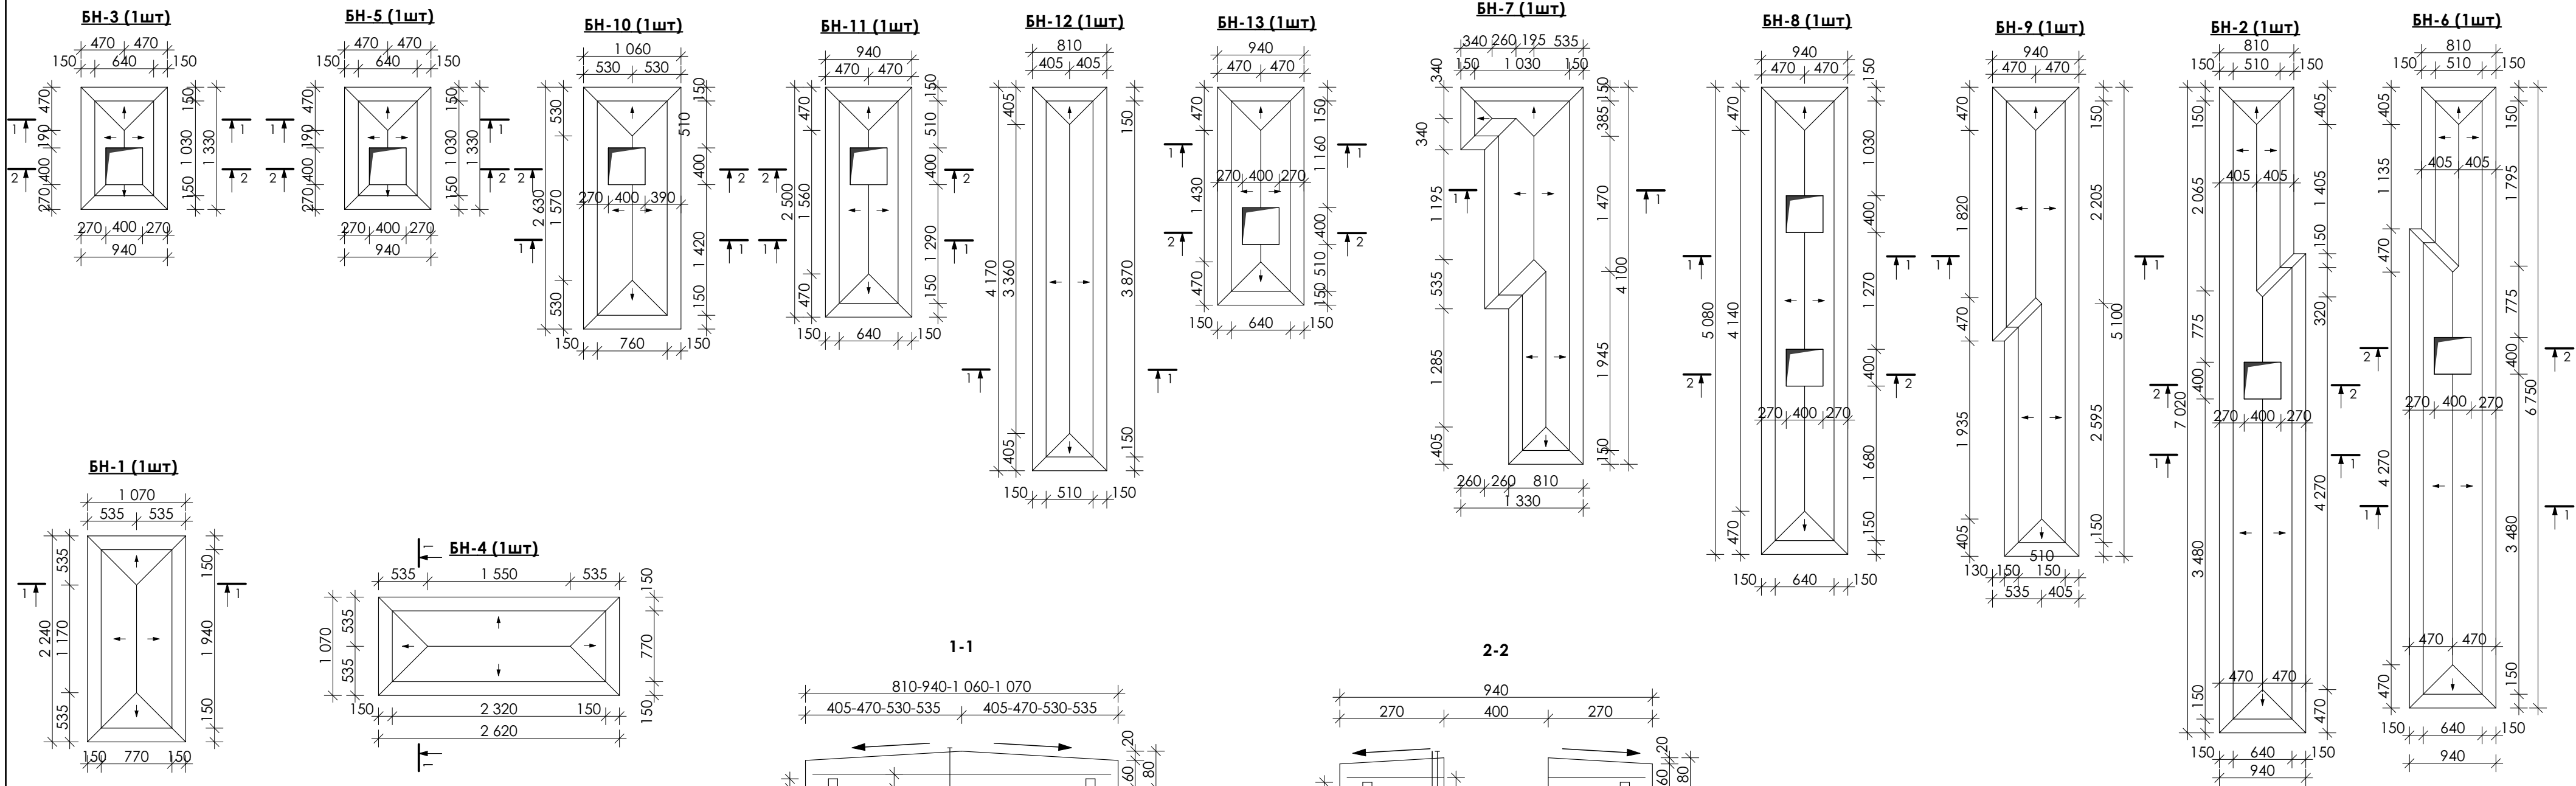

Фасад в осях 1а-9а. М 1:100




Фасад в осях Г/1-Аа. М 1:100

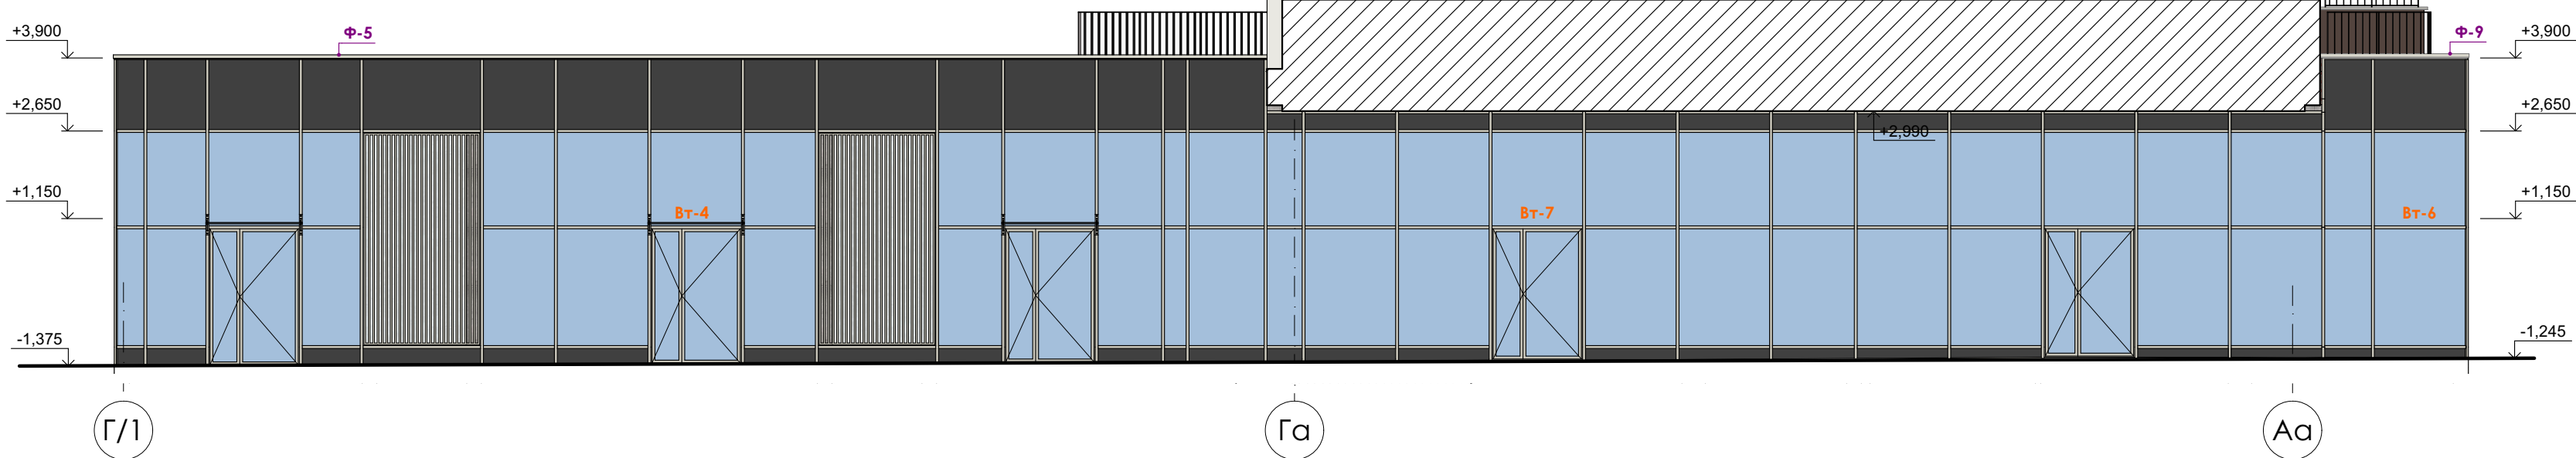

Фасад в осях Аа-Г/1. М 1:100




Фасад в осях Аа. М 1:100

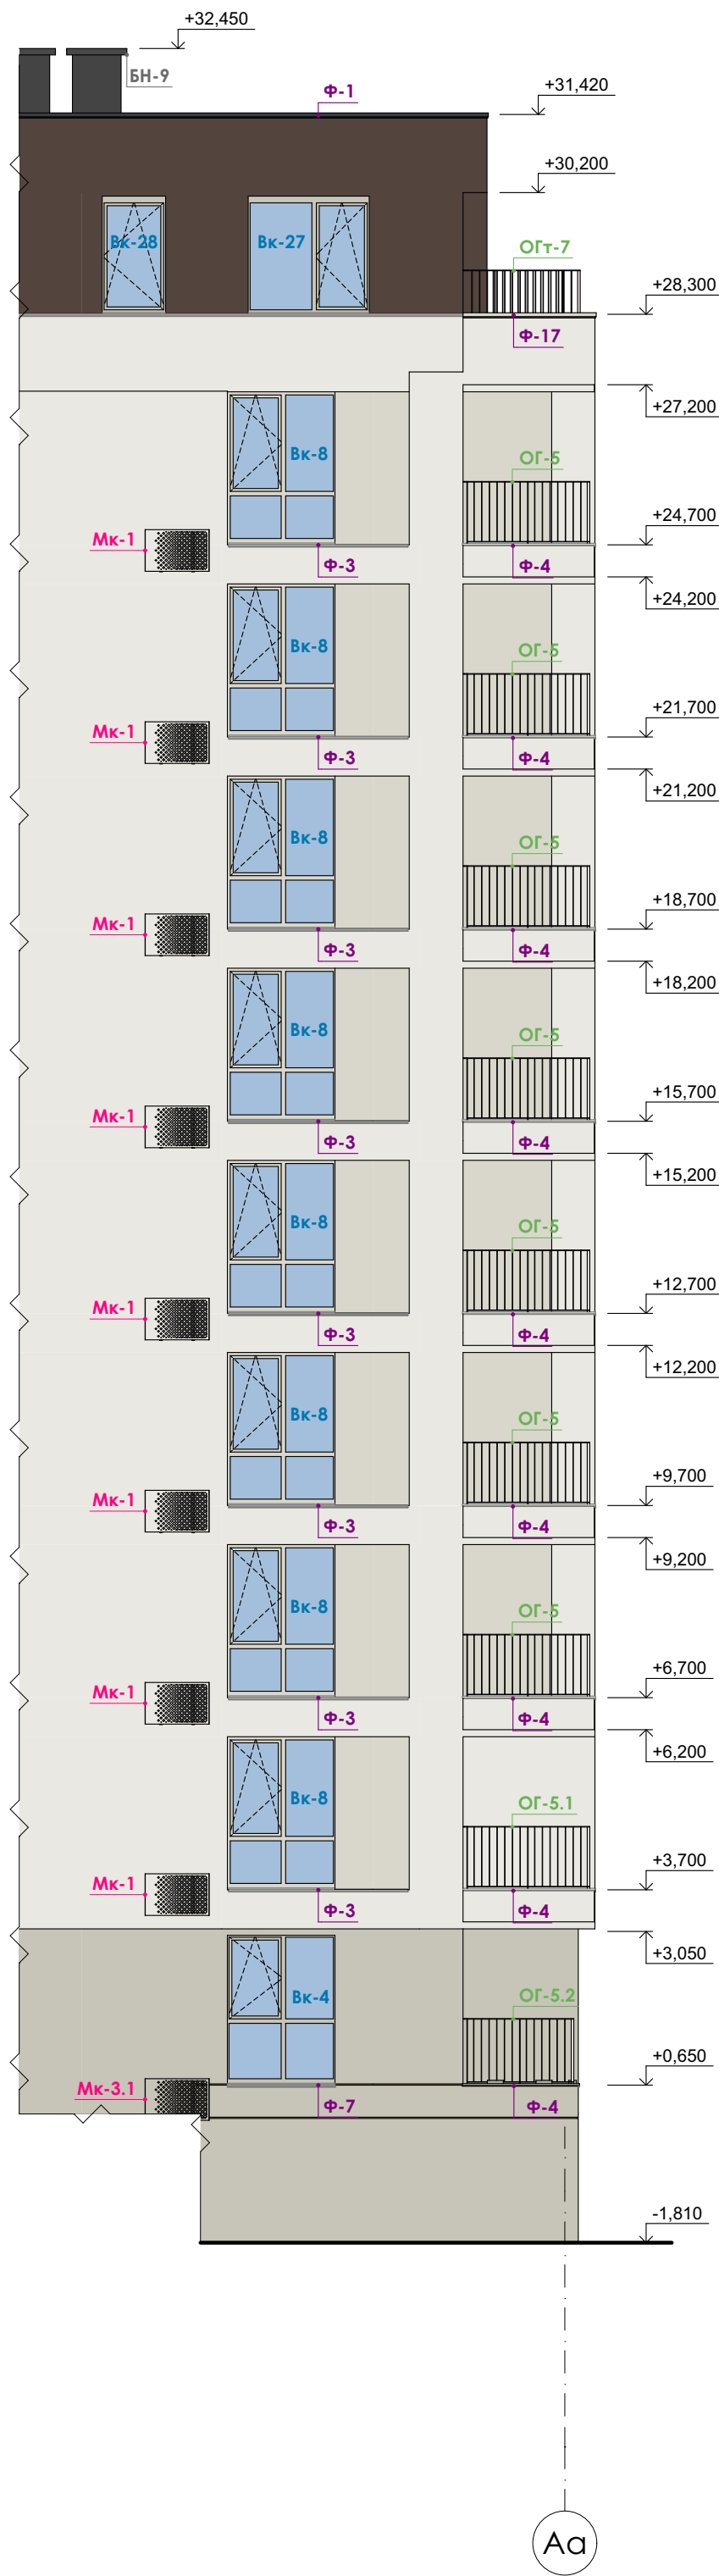


Фасад в осях 9а-1а. М 1:100



Фасад в осях Аа-Га. М 1:100

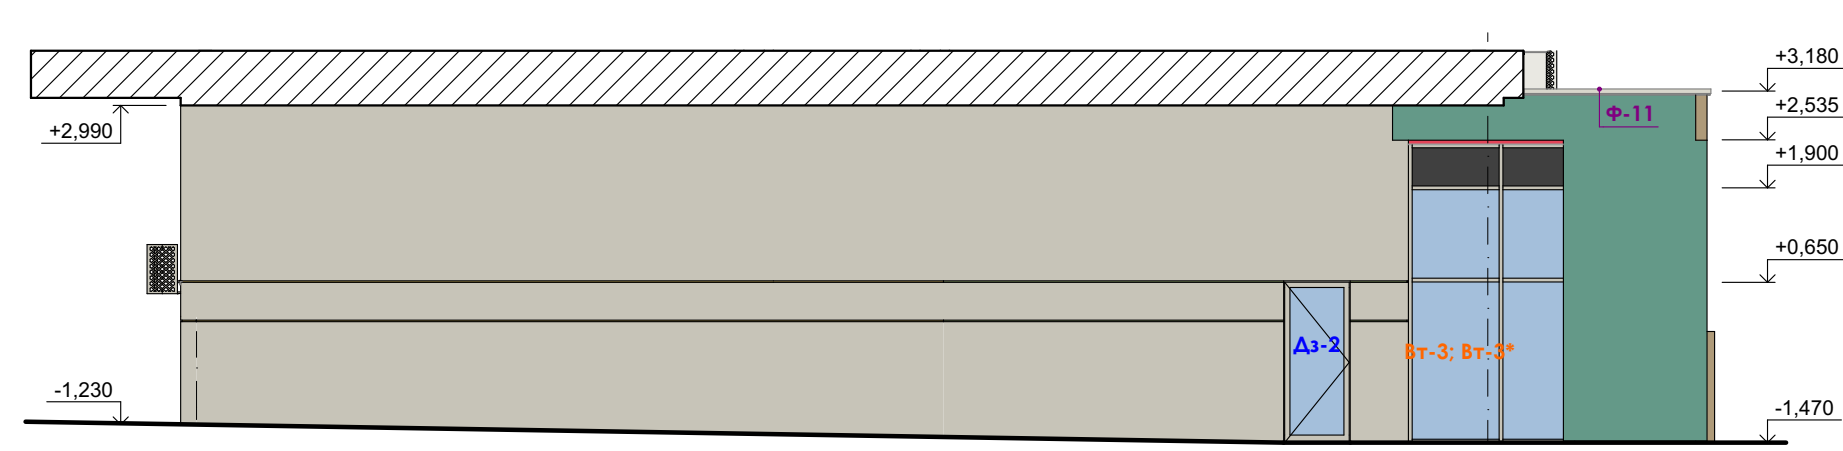

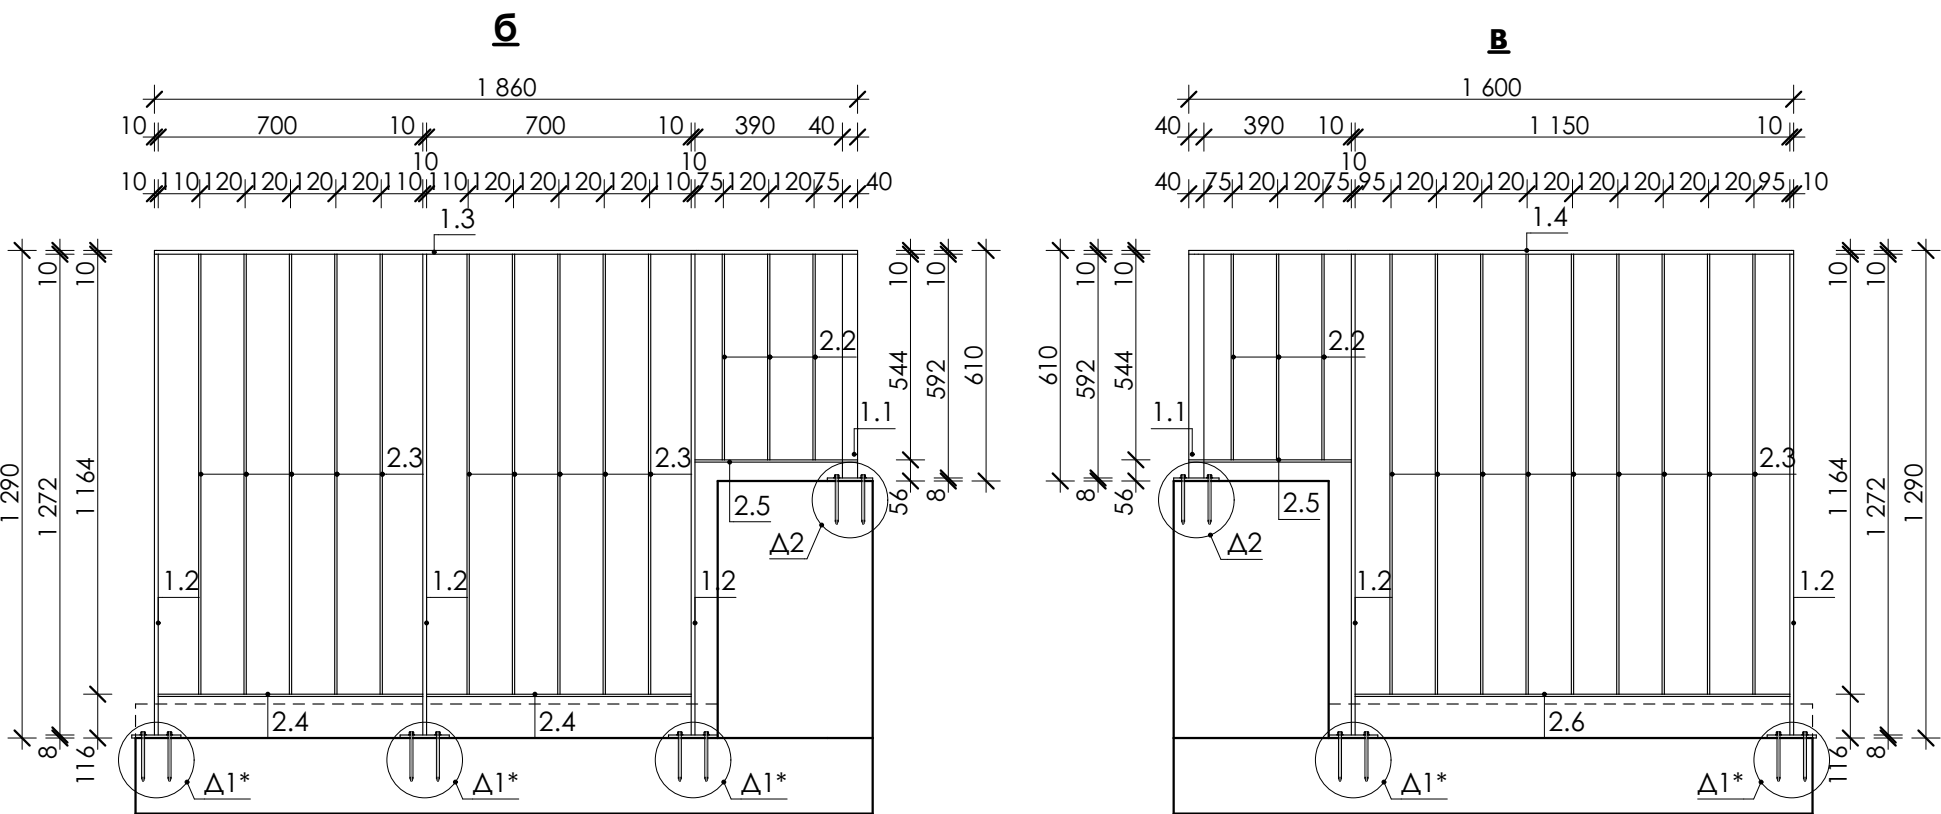

1-1


2-2

A1*
M1:10







A1
M1:10

6 - Анкер-шуруп HUS4-HF 10x150 (бетон)





цегла повнотіла а - Клеєвий анкер НІТ-НУ 170 500/2-ЕЕ + Анкерна шпилька HAS-U 5.8 HDG M10x130

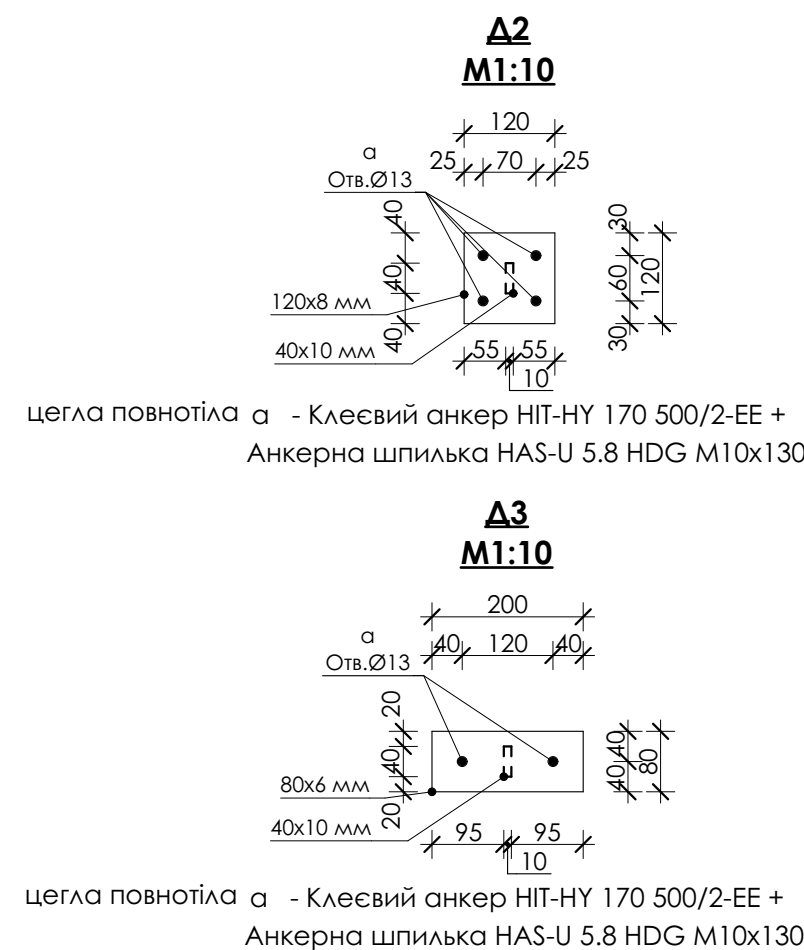











ОГ-2

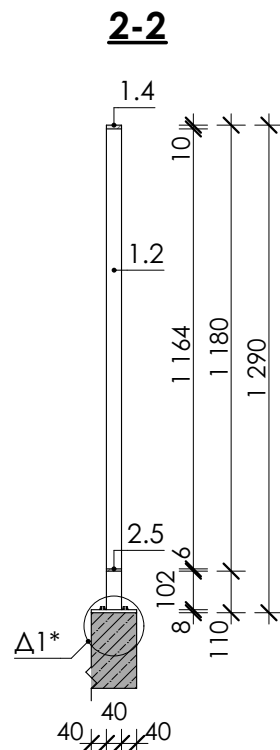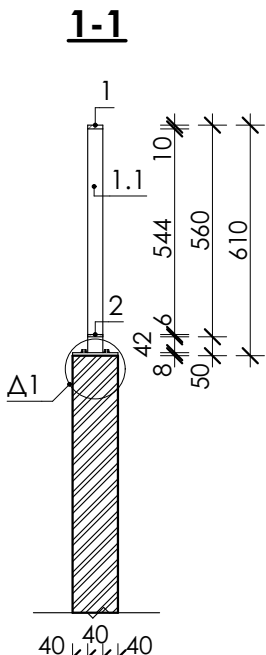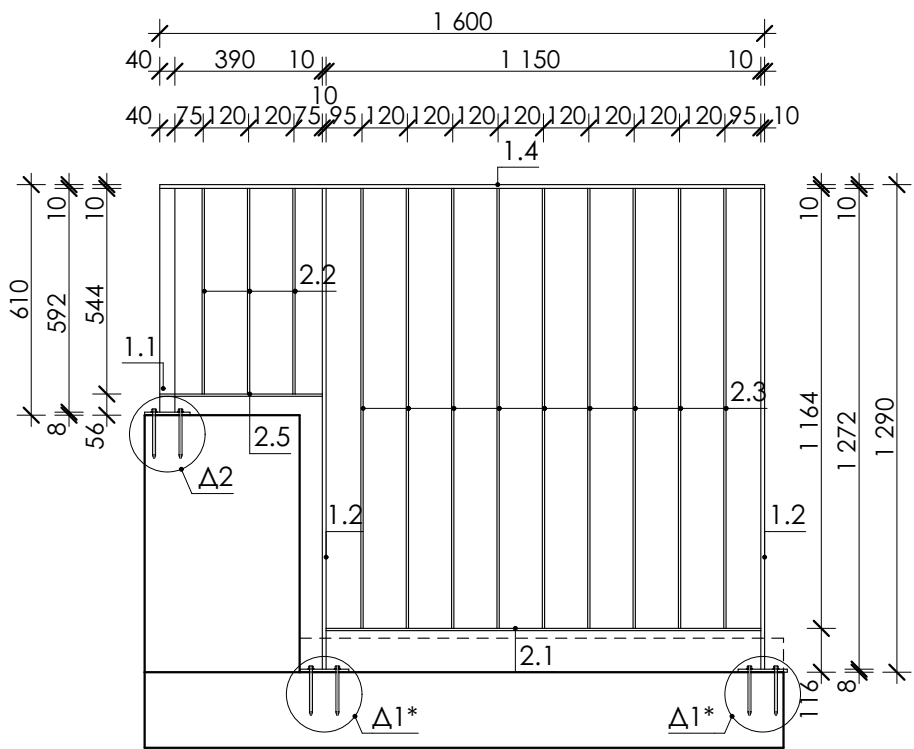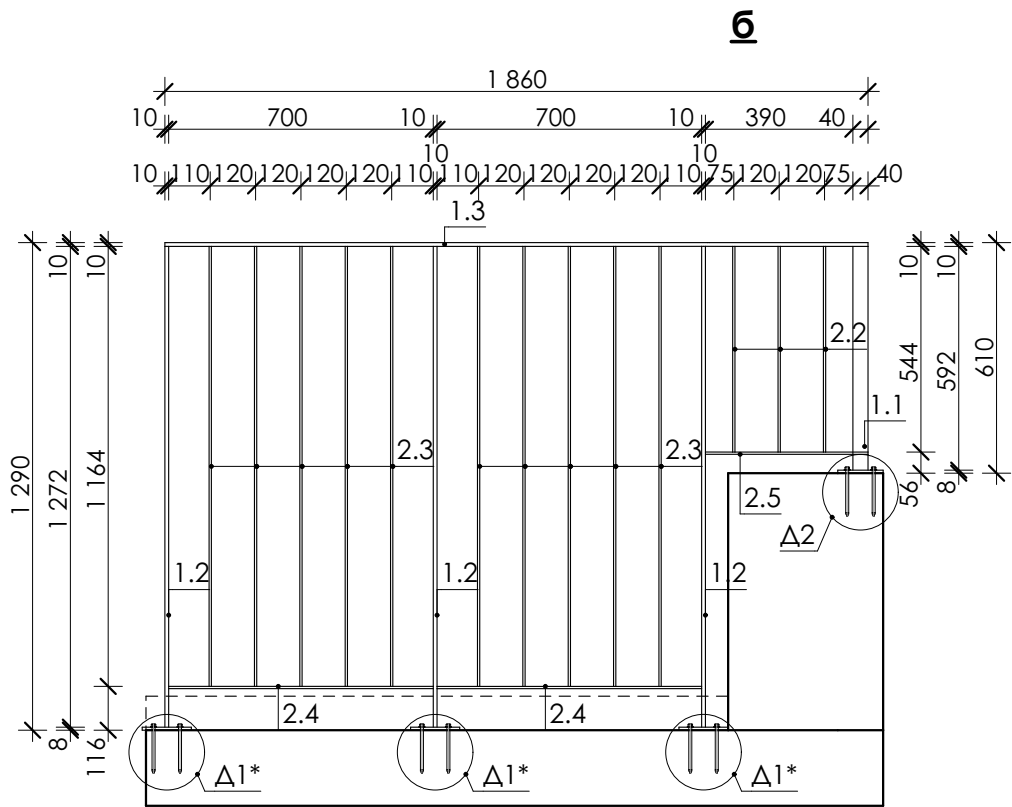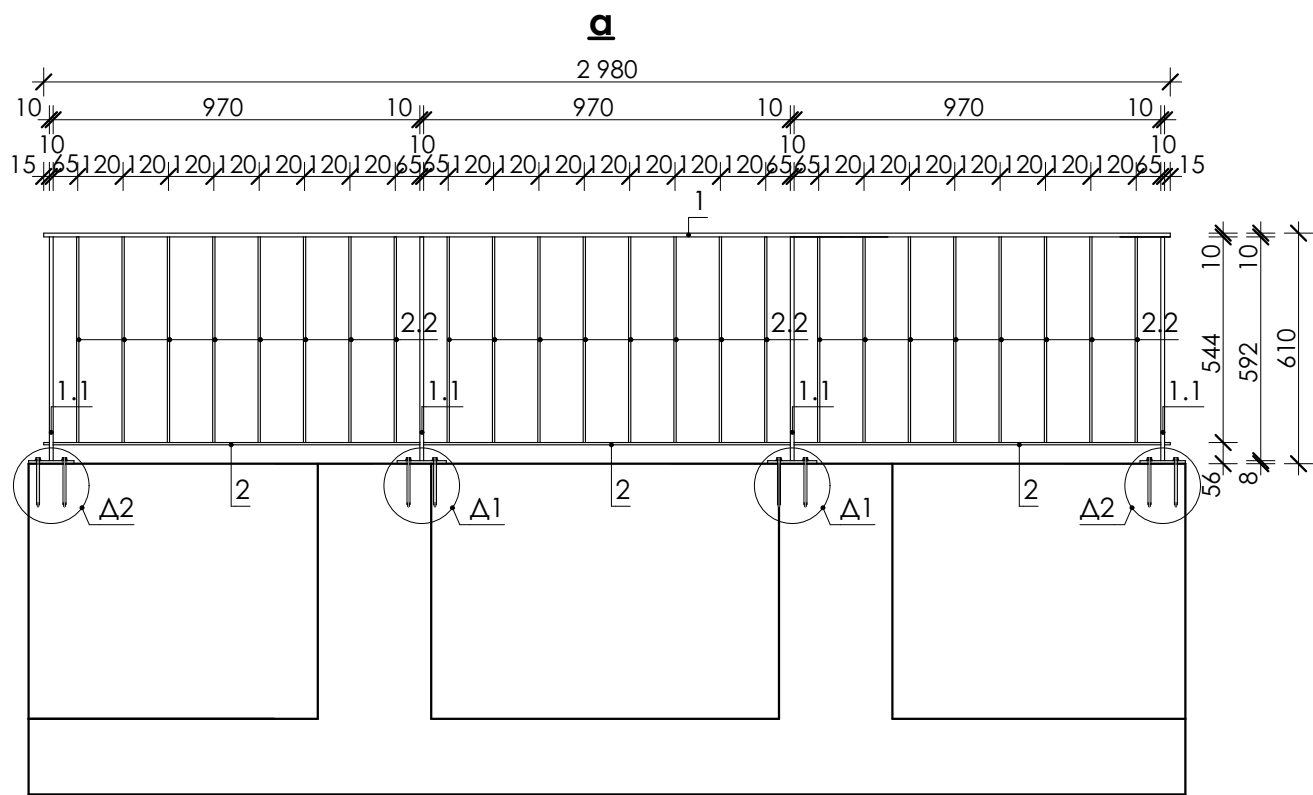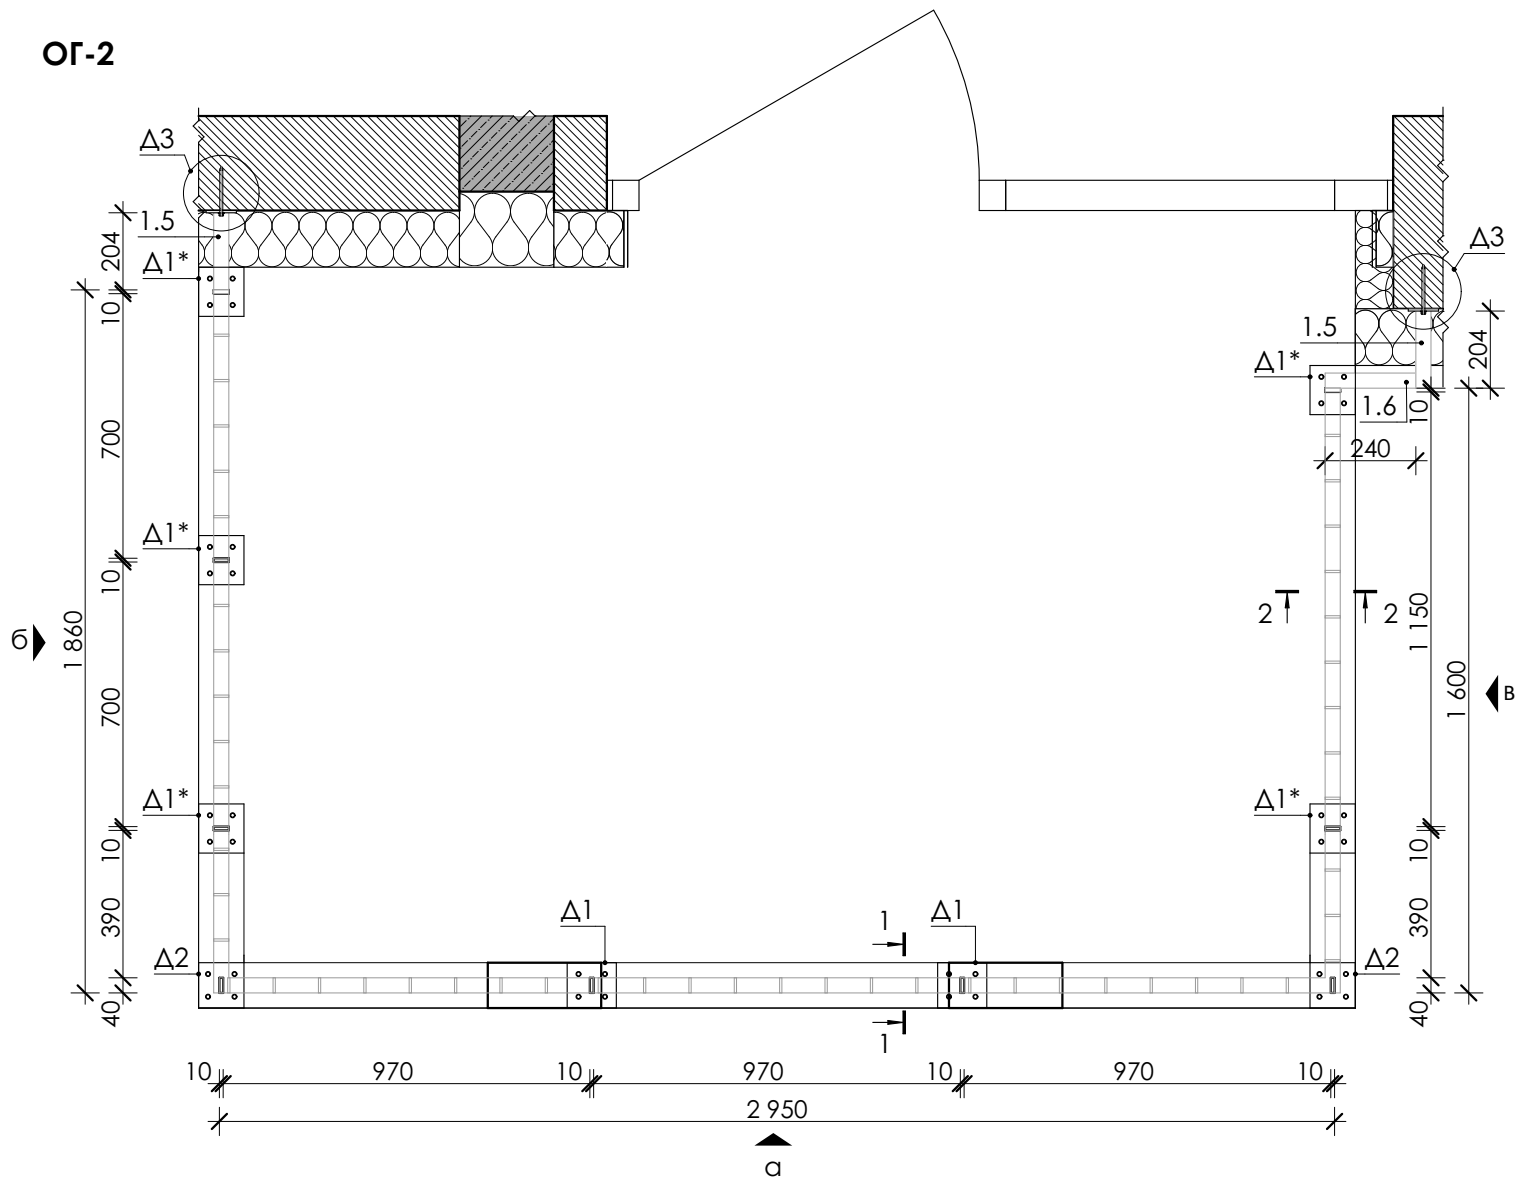

Марка поз.	Позначення	Найменування	Л,м	К-сть,шт	Маса 1 м.п.,кг	Маса од., кг	Загальн а Л,м	Загальні витрати кг на 1шт.
ОГ-2								
1	ΔСТУ 4747-2007	□ 40x10	2,98	1	3,14	9,36	2,98	9,36
1.1	ΔСТУ 4747-2007	□ 40x10	0,592	4	3,14	1,86	2,37	7,44
1.2	ΔСТУ 4747-2007	□ 40x10	1,272	5	3,14	3,99	6,36	19,97
1.3	ΔСТУ 4747-2007	□ 40x10	1,86	1	3,14	5,84	1,86	5,84
1.4	ΔСТУ 4747-2007	□ 40x10	1,6	1	3,14	5,02	1,60	5,02
1.5	ΔСТУ 4747-2007	□ 40x10	0,204	2	3,14	0,64	0,41	1,28
1.6	ΔСТУ 4747-2007	□ 40x10	0,24	1	3,14	0,75	0,24	0,75
							15,82	49,66
2	ΔСТУ 4747-2007	□ 40x6	1,17	3	1,884	2,20	3,51	6,61
2.1	ΔСТУ 4747-2007	□ 40x6	1,15	1	1,884	2,17	1,15	2,17
2.2	ΔСТУ 4747-2007	□ 40x6	0,544	30	1,884	1,02	17,95	33,82
2.3	ΔСТУ 4747-2007	□ 40x6	1,164	19	1,884	2,19	22,12	41,67
2.4	ΔСТУ 4747-2007	□ 40x6	0,7	2	1,884	1,32	1,40	2,64
2.5	ΔСТУ 4747-2007	□ 40x6	0,39	2	1,884	0,73	0,78	1,47
							46,91	88,37
Δ1/Δ1*	ΔСТУ 4747-2007	— 120x8	0,13	7	7,536	0,98	0,91	6,86
Δ2	ΔСТУ 4747-2007	— 120x8	0,12	2	7,536	0,90432	0,24	1,81
Δ3	ΔСТУ 4747-2007	— 80x6	0,2	2	3,768	0,7536	0,40	1,51
							1,55	10,17
Клеєвий анкер HIT-HY 170 500/2-EE +				20				
Анкерна шпилька HAS-U 5.8 HDG M10x130				20				
Анкер-шуруп HUS4-HF 10x150 (бетон)				20				
Накладка на опору 40x10				9				
						ОГ-2		
						7 шт.		







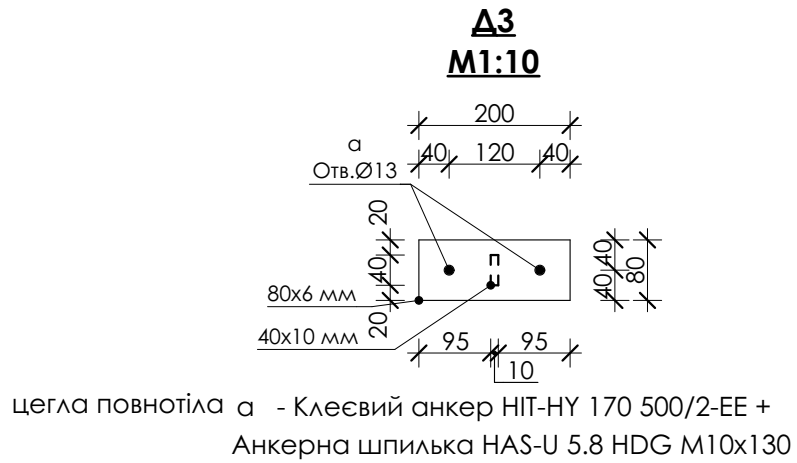
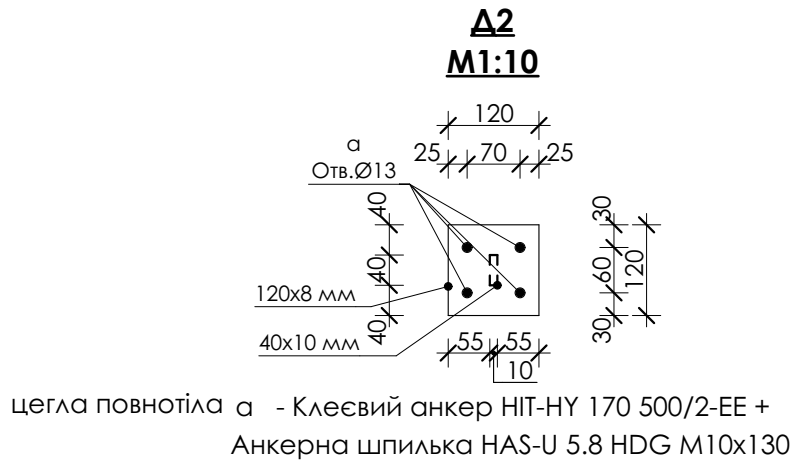
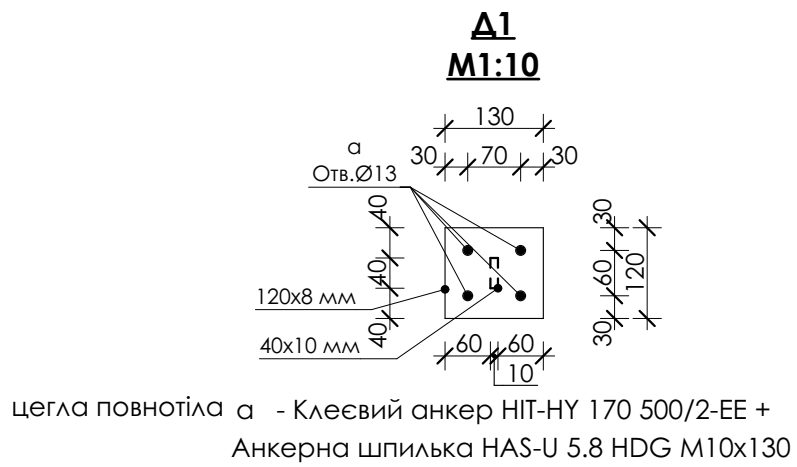
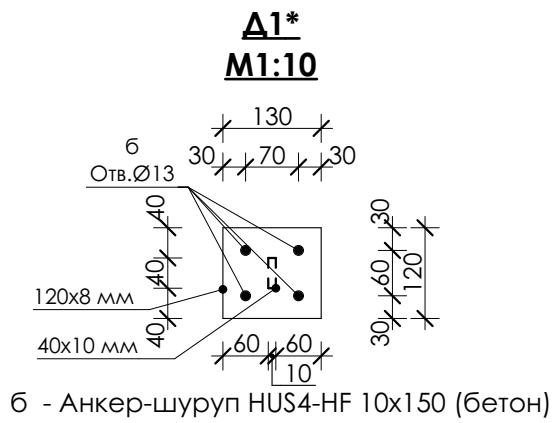


ОГ-3

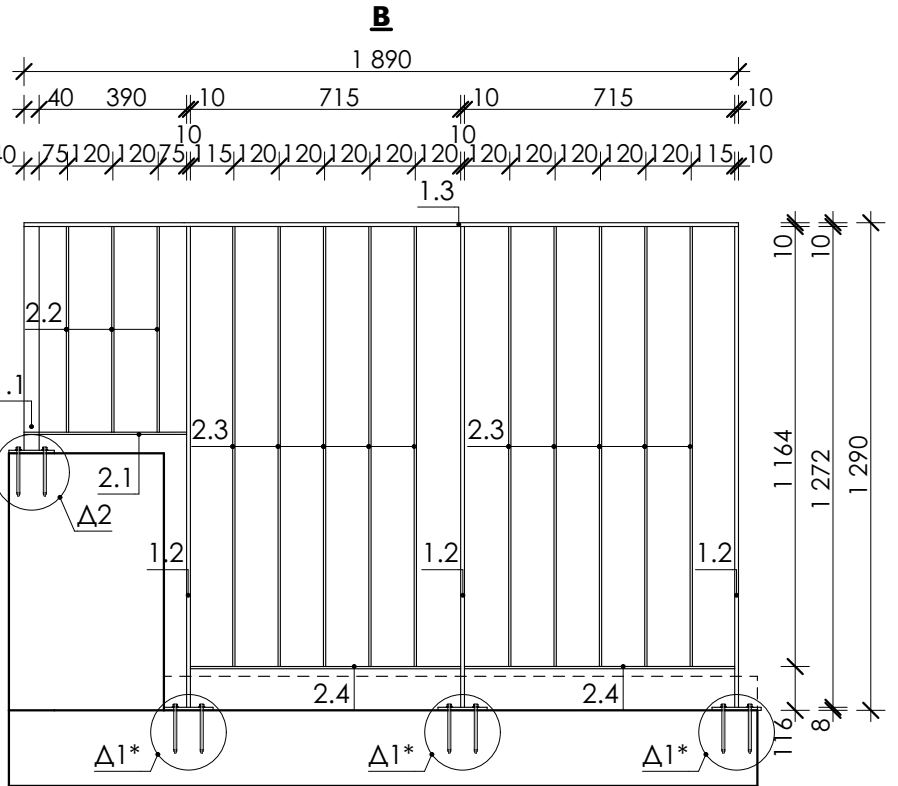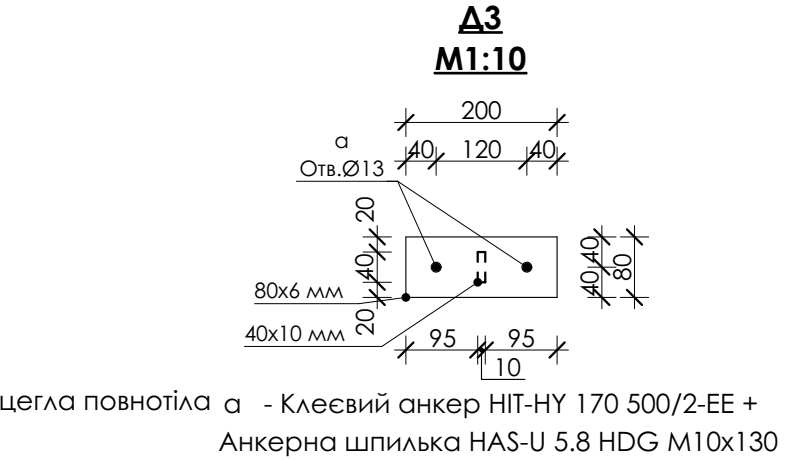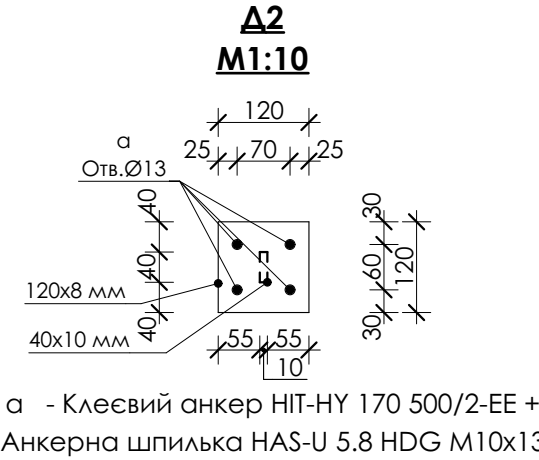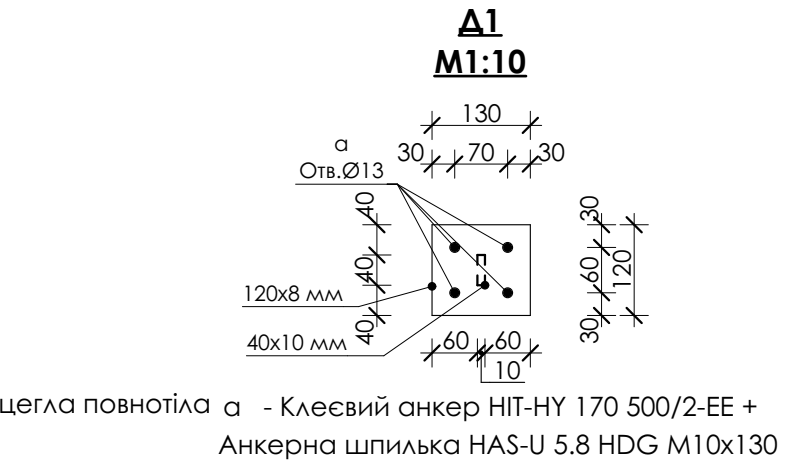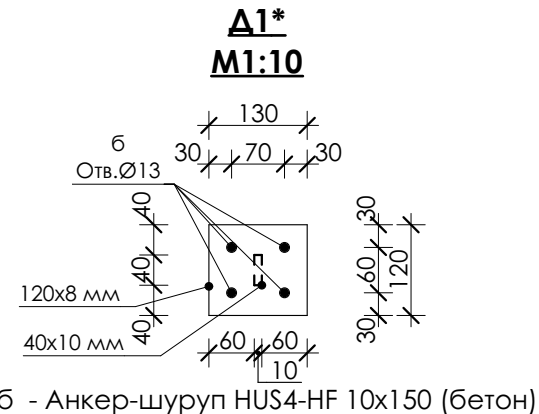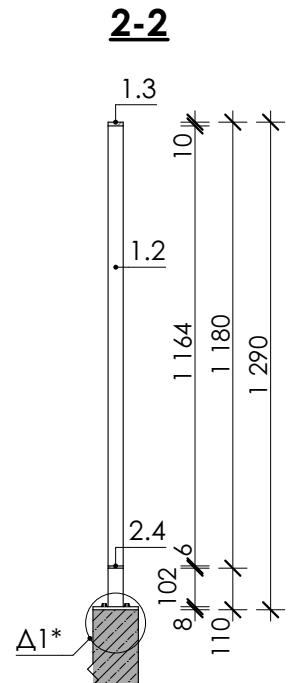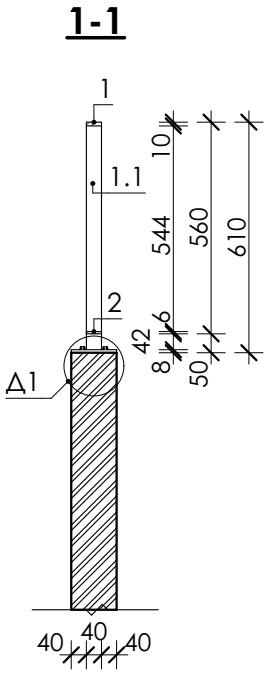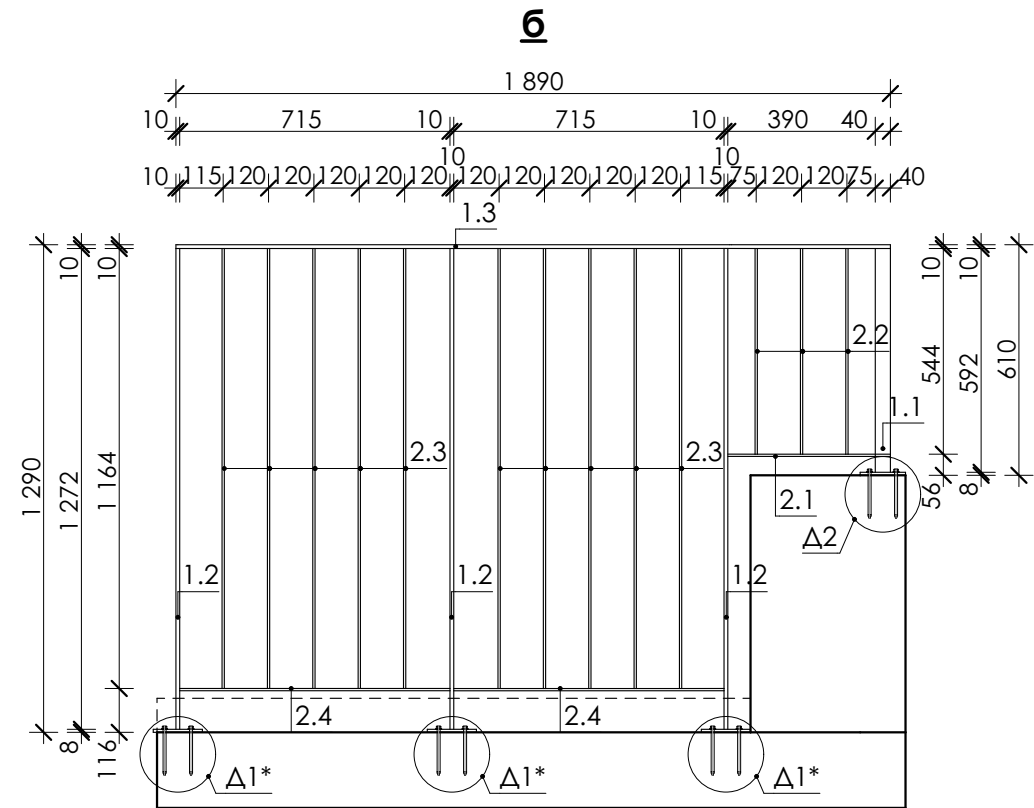
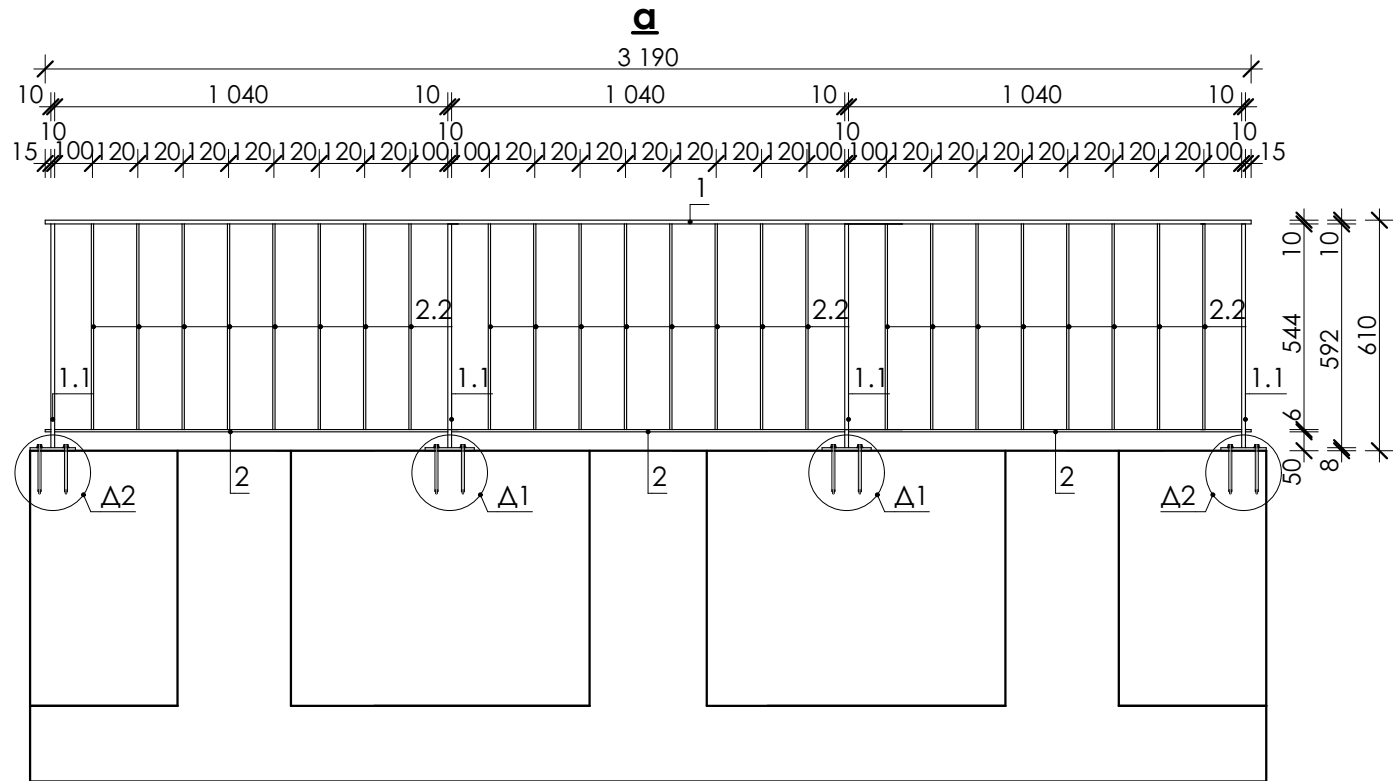
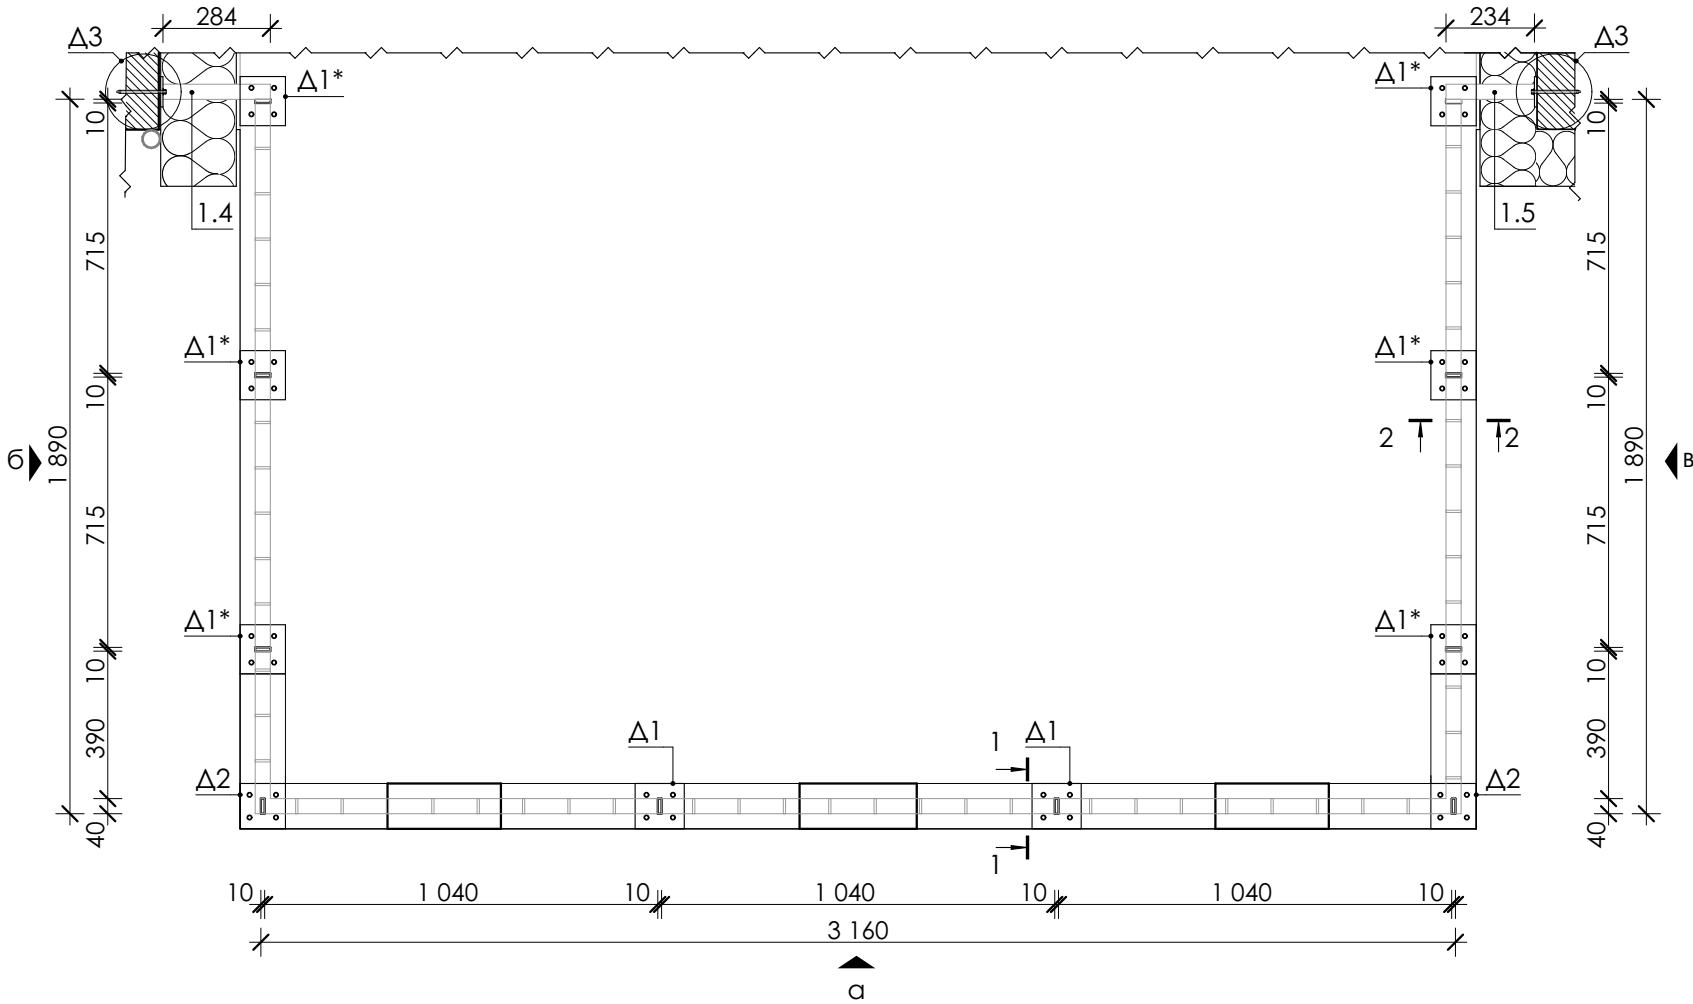


Марка поз.	Позначення	Найменування	L,м	К-сть,шт	Маса 1 м.п.,кг	Маса од., кг	Загальн а L,м	Загальні витрати кг на 1шт.
ОГ-3								
1	ΔСТУ 4747-2007	□ 40x10	3,19	1	3,14	10,02	3,19	10,02
1.1	ΔСТУ 4747-2007	□ 40x10	0,592	4	3,14	1,86	2,37	7,44
1.2	ΔСТУ 4747-2007	□ 40x10	1,272	6	3,14	3,99	7,63	23,96
1.3	ΔСТУ 4747-2007	□ 40x10	1,89	2	3,14	5,93	3,78	11,87
1.4	ΔСТУ 4747-2007	□ 40x10	0,284	1	3,14	0,89	0,28	0,89
1.5	ΔСТУ 4747-2007	□ 40x10	0,234	1	3,14	0,73	0,23	0,73
							17,49	54,91
2	ΔСТУ 4747-2007	□ 40x6	1,04	3	1,884	1,96	3,12	5,88
2.1	ΔСТУ 4747-2007	□ 40x6	0,39	2	1,884	0,73	0,78	1,47
2.2	ΔСТУ 4747-2007	□ 40x6	0,544	30	1,884	1,02	16,32	30,75
2.3	ΔСТУ 4747-2007	□ 40x6	1,164	20	1,884	2,19	23,28	43,86
2.4	ΔСТУ 4747-2007	□ 40x6	0,715	4	1,884	1,35	2,86	5,39
							46,36	87,34
Δ1/Δ1*	ΔСТУ 4747-2007	— 120x8	0,13	8	7,536	0,98	1,04	7,84
Δ2	ΔСТУ 4747-2007	— 120x8	0,12	2	7,536	0,90432	0,24	1,81
Δ3	ΔСТУ 4747-2007	— 80x6	0,2	2	3,768	0,7536	0,40	1,51
							1,68	11,15
Клеєвий анкер HIT-HY 170 500/2-EE +					20			
Анкерна шпилька HAS-U 5.8 HDG M10x130					20			
Анкер-шуруп HUS4-HF 10x150 (бетон)					24			
Накладка на опору 40x10					10			
						ОГ-3		7 шт.

ОГ-4

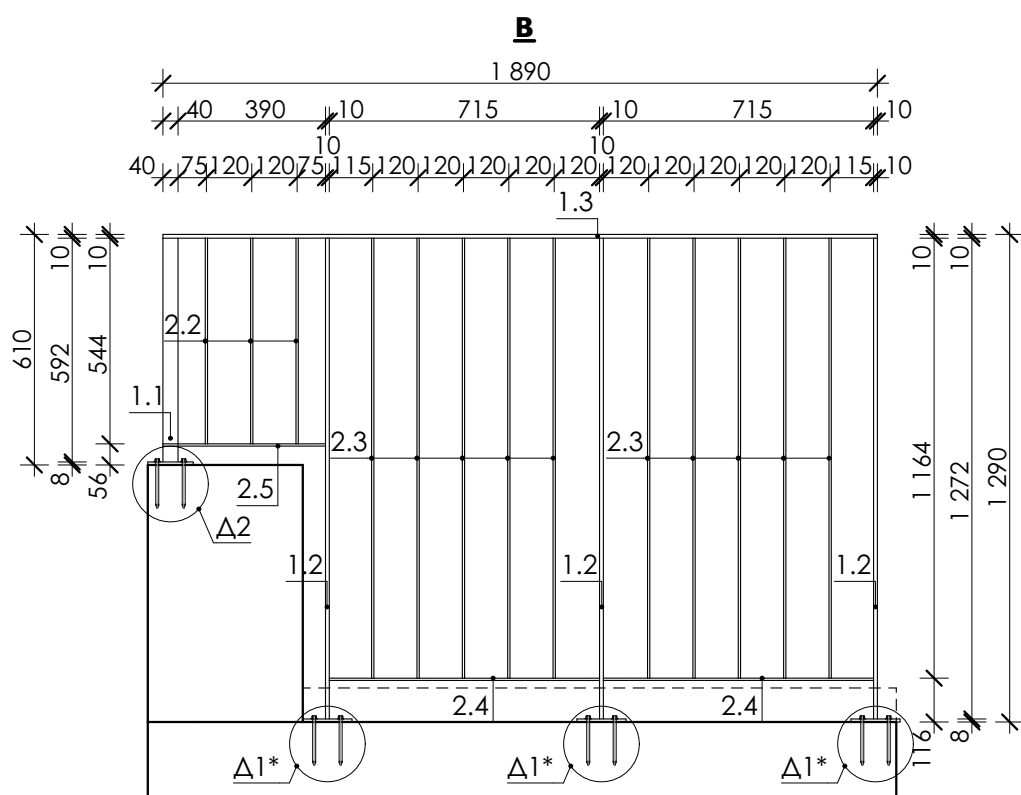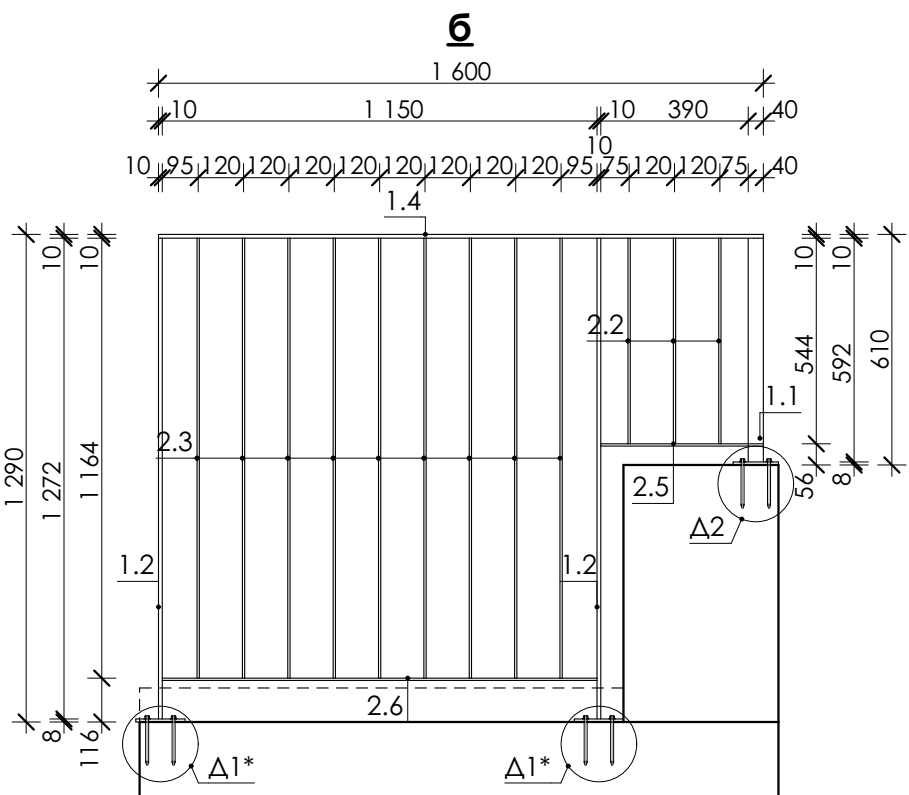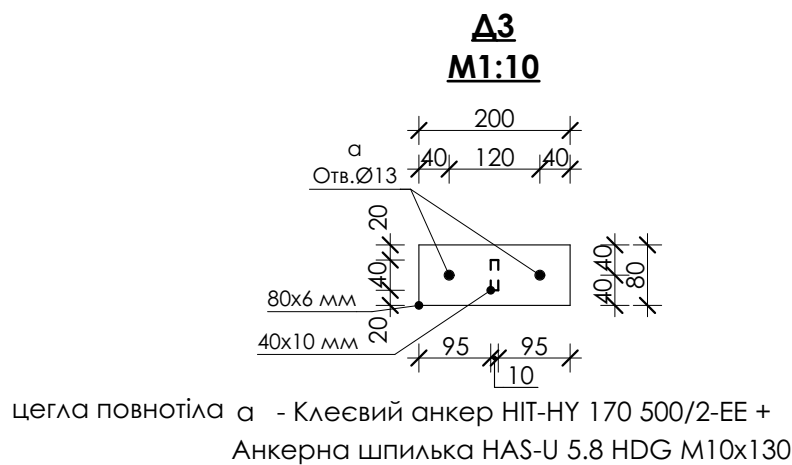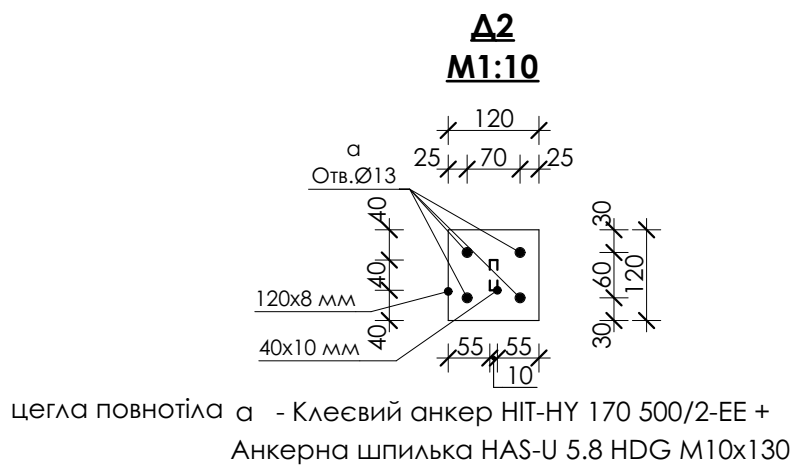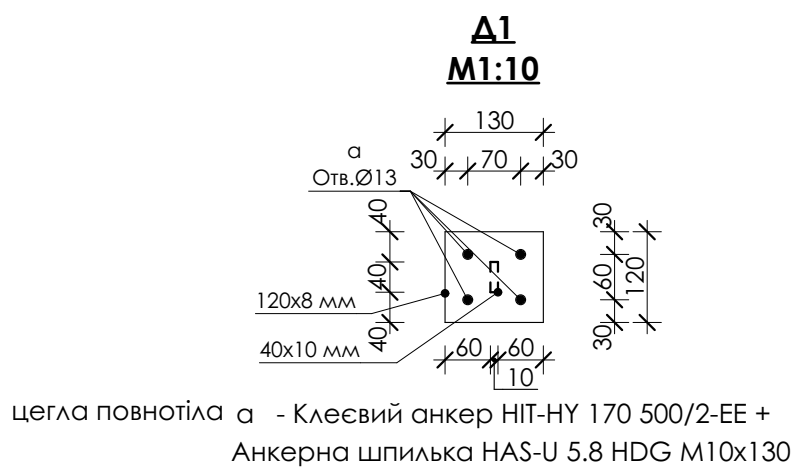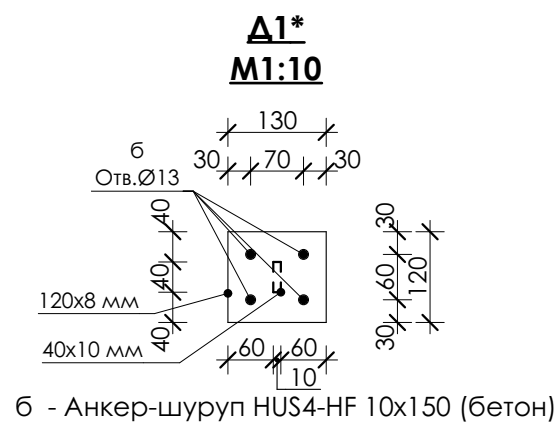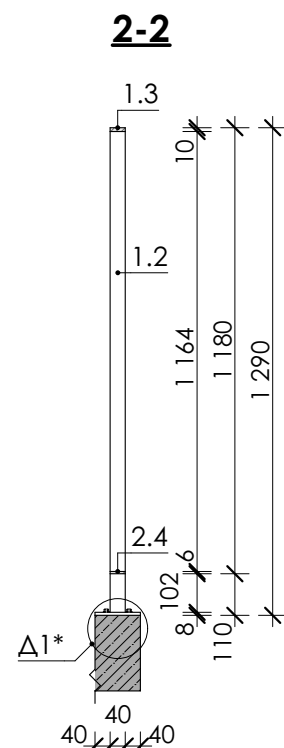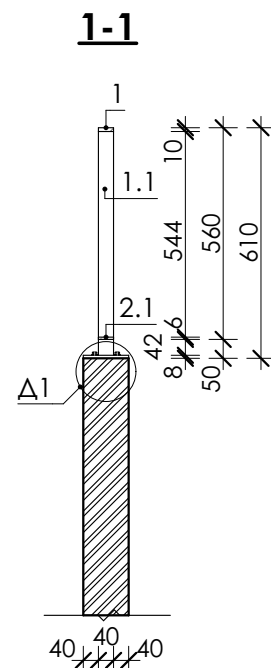
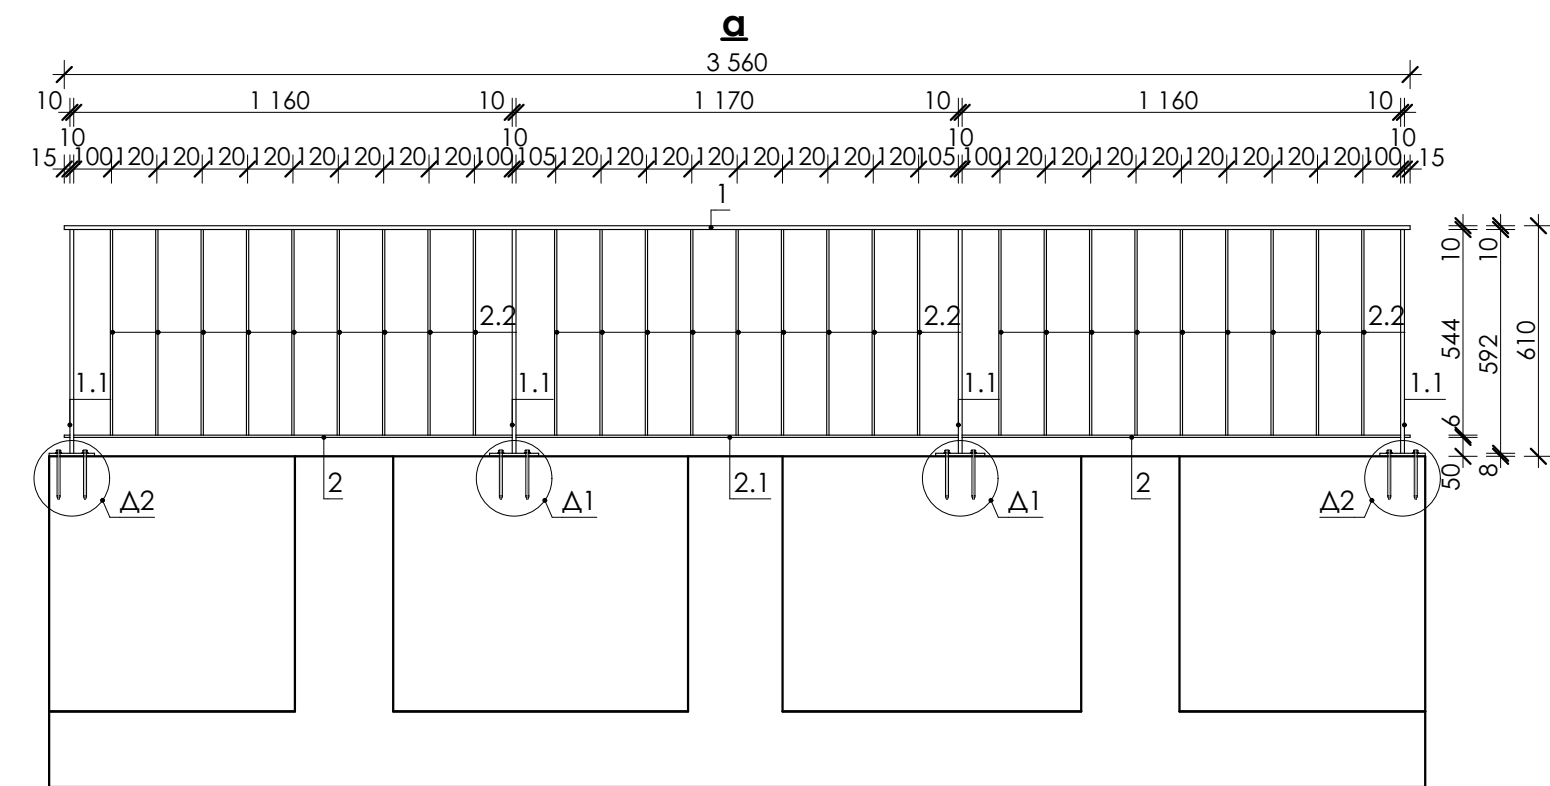
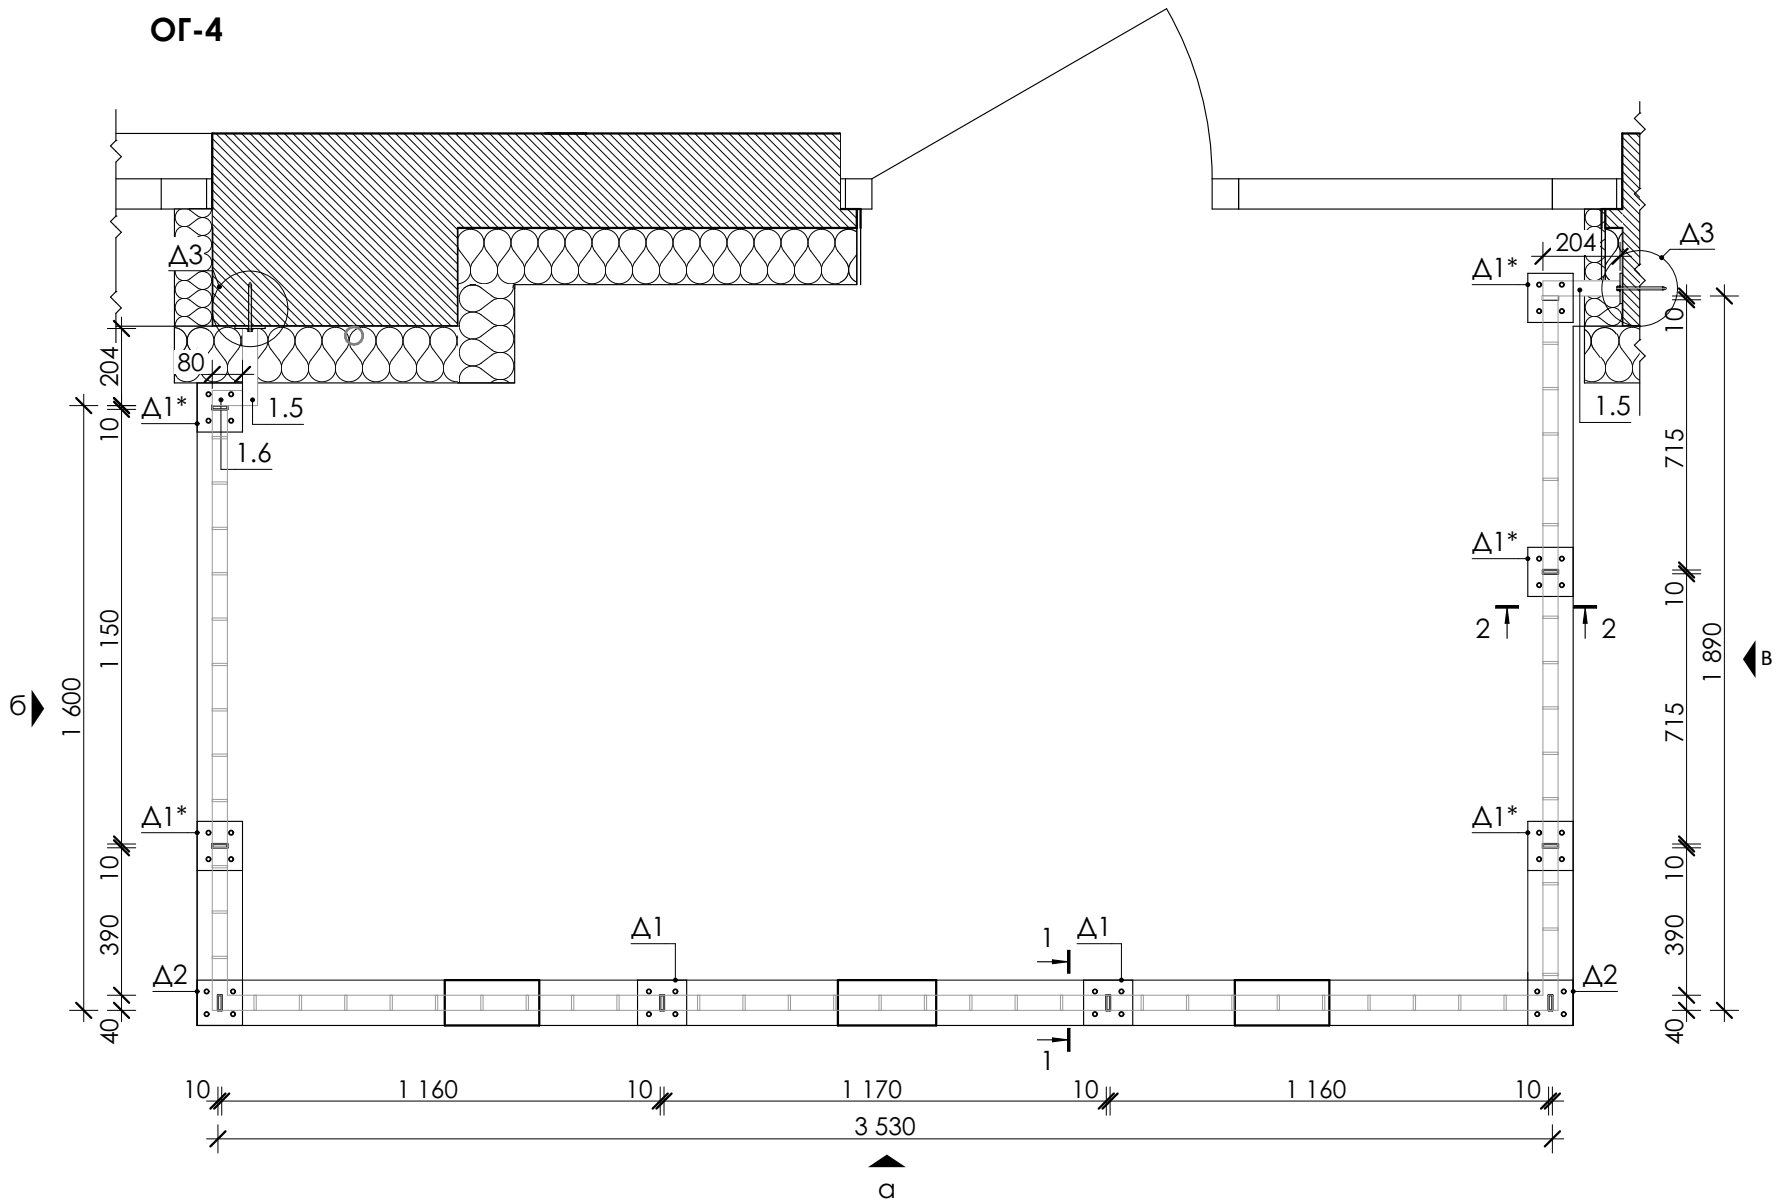


Марка поз.	Позначення	Найменування	L,м	К-сть,шт	Маса 1 м.п.,кг	Маса од., кг	Загальн а L,м	Загальні витрати кг на 1шт.
ОГ-4								
1	ΔСТУ 4747-2007	□ 40x10	3,56	1	3,14	11,18	3,56	11,18
1.1	ΔСТУ 4747-2007	□ 40x10	0,592	4	3,14	1,86	2,37	7,44
1.2	ΔСТУ 4747-2007	□ 40x10	1,272	5	3,14	3,99	6,36	19,97
1.3	ΔСТУ 4747-2007	□ 40x10	1,89	1	3,14	5,93	1,89	5,93
1.4	ΔСТУ 4747-2007	□ 40x10	1,6	1	3,14	5,02	1,60	5,02
1.5	ΔСТУ 4747-2007	□ 40x10	0,204	2	3,14	0,64	0,41	1,28
1.6	ΔСТУ 4747-2007	□ 40x10	0,08	1	3,14	0,25	0,08	0,25
							16,27	51,08
2	ΔСТУ 4747-2007	□ 40x6	1,16	2	1,884	2,19	2,32	4,37
2.1	ΔСТУ 4747-2007	□ 40x6	1,17	1	1,884	2,20	1,17	2,20
2.2	ΔСТУ 4747-2007	□ 40x6	0,544	33	1,884	1,02	17,95	33,82
2.3	ΔСТУ 4747-2007	□ 40x6	1,164	19	1,884	2,19	22,12	41,67
2.4	ΔСТУ 4747-2007	□ 40x6	0,715	2	1,884	1,35	1,43	2,69
2.5	ΔСТУ 4747-2007	□ 40x6	0,39	2	1,884	0,73	0,78	1,47
2.6	ΔСТУ 4747-2007	□ 40x6	1,15	1	1,884	2,17	1,15	2,17
							46,92	88,39
Δ1/Δ1*	ΔСТУ 4747-2007	— 120x8	0,13	7	7,536	0,98	0,91	6,86
Δ2	ΔСТУ 4747-2007	— 120x8	0,12	2	7,536	0,90432	0,24	1,81
Δ3	ΔСТУ 4747-2007	— 80x6	0,2	2	3,768	0,7536	0,40	1,51
							1,55	10,17
Клеєвий анкер HIT-HY 170 500/2-EE + Анкерна шпилька HAS-U 5.8 HDG M10x130				20				
Анкер-шуруп HUS4-HF 10x150 (бетон)				20				
Накладка на опору 40x10				9				
ОГ-4							7 шт.	

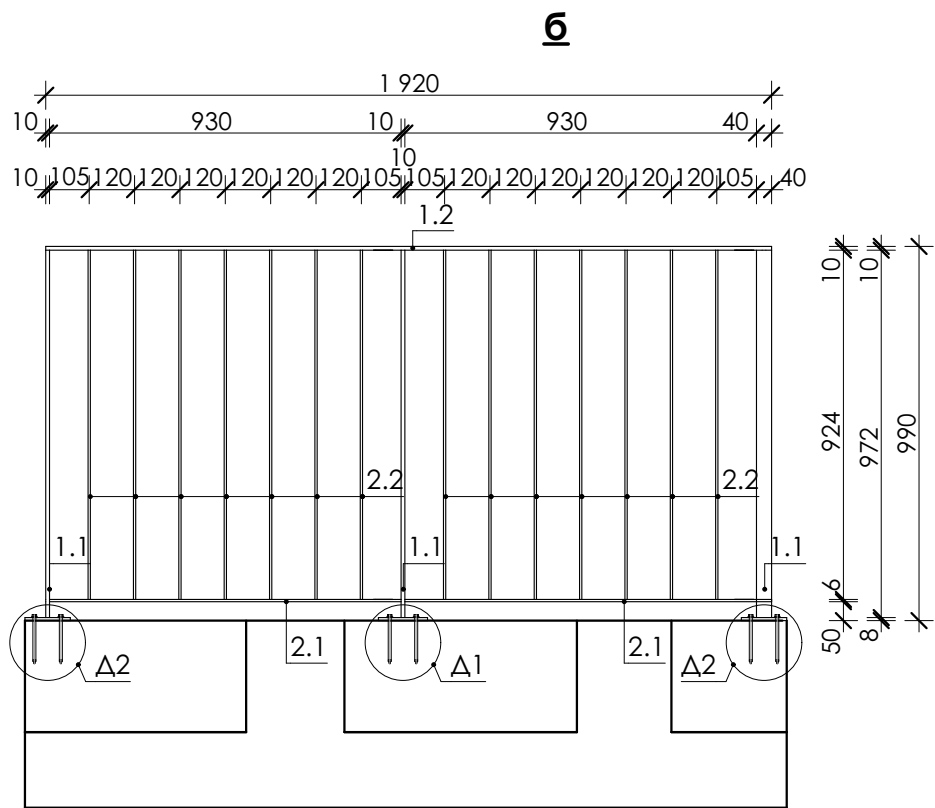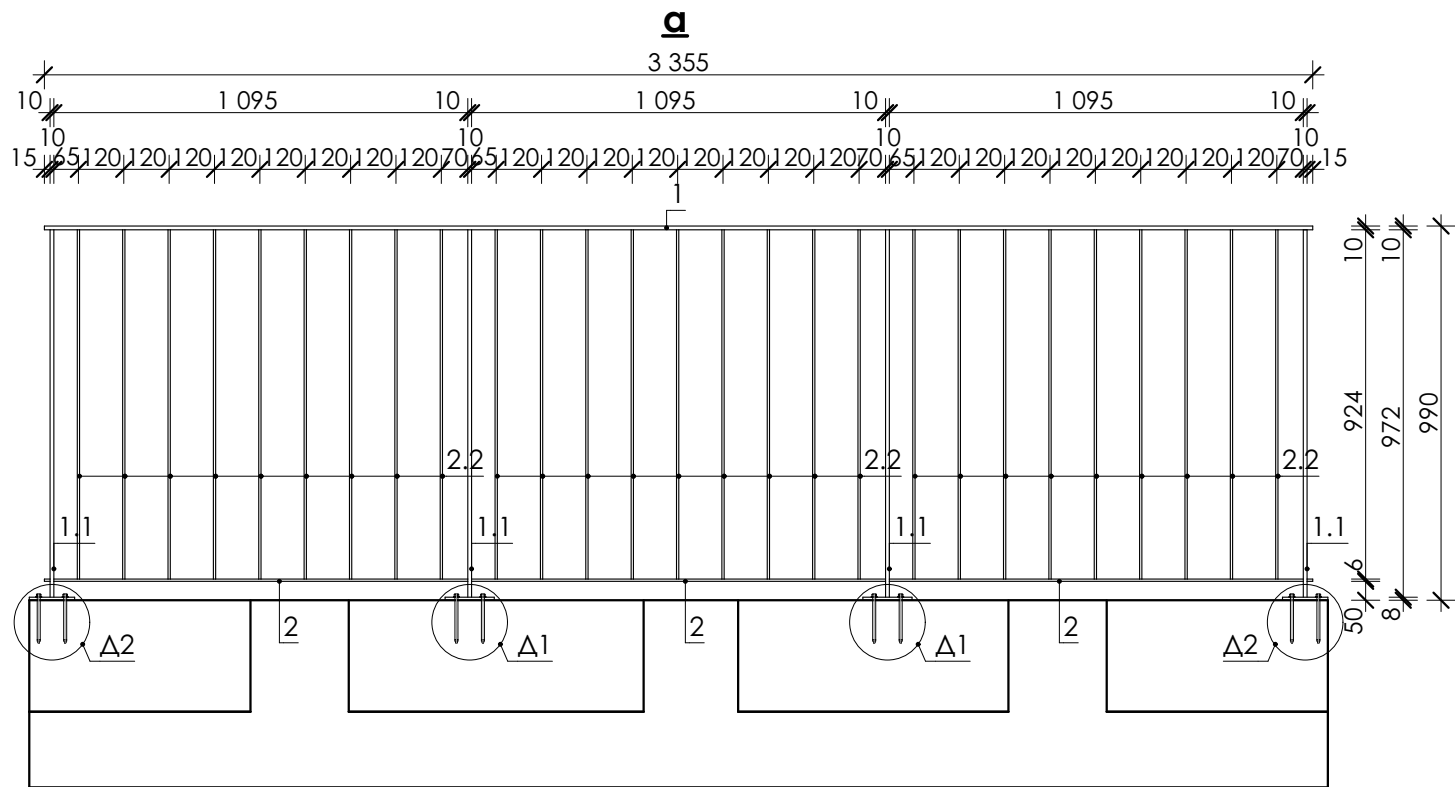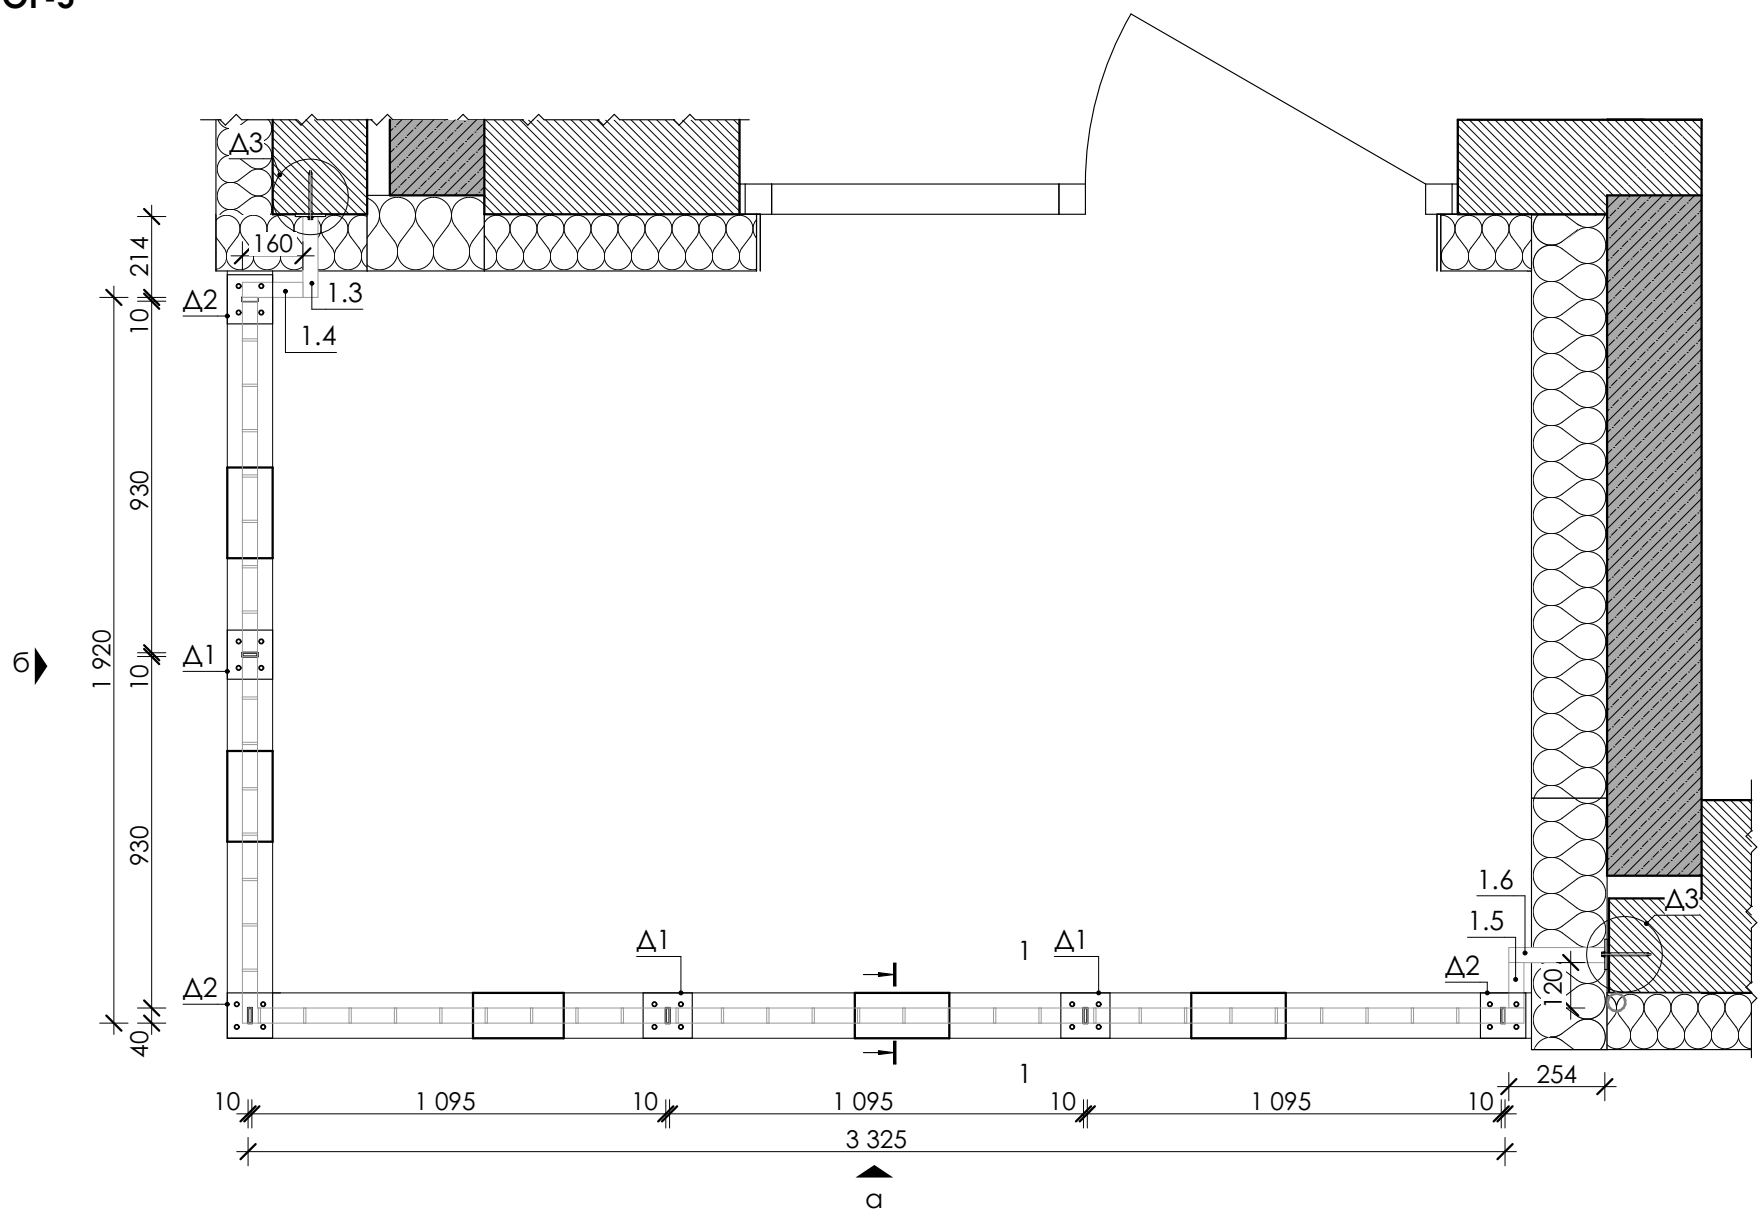

Марка поз.	Позначення	Найменування	L,м	К-сть,шт	Маса 1 м.п.,кг	Маса од., кг	Загальн а L,м	Загальні витрати кг на 1шт.
ОГ-5								
1	ΔСТУ 4747-2007	□ 40x10	3,355	1	3,14	10,53	3,36	10,53
1.1	ΔСТУ 4747-2007	□ 40x10	0,972	6	3,14	3,05	5,83	18,31
1.2	ΔСТУ 4747-2007	□ 40x10	1,92	1	3,14	6,03	1,92	6,03
1.3	ΔСТУ 4747-2007	□ 40x10	0,214	1	3,14	0,67	0,21	0,67
1.4	ΔСТУ 4747-2007	□ 40x10	0,16	1	3,14	0,50	0,16	0,50
1.5	ΔСТУ 4747-2007	□ 40x10	0,12	1	3,14	0,38	0,12	0,38
1.6	ΔСТУ 4747-2007	□ 40x10	0,254	1	3,14	0,80	0,25	0,80
							11,86	37,22
2	ΔСТУ 4747-2007	□ 40x6	1,095	3	1,884	2,06	3,29	6,19
2.1	ΔСТУ 4747-2007	□ 40x6	0,93	2	1,884	1,75	1,86	3,50
2.2	ΔСТУ 4747-2007	□ 40x6	0,924	41	1,884	1,74	37,88	71,37
							43,03	81,07
Δ1	ΔСТУ 4747-2007	— 120x8	0,13	3	7,536	0,98	0,39	2,94
Δ2	ΔСТУ 4747-2007	— 120x8	0,12	3	7,536	0,90432	0,36	2,71
Δ3	ΔСТУ 4747-2007	— 80x6	0,2	2	3,768	0,7536	0,40	1,51
							1,15	7,16
Клеєвий анкер HIT-HY 170 500/2-EE +				28				
Анкерна шпилька HAS-U 5.8 HDG M10x130				28				
Накладка на опору 40x10				6				
						ОГ-5	7 шт.	


1-1

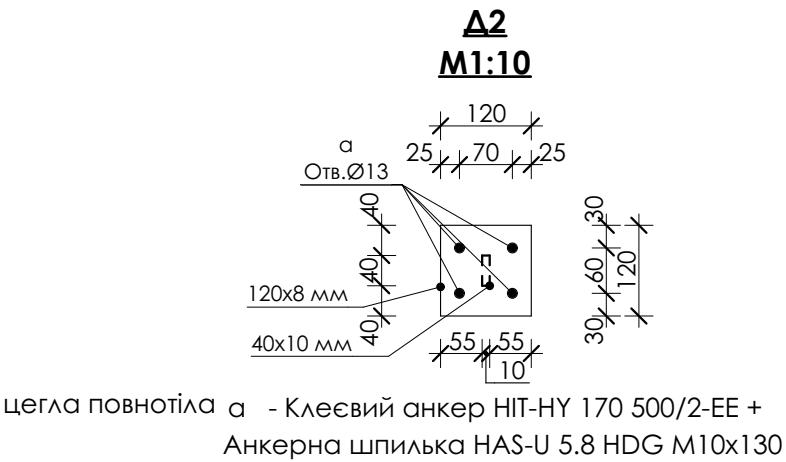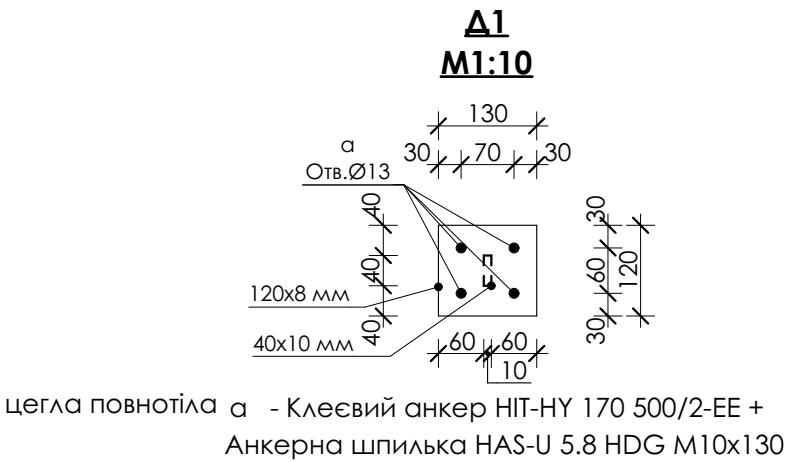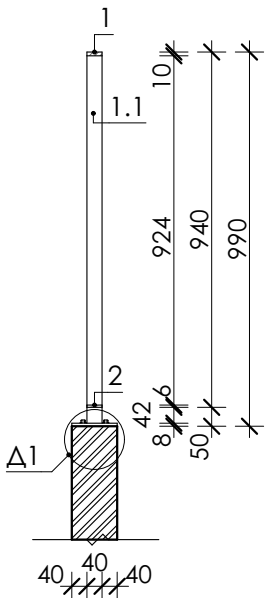









цегла повнотіла а - Клеєвий анкер HIT-HY 170 500/2-EE + Анкерна шпилька HAS-U 5.8 HDG M10x130

цегла повнотіла а - Клеєвий анкер HIT-HY 170 500/2-EE + Анкерна шпилька HAS-U 5.8 HDG M10x130







Δ3 M1:10

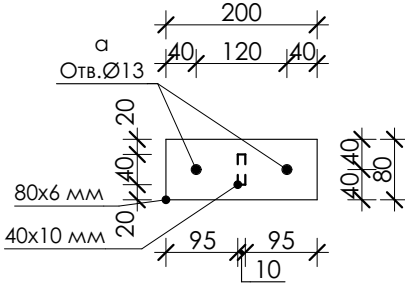





цегла повнотіла а - Клеєвий анкер HIT-HY 170 500/2-EE + Анкерна шпилька HAS-U 5.8 HDG M10x130

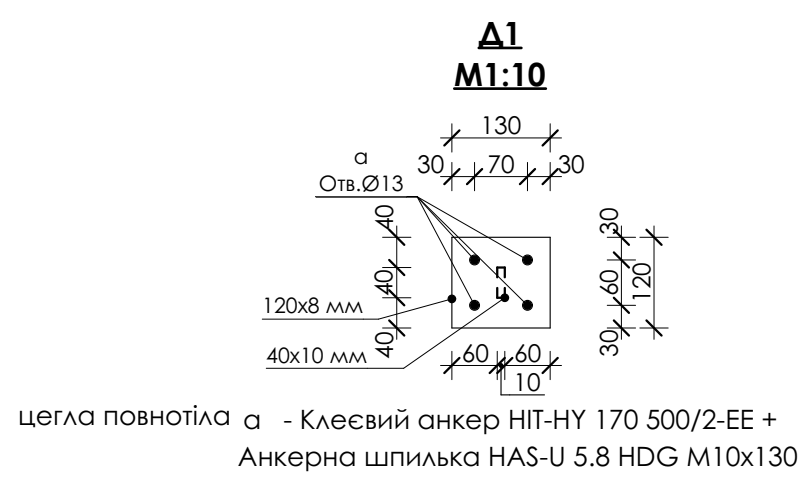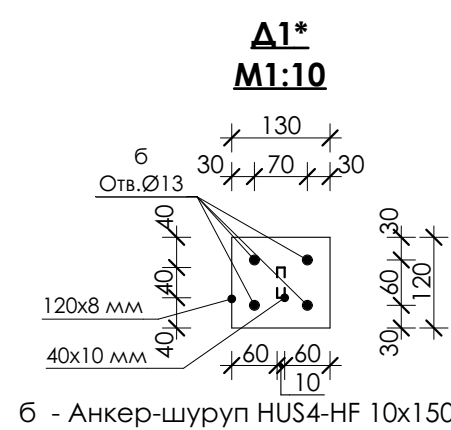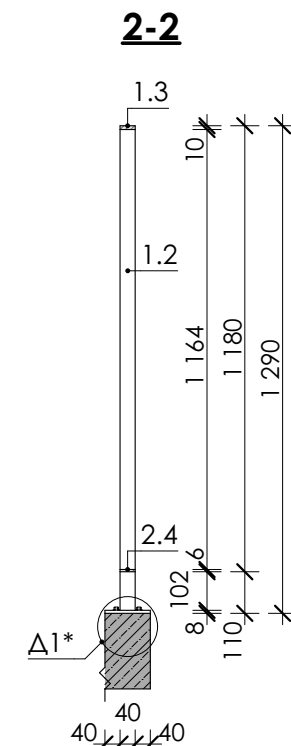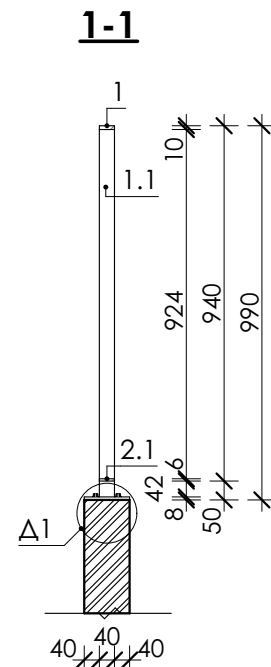
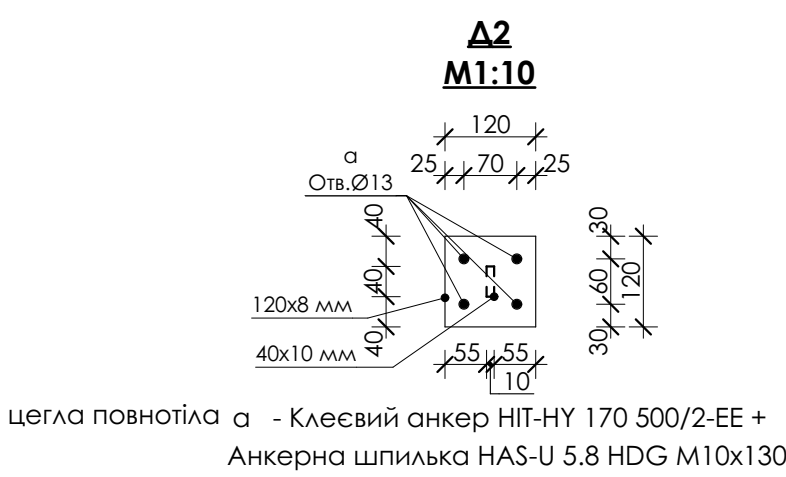
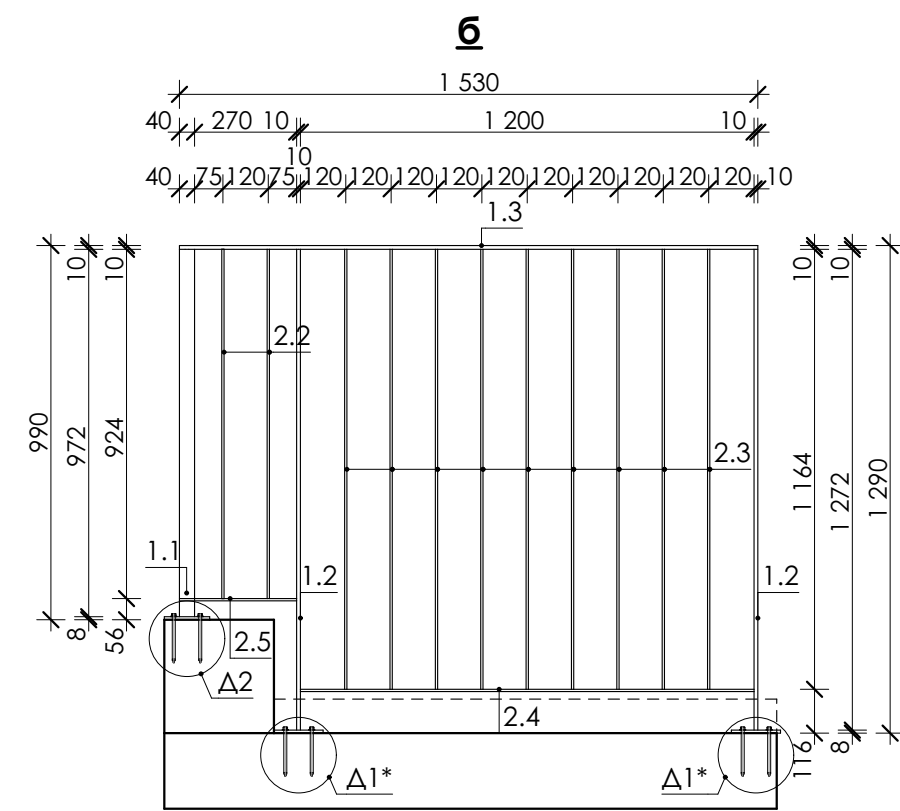
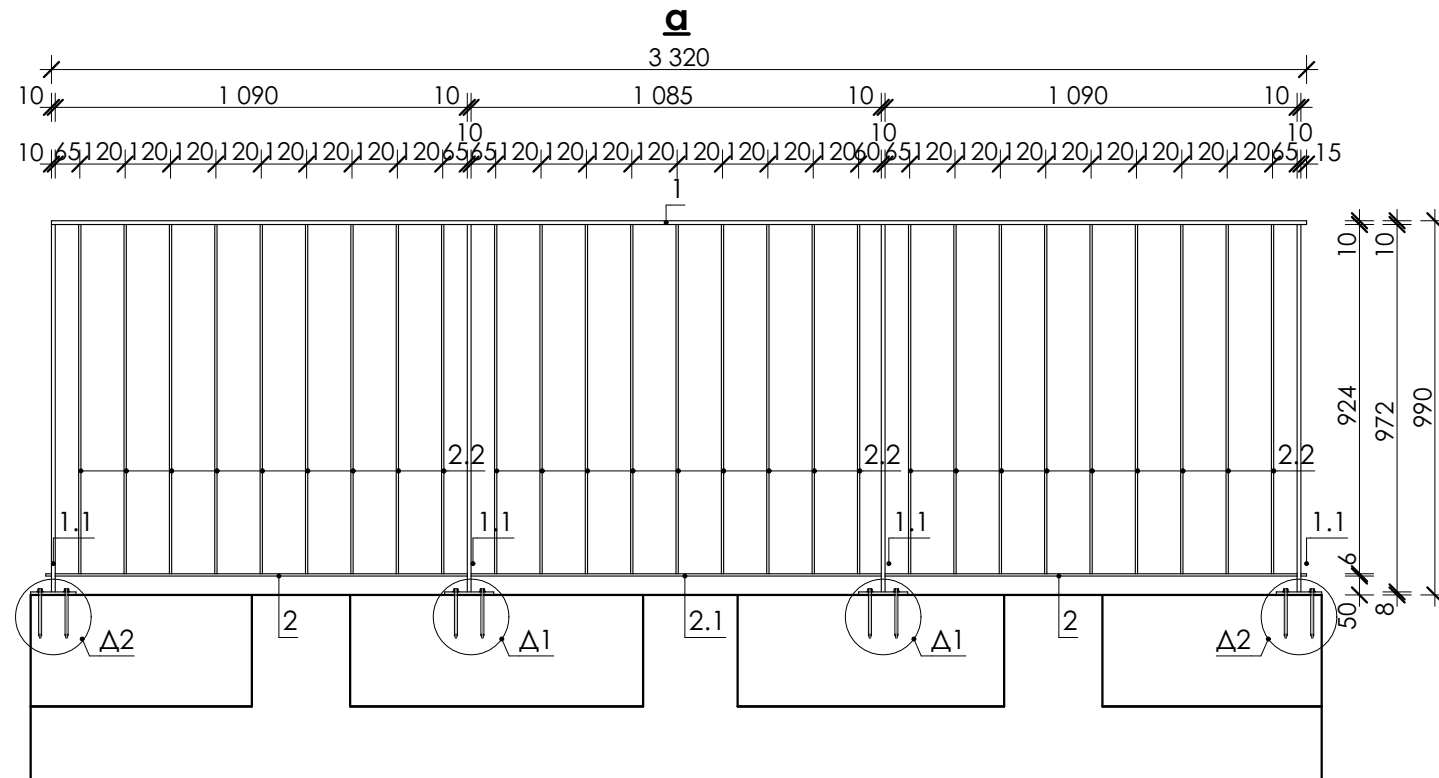
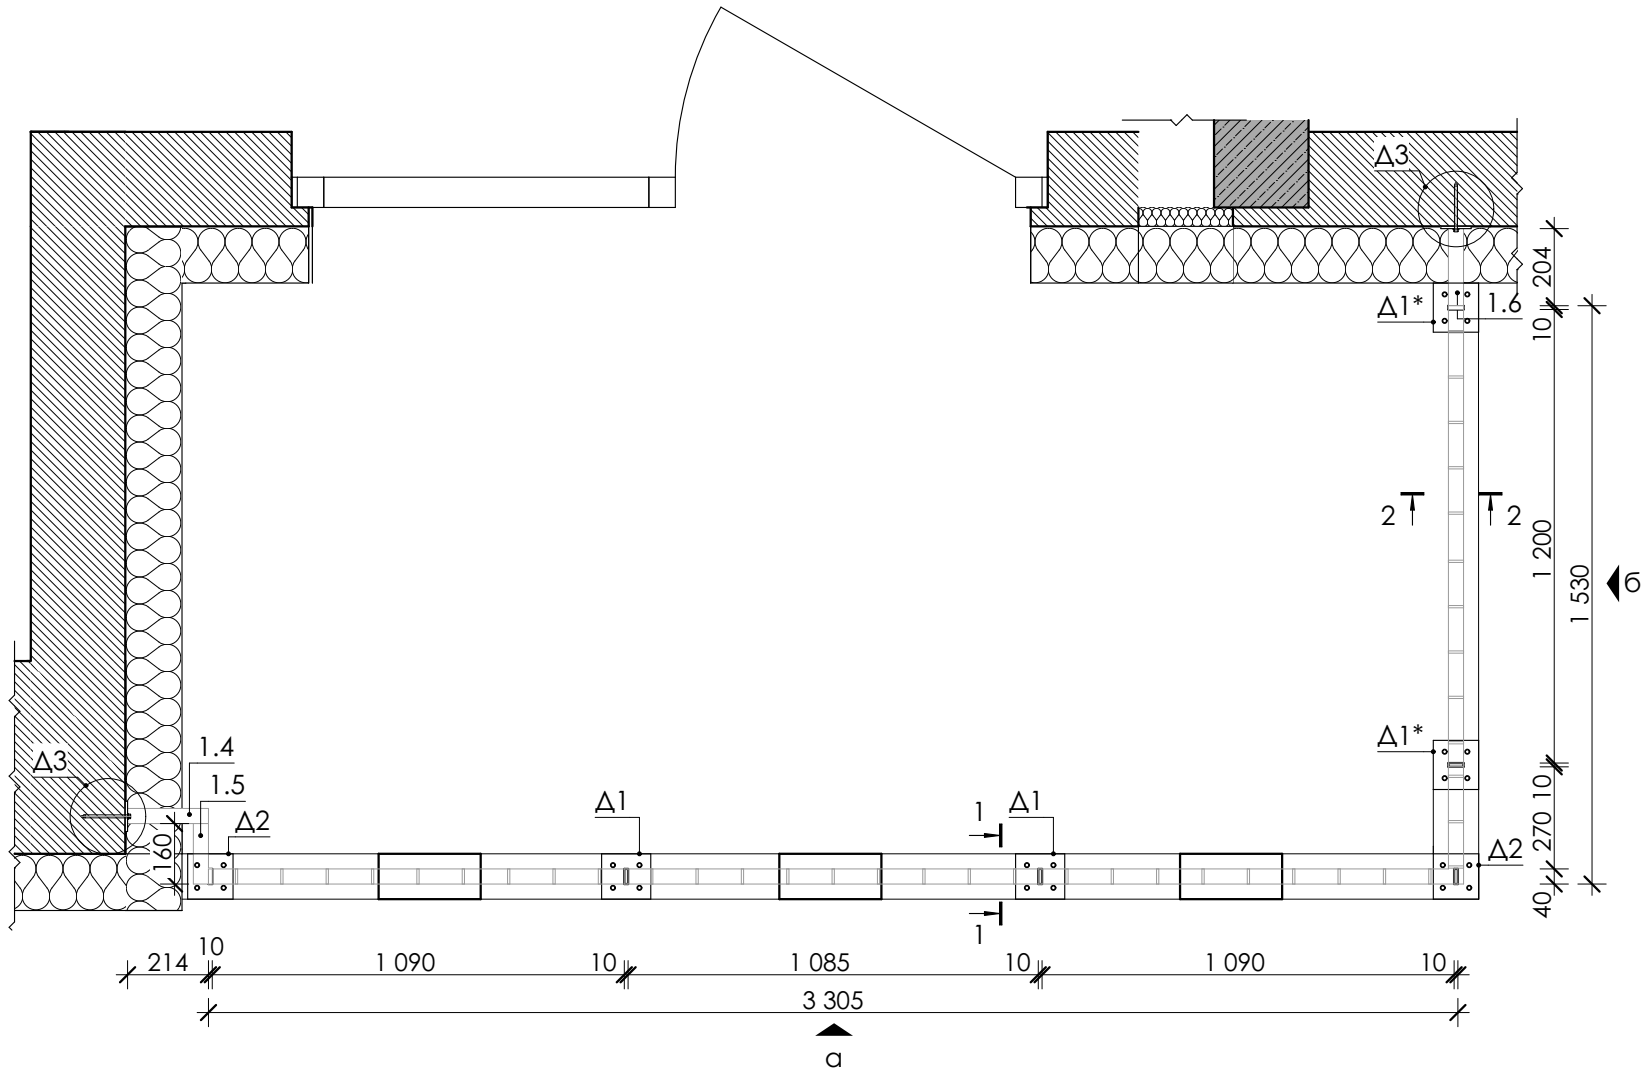


Марка поз.	Позначення	Найменування	L,м	К-сть,шт	Маса 1 м.п.,кг	Маса од., кг	Загальна L,м	Загальні витрати кг на 1шт.
ОГ-6								
1	ΔСТУ 4747-2007	□ 40x10	3,32	1	3,14	10,42	3,32	10,42
1.1	ΔСТУ 4747-2007	□ 40x10	0,972	4	3,14	3,05	3,89	12,21
1.2	ΔСТУ 4747-2007	□ 40x10	1,272	2	3,14	3,99	2,54	7,99
1.3	ΔСТУ 4747-2007	□ 40x10	1,53	1	3,14	4,80	1,53	4,80
1.4	ΔСТУ 4747-2007	□ 40x10	0,214	1	3,14	0,67	0,21	0,67
1.5	ΔСТУ 4747-2007	□ 40x10	0,16	1	3,14	0,50	0,16	0,50
1.6	ΔСТУ 4747-2007	□ 40x10	0,204	1	3,14	0,64	0,20	0,64
							11,66	36,60
2	ΔСТУ 4747-2007	□ 40x6	1,09	2	1,884	2,05	2,18	4,11
2.1	ΔСТУ 4747-2007	□ 40x6	1,085	1	1,884	2,04	1,09	2,04
2.2	ΔСТУ 4747-2007	□ 40x6	0,924	29	1,884	1,74	26,80	50,48
2.3	ΔСТУ 4747-2007	□ 40x6	1,164	9	1,884	2,19	10,48	19,74
2.4	ΔСТУ 4747-2007	□ 40x6	1,2	1	1,884	2,26	1,20	2,26
2.5	ΔСТУ 4747-2007	□ 40x6	0,27	1	1,884	0,51	0,27	0,51
							40,54	76,37
Δ1/Δ1*	ΔСТУ 4747-2007	— 120x8	0,13	4	7,536	0,98	0,52	3,92
Δ2	ΔСТУ 4747-2007	— 120x8	0,12	2	7,536	0,90432	0,24	1,81
Δ3	ΔСТУ 4747-2007	— 80x6	0,2	2	3,768	0,7536	0,40	1,51
							1,16	7,23
Клеєвий анкер HIT-HY 170 500/2-EE +				20				
Анкерна шпилька HAS-U 5.8 HDG M10x130				20				
Анкер-шуруп HUS4-HF 10x150 (бетон)				8				
Накладка на опору 40x10				6				
ОГ-6							7 шт.	

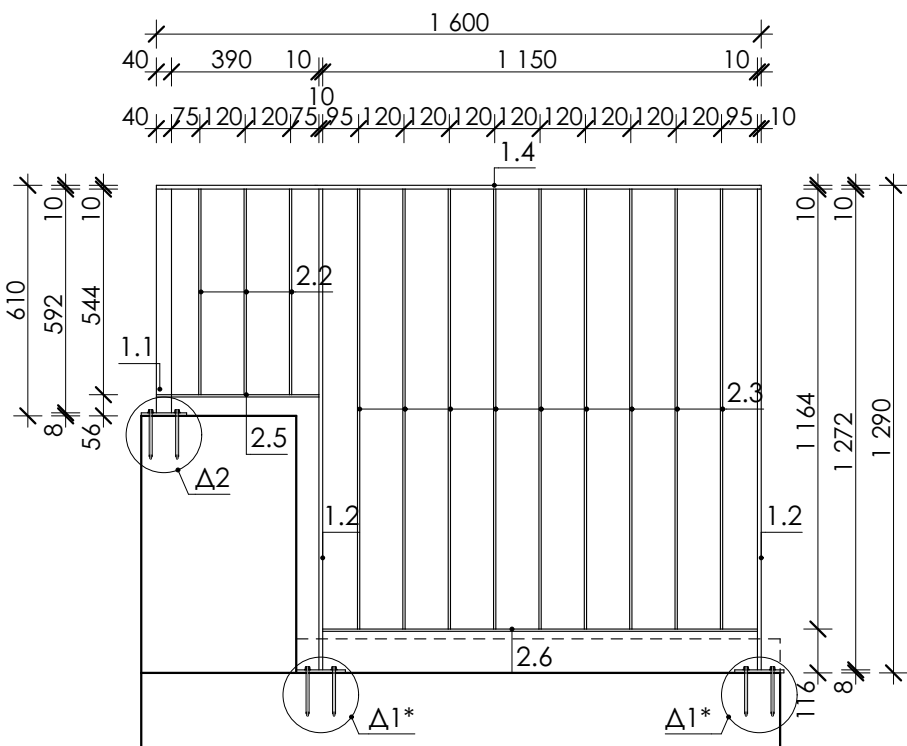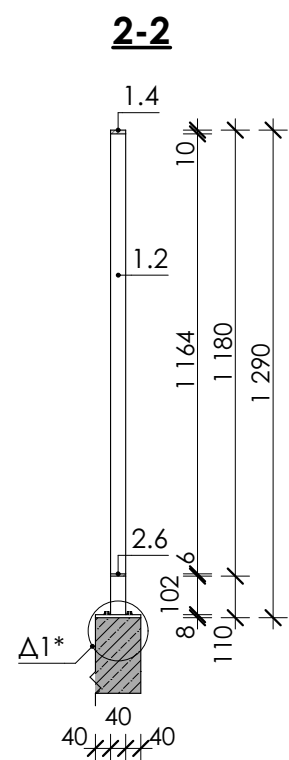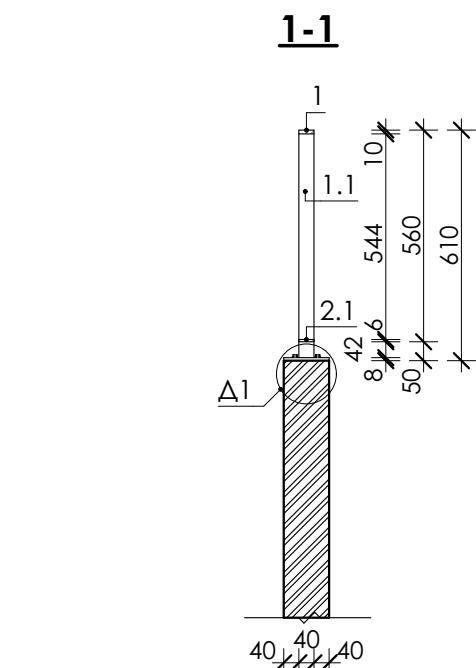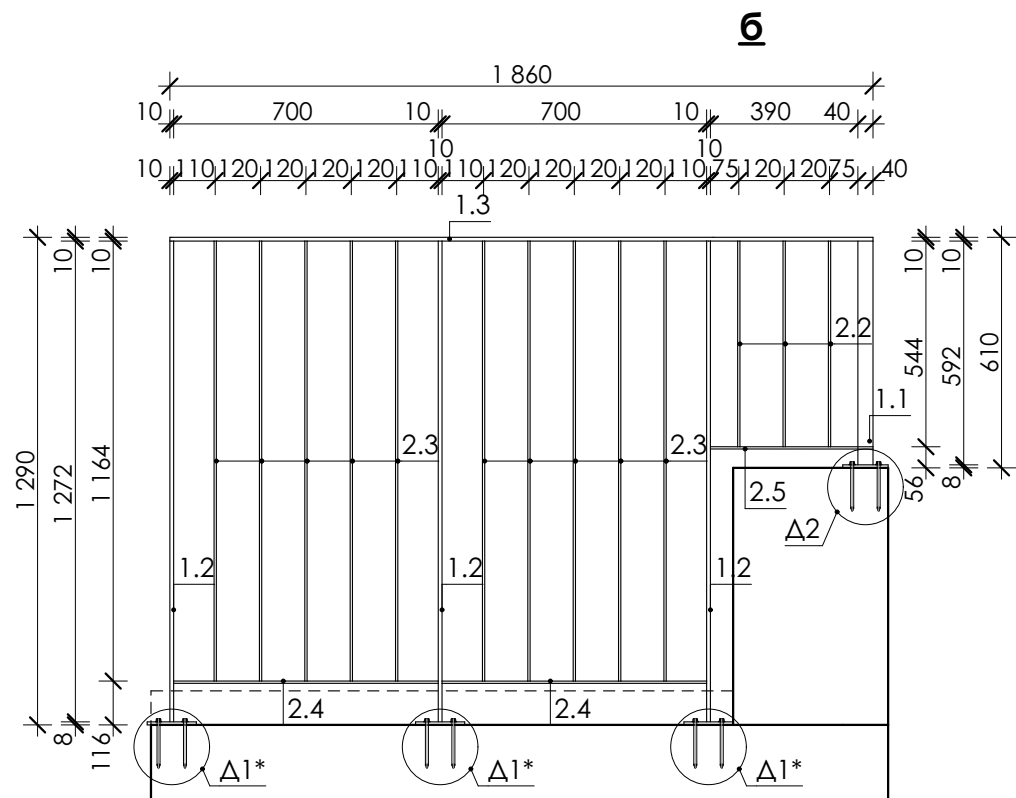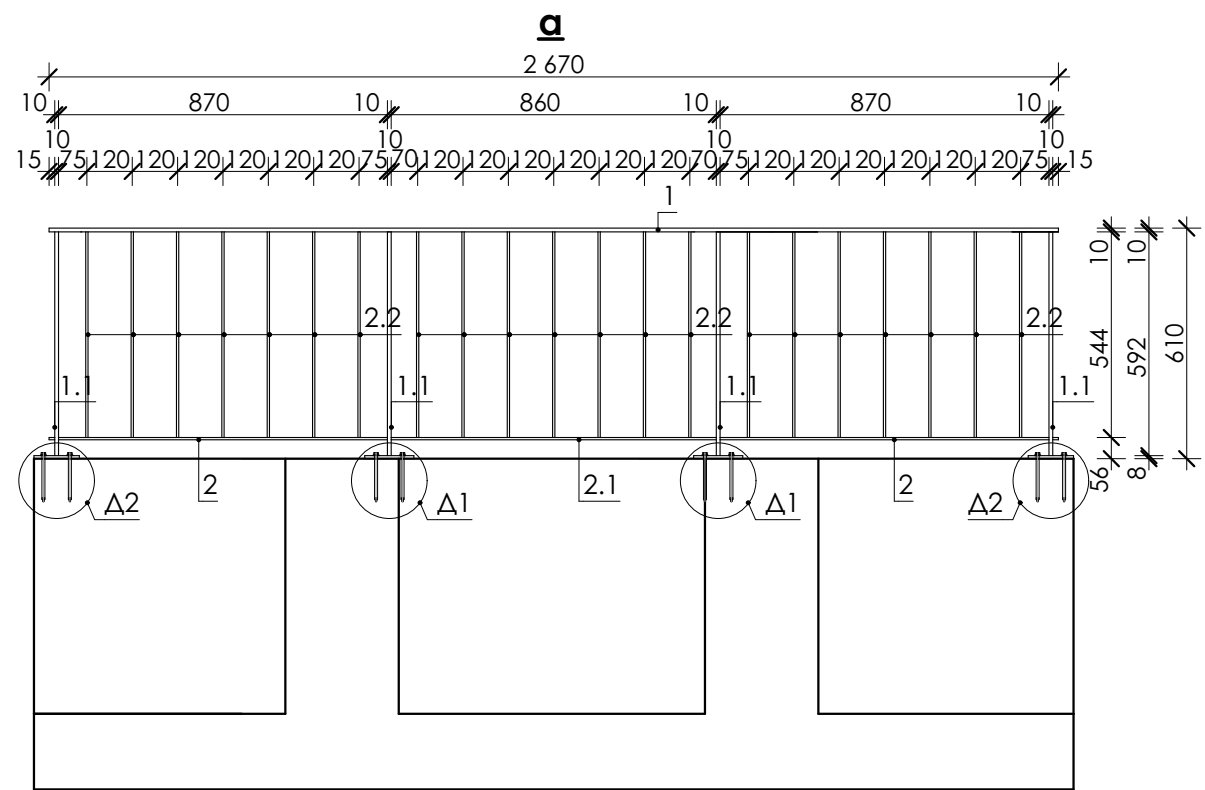
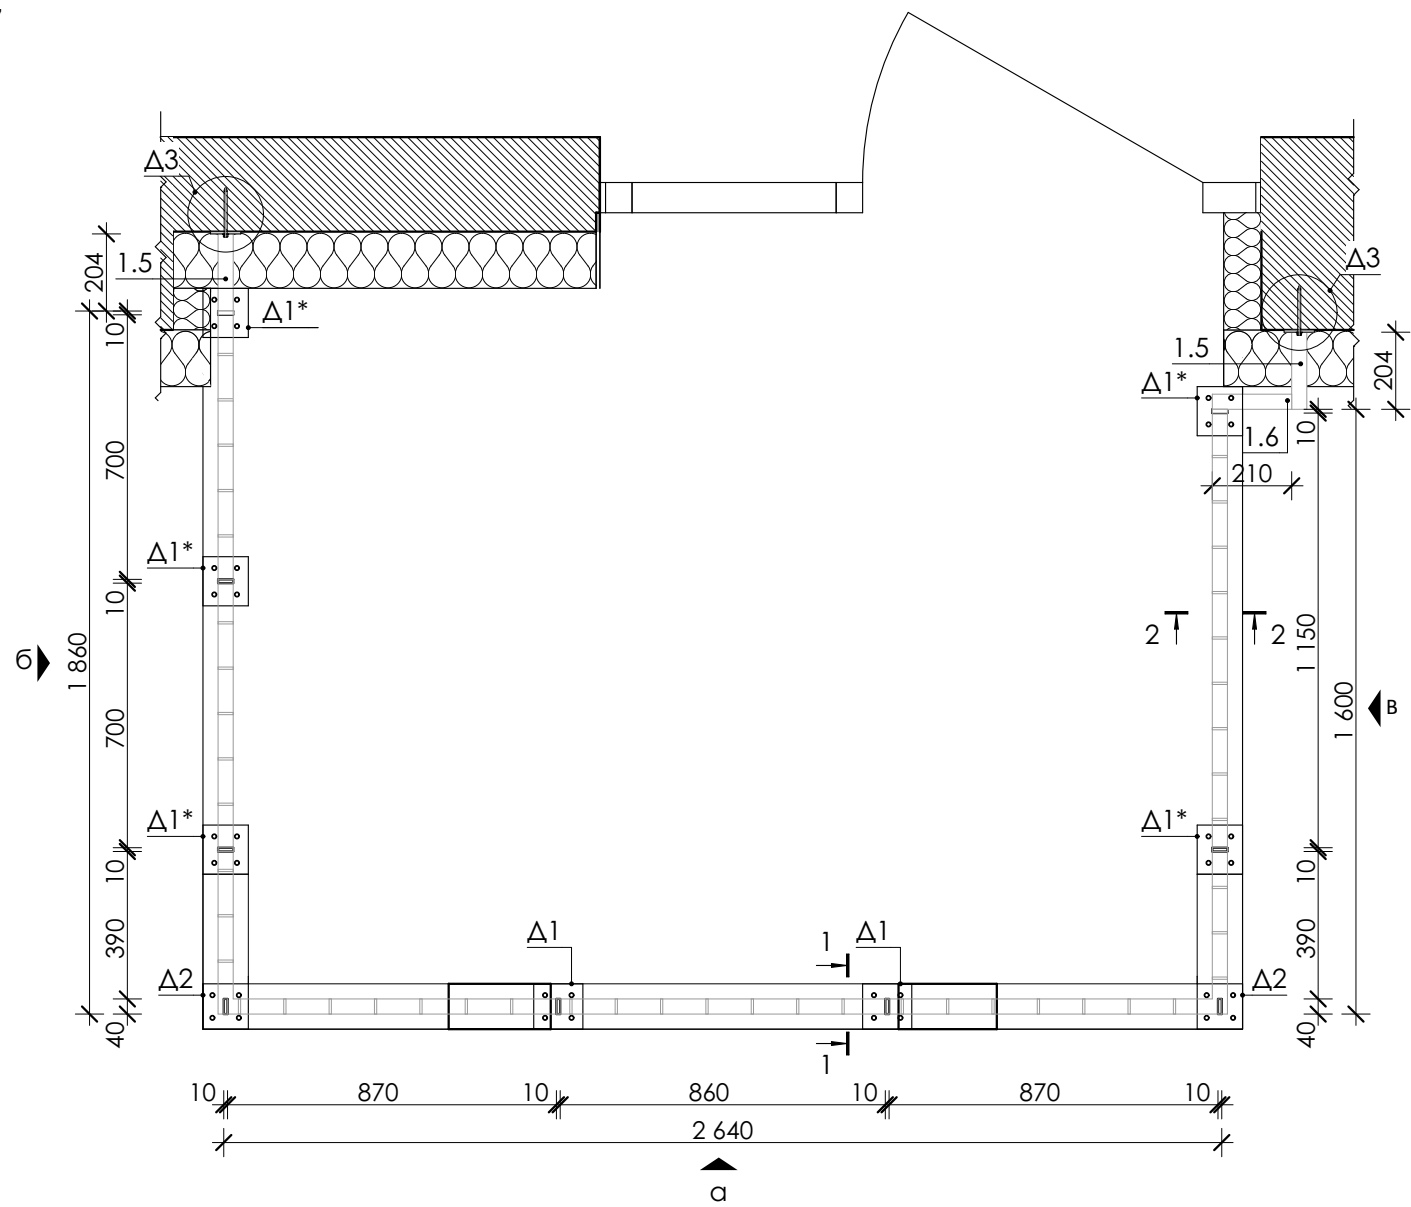












Марка поз.	Позначення	Найменування	Л,м	К-сть,шт	Маса 1 м.п.,кг	Маса од., кг	Загальн а Л,м	Загальні витрати кг на 1шт.
ОГ-7								
1	ΔСТУ 4747-2007	□ 40x10	2,67	1	3,14	8,38	2,67	8,38
1.1	ΔСТУ 4747-2007	□ 40x10	0,592	4	3,14	1,86	2,37	7,44
1.2	ΔСТУ 4747-2007	□ 40x10	1,272	5	3,14	3,99	6,36	19,97
1.3	ΔСТУ 4747-2007	□ 40x10	1,86	1	3,14	5,84	1,86	5,84
1.4	ΔСТУ 4747-2007	□ 40x10	1,6	1	3,14	5,02	1,60	5,02
1.5	ΔСТУ 4747-2007	□ 40x10	0,204	2	3,14	0,64	0,41	1,28
1.6	ΔСТУ 4747-2007	□ 40x10	0,21	1	3,14	0,66	0,21	0,66
							15,48	48,59
2	ΔСТУ 4747-2007	□ 40x6	0,87	2	1,884	1,64	1,74	3,28
2.1	ΔСТУ 4747-2007	□ 40x6	0,86	1	1,884	1,62	0,86	1,62
2.2	ΔСТУ 4747-2007	□ 40x6	0,544	27	1,884	1,02	14,69	27,67
2.3	ΔСТУ 4747-2007	□ 40x6	1,164	19	1,884	2,19	22,12	41,67
2.4	ΔСТУ 4747-2007	□ 40x6	0,7	2	1,884	1,32	1,40	2,64
2.5	ΔСТУ 4747-2007	□ 40x6	0,39	2	1,884	0,73	0,78	1,47
2.6	ΔСТУ 4747-2007	□ 40x6	1,15	1	1,884	2,17	1,15	2,17
							42,73	80,51
Δ1/Δ1*	ΔСТУ 4747-2007	— 120x8	0,13	7	7,536	0,98	0,91	6,86
Δ2	ΔСТУ 4747-2007	— 120x8	0,12	2	7,536	0,90432	0,24	1,81
Δ3	ΔСТУ 4747-2007	— 80x6	0,2	2	3,768	0,7536	0,40	1,51
							1,55	10,17
Клеєвий анкер HIT-HY 170 500/2-EE + Анкерна шпилька HAS-U 5.8 HDG M10x130				20				
Анкер-шуруп HUS4-HF 10x150 (бетон)				20				
Накладка на опору 40x10				9				
ОГ-7							7 шт.	

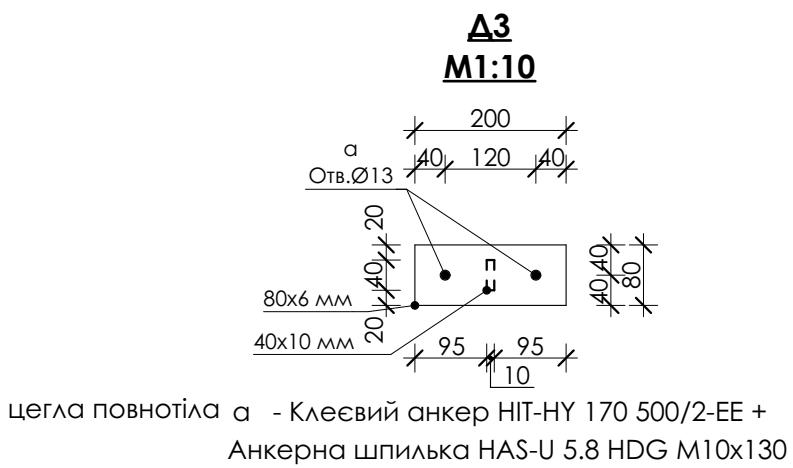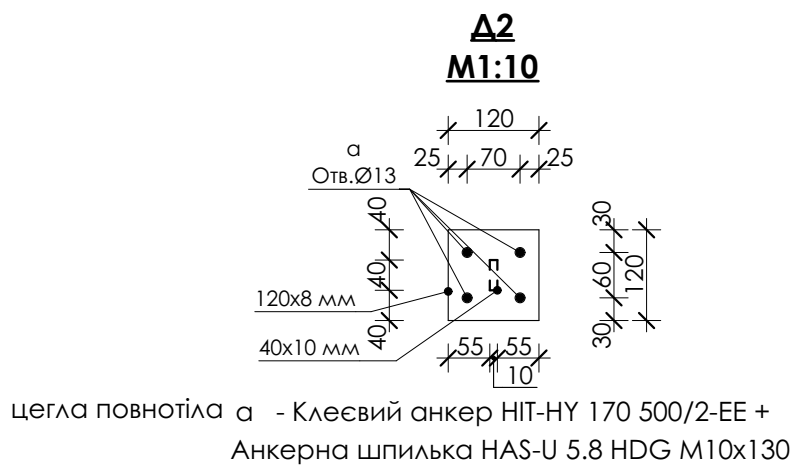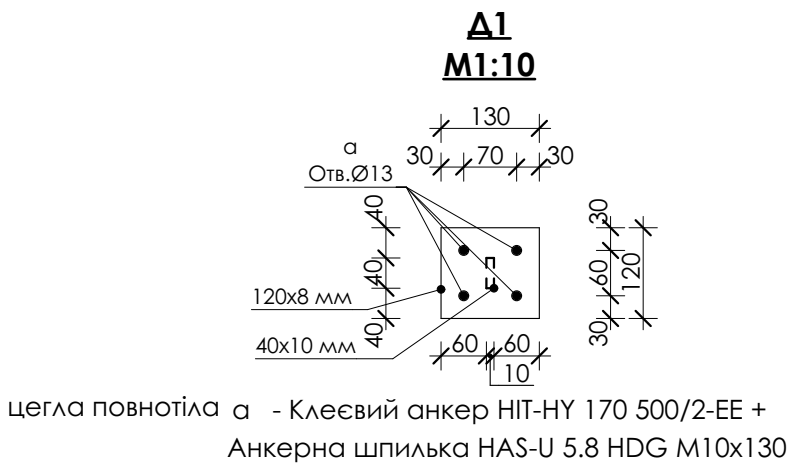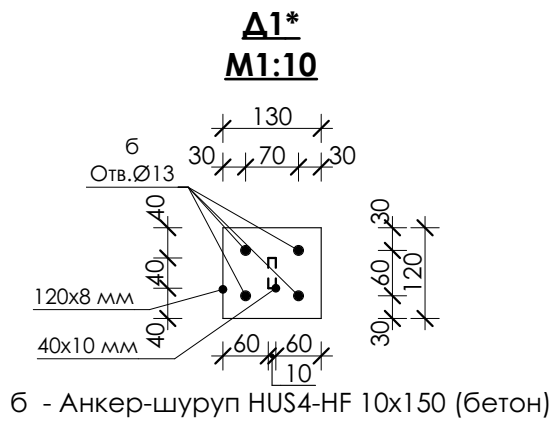

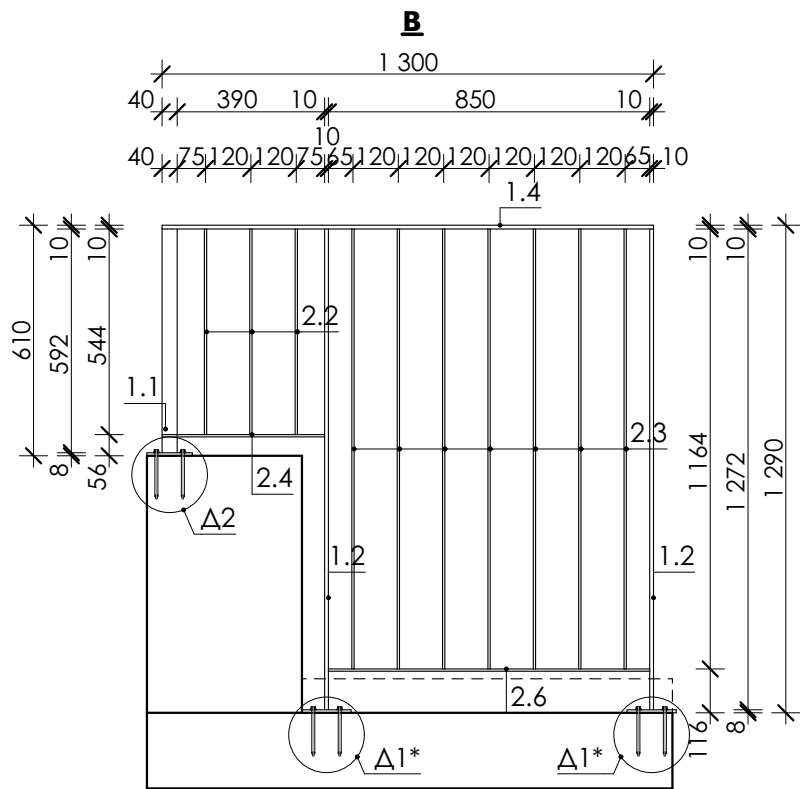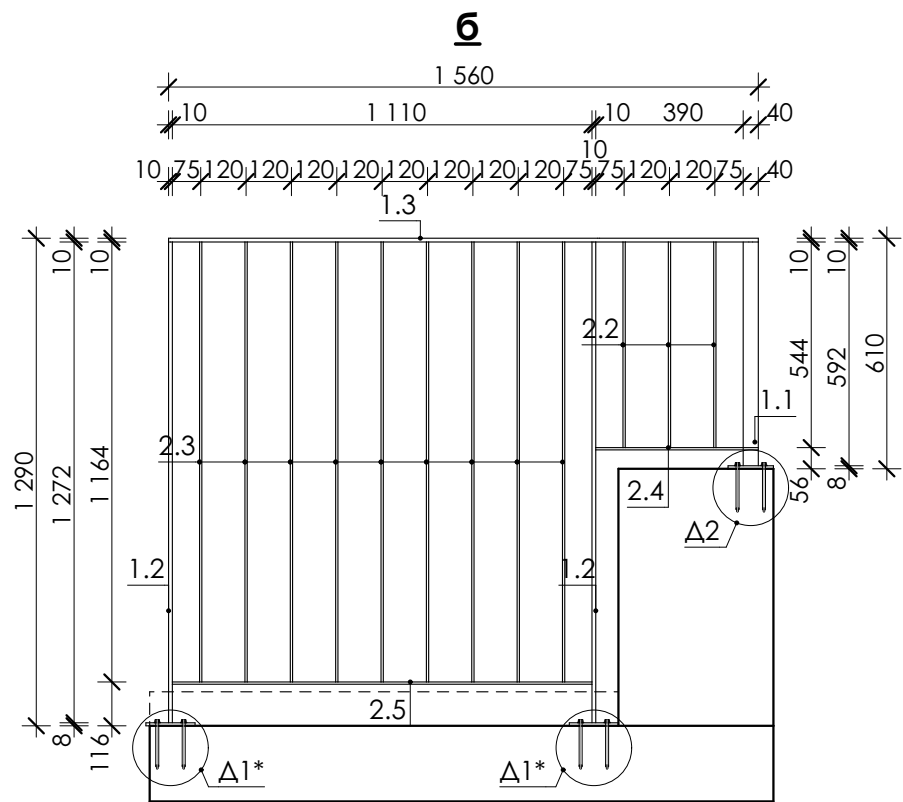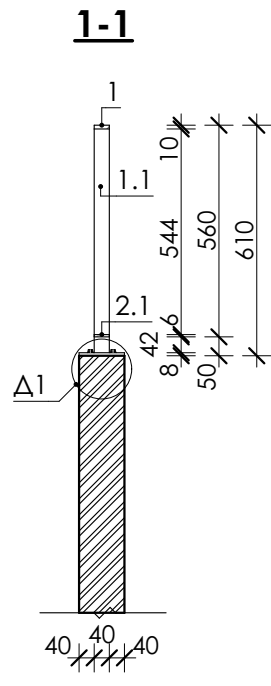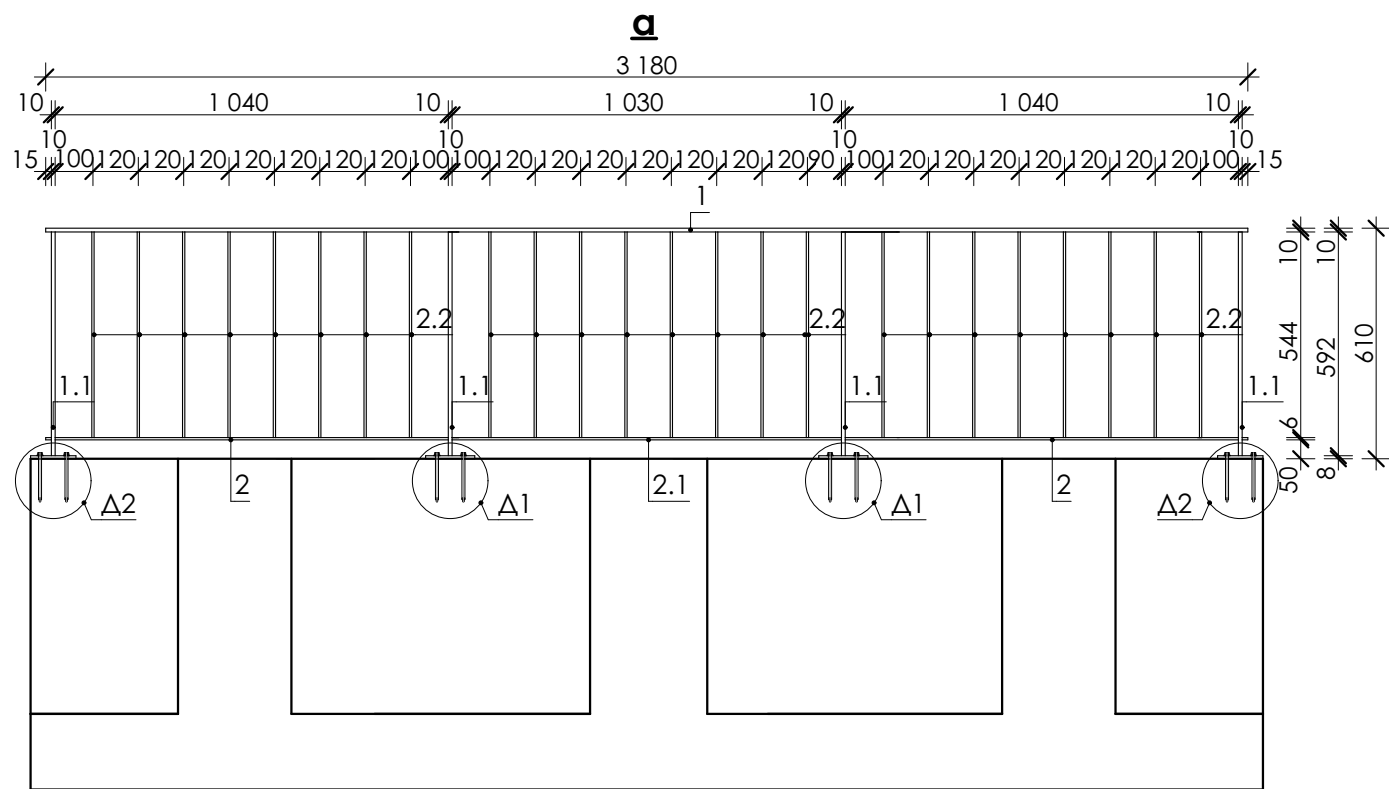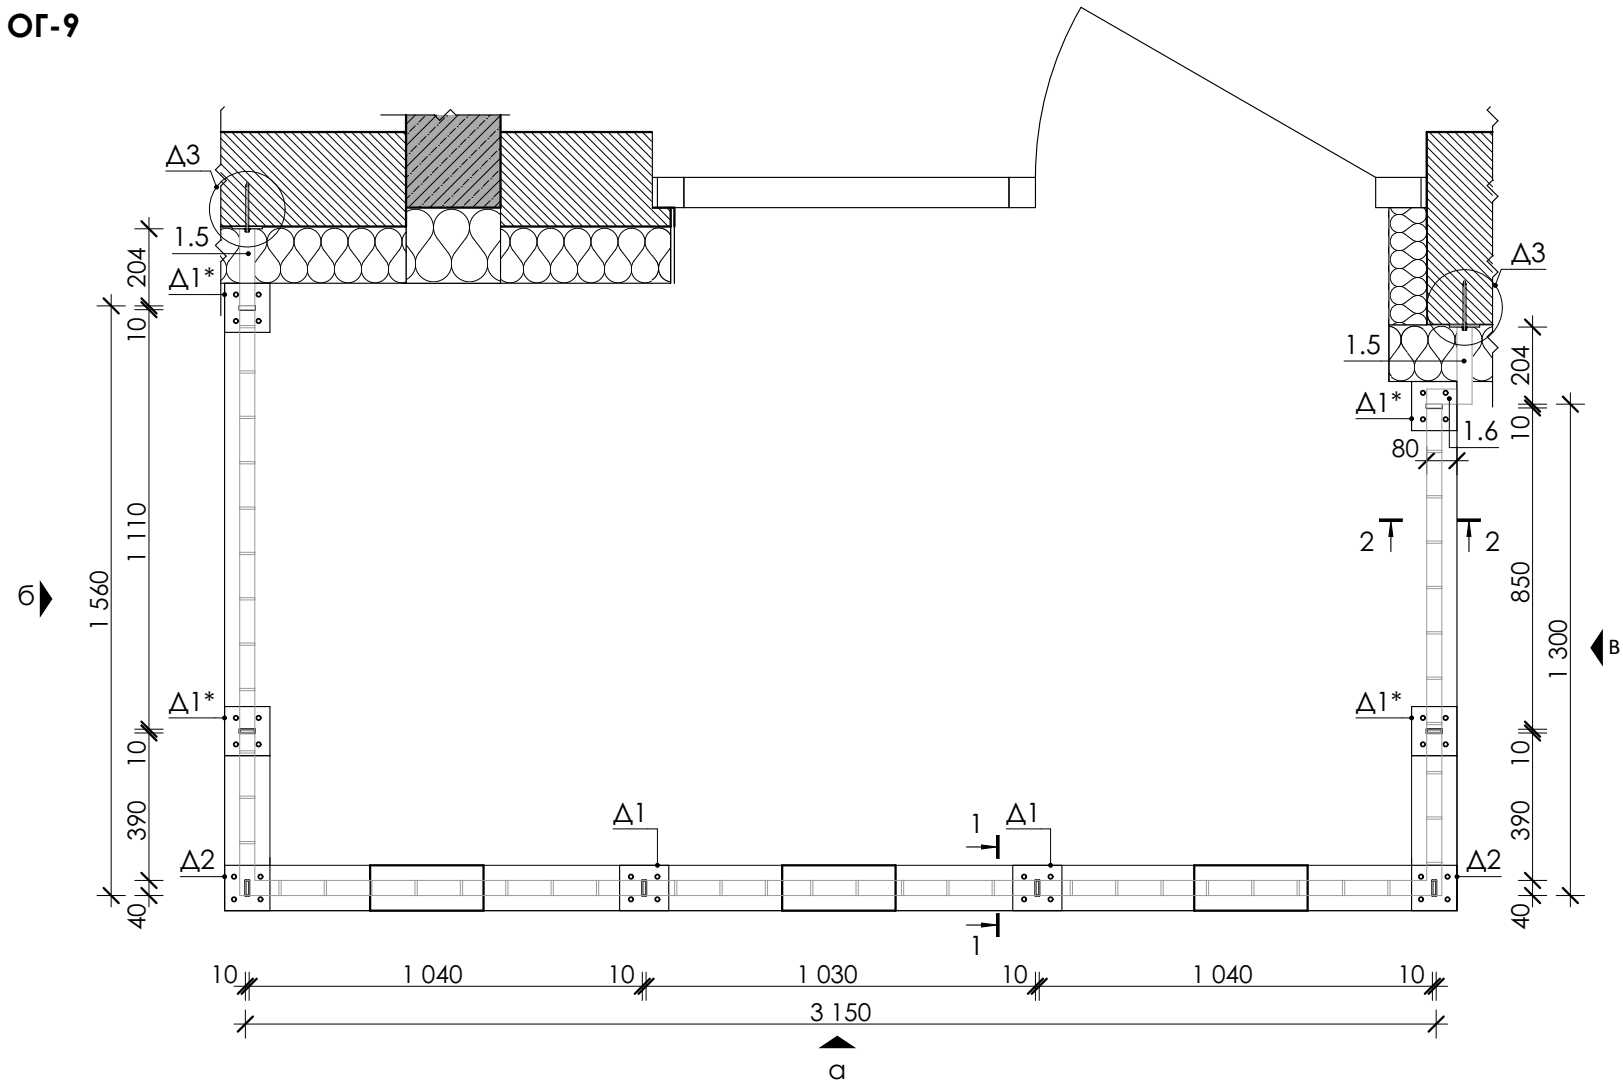


Марка поз.	Позначення	Найменування	Л,м	К-сть,шт	Маса 1 м.п.,кг	Маса од., кг	Загальн а Л,м	Загальні витрати кг на 1шт.
ОГ-9								
1	ΔСТУ 4747-2007	□ 40x10	3,18	1	3,14	9,99	3,18	9,99
1.1	ΔСТУ 4747-2007	□ 40x10	0,592	4	3,14	1,86	2,37	7,44
1.2	ΔСТУ 4747-2007	□ 40x10	1,272	4	3,14	3,99	5,09	15,98
1.3	ΔСТУ 4747-2007	□ 40x10	1,56	1	3,14	4,90	1,56	4,90
1.4	ΔСТУ 4747-2007	□ 40x10	1,3	1	3,14	4,08	1,30	4,08
1.5	ΔСТУ 4747-2007	□ 40x10	0,204	2	3,14	0,64	0,41	1,28
1.6	ΔСТУ 4747-2007	□ 40x10	0,08	1	3,14	0,25	0,08	0,25
							13,98	43,91
2	ΔСТУ 4747-2007	□ 40x6	1,04	2	1,884	1,96	2,08	3,92
2.1	ΔСТУ 4747-2007	□ 40x6	1,03	1	1,884	1,94	1,03	1,94
2.2	ΔСТУ 4747-2007	□ 40x6	0,544	30	1,884	1,02	16,32	30,75
2.3	ΔСТУ 4747-2007	□ 40x6	1,164	16	1,884	2,19	18,62	35,09
2.4	ΔСТУ 4747-2007	□ 40x6	0,39	2	1,884	0,73	0,78	1,47
2.5	ΔСТУ 4747-2007	□ 40x6	1,11	1	1,884	2,09	1,11	2,09
2.6	ΔСТУ 4747-2007	□ 40x6	0,85	1	1,884	1,60	0,85	1,60
							40,79	76,86
Δ1/Δ1*	ΔСТУ 4747-2007	— 120x8	0,13	6	7,536	0,98	0,78	5,88
Δ2	ΔСТУ 4747-2007	— 120x8	0,12	2	7,536	0,90432	0,24	1,81
Δ3	ΔСТУ 4747-2007	— 80x6	0,2	2	3,768	0,7536	0,40	1,51
							1,42	9,19
	Клеєвий анкер HIT-HY 170 500/2-EE + Анкерна шпилька HAS-U 5.8 HDG M10x130			20				
	Анкер-шуруп HUS4-HF 10x150 (бетон)			16				
	Накладка на опору 40x10			8				
						ОГ-9		
						7 шт.		

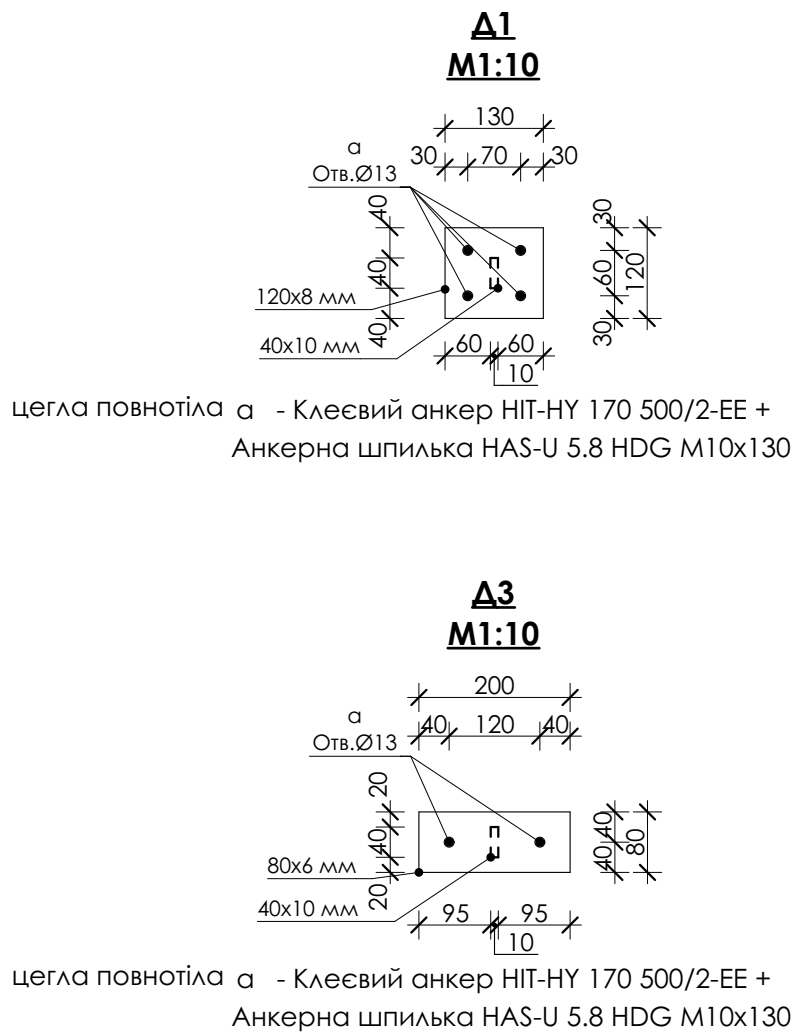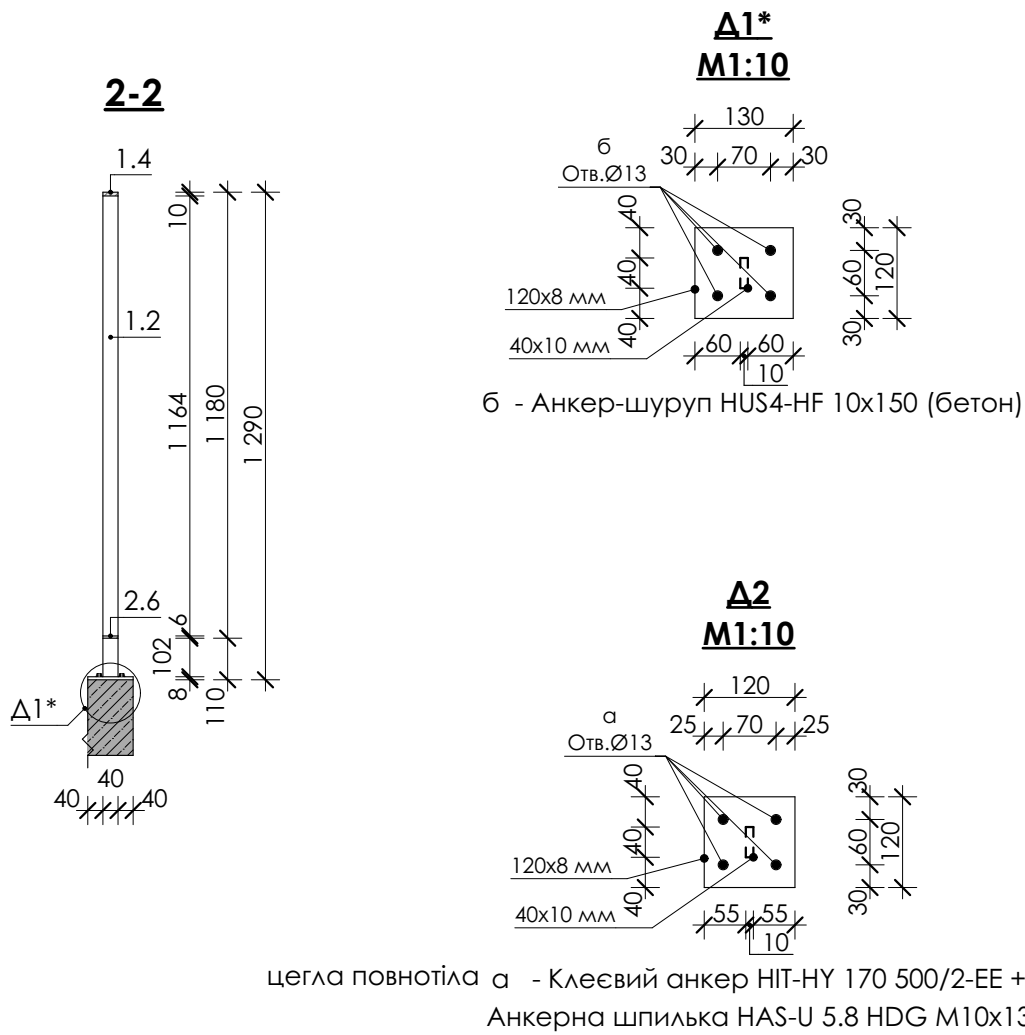


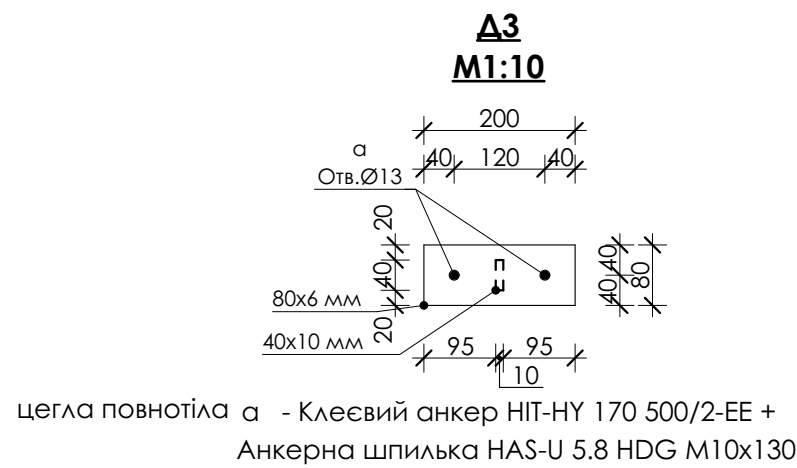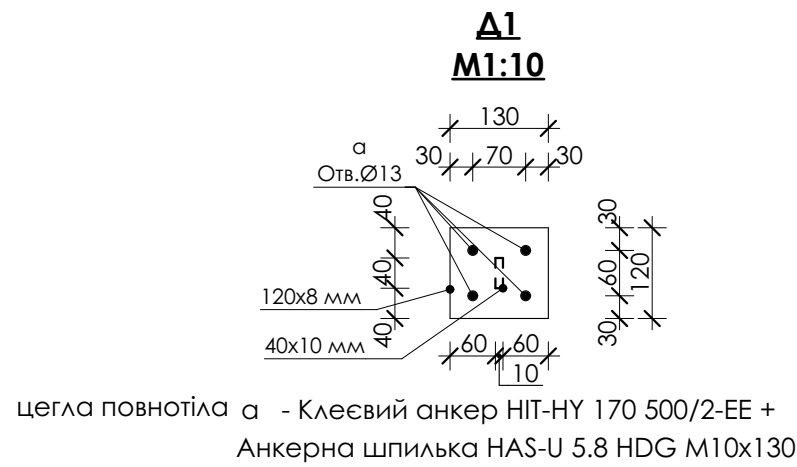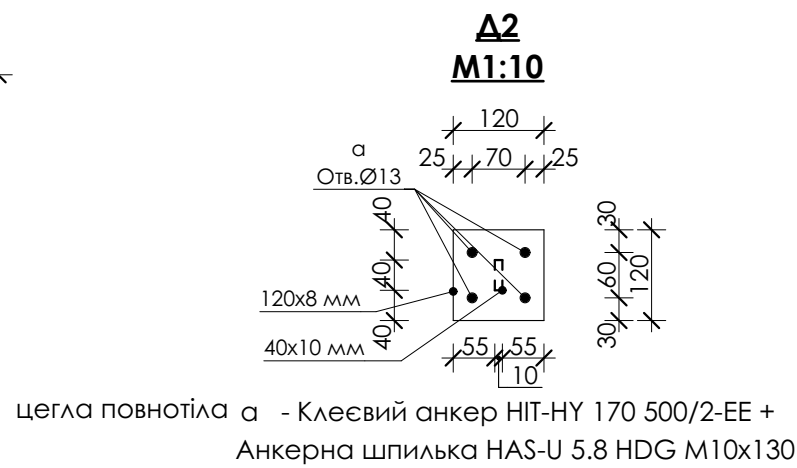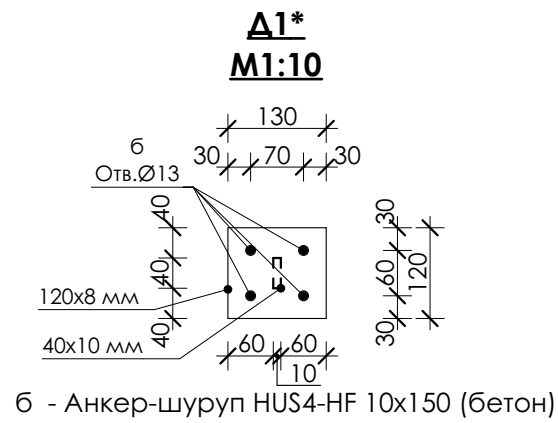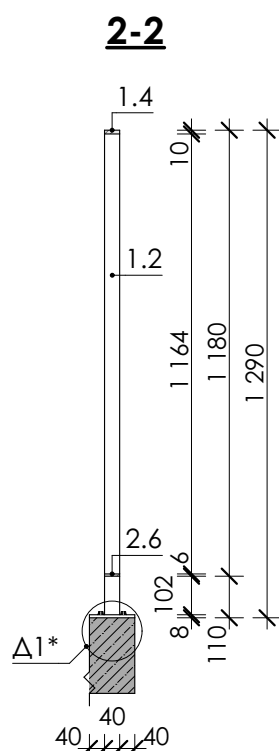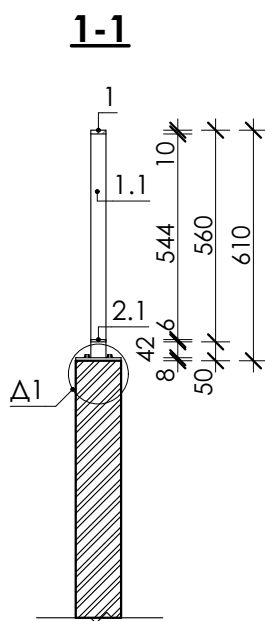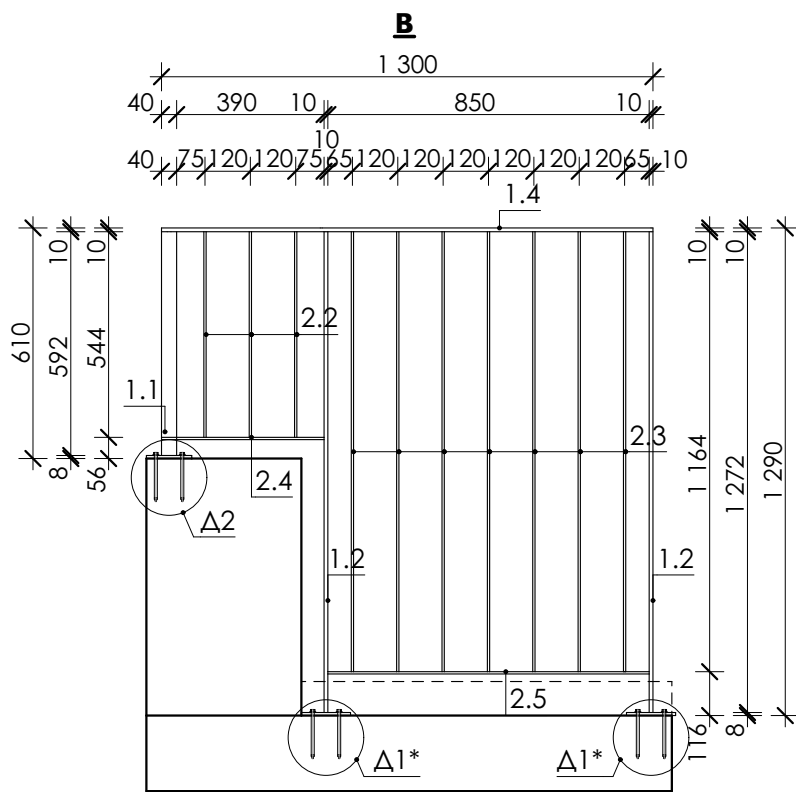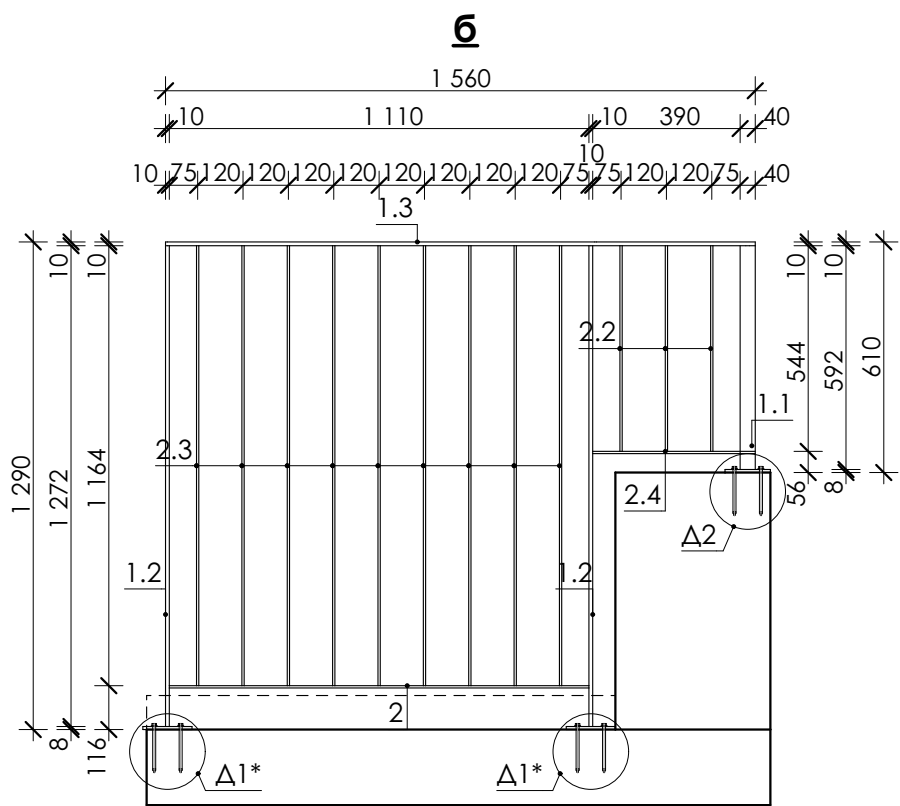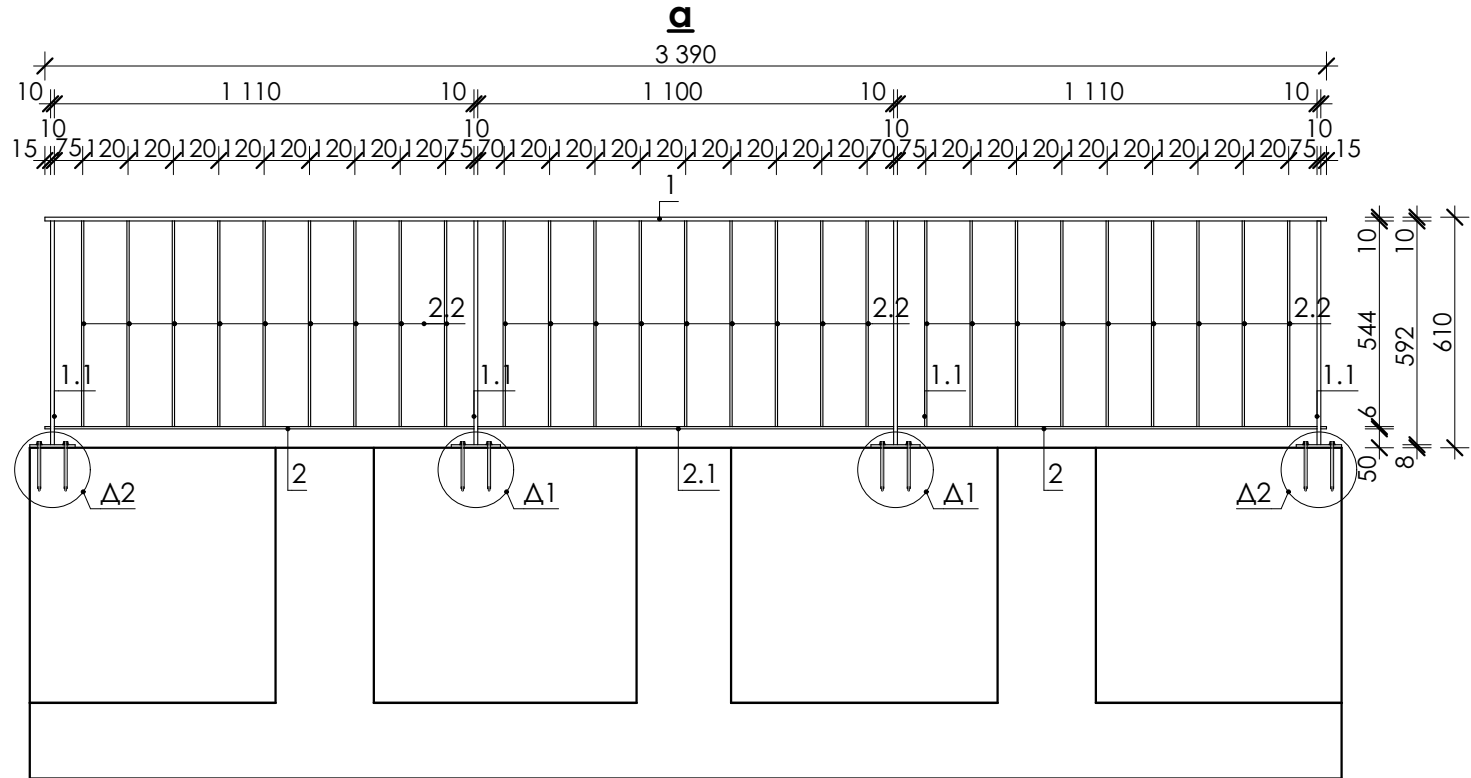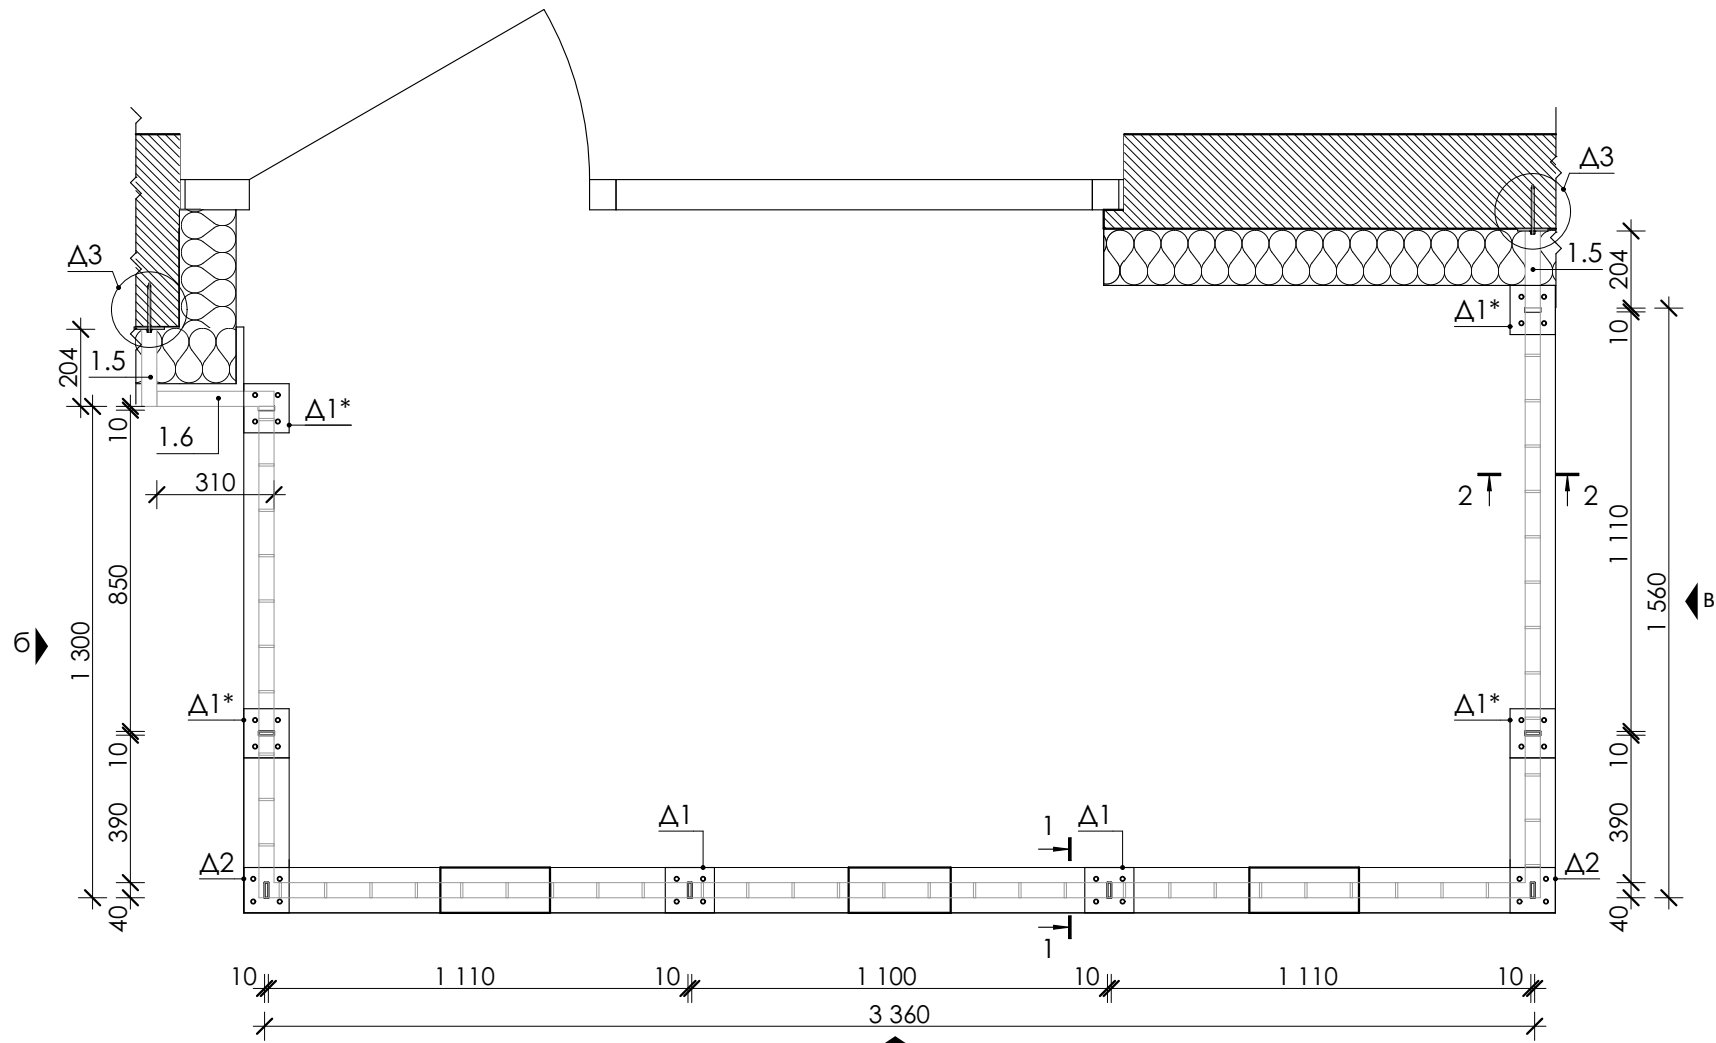




Марка поз.	Позначення	Найменування	L,м	К-сть,шт	Маса 1 м.п.,кг	Маса од., кг	Загальна L,м	Загальні витрати кг на 1шт.
ОГ-10								
1	ΔСТУ 4747-2007	□ 40x10	3,39	1	3,14	10,64	3,39	10,64
1.1	ΔСТУ 4747-2007	□ 40x10	0,592	4	3,14	1,86	2,37	7,44
1.2	ΔСТУ 4747-2007	□ 40x10	1,272	4	3,14	3,99	5,09	15,98
1.3	ΔСТУ 4747-2007	□ 40x10	1,56	1	3,14	4,90	1,56	4,90
1.4	ΔСТУ 4747-2007	□ 40x10	1,3	1	3,14	4,08	1,30	4,08
1.5	ΔСТУ 4747-2007	□ 40x10	0,204	2	3,14	0,64	0,41	1,28
1.6	ΔСТУ 4747-2007	□ 40x10	0,31	1	3,14	0,97	0,31	0,97
							14,42	45,29
2	ΔСТУ 4747-2007	□ 40x6	1,11	3	1,884	2,09	3,33	6,27
2.1	ΔСТУ 4747-2007	□ 40x6	1,10	1	1,884	2,07	1,10	2,07
2.2	ΔСТУ 4747-2007	□ 40x6	0,544	33	1,884	1,02	17,95	33,82
2.3	ΔСТУ 4747-2007	□ 40x6	1,164	16	1,884	2,19	18,62	35,09
2.4	ΔСТУ 4747-2007	□ 40x6	0,39	2	1,884	0,73	0,78	1,47
2.5	ΔСТУ 4747-2007	□ 40x6	0,85	1	1,884	1,60	0,85	1,60
							42,64	80,33
Δ1/Δ1*	ΔСТУ 4747-2007	— 120x8	0,13	6	7,536	0,98	0,78	5,88
Δ2	ΔСТУ 4747-2007	— 120x8	0,12	2	7,536	0,90432	0,24	1,81
Δ3	ΔСТУ 4747-2007	— 80x6	0,2	2	3,768	0,7536	0,40	1,51
							1,42	9,19
	Клеєвий анкер HIT-HY 170 500/2-EE +			20				
	Анкерна шпилька HAS-U 5.8 HDG M10x130			20				
	Анкер-шуруп HUS4-HF 10x150 (бетон)			16				
	Накладка на опору 40x10			8				
						ОГ-10	7 шт.	

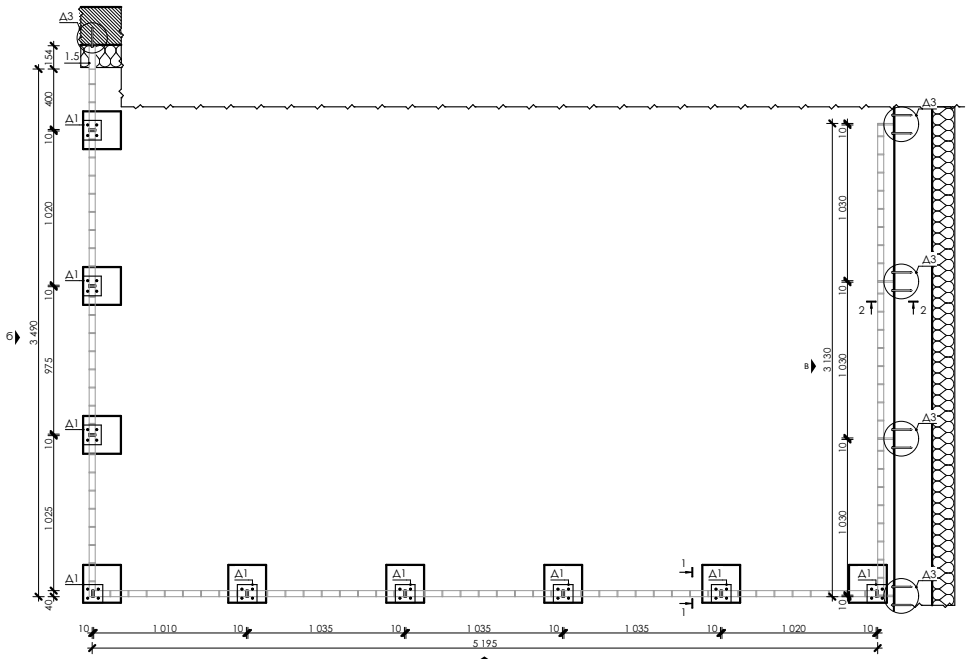


1-1

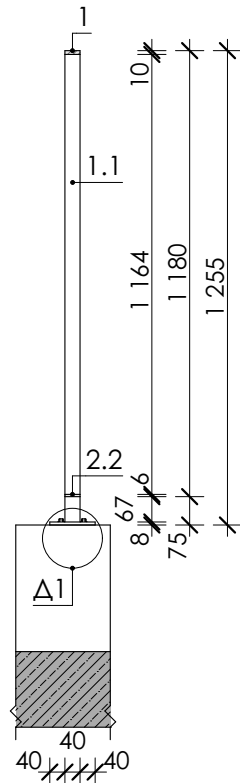

2-2

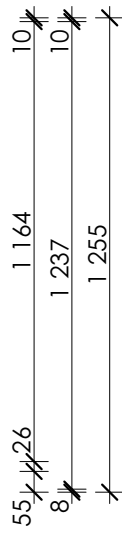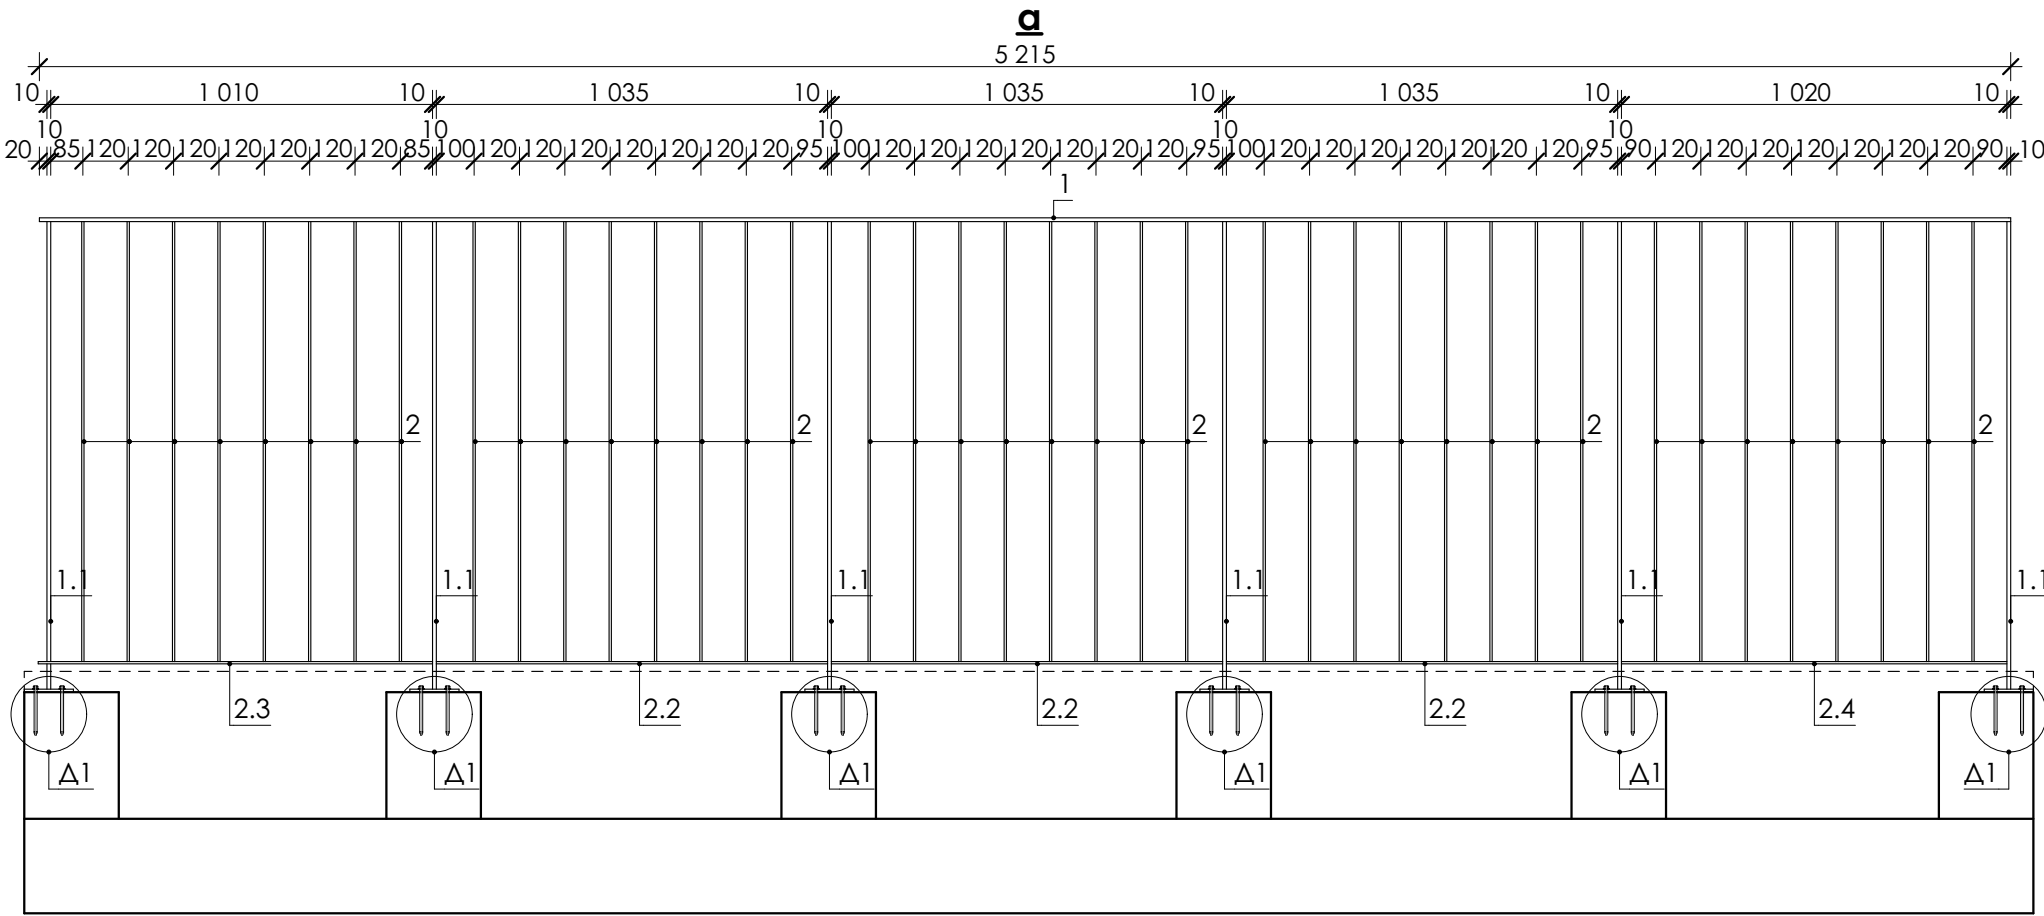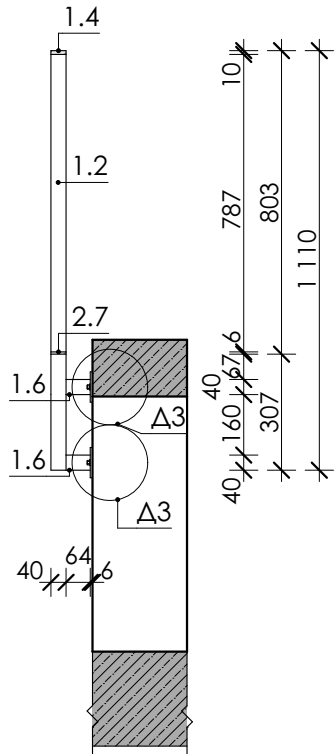


Δ1
M1:10


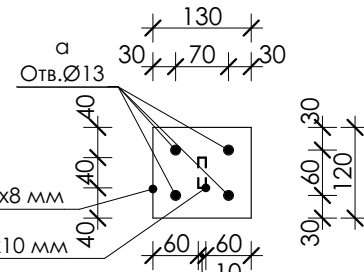


цегла повнотіла а - Клеєвий анкер HIT-HY 170 500/2-EE +
Анкерна шпилька HAS-U 5.8 HDG M10x130










Δ3
M1:10

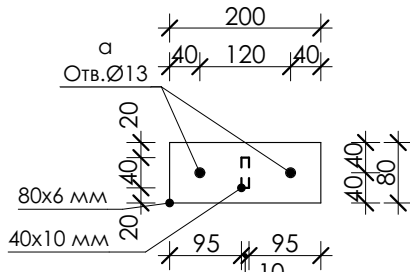


цегла повнотіла а - Клеєвий анкер HIT-HY 170 500/2-EE +
Анкерна шпилька HAS-U 5.8 HDG M10x130

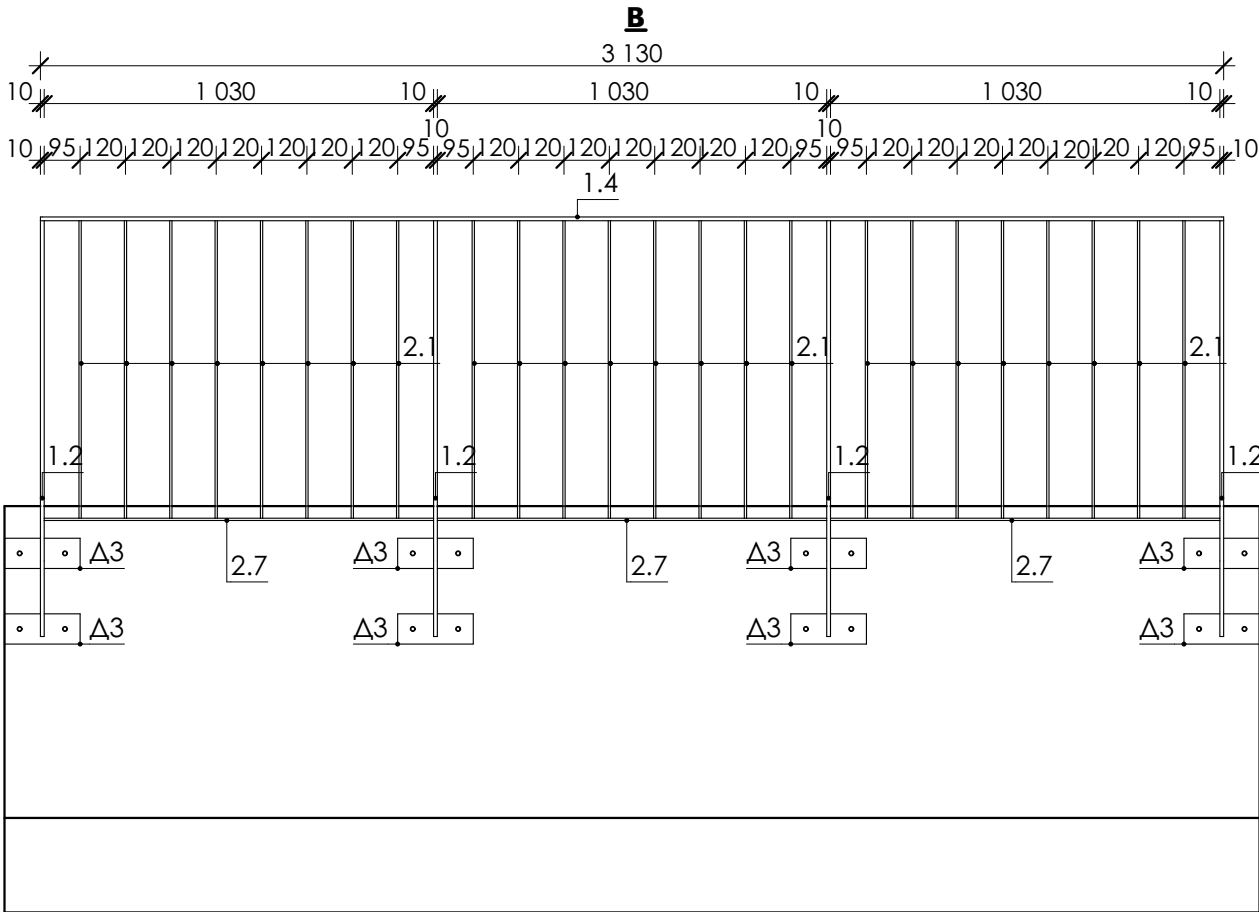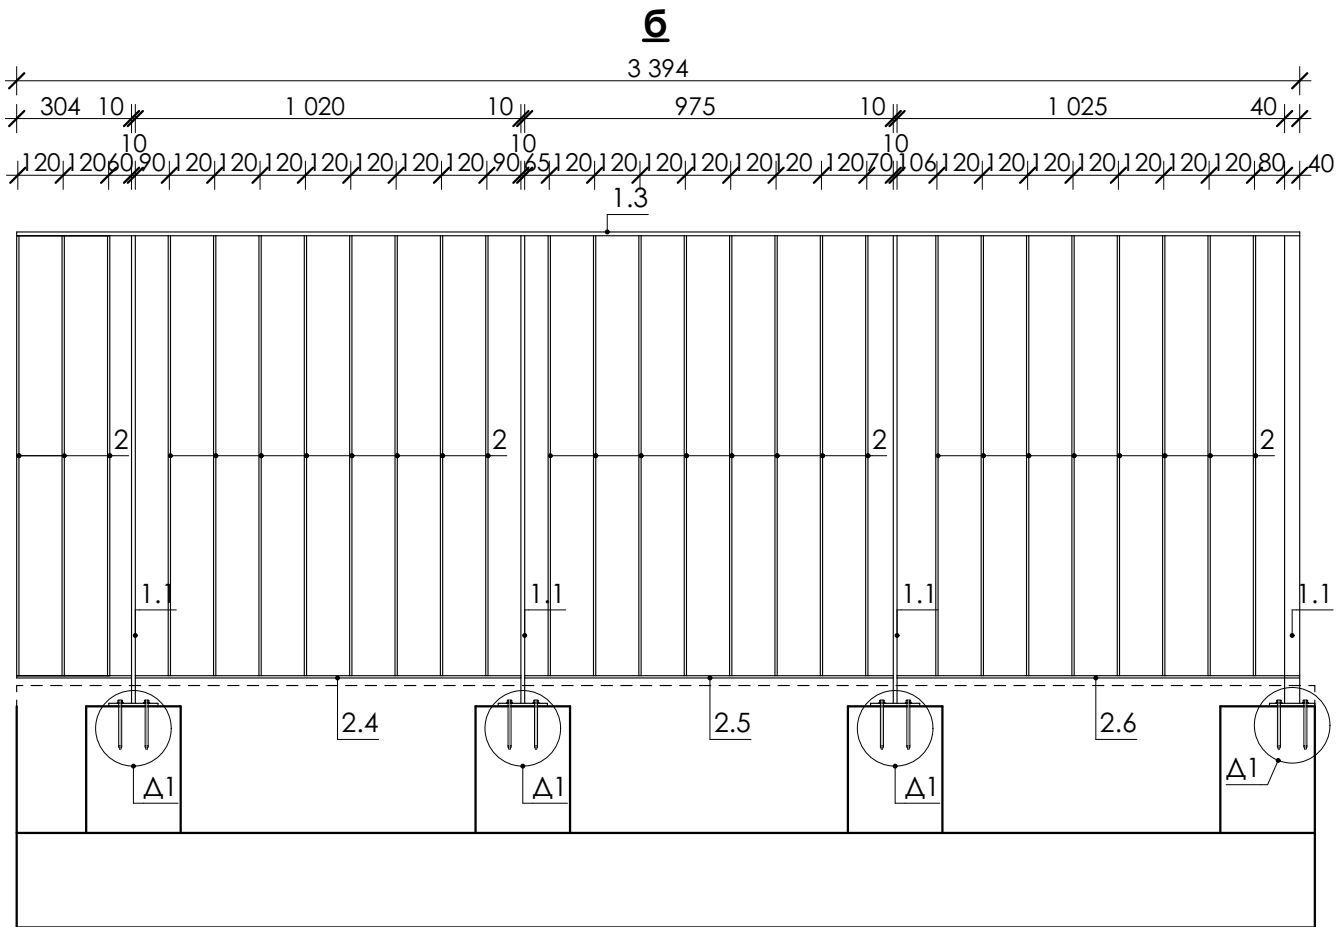


ОГТ-2

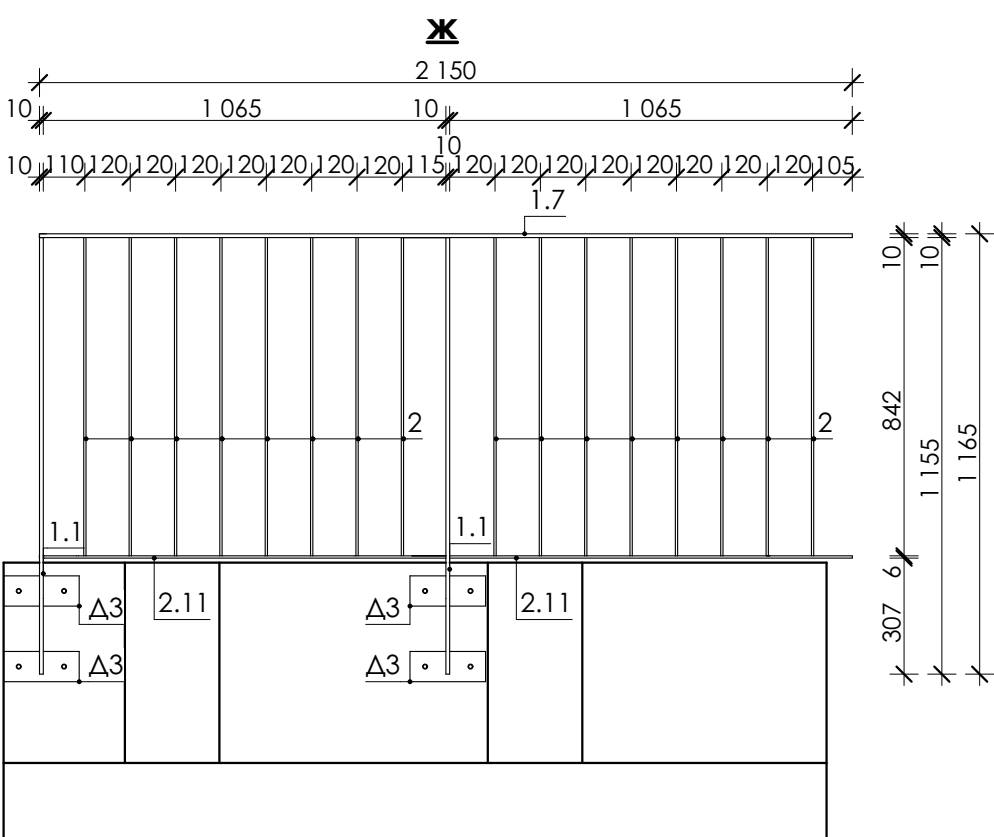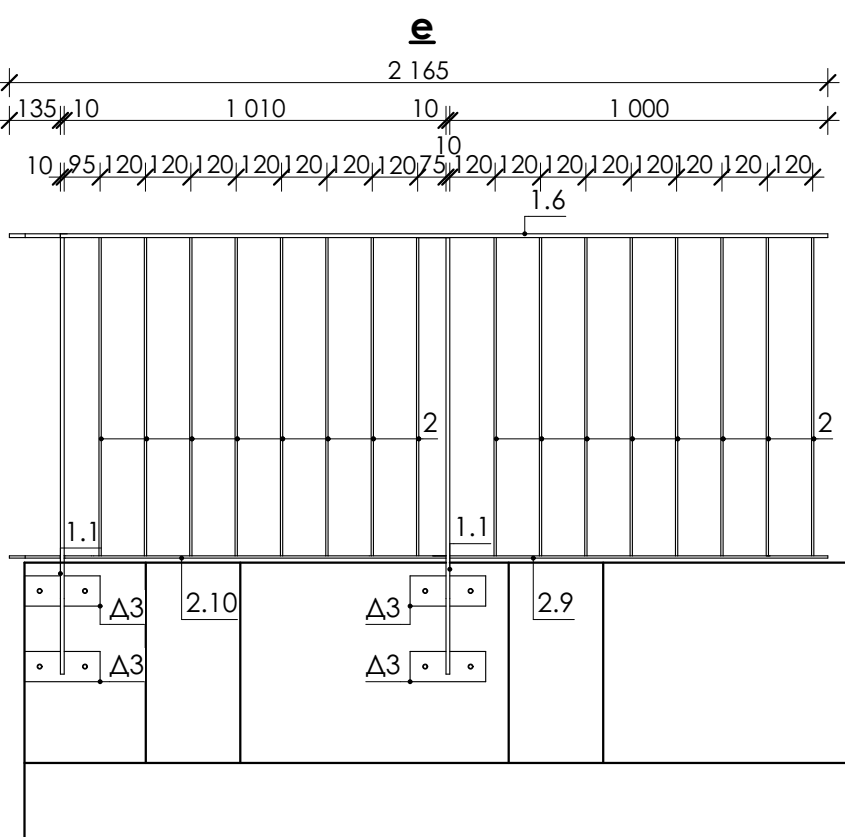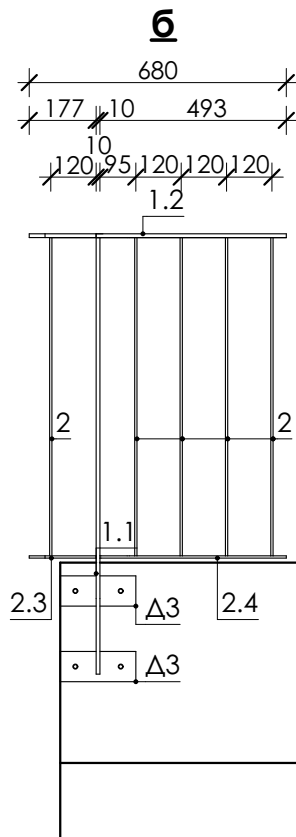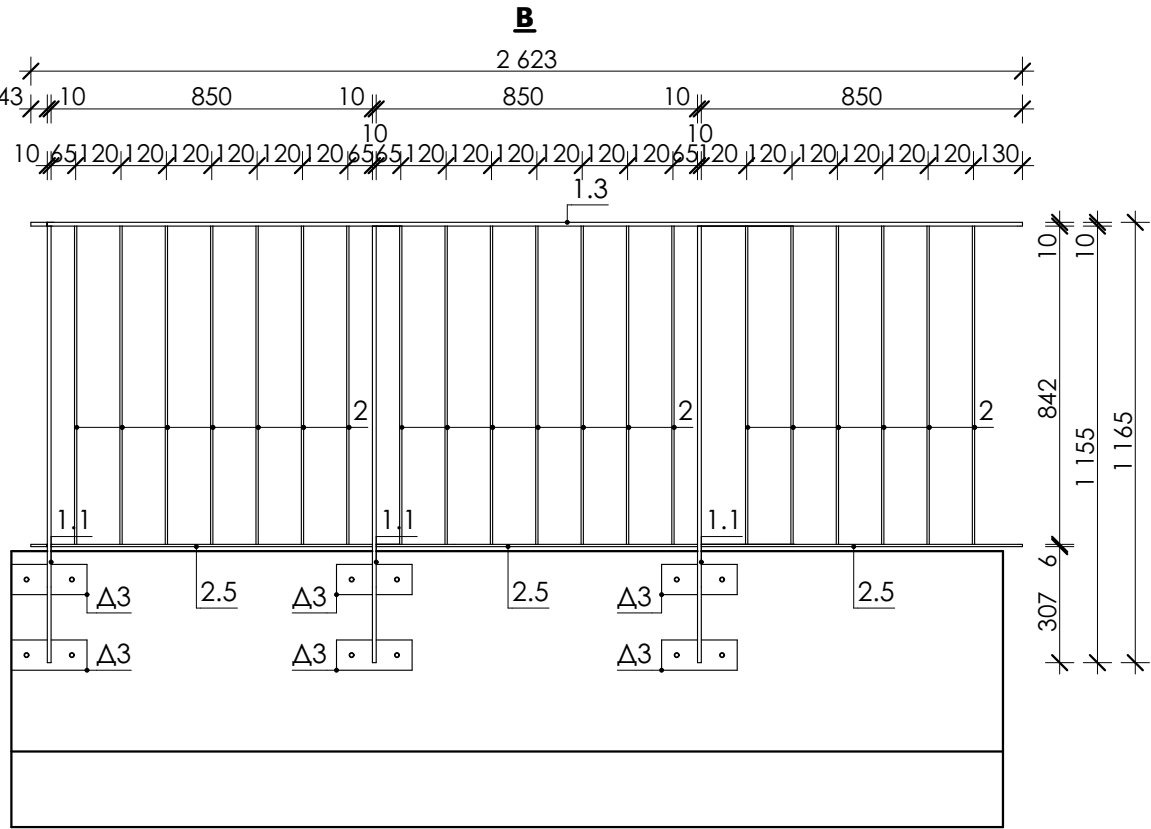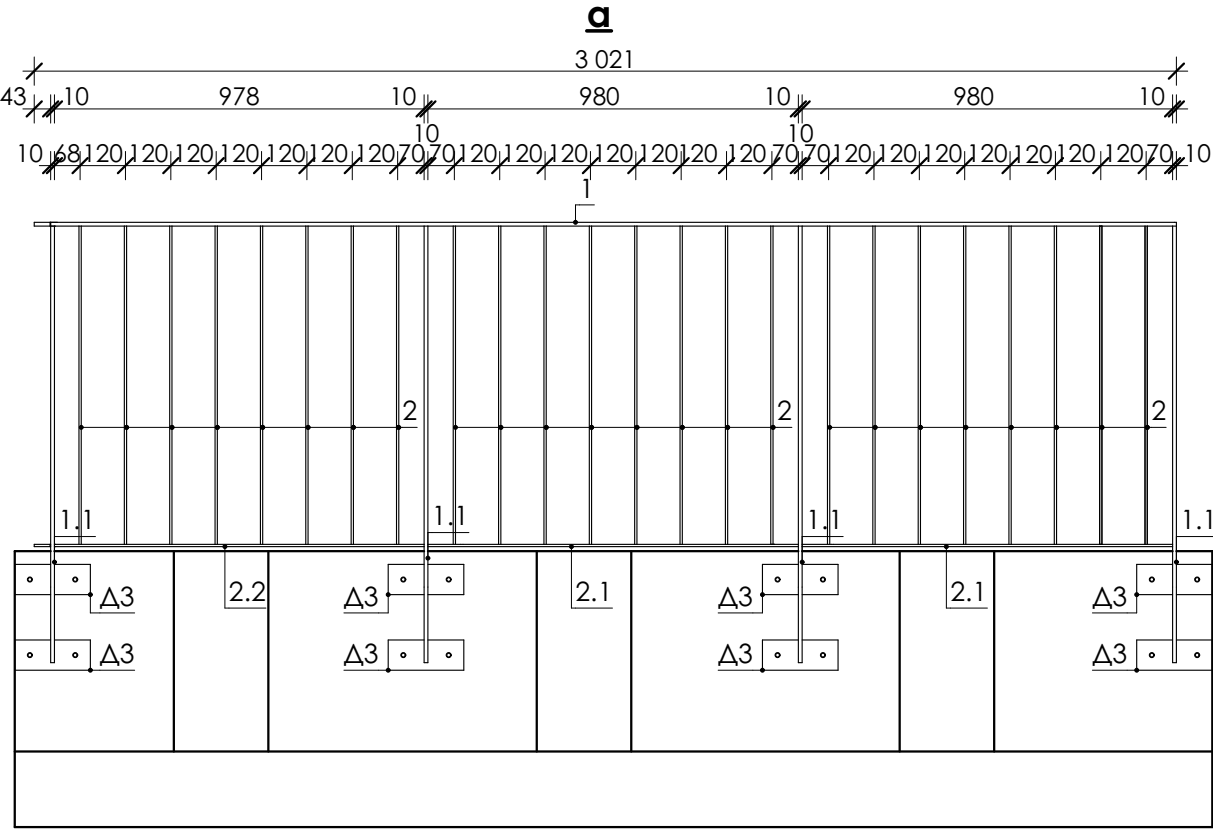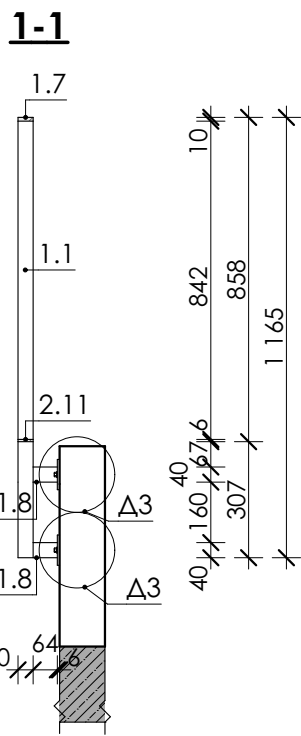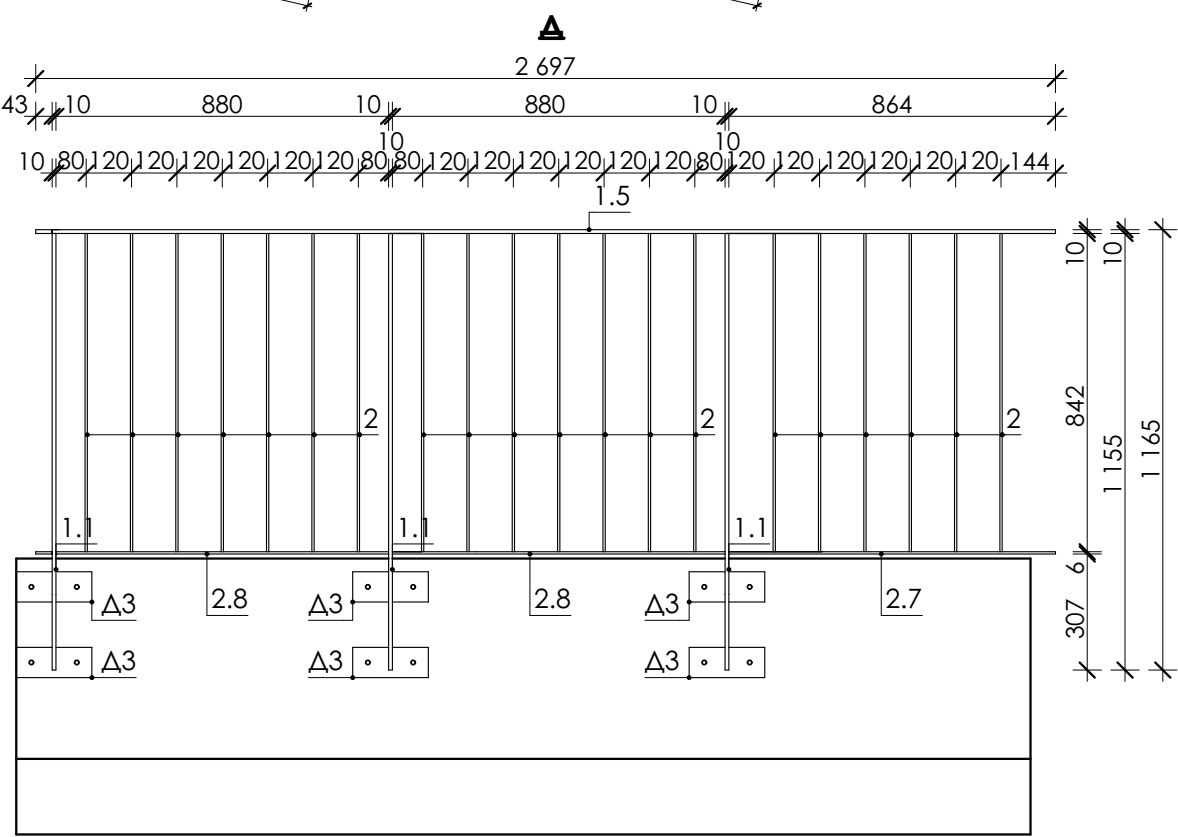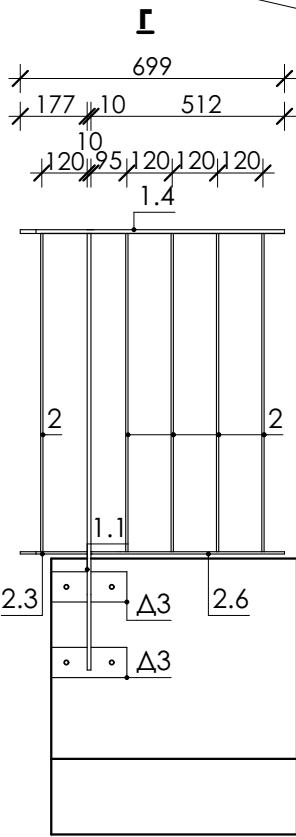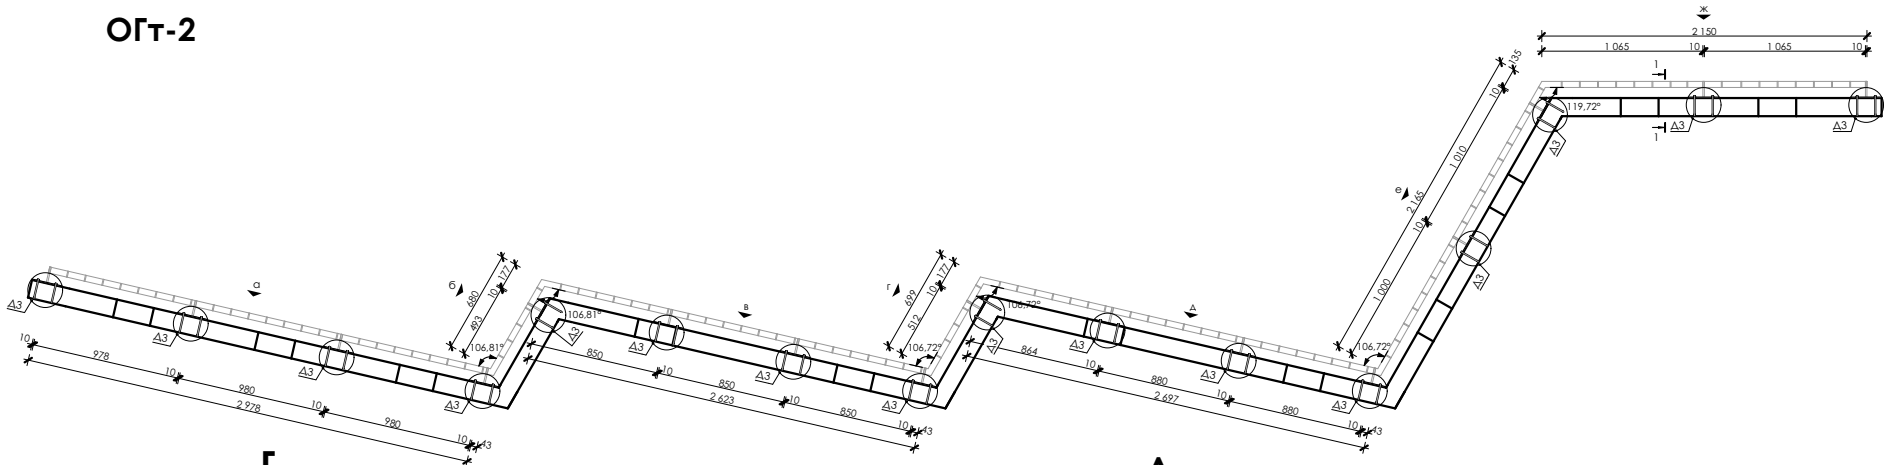








Марка поз.	Позначення	Найменування	L,м	К-сть,шт	Маса 1 м.п.,кг	Маса од., кг	Загальн а L,м	Загальні витрати кг на 1шт.
ОГТ-2								
1	ΔСТУ 4747-2007	□ 40x10	3,021	1	3,14	9,49	3,02	9,49
1.1	ΔСТУ 4747-2007	□ 40x10	1,155	16	3,14	3,63	18,48	58,03
1.2	ΔСТУ 4747-2007	□ 40x10	0,68	1	3,14	2,14	0,68	2,14
1.3	ΔСТУ 4747-2007	□ 40x10	2,623	1	3,14	8,24	2,62	8,24
1.4	ΔСТУ 4747-2007	□ 40x10	0,699	1	3,14	2,19	0,70	2,19
1.5	ΔСТУ 4747-2007	□ 40x10	2,697	1	3,14	8,47	2,70	8,47
1.6	ΔСТУ 4747-2007	□ 40x10	2,165	1	3,14	6,80	2,17	6,80
1.7	ΔСТУ 4747-2007	□ 40x10	2,15	1	3,14	6,75	2,15	6,75
1.8	ΔСТУ 4747-2007	□ 40x10	0,064	32	3,14	0,20	2,05	6,43
							34,56	108,53
2	ΔСТУ 4747-2007	□ 40x6	0,842	106	1,884	1,59	89,25	168,15
2.1	ΔСТУ 4747-2007	□ 40x6	0,98	2	1,884	1,85	1,96	3,69
2.2	ΔСТУ 4747-2007	□ 40x6	0,978	1	1,884	1,84	0,98	1,84
2.3	ΔСТУ 4747-2007	□ 40x6	0,177	2	1,884	0,33	0,35	0,67
2.4	ΔСТУ 4747-2007	□ 40x6	0,493	1	1,884	0,93	0,49	0,93
2.5	ΔСТУ 4747-2007	□ 40x6	0,85	3	1,884	1,60	2,55	4,80
2.6	ΔСТУ 4747-2007	□ 40x6	0,512	1	1,884	0,96	0,51	0,96
2.7	ΔСТУ 4747-2007	□ 40x6	0,864	1	1,884	1,63	0,86	1,63
2.8	ΔСТУ 4747-2007	□ 40x6	0,88	2	1,884	1,66	1,76	3,32
2.9	ΔСТУ 4747-2007	□ 40x6		1	1,884	1,88	1,00	1,88
2.10	ΔСТУ 4747-2007	□ 40x6	1,01	1	1,884	1,90	1,01	1,90
2.11	ΔСТУ 4747-2007	□ 40x6	1,065	2	1,884	2,01	2,13	4,01
Δ3	ΔСТУ 4747-2007	— 80x6	0,2	32	3,768	0,7536	102,86	193,79
							6,40	24,12
Клеєвий анкер HIT-HY 170 500/2-EE +				64				
Анкерна шпилька HAS-U 5.8 HDG M10x130				64				
ОГТ-2							1 шт.	

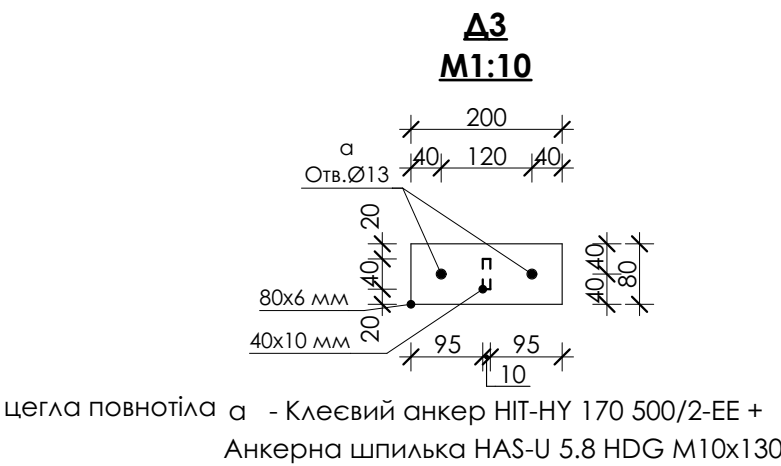

ОГТ-3


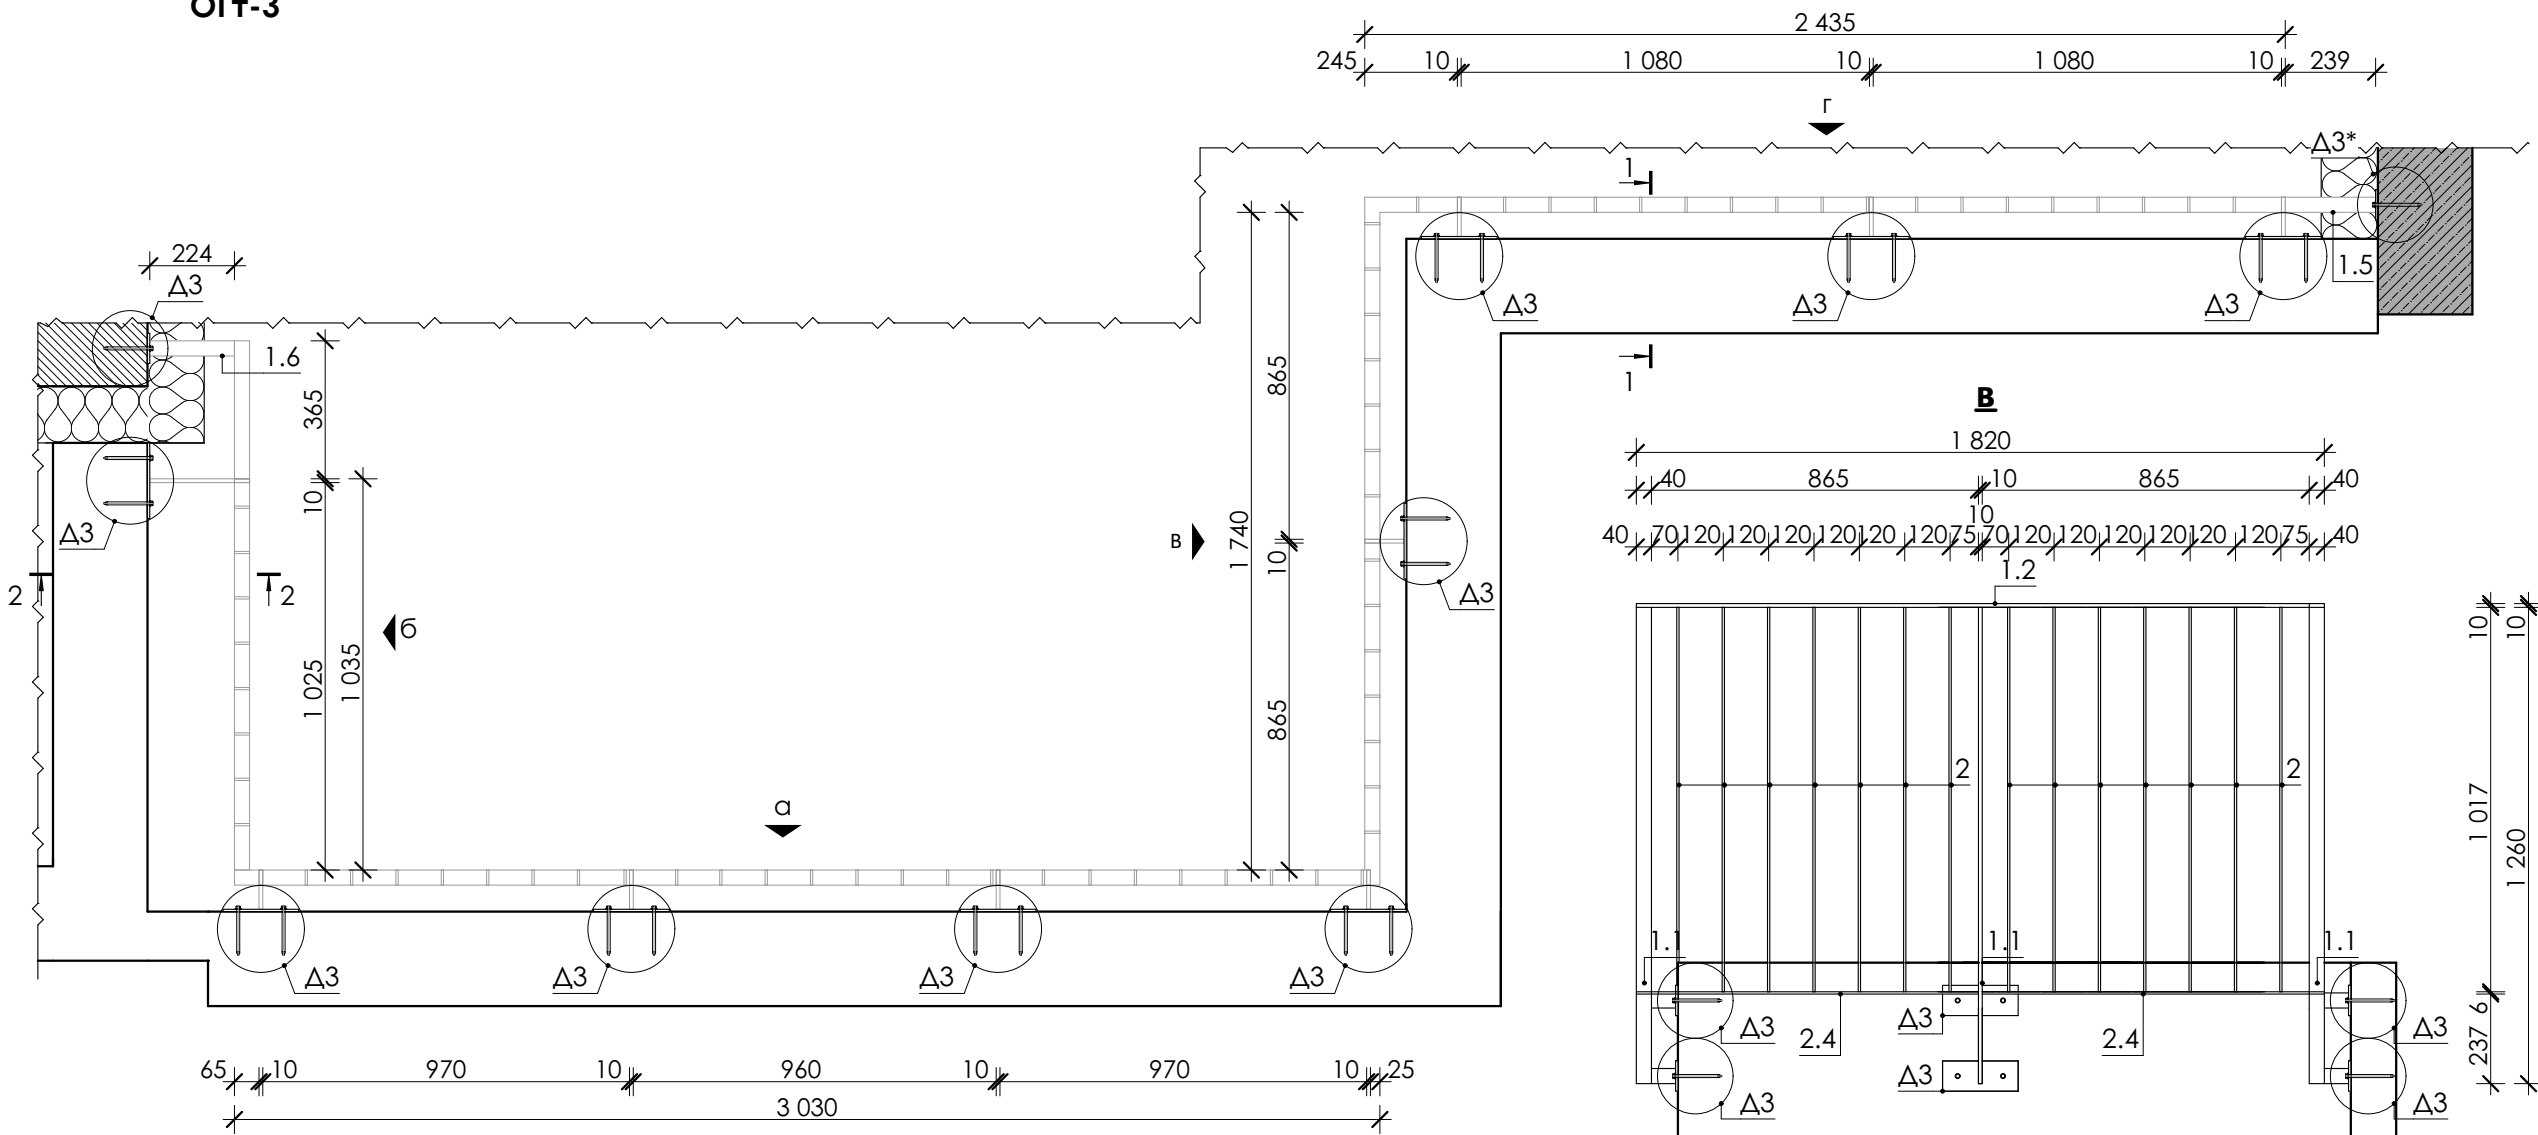


Марка поз.	Позначення	Найменування	L,м	К-сть,шт	Маса 1 м.п.,кг	Маса од., кг	Загальн а L,м	Загальні витрати кг на 1шт.
ОГТ-3								
1	ΔСТУ 4747-2007	□ 40x10	2,94	1	3,14	9,23	2,94	9,23
1.1	ΔСТУ 4747-2007	□ 40x10	1,26	9	3,14	3,96	11,34	35,61
1.2	ΔСТУ 4747-2007	□ 40x10	1,82	1	3,14	5,71	1,82	5,71
1.3	ΔСТУ 4747-2007	□ 40x10	2,435	1	3,14	7,65	2,44	7,65
1.4	ΔСТУ 4747-2007	□ 40x10	1,07	1	3,14	3,36	1,07	3,36
1.5	ΔСТУ 4747-2007	□ 40x10	0,239	1	3,14	0,75	0,24	0,75
1.6	ΔСТУ 4747-2007	□ 40x10	0,224	3	3,14	0,70	0,67	2,11
1.7	ΔСТУ 4747-2007	□ 40x10	0,064	16	3,14	0,20	1,02	3,22
							21,54	67,64
2	ΔСТУ 4747-2007	□ 40x6	1,017	62	1,884	1,92	63,05	118,79
2.1	ΔСТУ 4747-2007	□ 40x6	0,97	2	1,884	1,83	1,94	3,65
2.2	ΔСТУ 4747-2007	□ 40x6	0,96	1	1,884	1,81	0,96	1,81
2.3	ΔСТУ 4747-2007	□ 40x6	1,070	1	1,884	2,02	1,07	2,02
2.4	ΔСТУ 4747-2007	□ 40x6	0,865	2	1,884	1,63	1,73	3,26
2.5	ΔСТУ 4747-2007	□ 40x6	1,08	2	1,884	2,03	2,16	4,07
							70,91	133,60
Δ3/Δ3*	ΔСТУ 4747-2007	— 80x6	0,2	11	3,768	0,7536	2,20	8,29
							2,20	8,29
	Клеєвий анкер HIT-HY 170 500/2-EE +			20				
	Анкерна шпилька HAS-U 5.8 HDG M10x130			20				
	Анкер-шуруп HUS4-HF 10x150 (бетон)			2				
ОГТ-3							1 шт.	

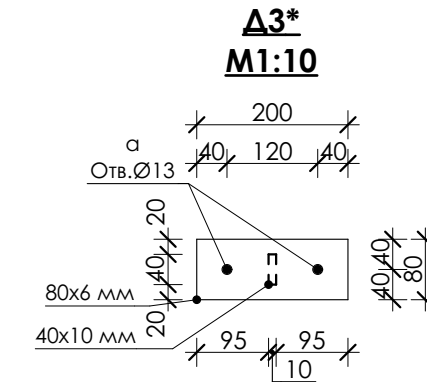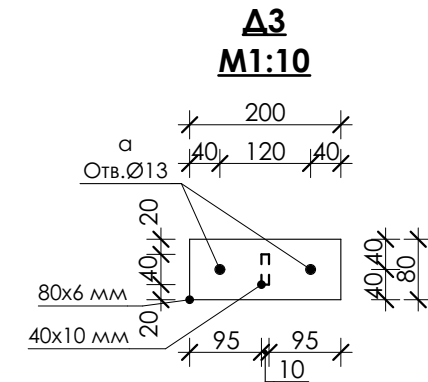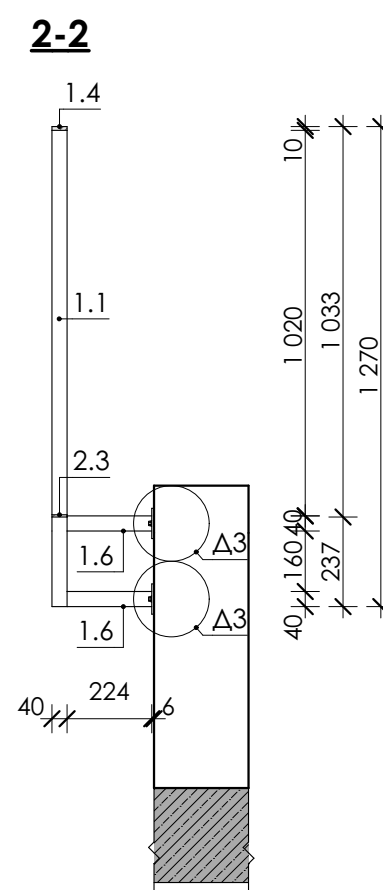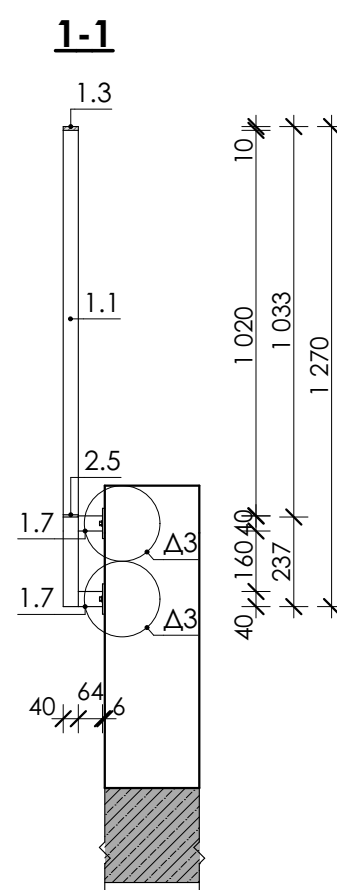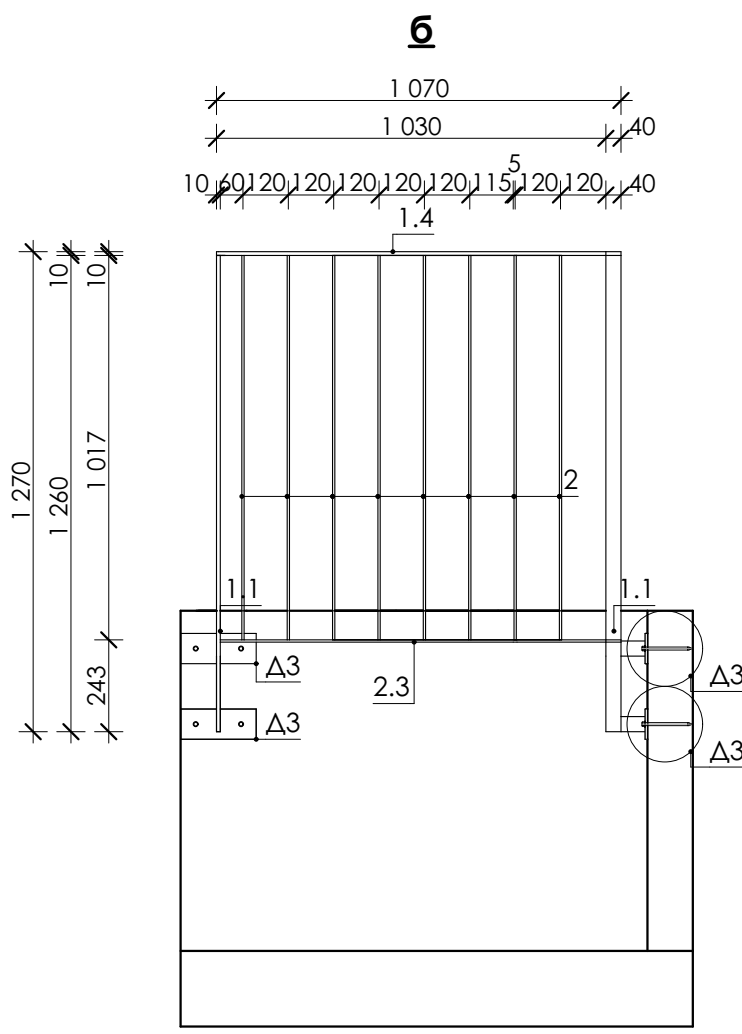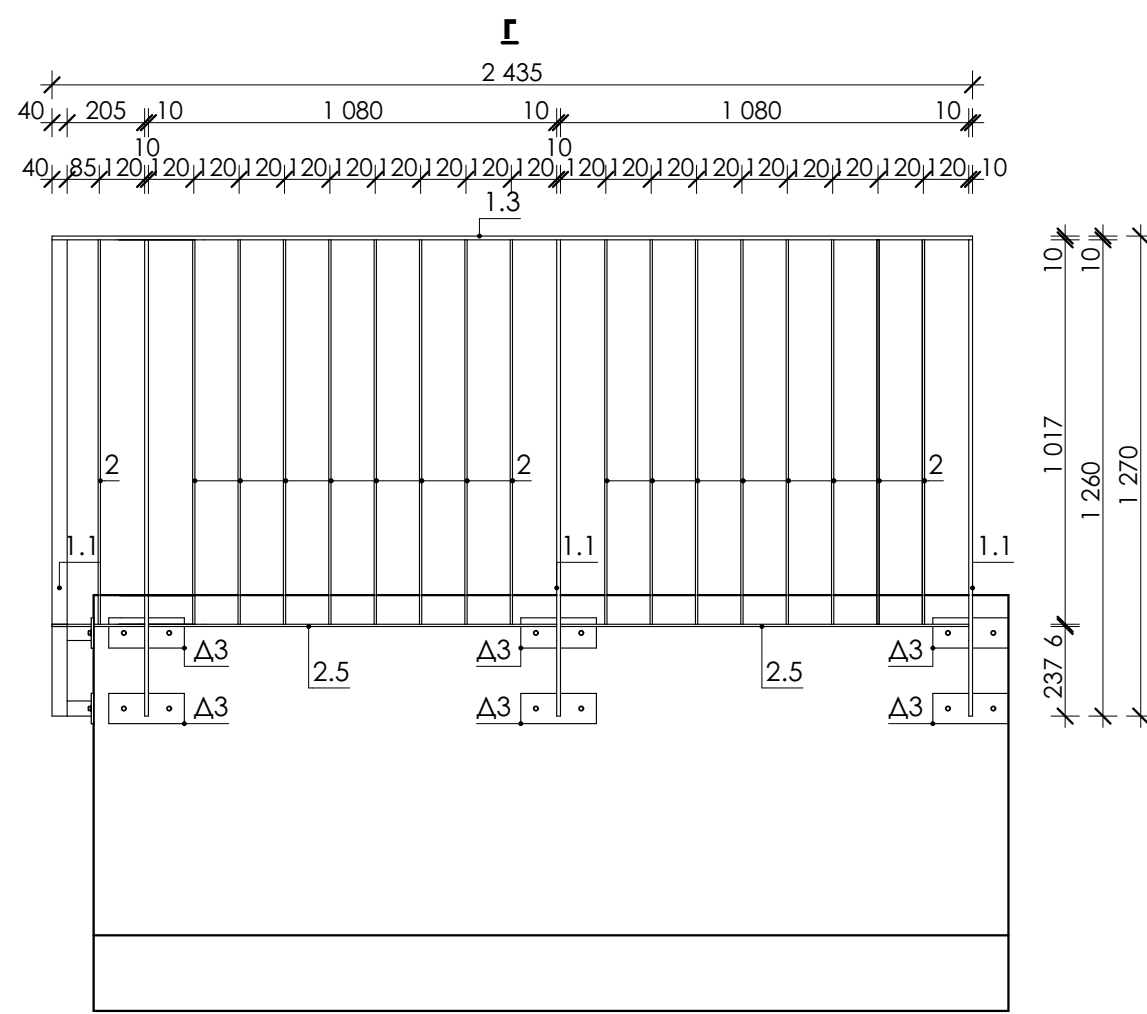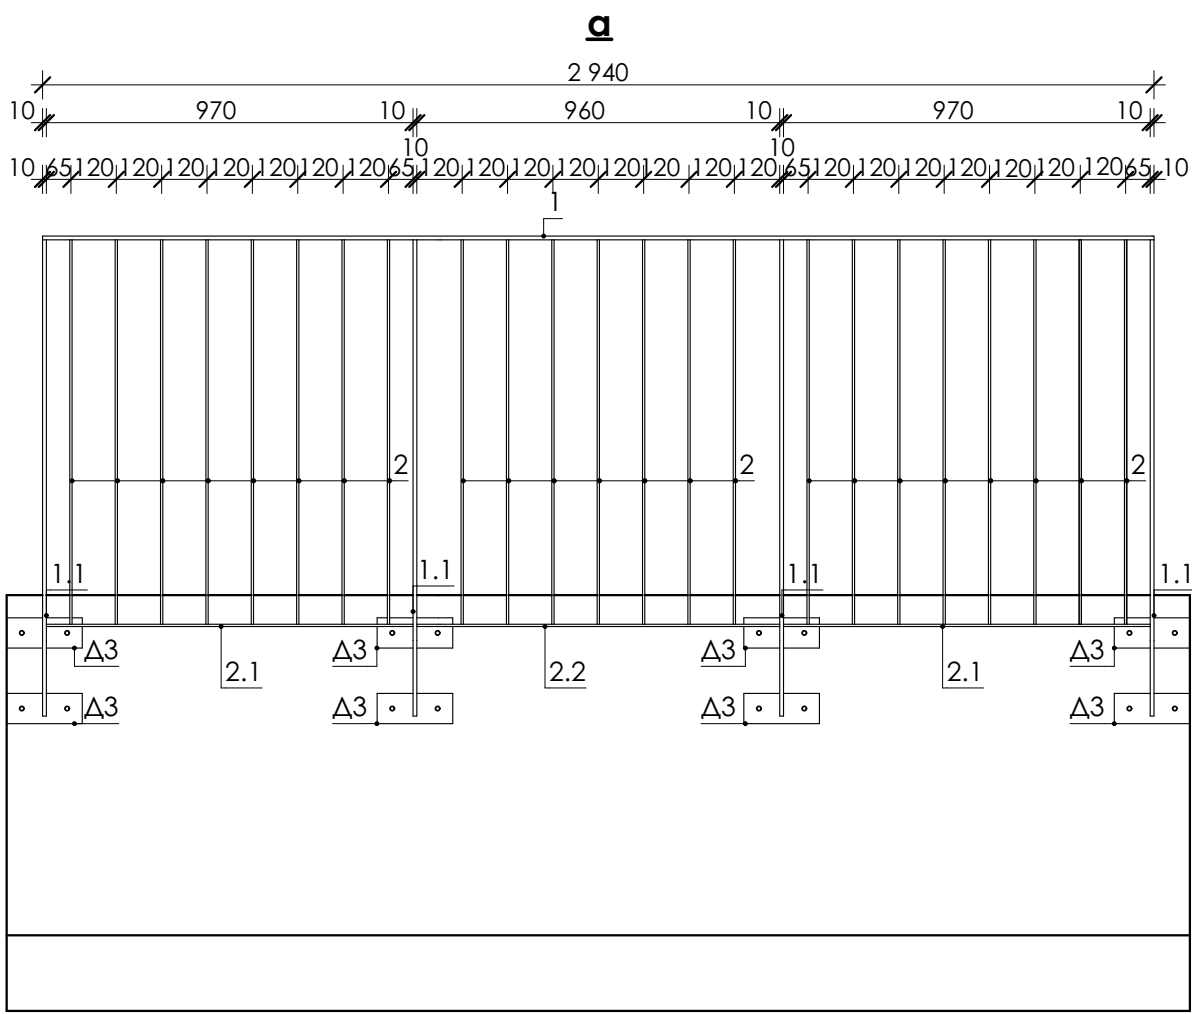


цегла повнотіла а - Клеєвий анкер HIT-HY 170 500/2-EE + Анкерна шпилька HAS-U 5.8 HDG M10x130

б - Анкер-шуруп HUS4-HF 10x150 (бетон)

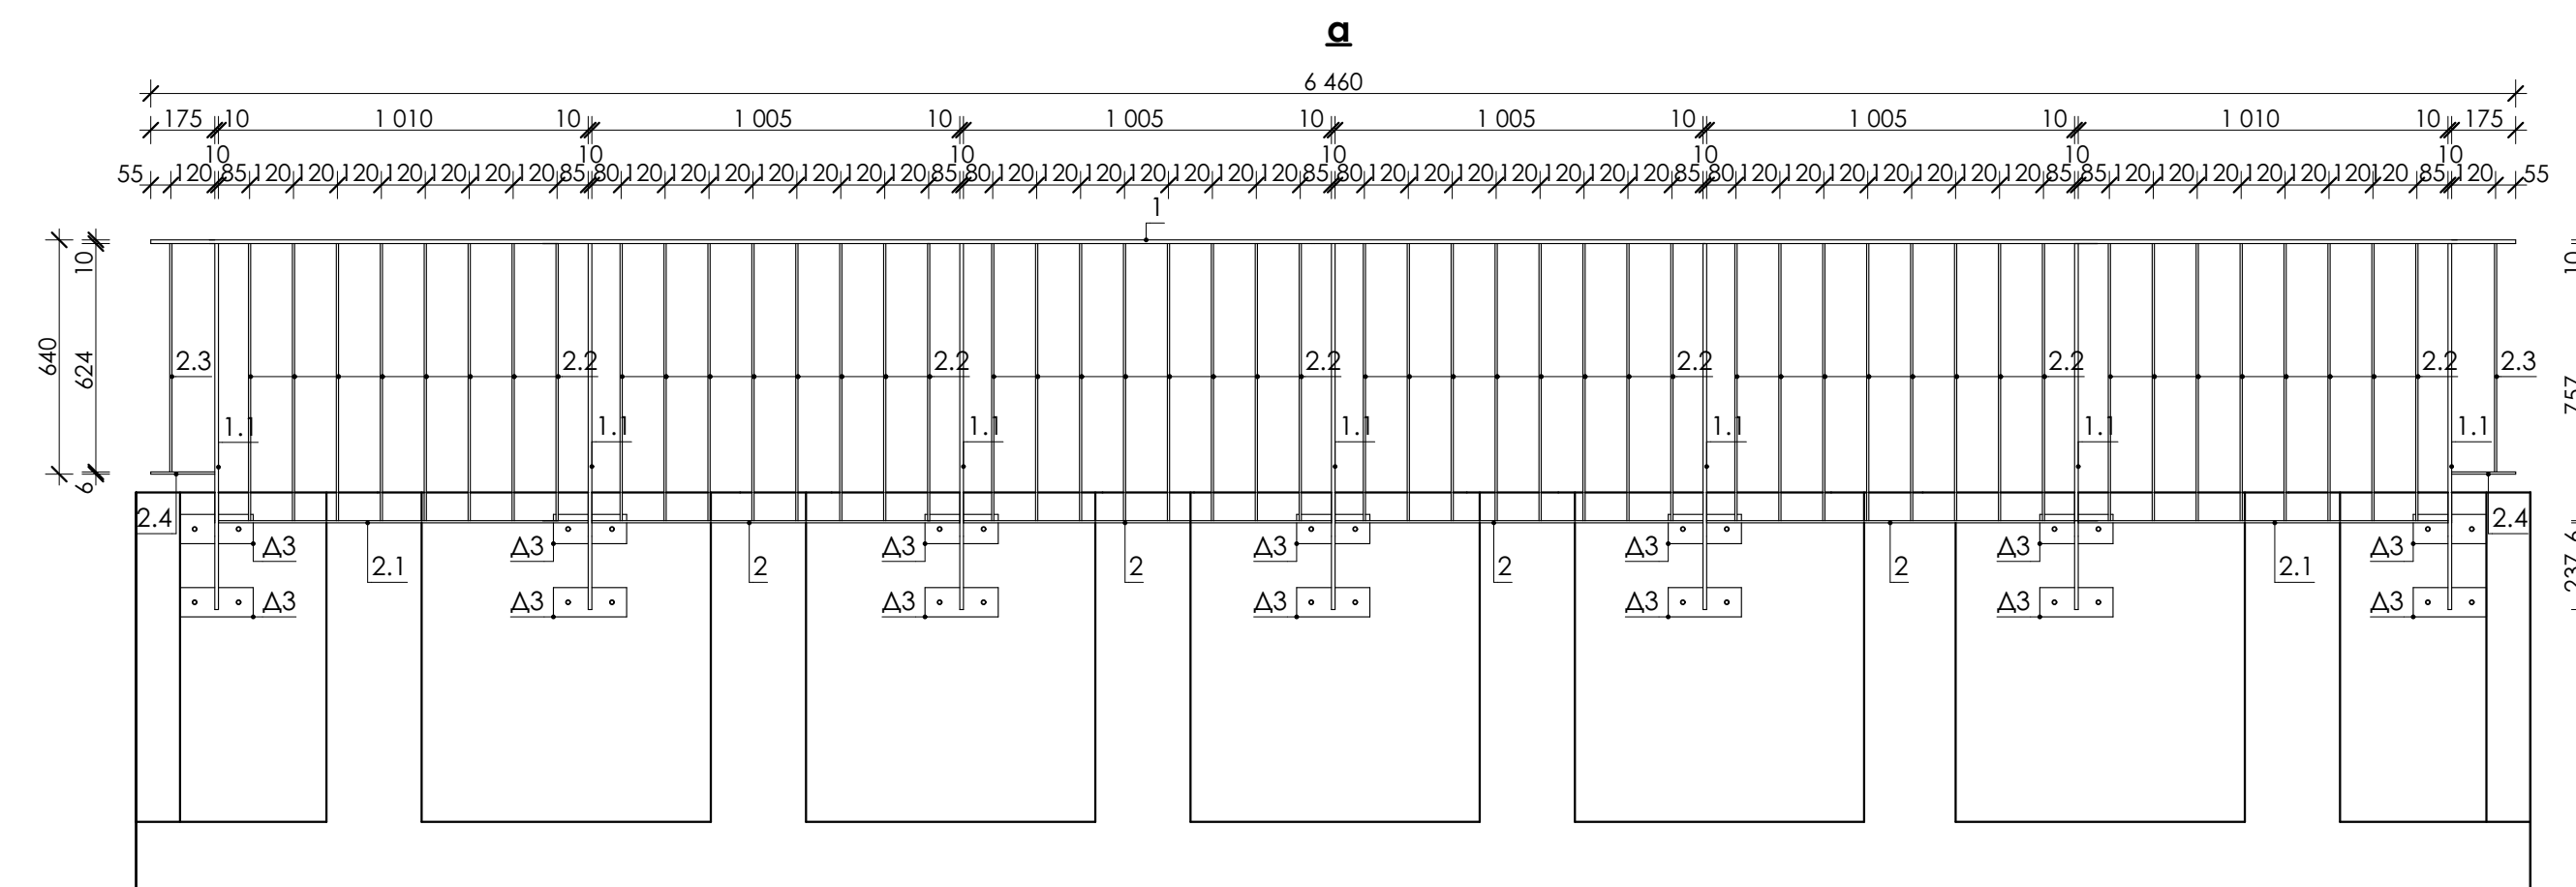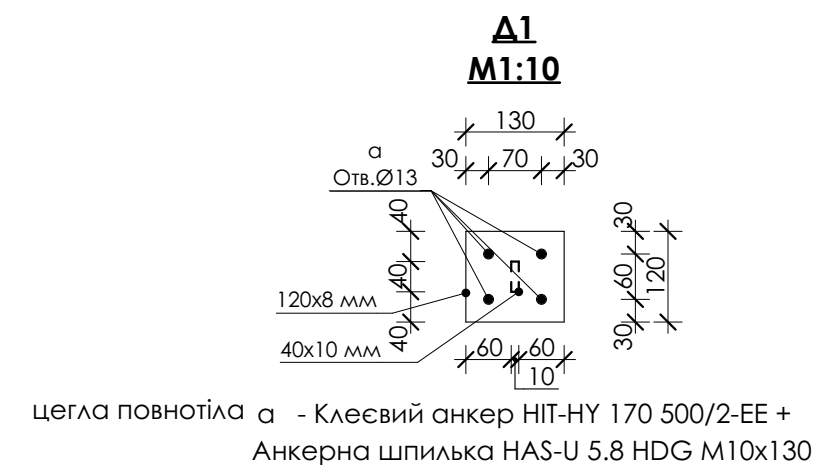

Марка поз.	Позначення	Найменування	L,м	К- сть,шт	Маса 1 м.п.,кг	Маса од., кг	Загальн а L,м	Загальні витрати кг на 1шт.
ОГТ-4								
1	ΔCTY 4747-2007	□ 40x10	6,46	1	3,14	20,28	6,46	20,28
1.1	ΔCTY 4747-2007	□ 40x10	1	9	3,14	3,14	9,00	28,2
1.2	ΔCTY 4747-2007	□ 40x10	1,46	1	3,14	4,58	1,46	4,58
1.3	ΔCTY 4747-2007	□ 40x10	1,42	1	3,14	4,46	1,42	4,46
1.4	ΔCTY 4747-2007	□ 40x10	0,309	1	3,14	0,97	0,31	0,97
1.5	ΔCTY 4747-2007	□ 40x10	0,299	1	3,14	0,94	0,30	0,94
1.6	ΔCTY 4747-2007	□ 40x10	0,09	1	3,14	0,28	0,09	0,28
1.7	ΔCTY 4747-2007	□ 40x10	0,672	2	3,14	2,11	1,34	4,22
1.8	ΔCTY 4747-2007	□ 40x10	0,174	4	3,14	0,55	0,70	2,19
1.9	ΔCTY 4747-2007	□ 40x10	0,064	14	3,14	0,20	0,90	2,81
							21,97	69,00
2	ΔCTY 4747-2007	□ 40x6	1,005	4	1,884	1,89	4,02	7,57
2.1	ΔCTY 4747-2007	□ 40x6	1,01	2	1,884	1,90	2,02	3,81
2.2	ΔCTY 4747-2007	□ 40x6	0,757	56	1,884	1,43	42,39	79,87
2.3	ΔCTY 4747-2007	□ 40x6	0,624	17	1,884	1,18	10,61	19,99
2.4	ΔCTY 4747-2007	□ 40x6	0,175	2	1,884	0,33	0,35	0,66
2.5	ΔCTY 4747-2007	□ 40x6	0,7	1	1,884	1,32	0,70	1,32
2.6	ΔCTY 4747-2007	□ 40x6	0,740	1	1,884	1,39	0,74	1,39
2.7	ΔCTY 4747-2007	□ 40x6	0,98	1	1,884	1,85	0,98	1,85
2.8	ΔCTY 4747-2007	□ 40x6	0,42	1	1,884	0,79	0,42	0,79
							62,23	117,24
Δ1	ΔCTY 4747-2007	— 120x8	0,13	2	7,536	0,98	0,26	1,96
Δ3/Δ3*	ΔCTY 4747-2007	— 80x6	0,2	20	3,768	0,7536	4,00	15,07
							4,26	17,03
	Клесвий анкер HIT-HY 170 500/2-EE +			46				
	Анкерна шпилька HAS-U 5.8 HDG M10x130			46				
	Накладка на опору 40x10			2				
	Анкер-шуруп HUS4-HF 10x150 (бетон)			2				
	ОГТ-4						1 шт.	







ОГТ-5

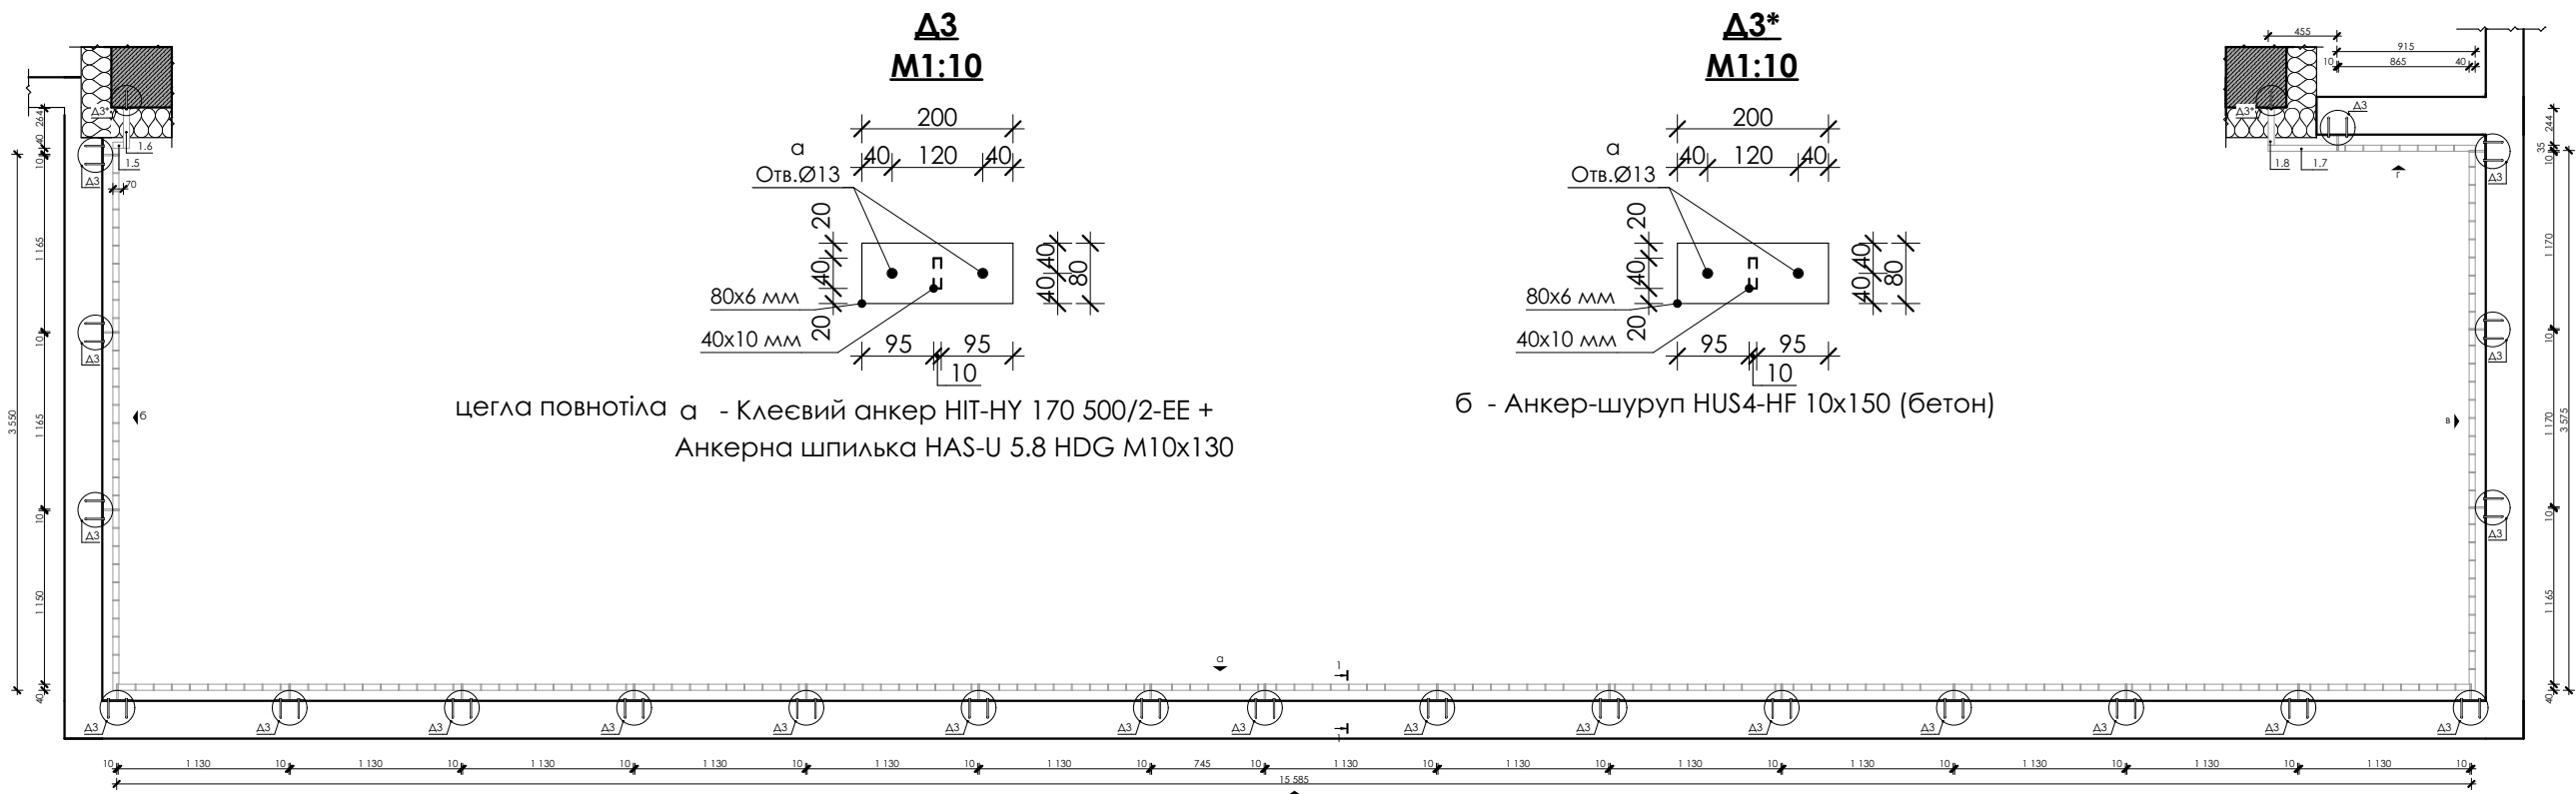


цегла повнотіла а - Клеєвий анкер HIT-HY 170 500/2-EE +
Анкерна шпилька HAS-U 5.8 HDG M10x130

б - Анкер-шуруп HUS4-HF 10x150 (бетон)



Марка поз.	Позначення	Найменування	L,м	К-сть,шт	Маса 1 м.п.,кг	Маса од., кг	Загальна L,м	Загальні витрати кг на 1шт.
ОГТ-5								
1	ΔСТУ 4747-2007	□ 40x10	15,635	1	3,14	49,09	15,64	49,09
1.1	ΔСТУ 4747-2007	□ 40x10	1,3	22	3,14	4,08	28,60	89,80
1.2	ΔСТУ 4747-2007	□ 40x10	3,535	1	3,14	11,10	3,54	11,10
1.3	ΔСТУ 4747-2007	□ 40x10	3,51	1	3,14	11,02	3,51	11,02
1.4	ΔСТУ 4747-2007	□ 40x10	0,905	1	3,14	2,84	0,91	2,84
1.5	ΔСТУ 4747-2007	□ 40x10	0,07	1	3,14	0,22	0,07	0,22
1.6	ΔСТУ 4747-2007	□ 40x10	0,264	1	3,14	0,83	0,26	0,83
1.7	ΔСТУ 4747-2007	□ 40x10	0,455	1	3,14	1,43	0,46	1,43
1.8	ΔСТУ 4747-2007	□ 40x10	0,244	1	3,14	0,77	0,24	0,77
1.9	ΔСТУ 4747-2007	□ 40x10	0,064	44	3,14	0,20	2,82	8,84
							56,03	175,95
2	ΔСТУ 4747-2007	□ 40x6	1,057	184	1,884	1,99	194,49	366,42
2.1	ΔСТУ 4747-2007	□ 40x6	1,03	13	1,884	1,94	13,39	25,23
2.2	ΔСТУ 4747-2007	□ 40x6	0,745	1	1,884	1,40	0,75	1,40
2.3	ΔСТУ 4747-2007	□ 40x6	1,165	3	1,884	2,19	3,50	6,58
2.4	ΔСТУ 4747-2007	□ 40x6	1,17	2	1,884	2,20	2,34	4,41
2.5	ΔСТУ 4747-2007	□ 40x6	1,15	1	1,884	2,17	1,15	2,17
2.6	ΔСТУ 4747-2007	□ 40x6	0,905	1	1,884	1,71	0,91	1,71
							216,51	407,91
Δ3/Δ3*	ΔСТУ 4747-2007	— 80x6	0,2	46	3,768	0,7536	9,20	34,67
							9,20	34,67
	Клеєвий анкер HIT-HY 170 500/2-EE +			88				
	Анкерна шпилька HAS-U 5.8 HDG M10x130			88				
	Анкер-шуруп HUS4-HF 10x150 (бетон)			4				
						ОГТ-5 1 шт.		

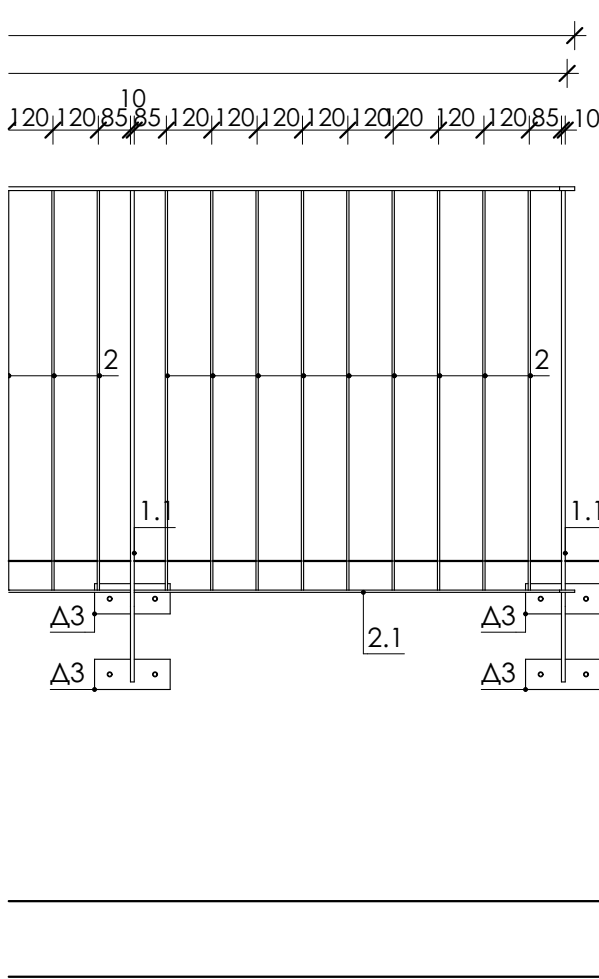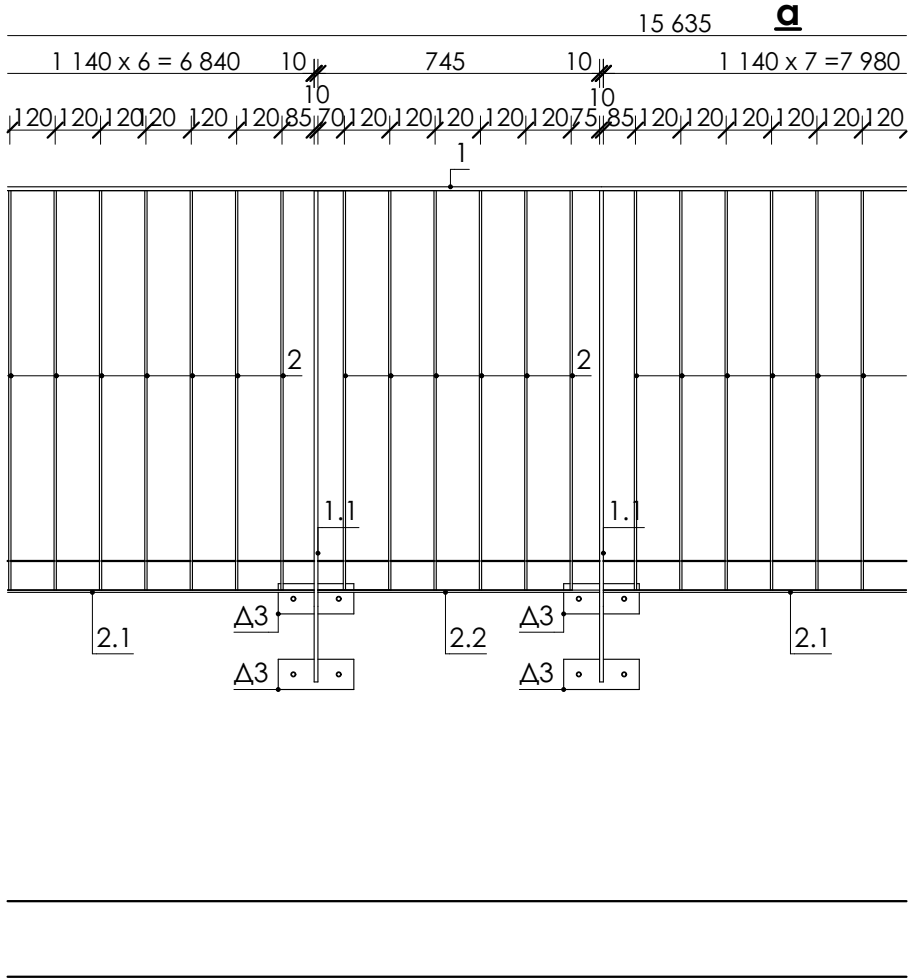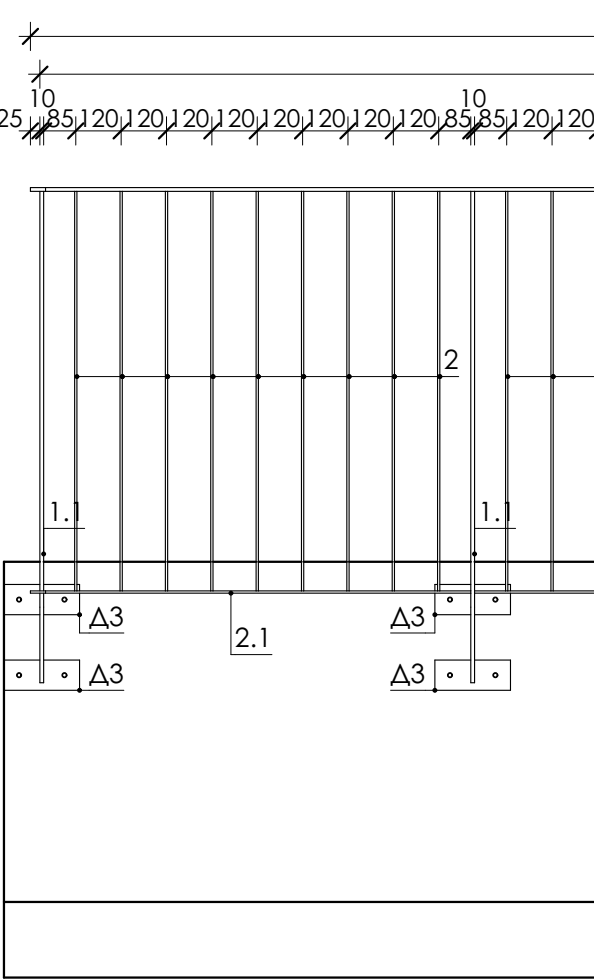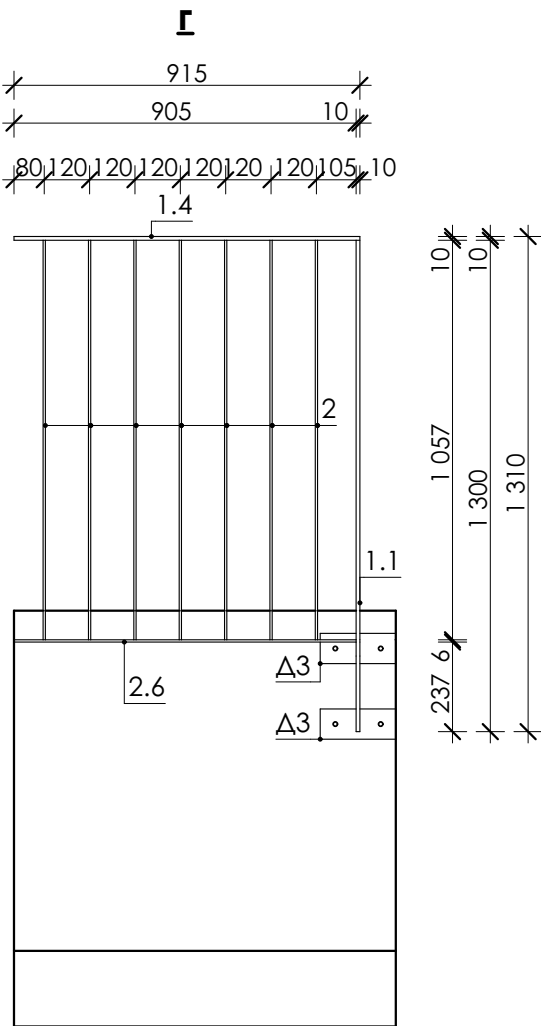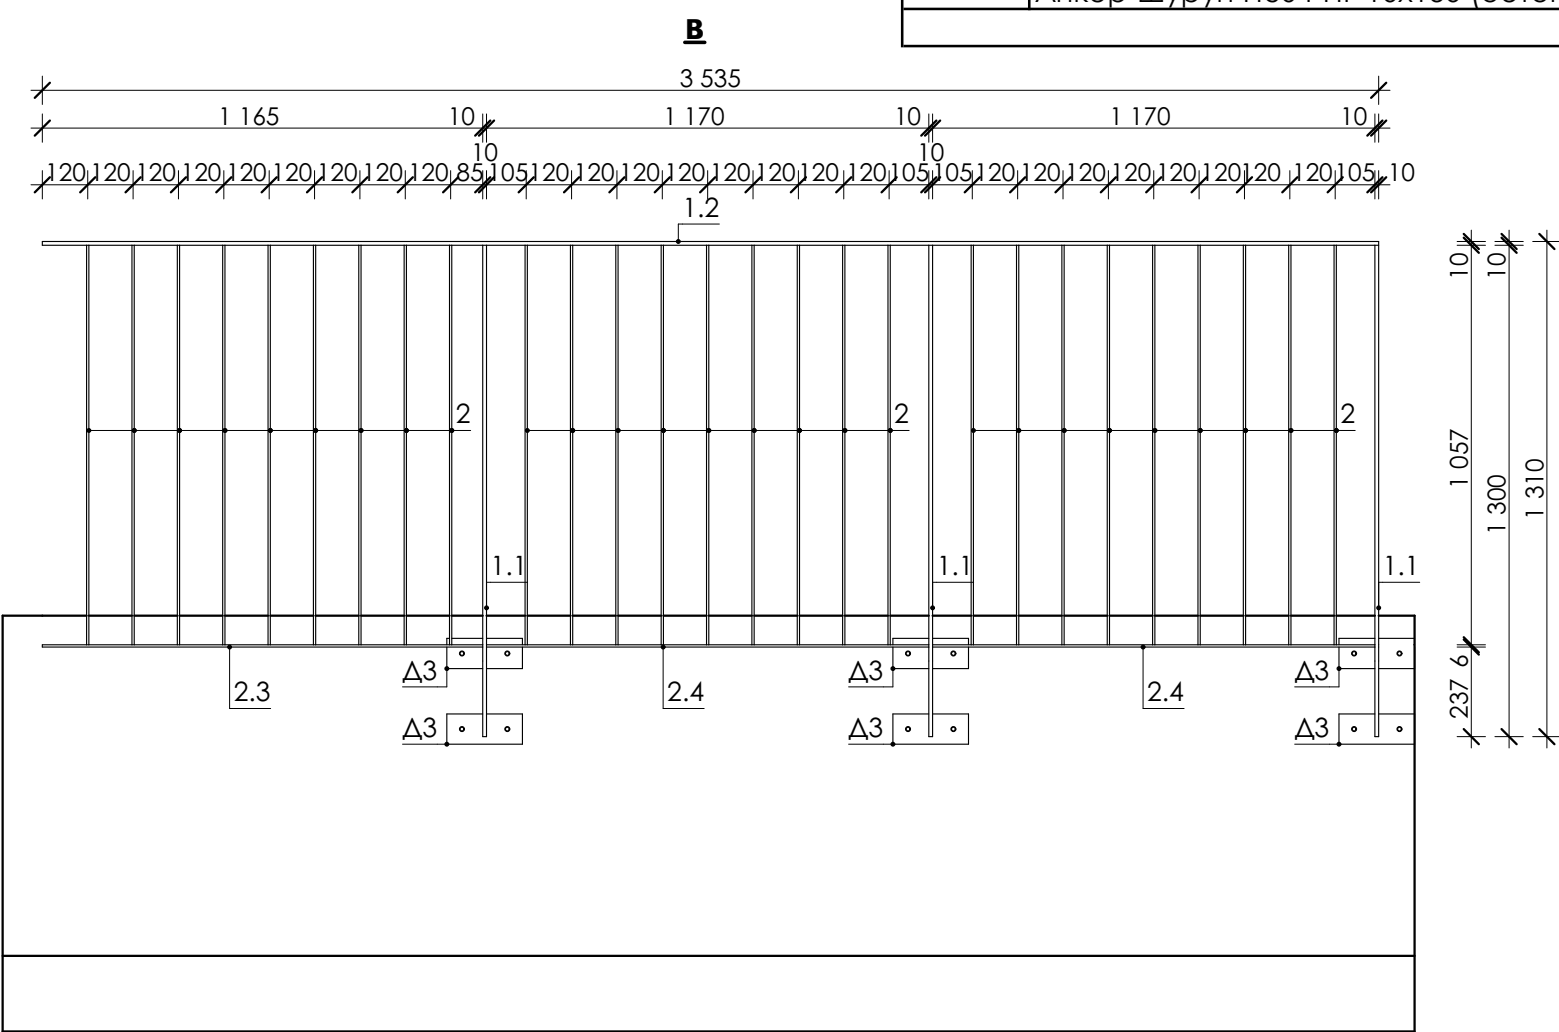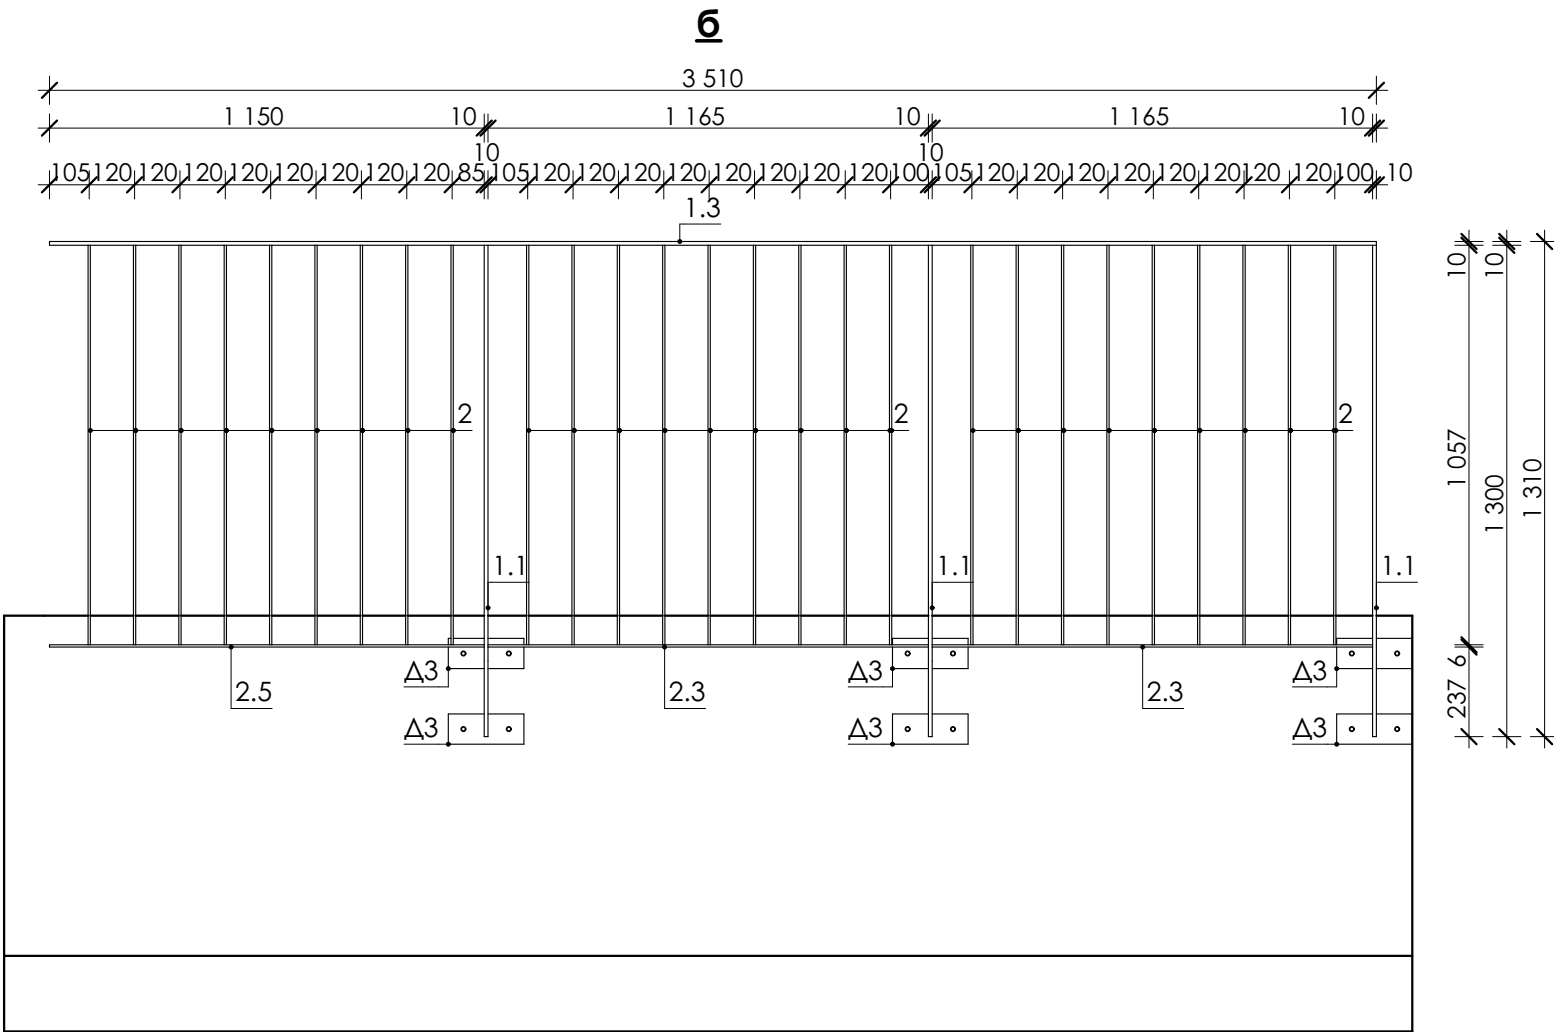



1-1

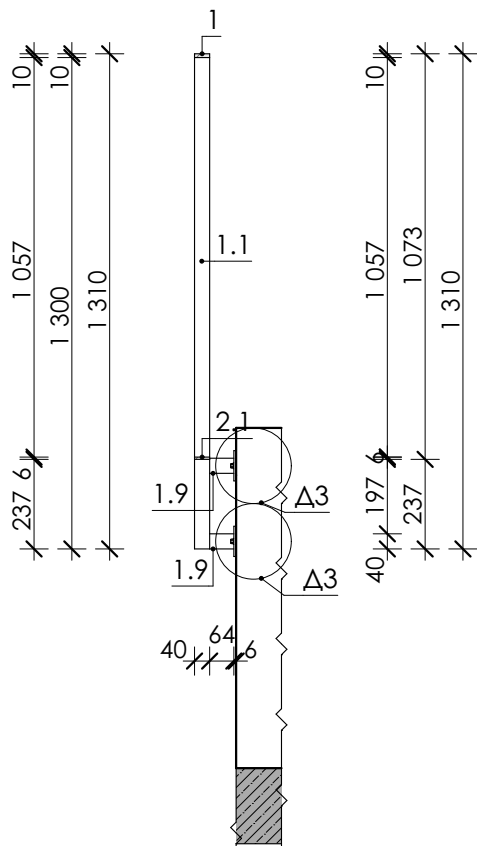

ОГТ-6

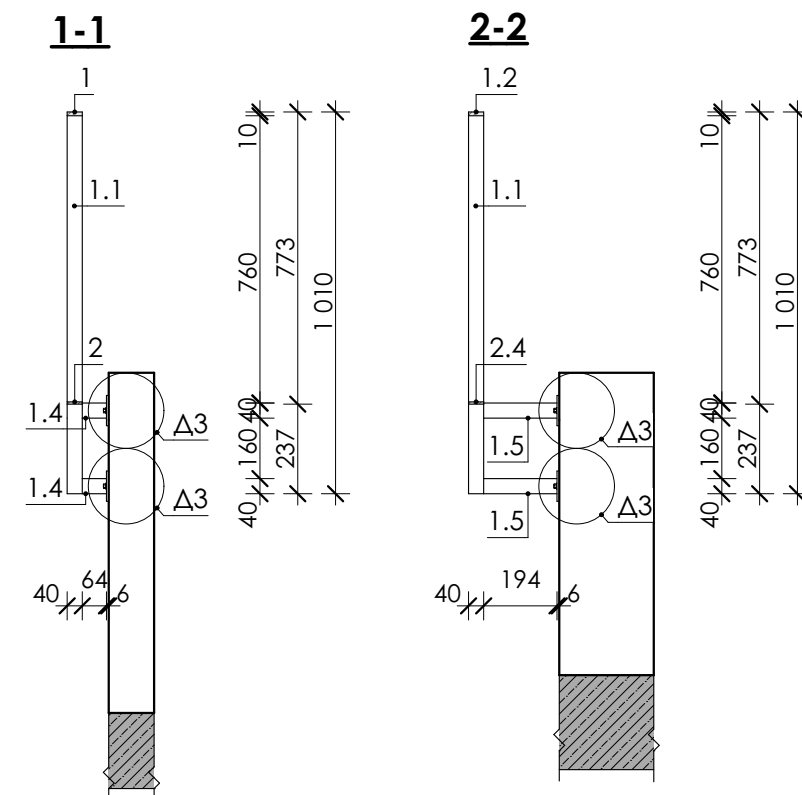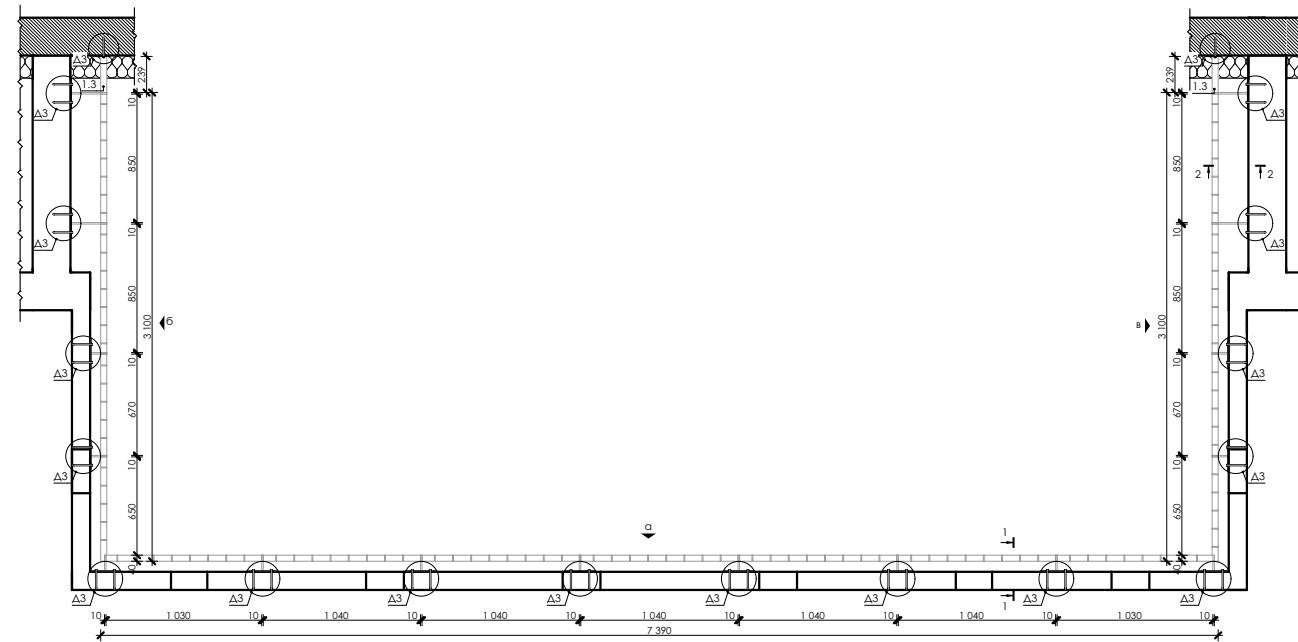

Марка поз.	Позначення	Найменування	L,м	K- СТЬ,ШТ	Маса l м.п.,кг	Маса од., кг	Загальн а L,м	Загальні витрати кг на 1шт.
ОГт-6								
1	ΔСТУ 4747-2007	□ 40x10	7,39	1	3,14	23,20	7,39	23,20
1.1	ΔСТУ 4747-2007	□ 40x10	1	16	3,14	3,14	16,00	50,24
1.2	ΔСТУ 4747-2007	□ 40x10	3,06	2	3,14	9,61	6,12	19,22
1.3	ΔСТУ 4747-2007	□ 40x10	0,239	2	3,14	0,75	0,48	1,50
1.4	ΔСТУ 4747-2007	□ 40x10	0,064	24	3,14	0,20	1,54	4,82
1.5	ΔСТУ 4747-2007	□ 40x10	0,194	8	3,14	0,61	1,55	4,87
							33,08	103,86
2	ΔСТУ 4747-2007	□ 40x6	1,04	5	1,884	1,96	5,20	9,80
2.1	ΔСТУ 4747-2007	□ 40x6	1,03	2	1,884	1,94	2,06	3,88
2.2	ΔСТУ 4747-2007	□ 40x6	0,757	104	1,884	1,43	78,73	148,32
2.3	ΔСТУ 4747-2007	□ 40x6	0,670	2	1,884	1,26	1,34	2,52
2.4	ΔСТУ 4747-2007	□ 40x6	0,65	2	1,884	1,22	1,30	2,45
2.5	ΔСТУ 4747-2007	□ 40x6	0,85	4	1,884	1,60	3,40	6,41
							92,03	173,38
ΔЗ	ΔСТУ 4747-2007	— 80x6	0,2	34	3,768	0,7536	6,80	25,62
							6,80	25,62
	Клеєвий анкер HIT-HY 170 500/2-EE +			68				
	Анкерна шпилька HAS-U 5.8 HDG M10x130			68				
ОГт-6							1 шт.	

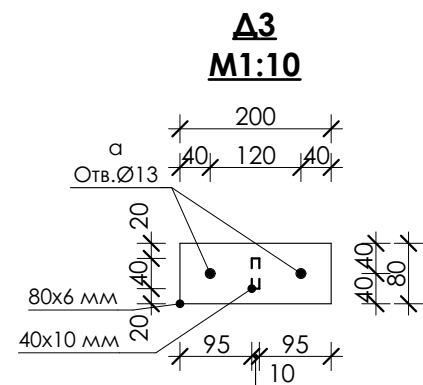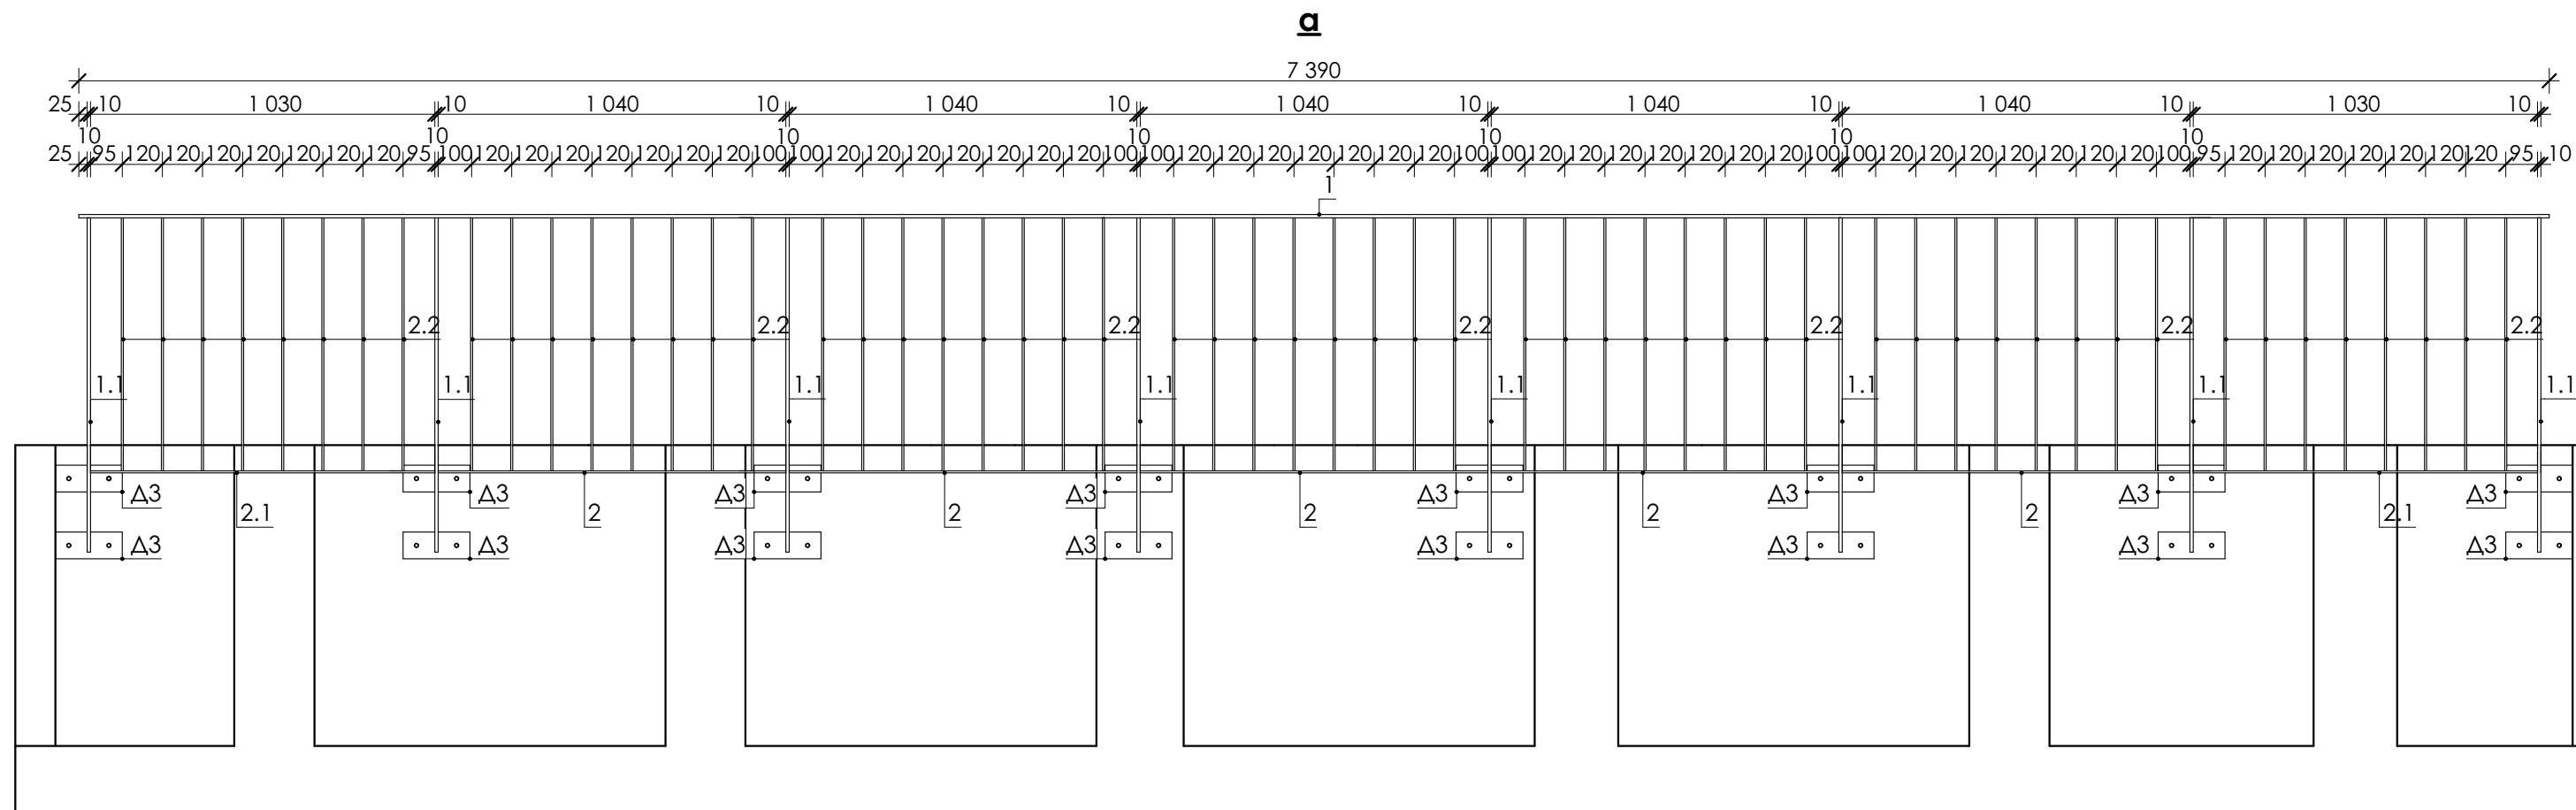

цегла повнотіла а - Клеєвий анкер НІТ-НУ 170 500/2-ЕЕ +
Анкерна шпилька HAS-U 5.8 HDG M10x130

