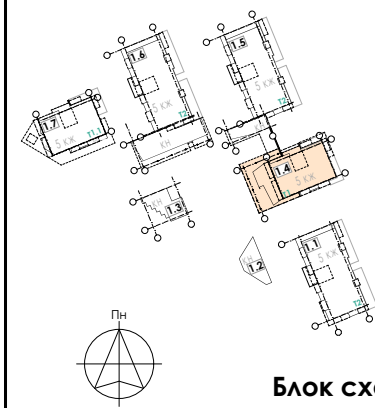
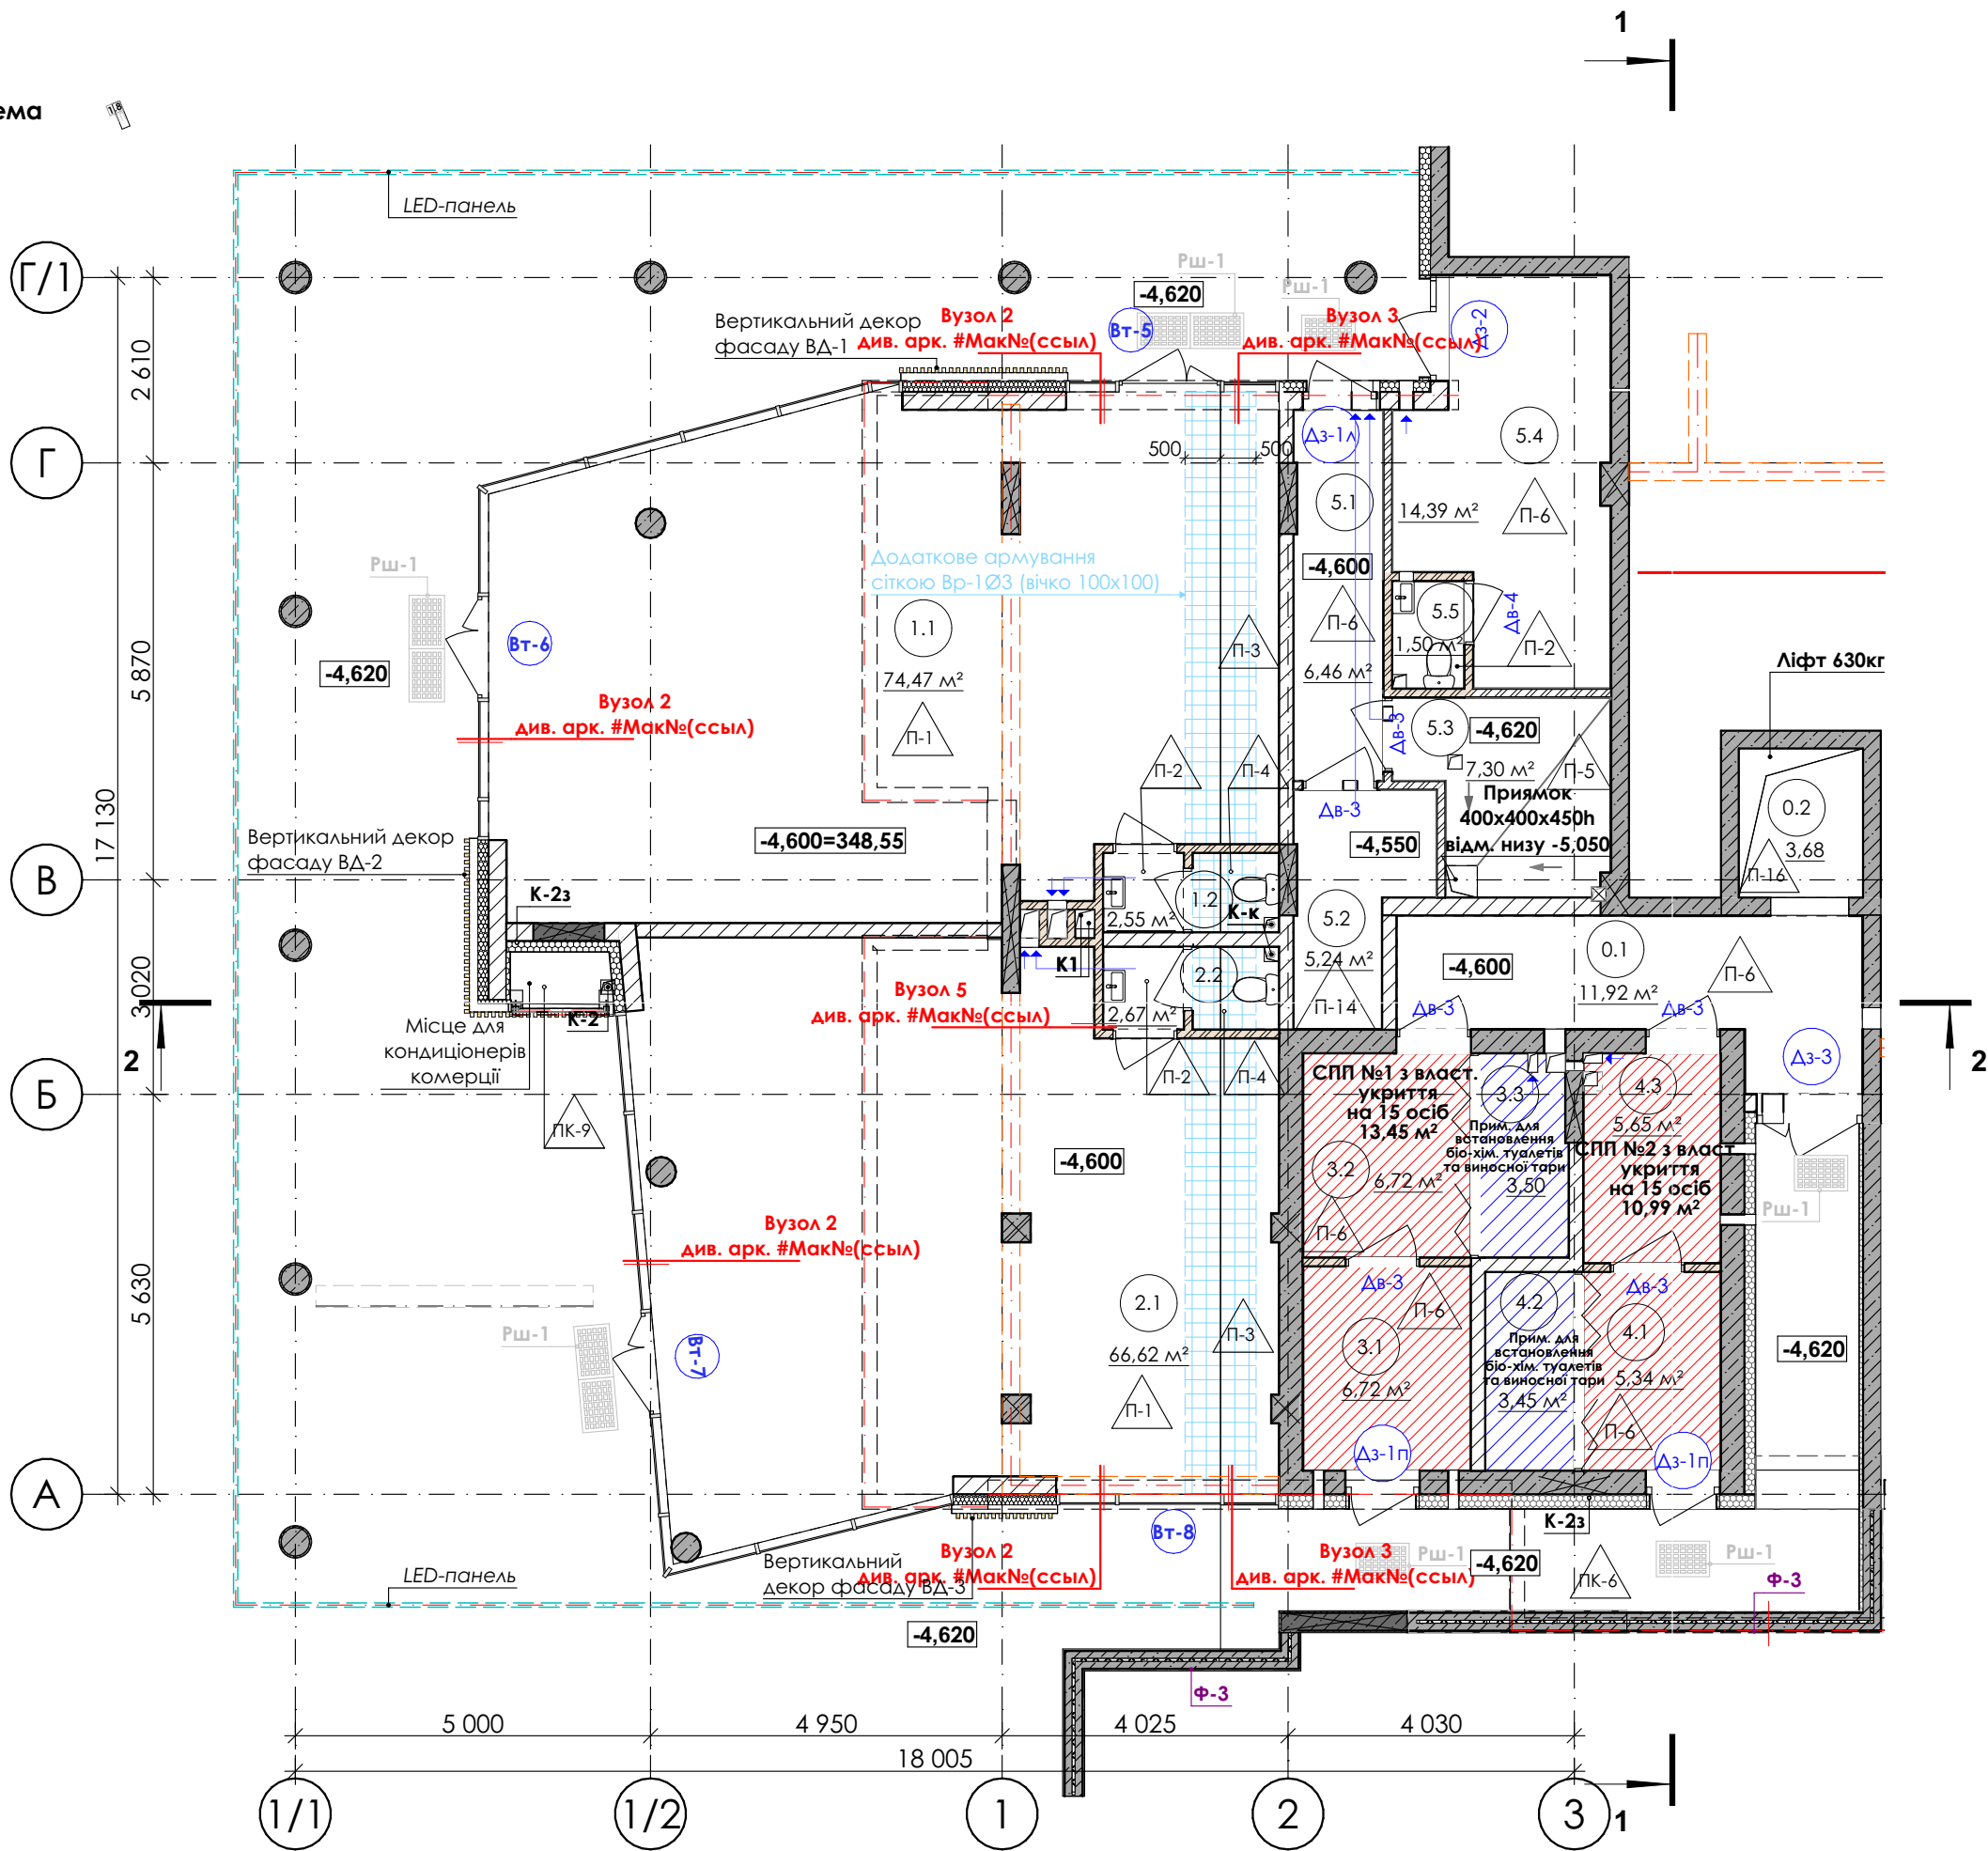




Маркувальний план цокольного поверху на відм. -4,600 М 1:100



УМОВНІ ПОЗНАЧЕННЯ

- зовнішня стіна (газоблок AEROC D400 - 250 мм, утеплювач мінвата 150 мм)
- внутрішня стіна (газоблок AEROC D500 - 200мм)
- залізобетонний пілон
- внутрішня перегородка, (цегла повнотіла -120 мм; утеплювач пінопласт - 20мм; цегла повнотіла -120 мм)
- внутрішня перегородка, (газоблок AEROC D500 - 75мм)
- внутрішня перегородка, (цегла повнотіла на ребро — 65 мм)
- вентиляційний канал
- колективний димовід
- каналізаційний стояк
- тип підлоги
- тип квартири
 - житлова площа квартири
 - площа приміщень квартири
 - загальна площа квартири
 - кількість кімнат
- підключення до вентиляційного каналу
- підключення до димового каналу
- підключення до К1
- К2 - каналізація дощова
- К1 - каналізація побутова
- +3,300 - відмітка рівня підлоги
- 16,44 - площа приміщення
- 2А.5 - номер приміщення
- Б6-1 - маркування балконних блоків,
- Δз-2 Δв-2 - Маркування зовнішніх/внутрішніх дверей
- Вк-1 ВТ-1 - маркування вікон/вітрин
- РА-2 РА-5 - маркування ревізійних дверцят
- Ф-1 - маркування фасонних елементів
- ОГ-1 - маркування огорожень
- МК-1 - маркування корзин для кондиціонера
- МЕ-1 - маркування екранів для кондиціонерів
- ПБ-1 - маркування балконних перегородок
- номер вузла
- Вузол 5 - вузли
- Див. арк. - номер аркуша
- Св-1 - стельові світильники балконів/лоджій/терас
- Додаткове армування сіткою Вр-1 Ø3 (вічко 100x100)


Тип	№ п.п.	Найменування	Площа	Прим.
0. Приміщення загального користування				
	0.1	Тамбур-шлюз 1-го типу	11,92	
	0.2	Ліфт 630 кг	3,68	
			15,60 м²	
1. Комерційне приміщення				
	1.1	Торгівельна зала	74,47	
	1.2	Санвузол	2,55	
			77,02 м²	
2. Комерційне приміщення				
	2.1	Торгівельна зала	66,62	
	2.2	Санвузол	2,67	
			69,29 м²	
3. Комори для мешканців будинку (СПП №1 з властивостями ПРУ)				
	3.1	Тамбур (комора для мешканців будинку)	6,72	
	3.2	Комора для мешканців будинку №2	6,72	
	3.3	Комора для мешканців будинку №1	3,50	
			16,94 м²	
4. Комори для мешканців будинку (СПП №2 з властивостями ПРУ)				
	4.1	Тамбур	5,34	
	4.2	Комора для мешканців будинку №3	3,45	
	4.3	Комора для мешканців будинку №4	5,65	
			14,44 м²	
5. Технічні приміщення				
	5.1	Коридор	6,46	
	5.2	Електроштова	5,24	
	5.3	Вузол вводу	7,30	
	5.4	Пожежний пост	14,39	
	5.5	Санвузол	1,50	
			34,89 м²	
			228,18 м²	

Додаткове армування підлоги цокольного поверху
Додаткове армування сіткою Вр-1 Ø3 (вічко 100x100) 14,87

Специфікація світильників		
Марка	Довжина, мм	Примітки
LED-панель	51 340	

Специфікація брудодісних решіток					
Марка трапа	Найменування	Вигляд	Розміри, мм	Кількість	Виробник
Рш-1	Брудодісна решітка		750x500	10	ACO Vario
					Алюмінієва з гумовим покриттям

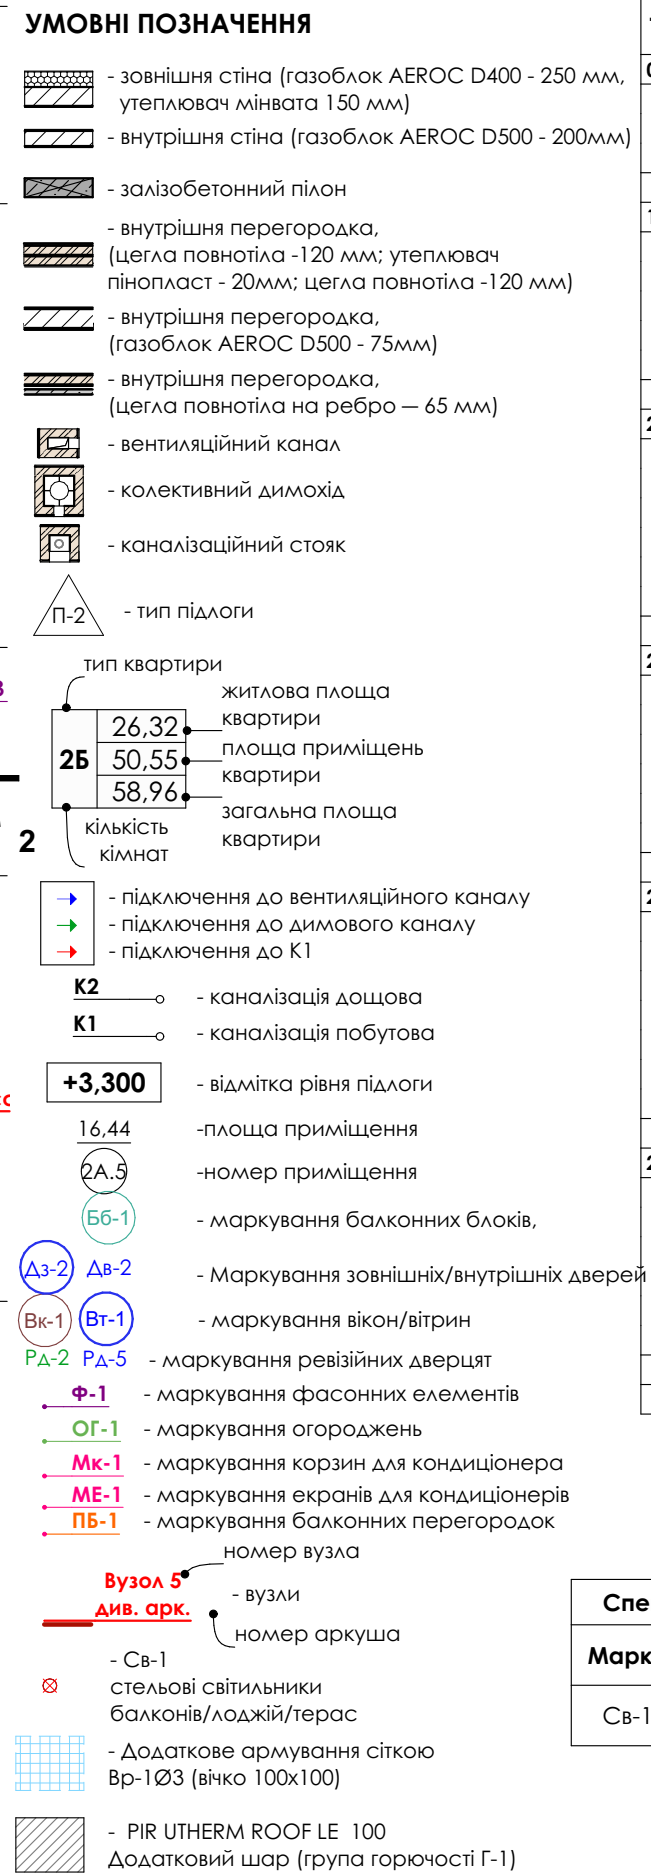Блок с/х




Специфікація балконних світильників СВ-1 1 поверх			
Марка	Найменування	Кількість	Примітки
СВ-1	Світильник стельовий, круглий	7	

Зведена специфікація балконних світильників СВ-1			
Марка	Найменування	Кількість	Примітки
СВ-1	Світильник стельовий, круглий	34	

Армування сіткою Вр-1Ø3 (вічко 100x100) -	16,30
---	-------

Специфікація водоприймальних воронок 1-го поверху						
Марка	Найменування		Кількість	Примітки		
Вр-1	Водоприймальна воронка з підігрівом		1	див. розділ ВК		
Специфікація трапів 1-го поверху						
Марка трапа	Найменування	Вигляд	Розміри, мм	Кількість	Виробник	Примітки
Тр-1	Трап горизонтальний		100x100 h=50	4	Valrom	див. розділ ВК
Зведена специфікація трапів Тр-1						
Марка трапа	Найменування	Вигляд	Розміри, мм	Кількість	Виробник	Примітки
Тр-1	Трап горизонтальний		100x100 h=50	32	Valrom	див. розділ ВК

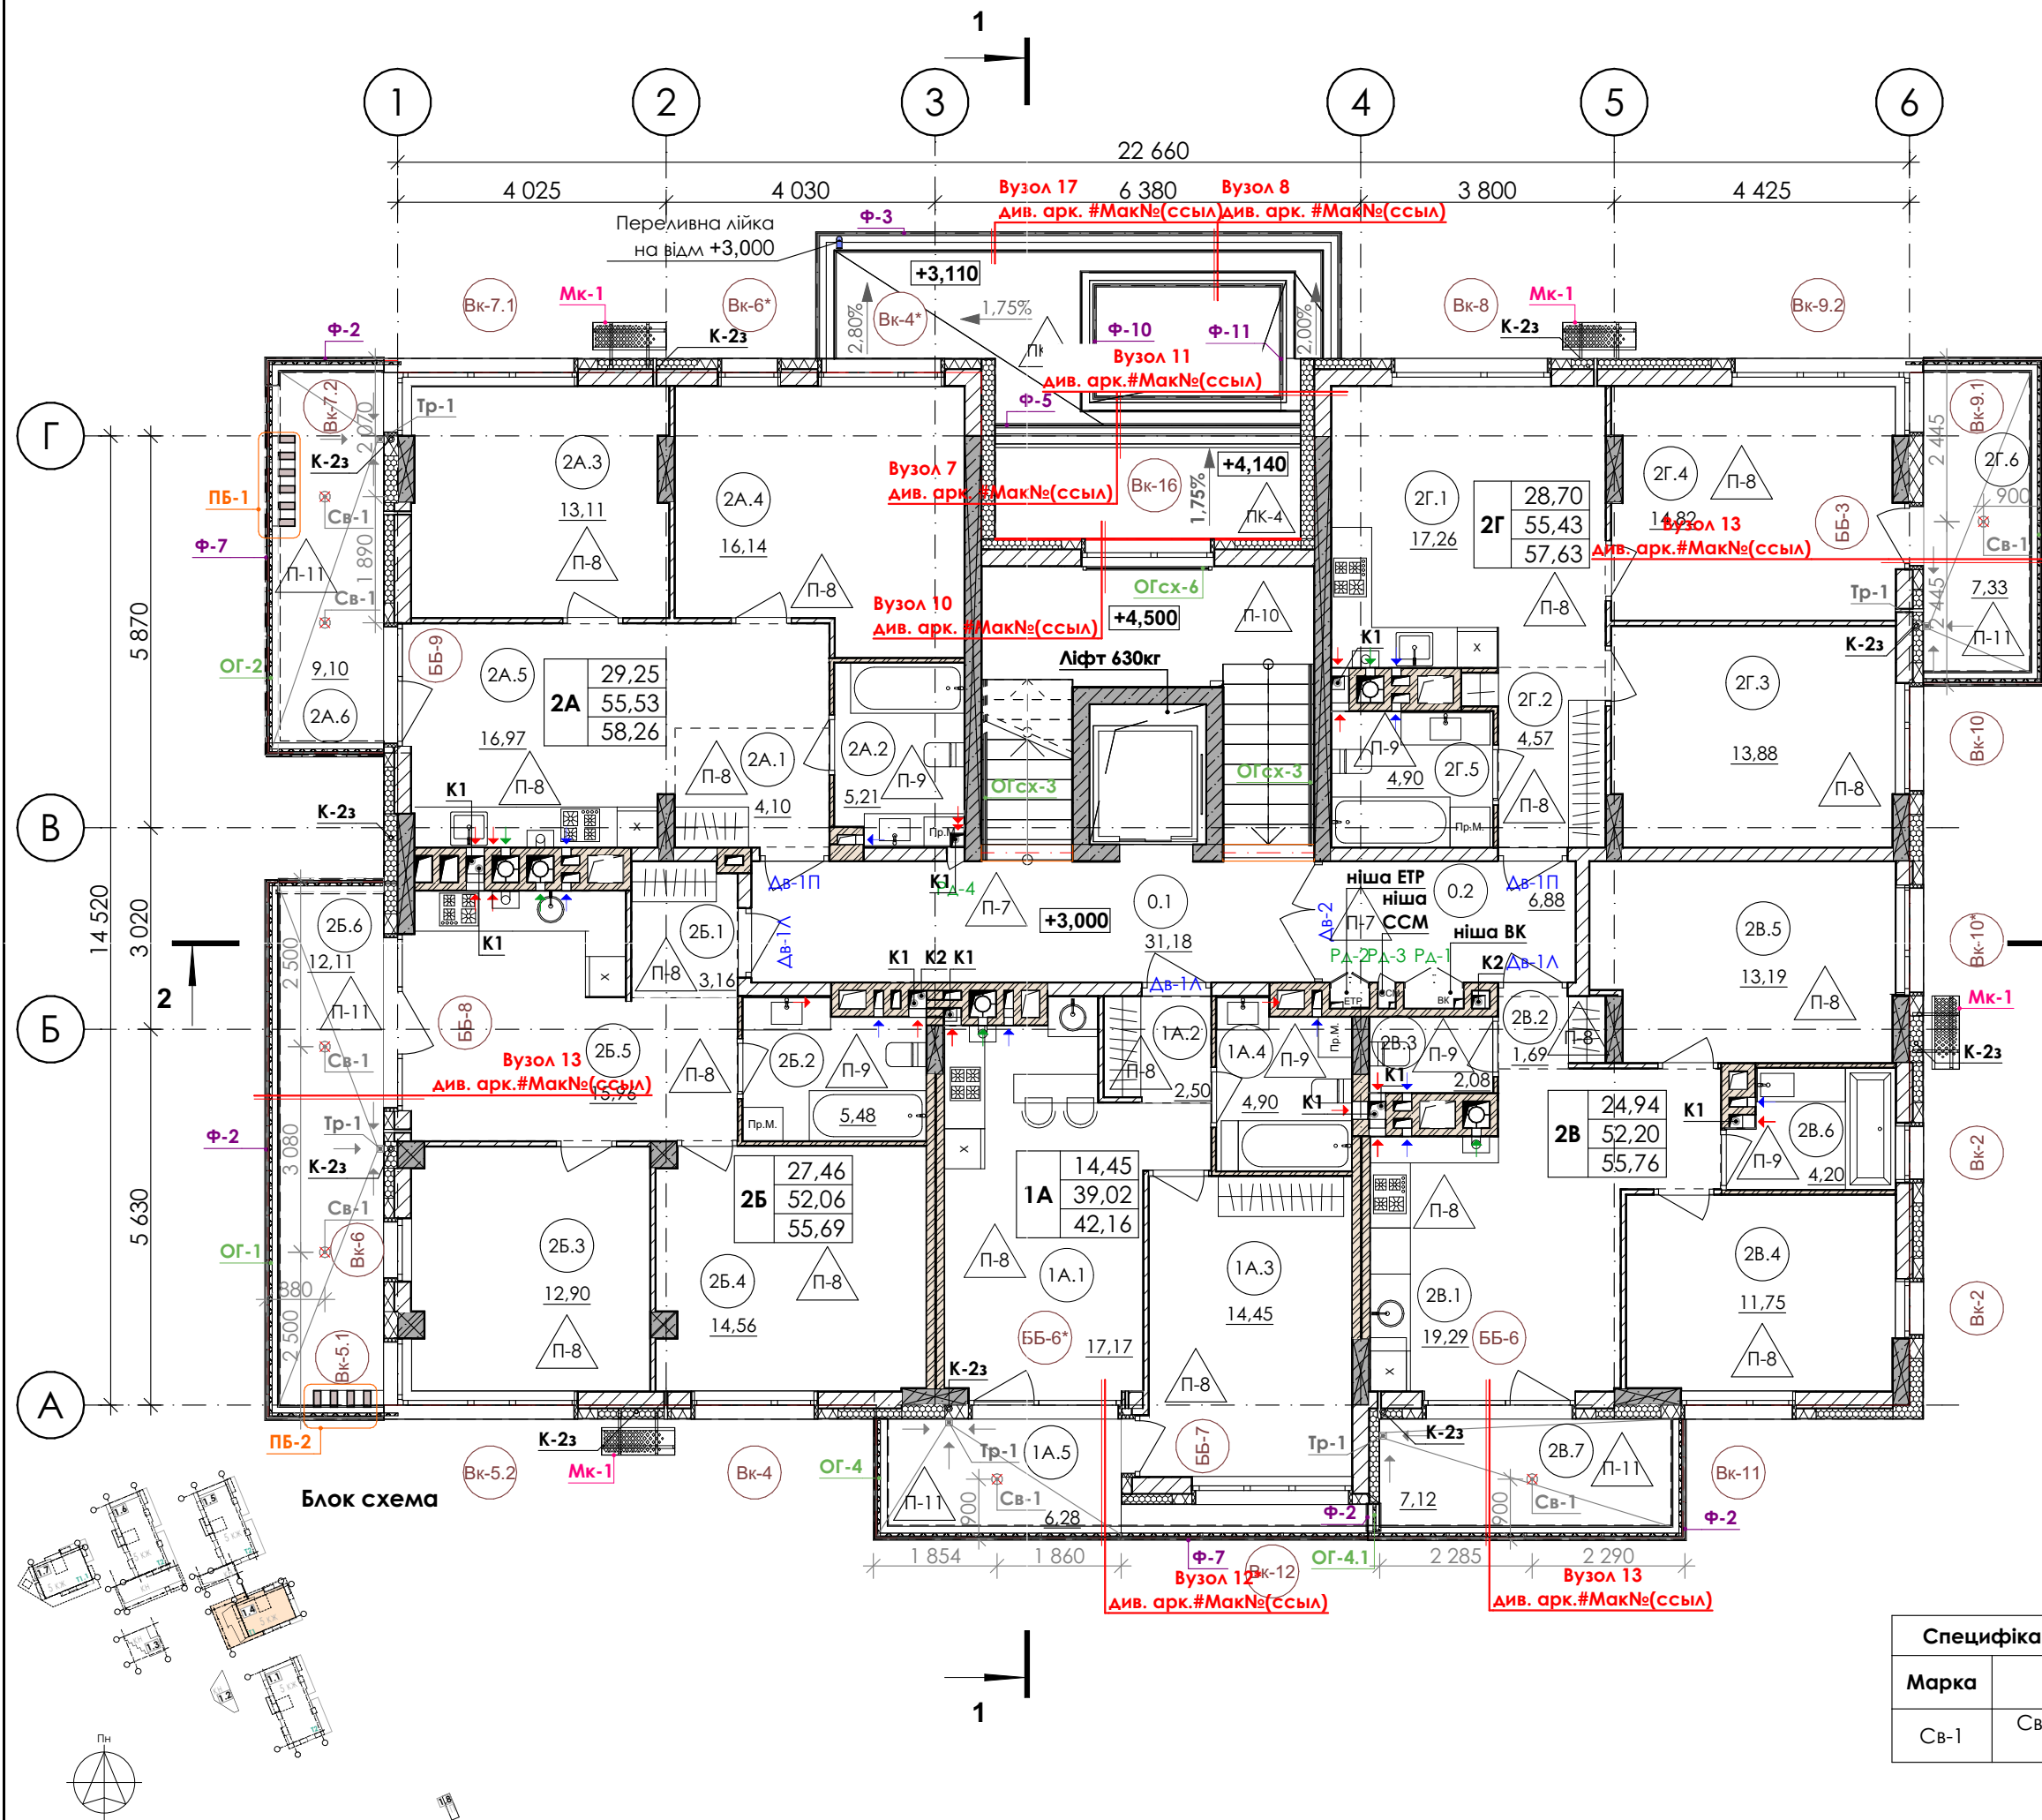Маркувальний план 2-го поверху на відм. +3,000 М 1:100



УМОВНІ ПОЗНАЧЕННЯ

- зовнішня стіна (газоблок AEROC D400 - 250 мм, утеплювач мінівата 150 мм)
- внутрішня стіна (газоблок AEROC D500 - 200мм)
- залізобетонний пілон
- внутрішня перегородка, (цегла повнотіла -120 мм; утеплювач пінопласт - 20мм; цегла повнотіла -120 мм)
- внутрішня перегородка, (газоблок AEROC D500 - 75мм)
- внутрішня перегородка, (цегла повнотіла на ребро — 65 мм)
- вентиляційний канал
- колективний димохід
- каналізаційний стояк
- тип підлоги
- тип квартири
 - житлова площа квартири
 - площа приміщень квартири
 - загальна площа квартири
 - кількість кімнат
- підключення до вентиляційного каналу
- підключення до димового каналу
- підключення до К1
- K2 - каналізація дощова
- K1 - каналізація побутова
- +3,300 - відмітка рівня підлоги
- 16,44 - площа приміщення
- 2A.5 - номер приміщення
- ББ-1 - маркування балконних блоків,
- ДЗ-2 ДВ-2 - Маркування зовнішніх/внутрішніх дверей
- ВК-1 ВТ-1 - маркування вікон/вітрин
- РА-2 РА-5 - маркування ревізійних дверцят
- Ф-1 - маркування фасонних елементів
- ОГ-1 - маркування огорожень
- МК-1 - маркування корзин для кондиціонера
- МЕ-1 - маркування екранів для кондиціонерів
- ПБ-1 - маркування балконних перегородок
- номер вузла
- Вузол 5 - вузли
- Див. арк. - номер аркуша
- Св-1 - стельові світильники балконів/лоджій/терас


Специфікація балконних світильників СВ-1 2 поверх			
Марка	Найменування	Кількість	Примітки
Св-1	Світильник стельовий, круглий	7	

Тип	№ п.п.	Найменування	Площа	Прим.
0. Приміщення загального користування				
	0.1	Сходово-клітка СК 1	31,18	
	0.2	Коридор	6,88	
			38,06 м²	
1А				
	1А.1	Кухня-їдальня	17,17	
	1А.2	Передпокій	2,50	
	1А.3	Спальня	14,45	
	1А.4	Суміщений санвузол	4,90	
	1А.5	Лоджія	3,14	
			42,16 м²	
2А				
	2А.1	Передпокій	4,10	
	2А.2	Суміщений санвузол	5,21	
	2А.3	Спальня	13,11	
	2А.4	Спальня	16,14	
	2А.5	Кухня-їдальня	16,97	
	2А.6	Балкон	2,73	
			58,26 м²	
2Б				
	2Б.1	Передпокій	3,16	
	2Б.2	Суміщений санвузол	5,48	
	2Б.3	Спальня	12,90	
			57,63 м²	

Тип	№ п.п.	Найменування	Площа	Прим.
2В				
	2В.4	Спальня	14,56	
	2В.5	Кухня-їдальня	15,96	
	2В.6	Балкон	3,63	
			55,69 м²	
2Г				
	2Г.1	Кухня-їдальня	19,29	
	2Г.2	Передпокій	1,69	
	2Г.3	Санвузол	2,08	
	2Г.4	Спальня	11,75	
	2Г.5	Спальня	13,19	
	2Г.6	Ванна	4,20	
	2Г.7	Лоджія	3,56	
			55,76 м²	
2Г				
	2Г.1	Кухня-їдальня	17,26	
	2Г.2	Передпокій	4,57	
	2Г.3	Спальня	13,88	
	2Г.4	Спальня	14,82	
	2Г.5	Суміщений санвузол	4,90	
	2Г.6	Балкон	2,20	
			57,63 м²	
			307,56 м²	

Специфікація трапів 2-го поверху						
Марка трапа	Найменування	Вигляд	Розміри, мм	Кількість	Виробник	Примітки
Тр-1	Трап горизонтальний		100x100 h=50	5	Valrom	див. розділ ВК

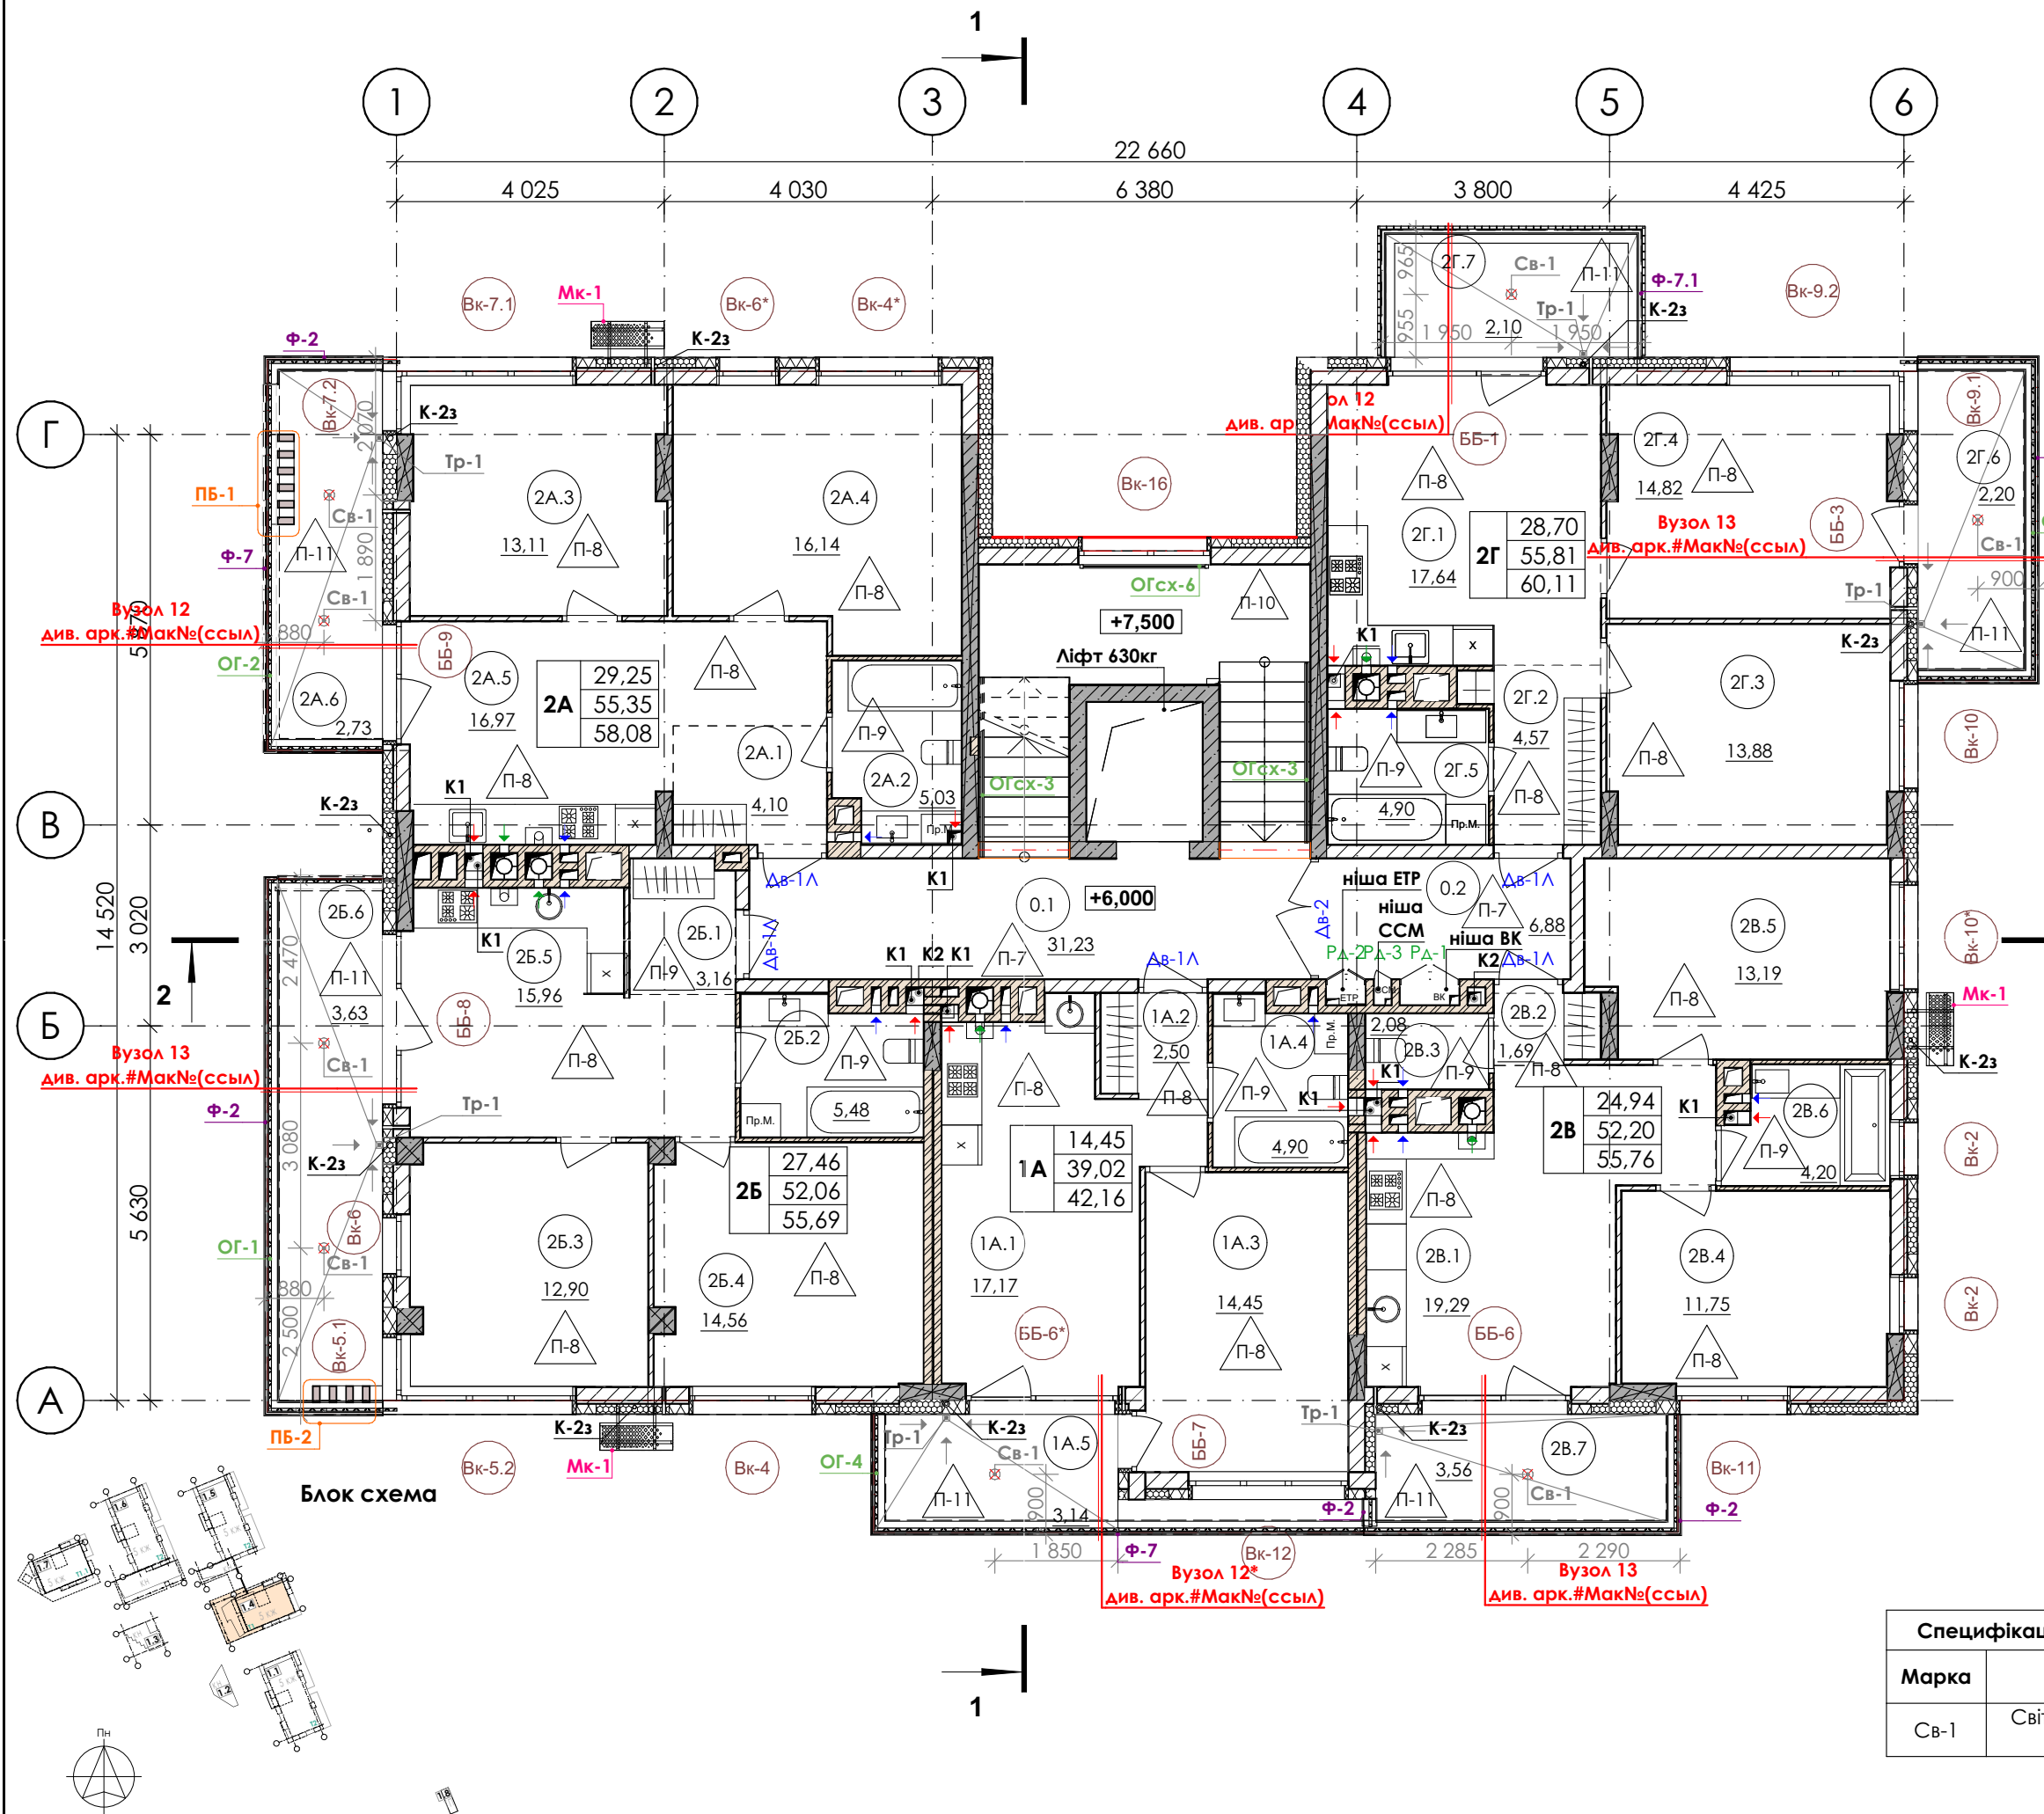Маркувальний план 3 поверху на відм. +6,000; М 1:100



УМОВНІ ПОЗНАЧЕННЯ

- зовнішня стіна (газоблок AEROC D400 - 250 мм, утеплювач мінвата 150 мм)
- внутрішня стіна (газоблок AEROC D500 - 200мм)
- залізобетонний пілон
- внутрішня перегородка, (цегла повнотіла -120 мм; утеплювач пінопласт - 20мм; цегла повнотіла -120 мм)
- внутрішня перегородка, (газоблок AEROC D500 - 75мм)
- внутрішня перегородка, (цегла повнотіла на ребро — 65 мм)
- вентиляційний канал
- колективний димохід
- каналізаційний стояк
- тип підлоги
- тип квартири
 - житлова площа квартири
 - площа приміщень квартири
 - загальна площа квартири
 - кількість кімнат
- підключення до вентиляційного каналу
- підключення до димового каналу
- підключення до К1
- К2 - каналізація дощова
- К1 - каналізація побутова
- відмітка рівня підлоги
- площа приміщення
- номер приміщення
- маркування балконних блоків,
- Маркування зовнішніх/внутрішніх дверей
- маркування вікон/вітрин
- маркування ревізійних дверцят
- маркування фасонних елементів
- маркування огорожень
- маркування корзин для кондиціонера
- маркування екранів для кондиціонерів
- маркування балконних перегородок
- номер вузла
- вузли
- номер аркуша
- Св-1
- стельові світильники балконів/лоджій/терас


Специфікація балконних світильників СВ-1 3 поверх			
Марка	Найменування	Кількість	Примітки
Св-1	Світильник стельовий, круглий	8	

Тип	№ п.п.	Найменування	Площа	Прим.
0. Приміщення загального користування				
	0.1	Сходово-клітка СК 1	31,23	
	0.2	Коридор	6,88	
			38,11 м²	
1А				
	1А.1	Кухня-їдальня	17,17	
	1А.2	Передпокій	2,50	
	1А.3	Спальня	14,45	
	1А.4	Суміщений санвузол	4,90	
	1А.5	Лоджія	3,14	
			42,16 м²	
2А				
	2А.1	Передпокій	4,10	
	2А.2	Суміщений санвузол	5,03	
	2А.3	Спальня	13,11	
	2А.4	Спальня	16,14	
	2А.5	Кухня-їдальня	16,97	
	2А.6	Балкон	2,73	
			58,08 м²	
2Б				
	2Б.1	Передпокій	3,16	
	2Б.2	Суміщений санвузол	5,48	
	2Б.3	Спальня	12,90	

Тип	№ п.п.	Найменування	Площа	Прим.
2В				
	2В.4	Спальня	14,56	
	2В.5	Кухня-їдальня	15,96	
	2В.6	Балкон	3,63	
			55,69 м²	
2Г				
	2Г.1	Кухня-їдальня	19,29	
	2Г.2	Передпокій	1,69	
	2Г.3	Санвузол	2,08	
	2Г.4	Спальня	11,75	
	2Г.5	Спальня	13,19	
	2Г.6	Ванна	4,20	
	2Г.7	Лоджія	3,56	
			55,76 м²	
2Г				
	2Г.1	Кухня-їдальня	17,64	
	2Г.2	Передпокій	4,57	
	2Г.3	Спальня	13,88	
	2Г.4	Спальня	14,82	
	2Г.5	Суміщений санвузол	4,90	
	2Г.6	Балкон	2,20	
	2Г.7	Балкон	2,10	
			60,11 м²	
			309,91 м²	

Специфікація трапів 3-го поверху						
Марка трапа	Найменування	Вигляд	Розміри, мм	Кількість	Виробник	Примітки
Тр-1	Трап горизонтальний		100x100 h=50	6	Valrom	див. розділ ВК

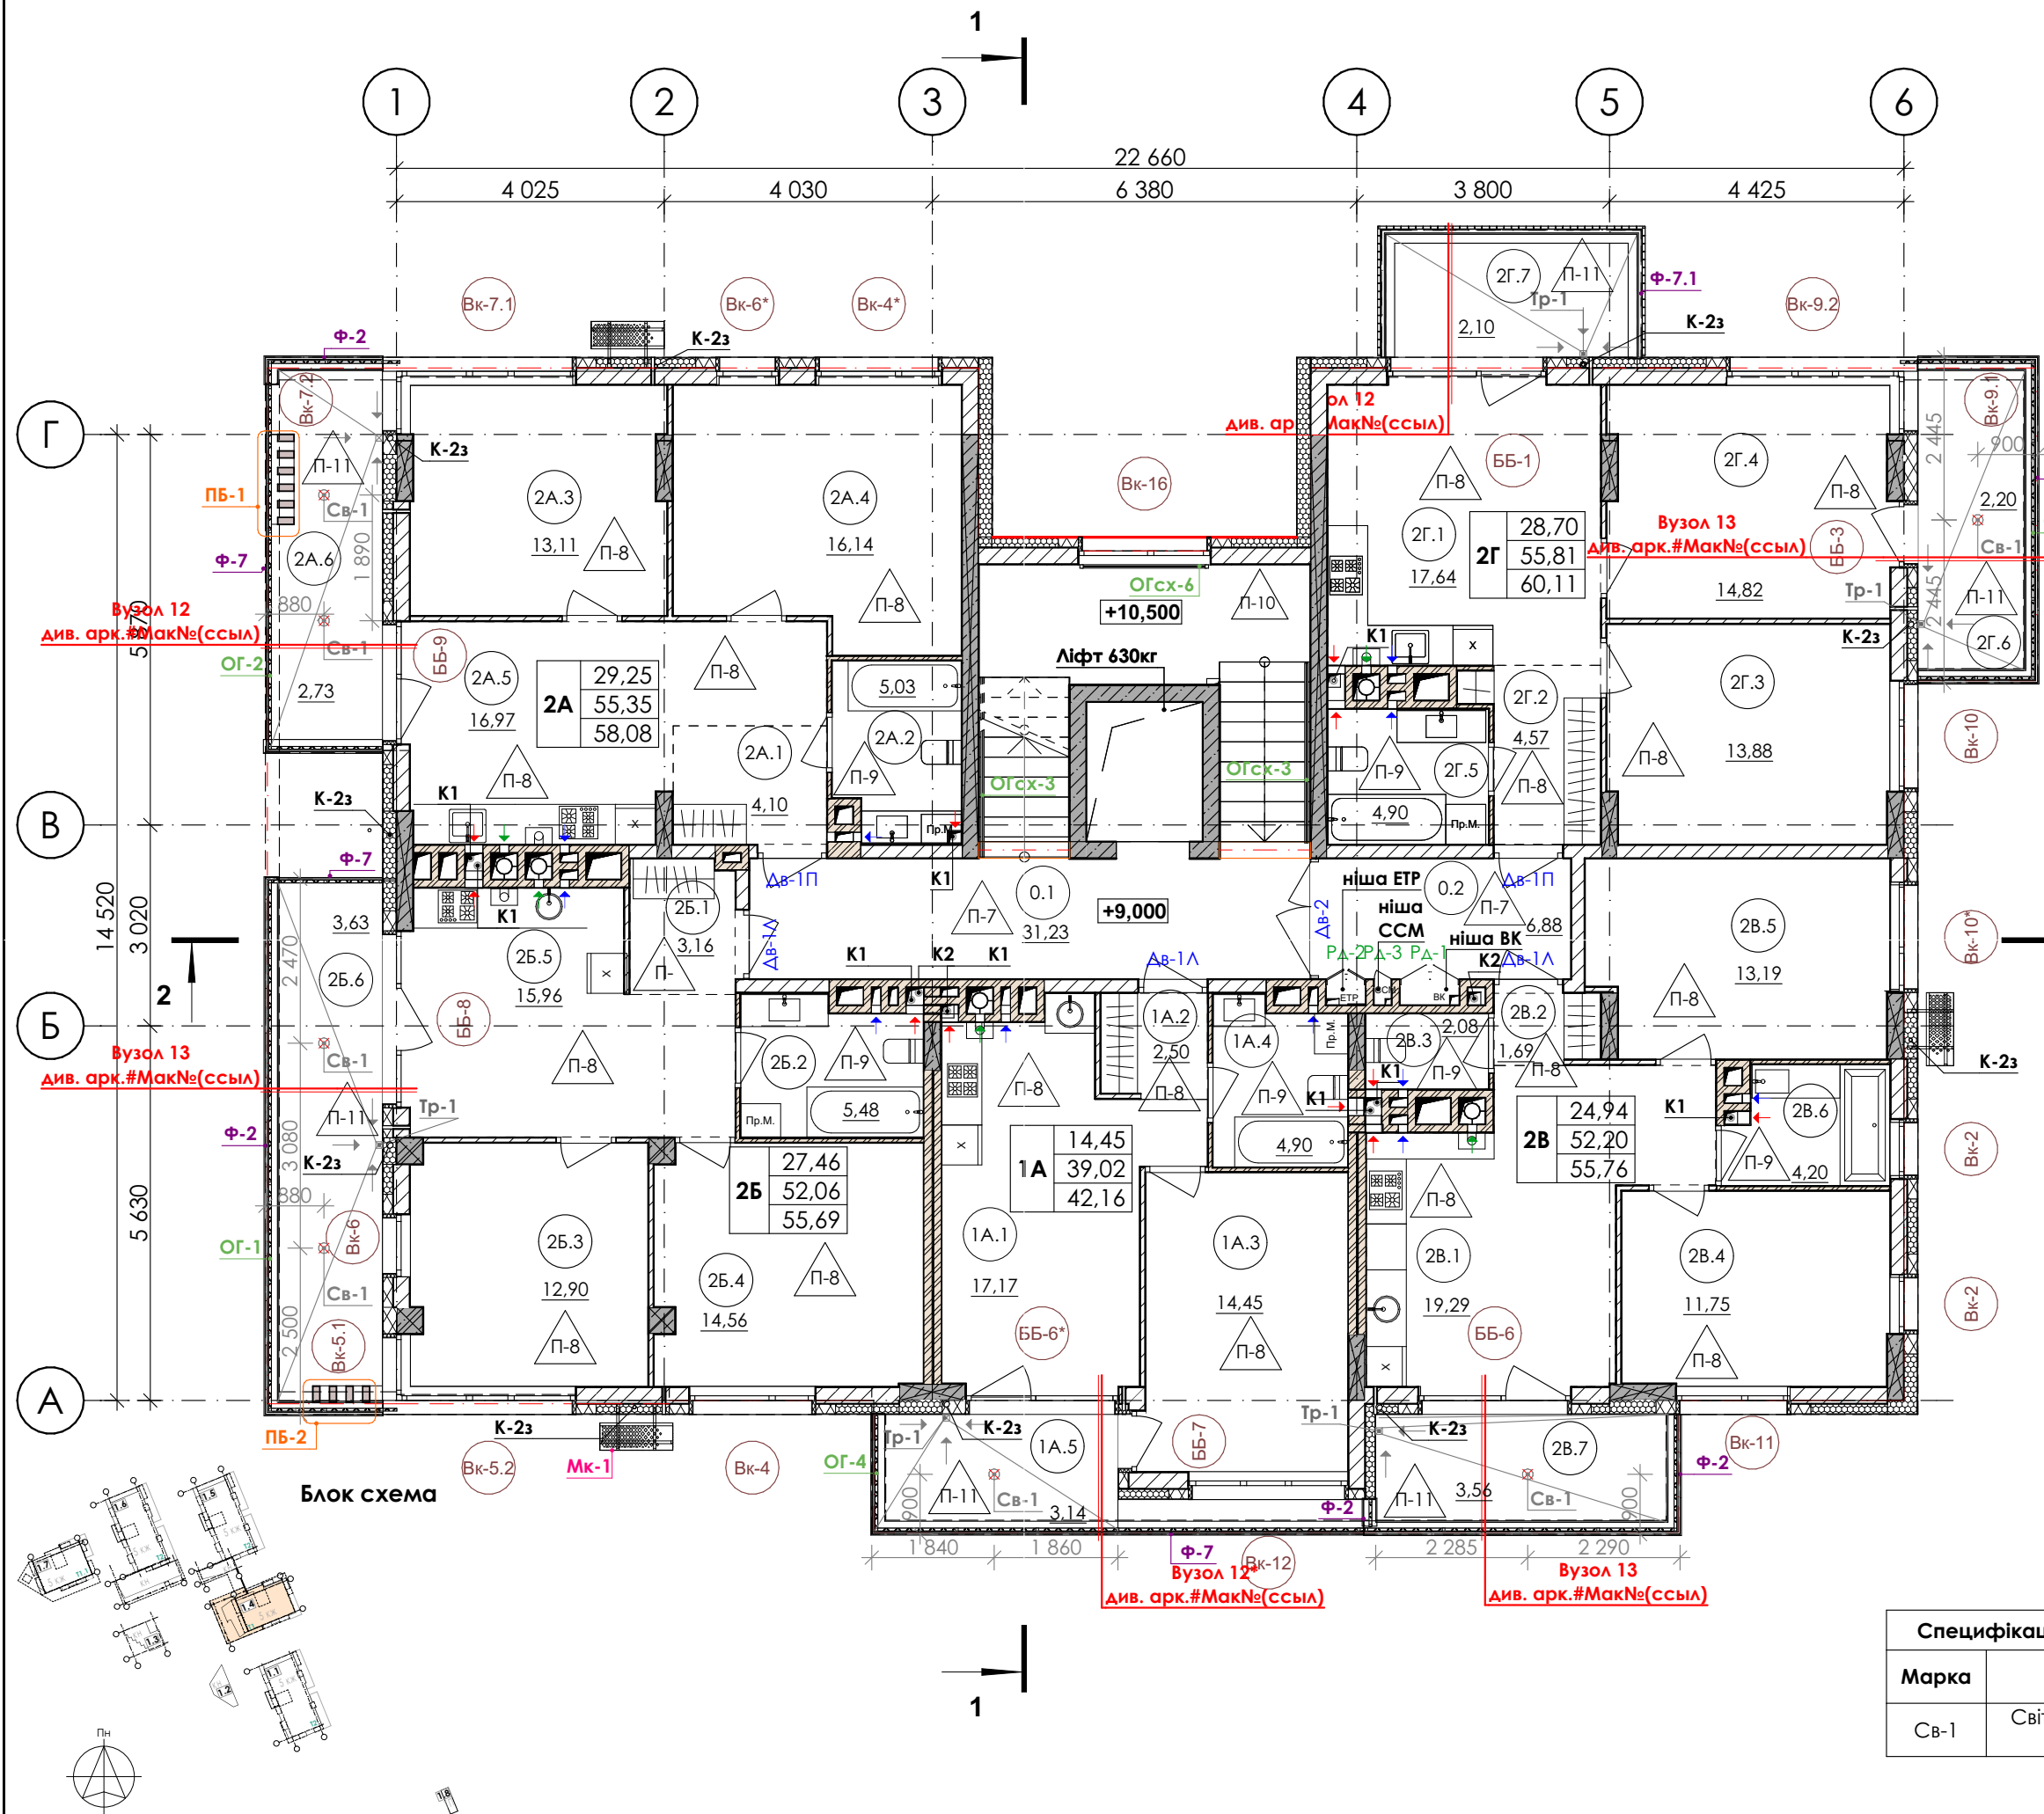Маркувальний план 4 поверху на відм. +9,000 М 1:100



УМОВНІ ПОЗНАЧЕННЯ

- зовнішня стіна (газоблок AEROC D400 - 250 мм, утеплювач мінівата 150 мм)
- внутрішня стіна (газоблок AEROC D500 - 200мм)
- залізобетонний пілон
- внутрішня перегородка, (цегла повнотіла -120 мм; утеплювач пінопласт - 20мм; цегла повнотіла -120 мм)
- внутрішня перегородка, (газоблок AEROC D500 - 75мм)
- внутрішня перегородка, (цегла повнотіла на ребро — 65 мм)
- вентиляційний канал
- колективний димохід
- каналізаційний стояк
- тип підлоги
- тип квартири
 - житлова площа квартири
 - площа приміщень квартири
 - загальна площа квартири
 - кількість кімнат
- підключення до вентиляційного каналу
- підключення до димового каналу
- підключення до К1
- K2 - каналізація дощова
- K1 - каналізація побутова
- відмітка рівня підлоги
- площа приміщення
- номер приміщення
- маркування балконних блоків,
- Маркування зовнішніх/внутрішніх дверей
- маркування вікон/вітрин
- маркування ревізійних дверцят
- маркування фасонних елементів
- маркування огорожень
- маркування корзин для кондиціонерів
- маркування екранів для кондиціонерів
- маркування балконних перегородок
- номер вузла
- вузли
- номер аркуша
- Св-1
- стельові світильники балконів/лоджій/терас


Специфікація балконних світильників Св-1 4 поверх			
Марка	Найменування	Кількість	Примітки
Св-1	Світильник стельовий, круглий	7	

Тип	№ п.п.	Найменування	Площа	Прим.
0. Приміщення загального користування				
	0.1	Сходово-клітка СК 1	31,23	
	0.2	Коридор	6,88	
			38,11 м²	
1А				
	1А.1	Кухня-їдальня	17,17	
	1А.2	Передпокій	2,50	
	1А.3	Спальня	14,45	
	1А.4	Суміщений санвузол	4,90	
	1А.5	Лоджія	3,14	
			42,16 м²	
2А				
	2А.1	Передпокій	4,10	
	2А.2	Суміщений санвузол	5,03	
	2А.3	Спальня	13,11	
	2А.4	Спальня	16,14	
	2А.5	Кухня-їдальня	16,97	
	2А.6	Балкон	2,73	
			58,08 м²	
2Б				
	2Б.1	Передпокій	3,16	
	2Б.2	Суміщений санвузол	5,48	
	2Б.3	Спальня	12,90	

Тип	№ п.п.	Найменування	Площа	Прим.
	2Б.4	Спальня	14,56	
	2Б.5	Кухня-їдальня	15,96	
	2Б.6	Балкон	3,63	
			55,69 м²	
2В				
	2В.1	Кухня-їдальня	19,29	
	2В.2	Передпокій	1,69	
	2В.3	Санвузол	2,08	
	2В.4	Спальня	11,75	
	2В.5	Спальня	13,19	
	2В.6	Ванна	4,20	
	2В.7	Лоджія	3,56	
			55,76 м²	
2Г				
	2Г.1	Кухня-їдальня	17,64	
	2Г.2	Передпокій	4,57	
	2Г.3	Спальня	13,88	
	2Г.4	Спальня	14,82	
	2Г.5	Суміщений санвузол	4,90	
	2Г.6	Балкон	2,20	
	2Г.7	Балкон	2,10	
			60,11 м²	
			309,91 м²	

Специфікація трапів 4-го поверху						
Марка трапа	Найменування	Вигляд	Розміри, мм	Кількість	Виробник	Примітки
Тр-1	Трап горизонтальний		100x100 h=50	6	Valrom	див. розділ ВК

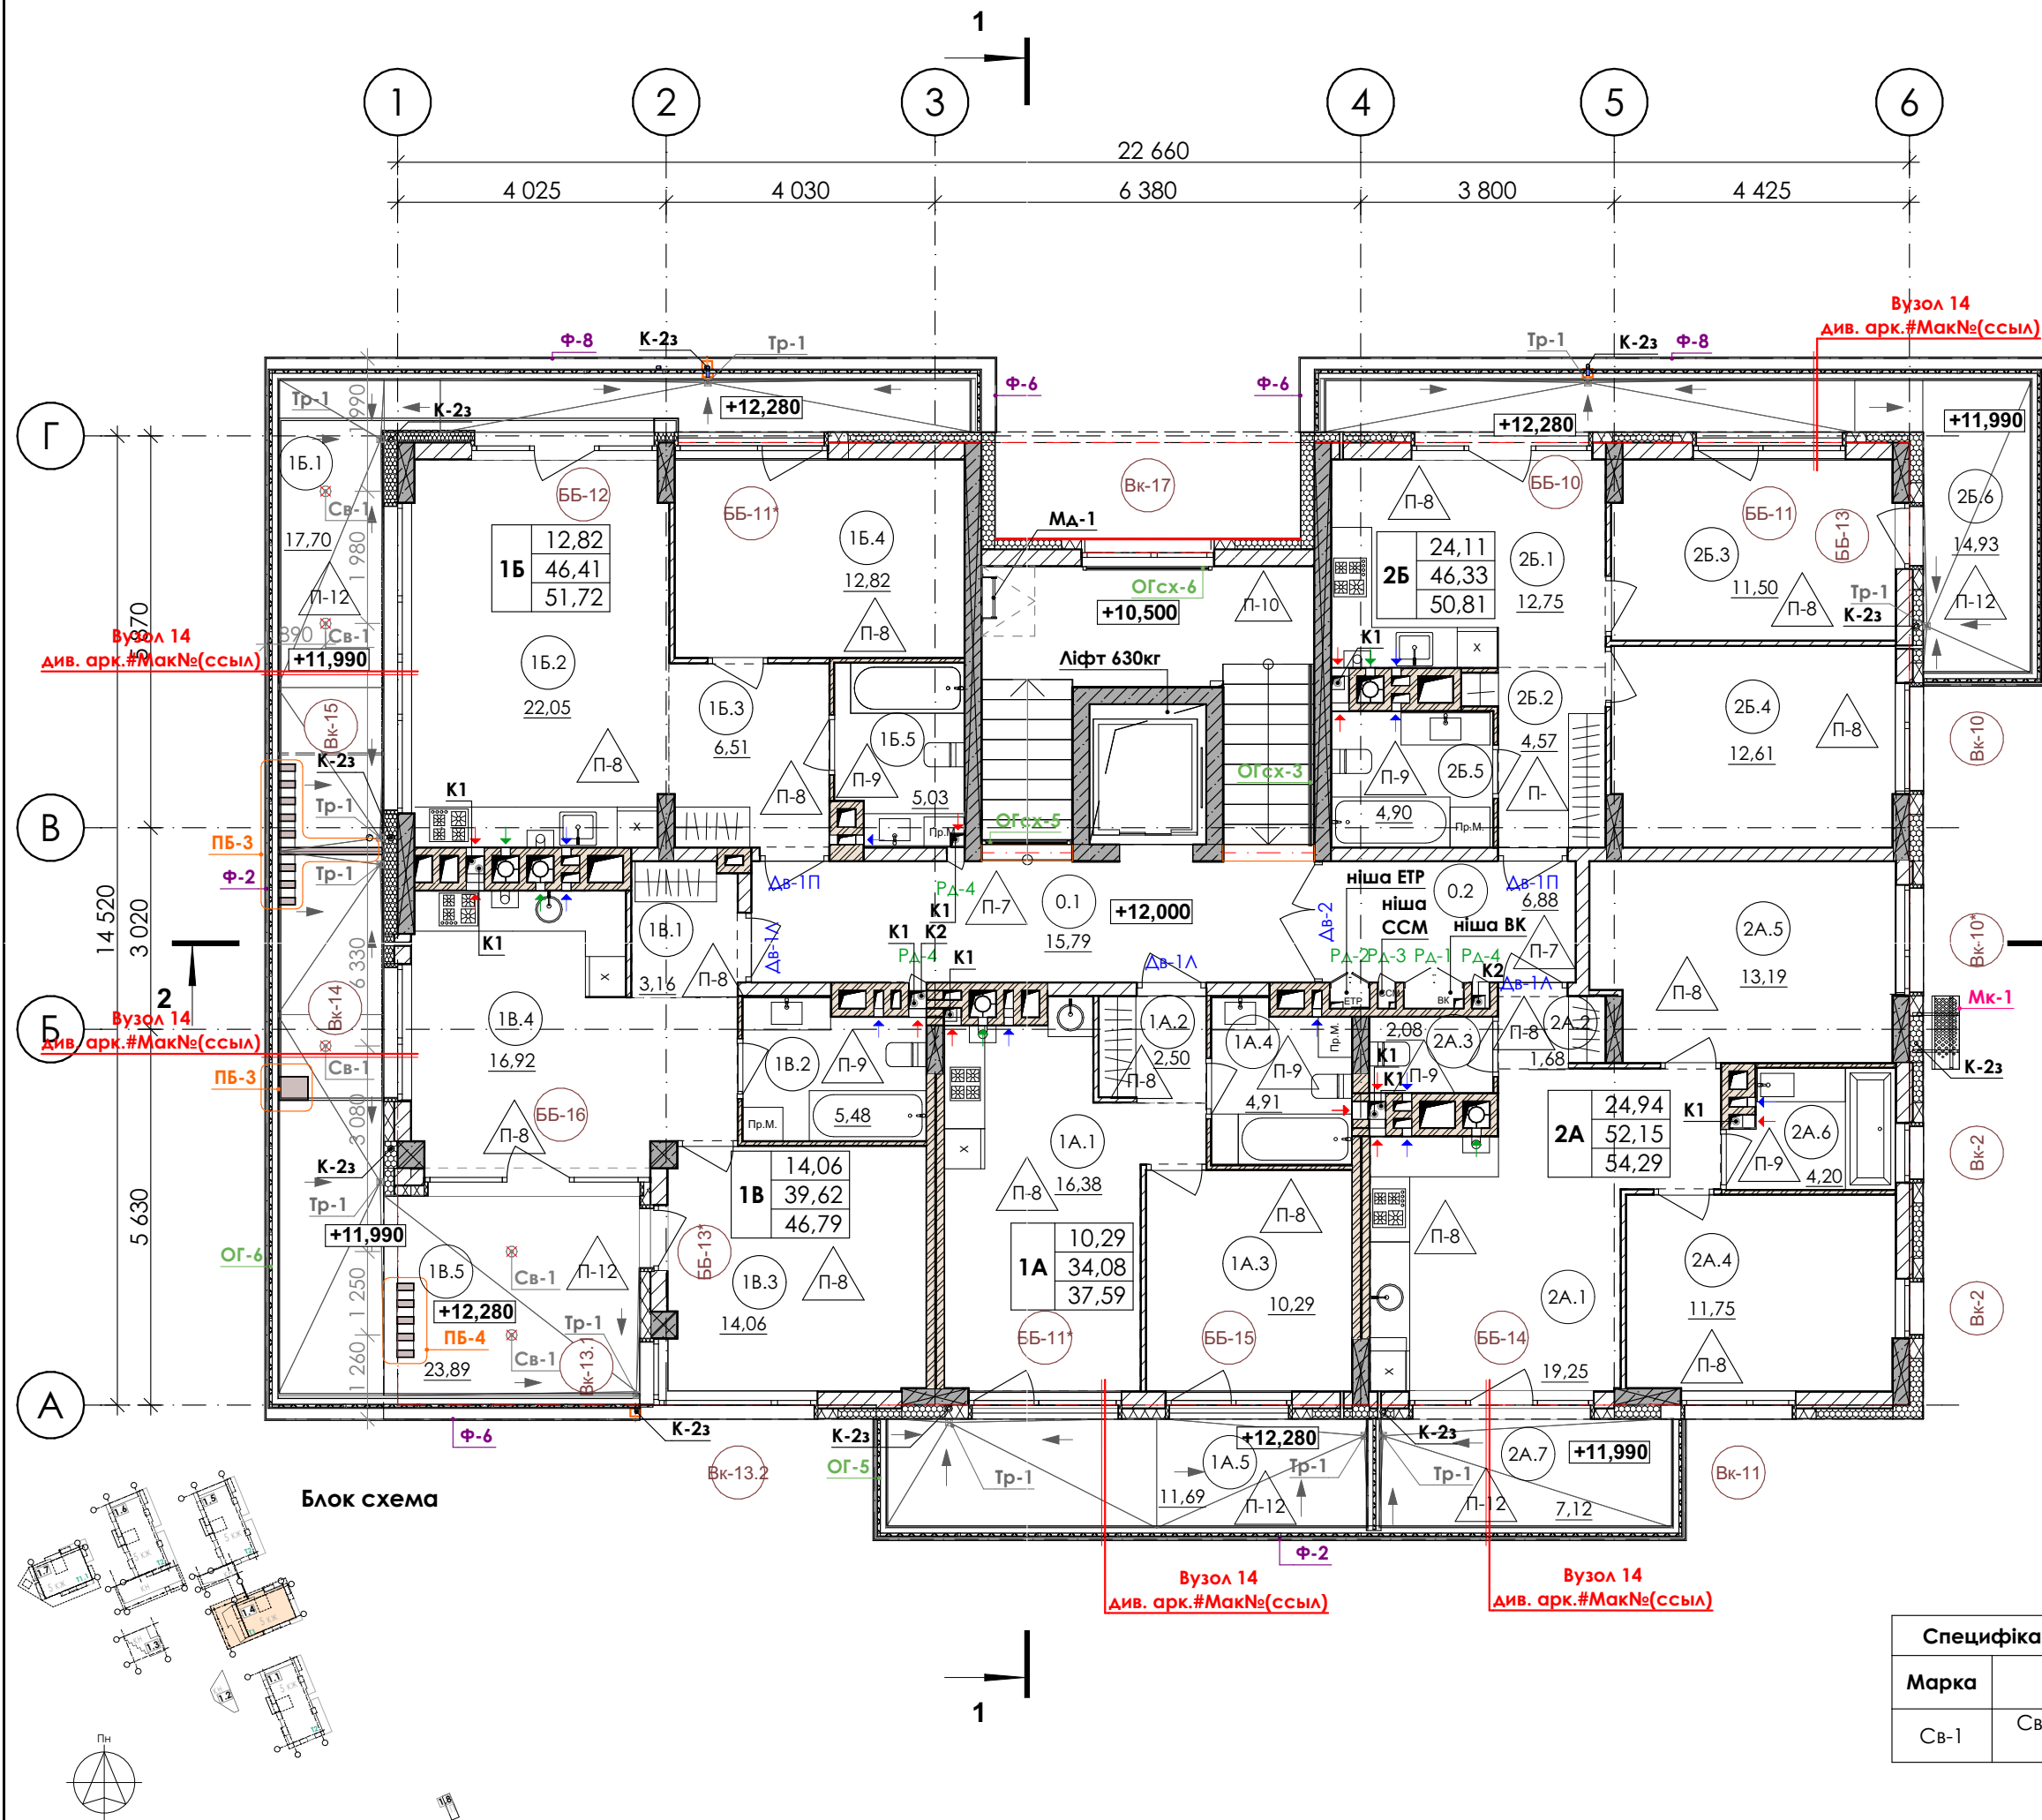Маркувальний план 5-го поверху на відм. +12,000 М1:100



УМОВНІ ПОЗНАЧЕННЯ


- зовнішня стіна (газоблок AEROC D400 - 250 мм, утеплювач мінвата 150 мм)
- внутрішня стіна (газоблок AEROC D500 - 200мм)
- залізобетонний пілон
- внутрішня перегородка, (цегла повнотіла -120 мм; утеплювач пінопласт - 20мм; цегла повнотіла -120 мм)
- внутрішня перегородка, (газоблок AEROC D500 - 75мм)
- внутрішня перегородка, (цегла повнотіла на ребро — 65 мм)
- вентиляційний канал
- колективний димохід
- каналізаційний стояк
- тип підлоги
- тип квартири
 - житлова площа квартири
 - площа приміщень квартири
 - загальна площа квартири
 - кількість кімнат
- підключення до вентиляційного каналу
- підключення до димового каналу
- підключення до K1
- K2 - каналізація дощова
- K1 - каналізація побутова
- +3,300 - відмітка рівня підлоги
- 16,44 - площа приміщення
- 2А.5 - номер приміщення
- ББ-1 - маркування балконних блоків,
- ДЗ-2 ДВ-2 - Маркування зовнішніх/внутрішніх дверей
- ВК-1 ВТ-1 - маркування вікон/вітрин
- РА-2 РА-5 - маркування ревізійних дверцят
- Ф-1 - маркування фасонних елементів
- ОГ-1 - маркування огорожень
- МК-1 - маркування корзин для кондиціонера
- МЕ-1 - маркування екранів для кондиціонерів
- ПБ-1 - маркування балконних перегородок
- номер вузла
- Вузол 5 - вузли
- Див. арк. - номер аркуша
- Св-1 - стельові світильники балконів/лоджій/терас

Тип	№ п.п.	Найменування	Площа	Прим.
0. Приміщення загального користування				
	0.1	Сходово-клітка СК 1	15,79	
	0.2	Коридор	6,88	
			22,67 м²	
1А				
	1А.1	Кухня-їдальня	16,38	
	1А.2	Передпокій	2,50	
	1А.3	Спальня	10,29	
	1А.4	Суміщений санвузол	4,91	
	1А.5	Балкон	3,51	
			37,59 м²	
1Б				
	1Б.1	Тераса	5,31	
	1Б.2	Кухня-їдальня	22,05	
	1Б.3	Передпокій	6,51	
	1Б.4	Спальня	12,82	
	1Б.5	Суміщений санвузол	5,03	
			51,72 м²	
1В				
	1В.1	Передпокій	3,16	
	1В.2	Суміщений санвузол	5,48	
	1В.3	Спальня	14,06	

Тип	№ п.п.	Найменування	Площа	Прим.
0.	1В.4	Кухня-їдальня	16,92	
	1В.5	Тераса	7,17	
			46,79 м²	
2А				
	2А.1	Кухня-їдальня	19,25	
	2А.2	Передпокій	1,68	
	2А.3	Санвузол	2,08	
	2А.4	Спальня	11,75	
	2А.5	Спальня	13,19	
	2А.6	Ванна	4,20	
	2А.7	Балкон	2,14	
			54,29 м²	
2Б				
	2Б.1	Кухня-їдальня	12,75	
	2Б.2	Передпокій	4,57	
	2Б.3	Спальня	11,50	
	2Б.4	Спальня	12,61	
	2Б.5	Суміщений санвузол	4,90	
	2Б.6	Балкон	4,48	
			50,81 м²	
			263,87 м²	

Специфікація трапів 5-го поверху						
Марка трапа	Найменування	Вигляд	Розміри, мм	Кількість	Виробник	Примітки
Тр-1	Трап горизонтальний		100x100 h=50	11	Valrom	див. розділ ВК

Специфікація балконних світильників СВ-1 5 поверх			
Марка	Найменування	Кількість	Примітки
Св-1	Світильник стельовий, круглий	5	

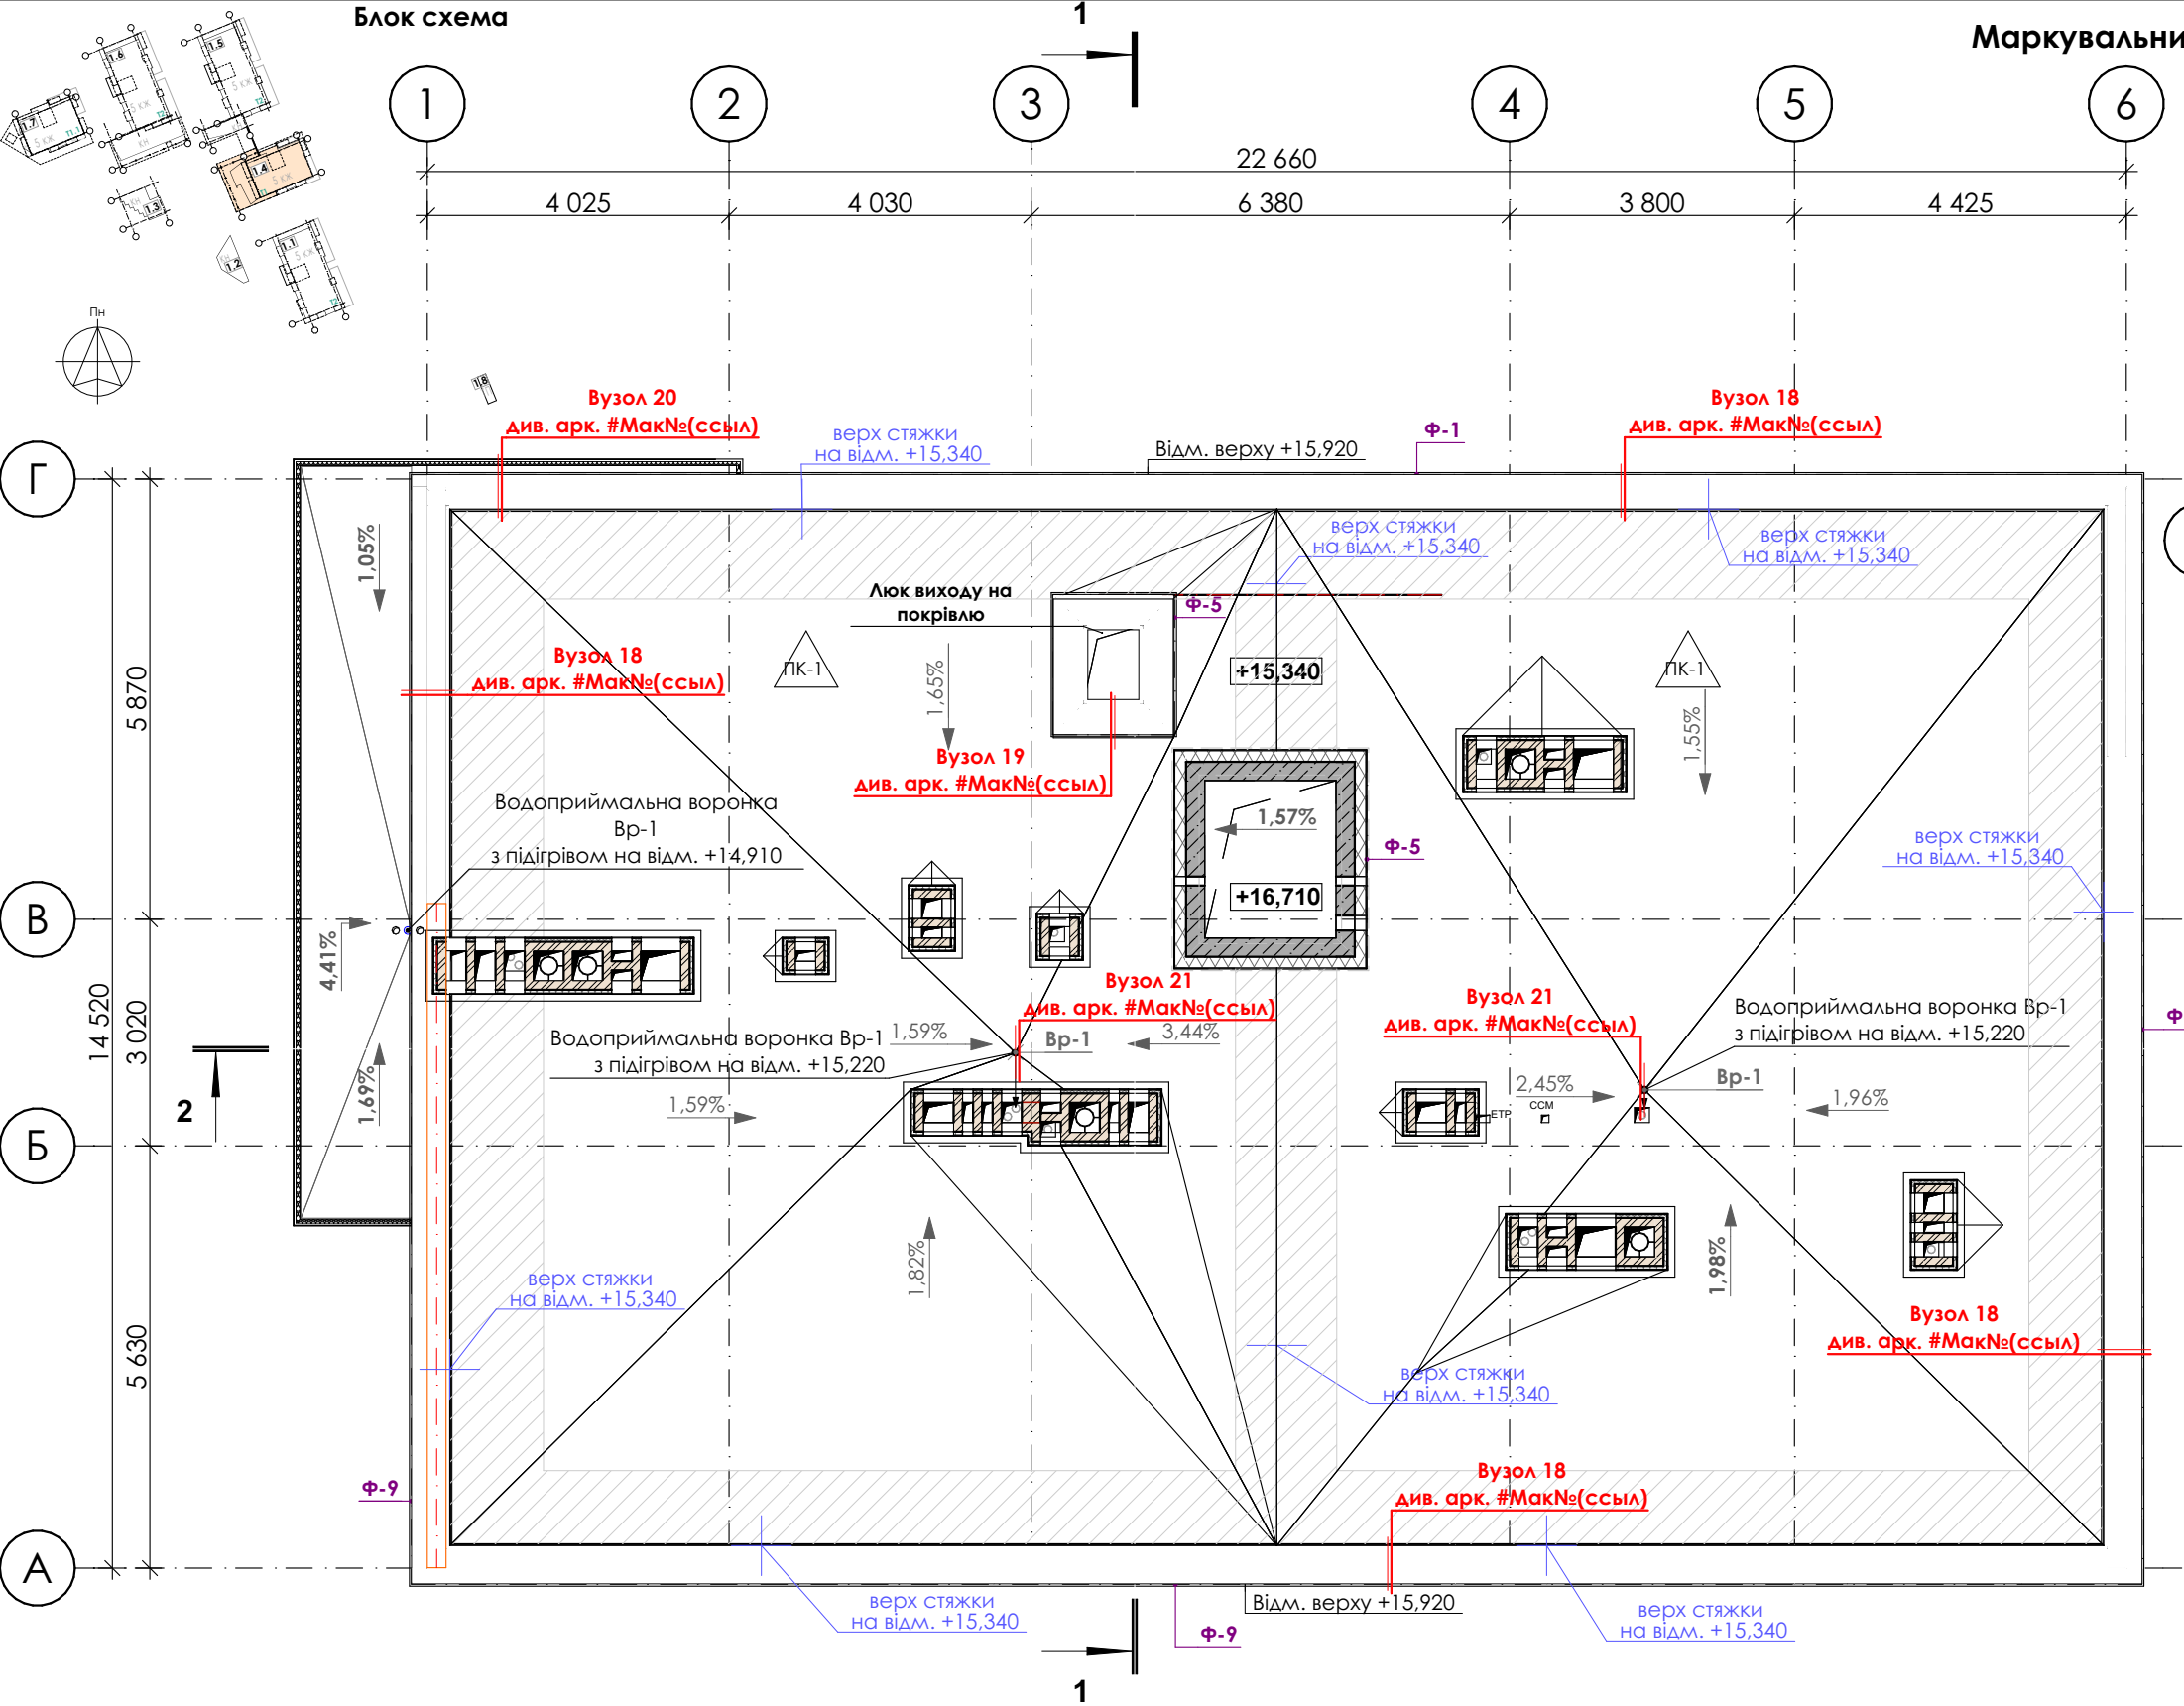

УМОВНІ ПОЗНАЧЕННЯ

- зовнішня стіна (Цегла повнотіла М100 - 250 мм, утеплювач плити пінополістирольні ПСБ-25, 200 мм/50мм)
- вентиляційний канал (повнотіла цегла 120/250мм)
- колективний димохід
- каналізаційний стояк
- залізобетонний пілон
- тип підлоги/стелі
- 1.90%- напрям і ухил стоку води
- водоприймальна воронка
- +15,340 - відмітка рівня підлоги
- БН-1 - маркування плит накриття вентканалів
- Ф-1 - маркування фасонних елементів
- номер вузла
- вузли
- номер аркуша
- PIR UTHERM ROOF LE 100
- Додатковий шар (група горючості Г-1)

Специфікація воронок покрівлі

Марка	Найменування	Кількість	Примітки
Вр-1	Водоприймальна воронка з підігрівом	2	див. розділ ВК

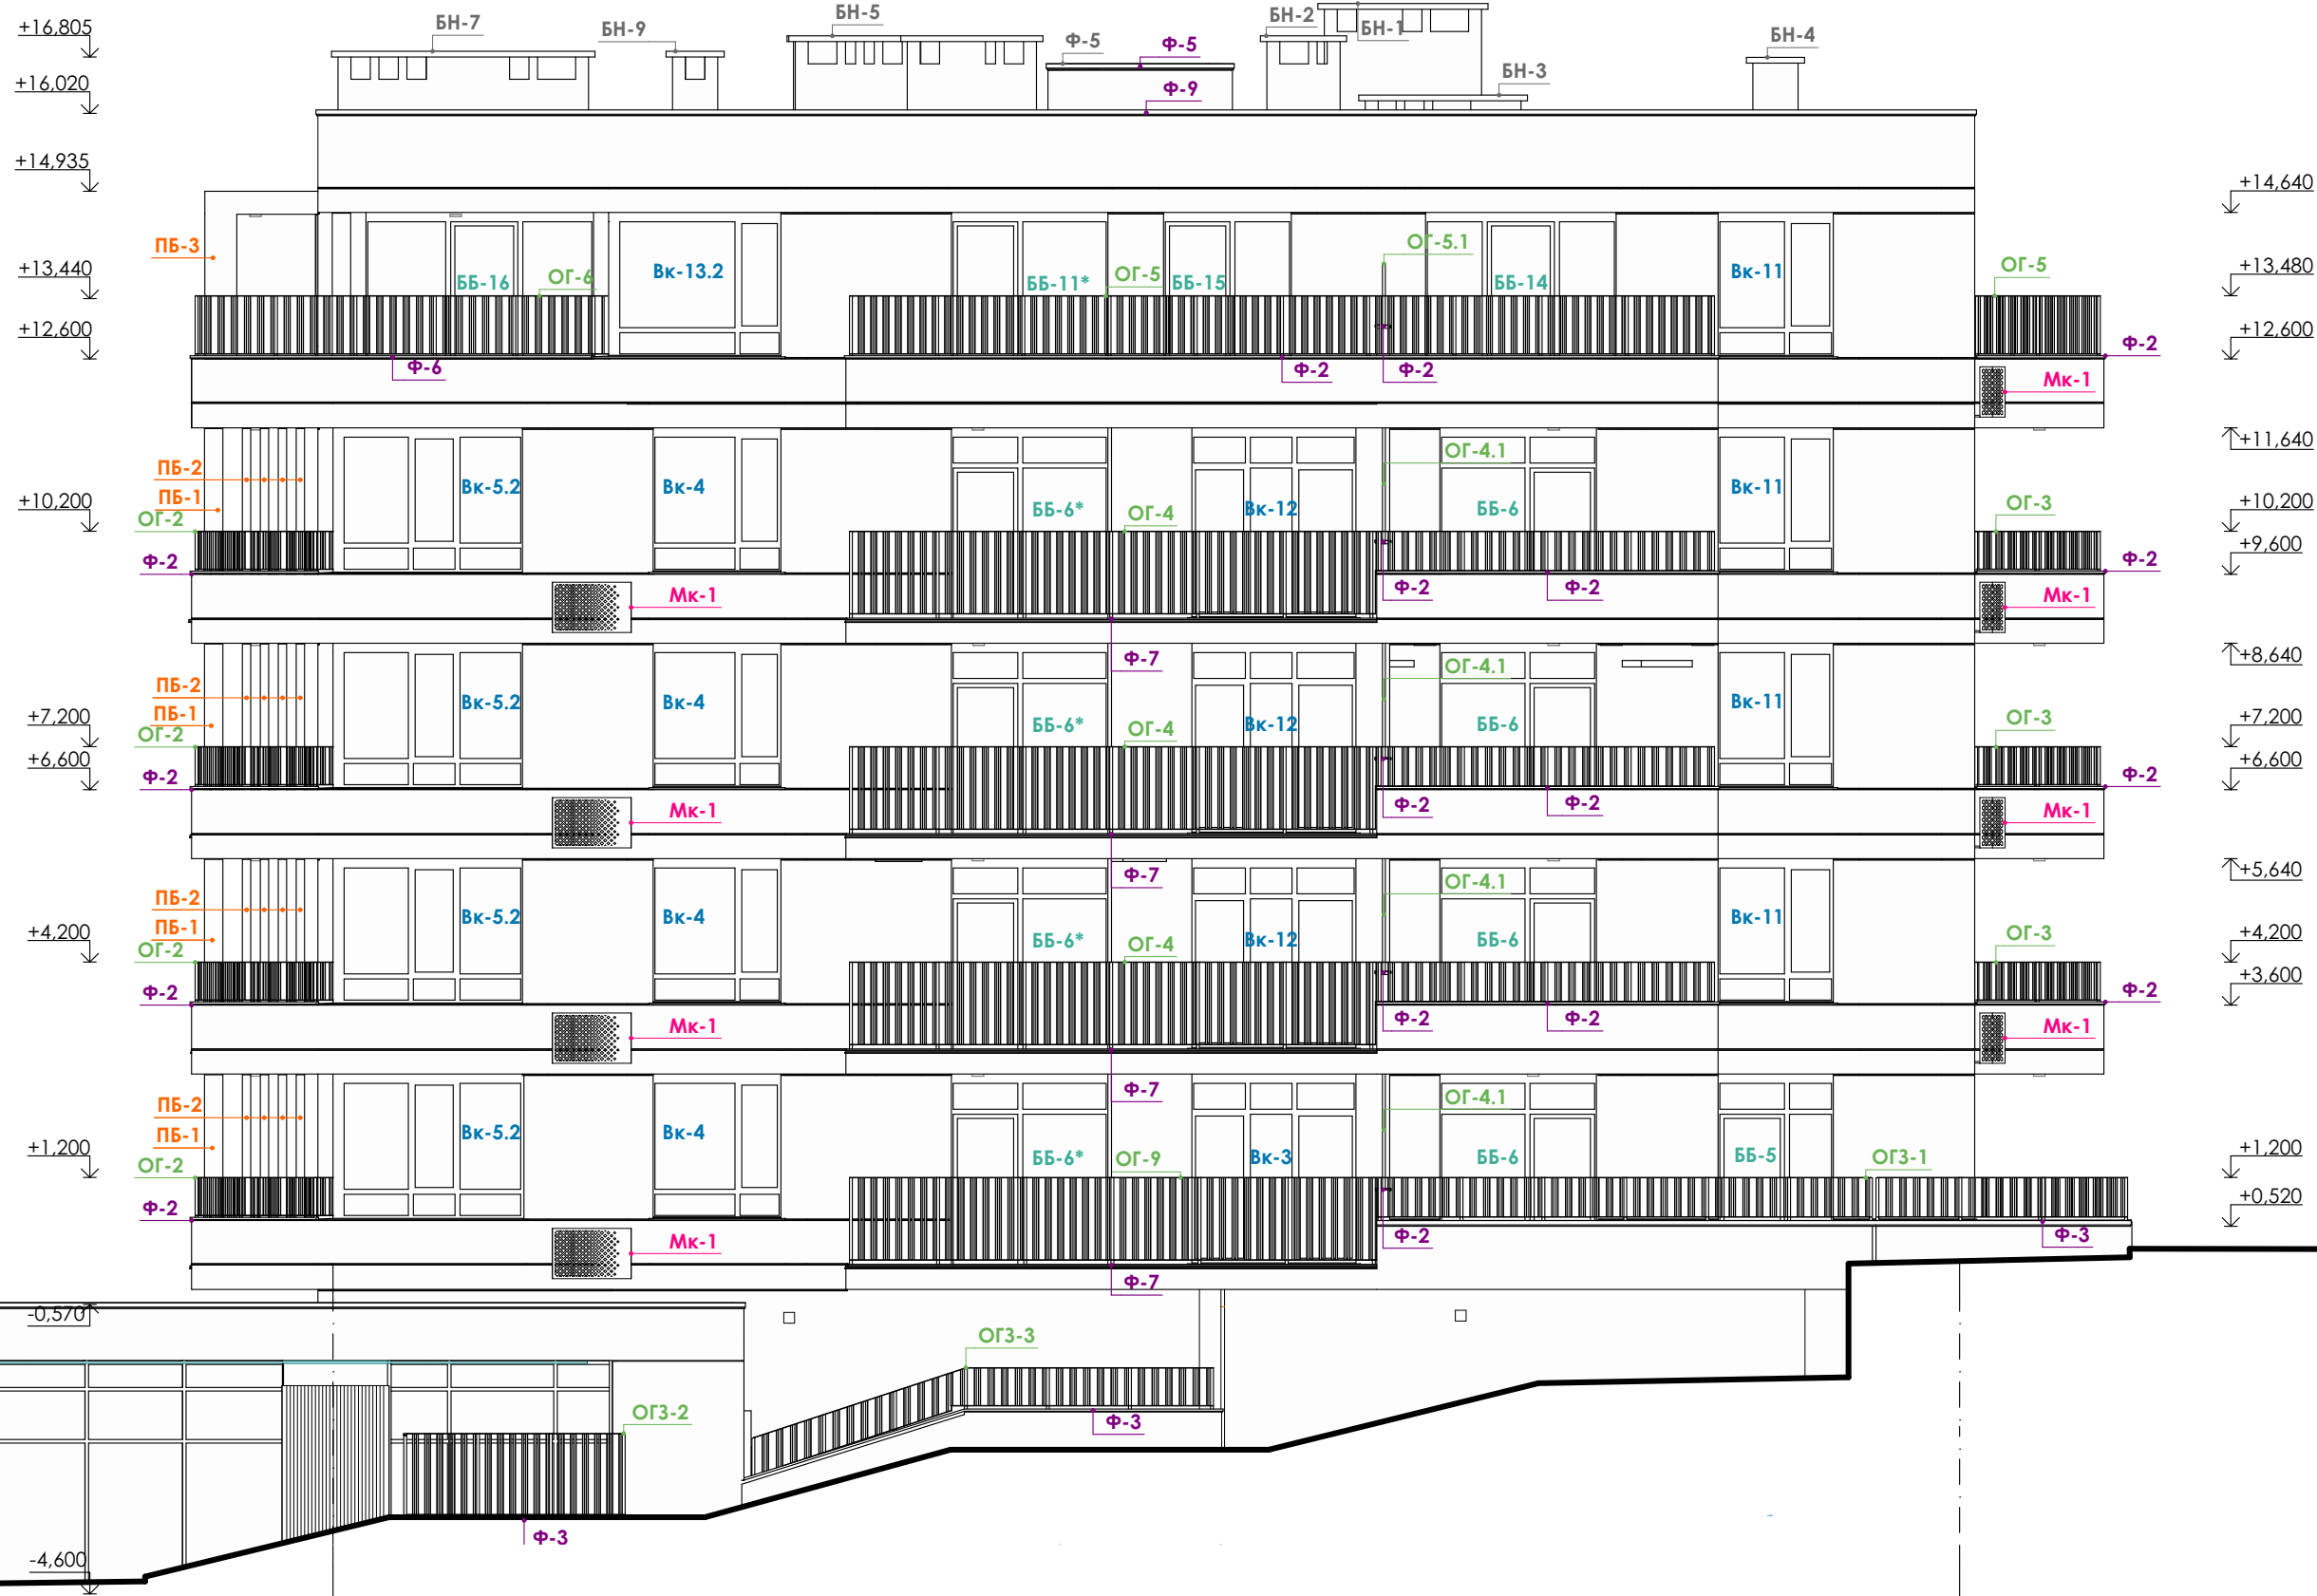
УМОВНІ ПОЗНАЧЕННЯ

-  - зовнішня стіна (газоблок AEROC D400 - 250 мм, утеплювач пінополістирол 150 мм)
-  - внутрішня стіна (газоблок AEROC D400 - 200 мм)
-  - внутрішня стіна (цегла - 120 мм)
-  - зовнішня стіна (цегла - 250 мм), утеплення 50/50
-  - залізобетонний пілон
-  - залізобетонне перекриття

+3,000 - висотні відмітки




Фасад в осях 1-6 М 1:100



Умовні позначення:


- | | | | |
|-------------|---|---------------|--|
| Вк-3 | - Маркування заповнення віконних прорізів | ПБ-1 | - Маркування перегородок балконних |
| ББ-1 | - Маркування заповнення балконних прорізів | Ф-1 | - Маркування фасонних елементів |
| Вт-1 | - Маркування заповнення вітрин | БН-2 | - Маркування плит накриття вентканалів |
| Мк-1 | - Маркування корзин під зовнішній блок кондиціонера | +5,400 | - Відмітки |

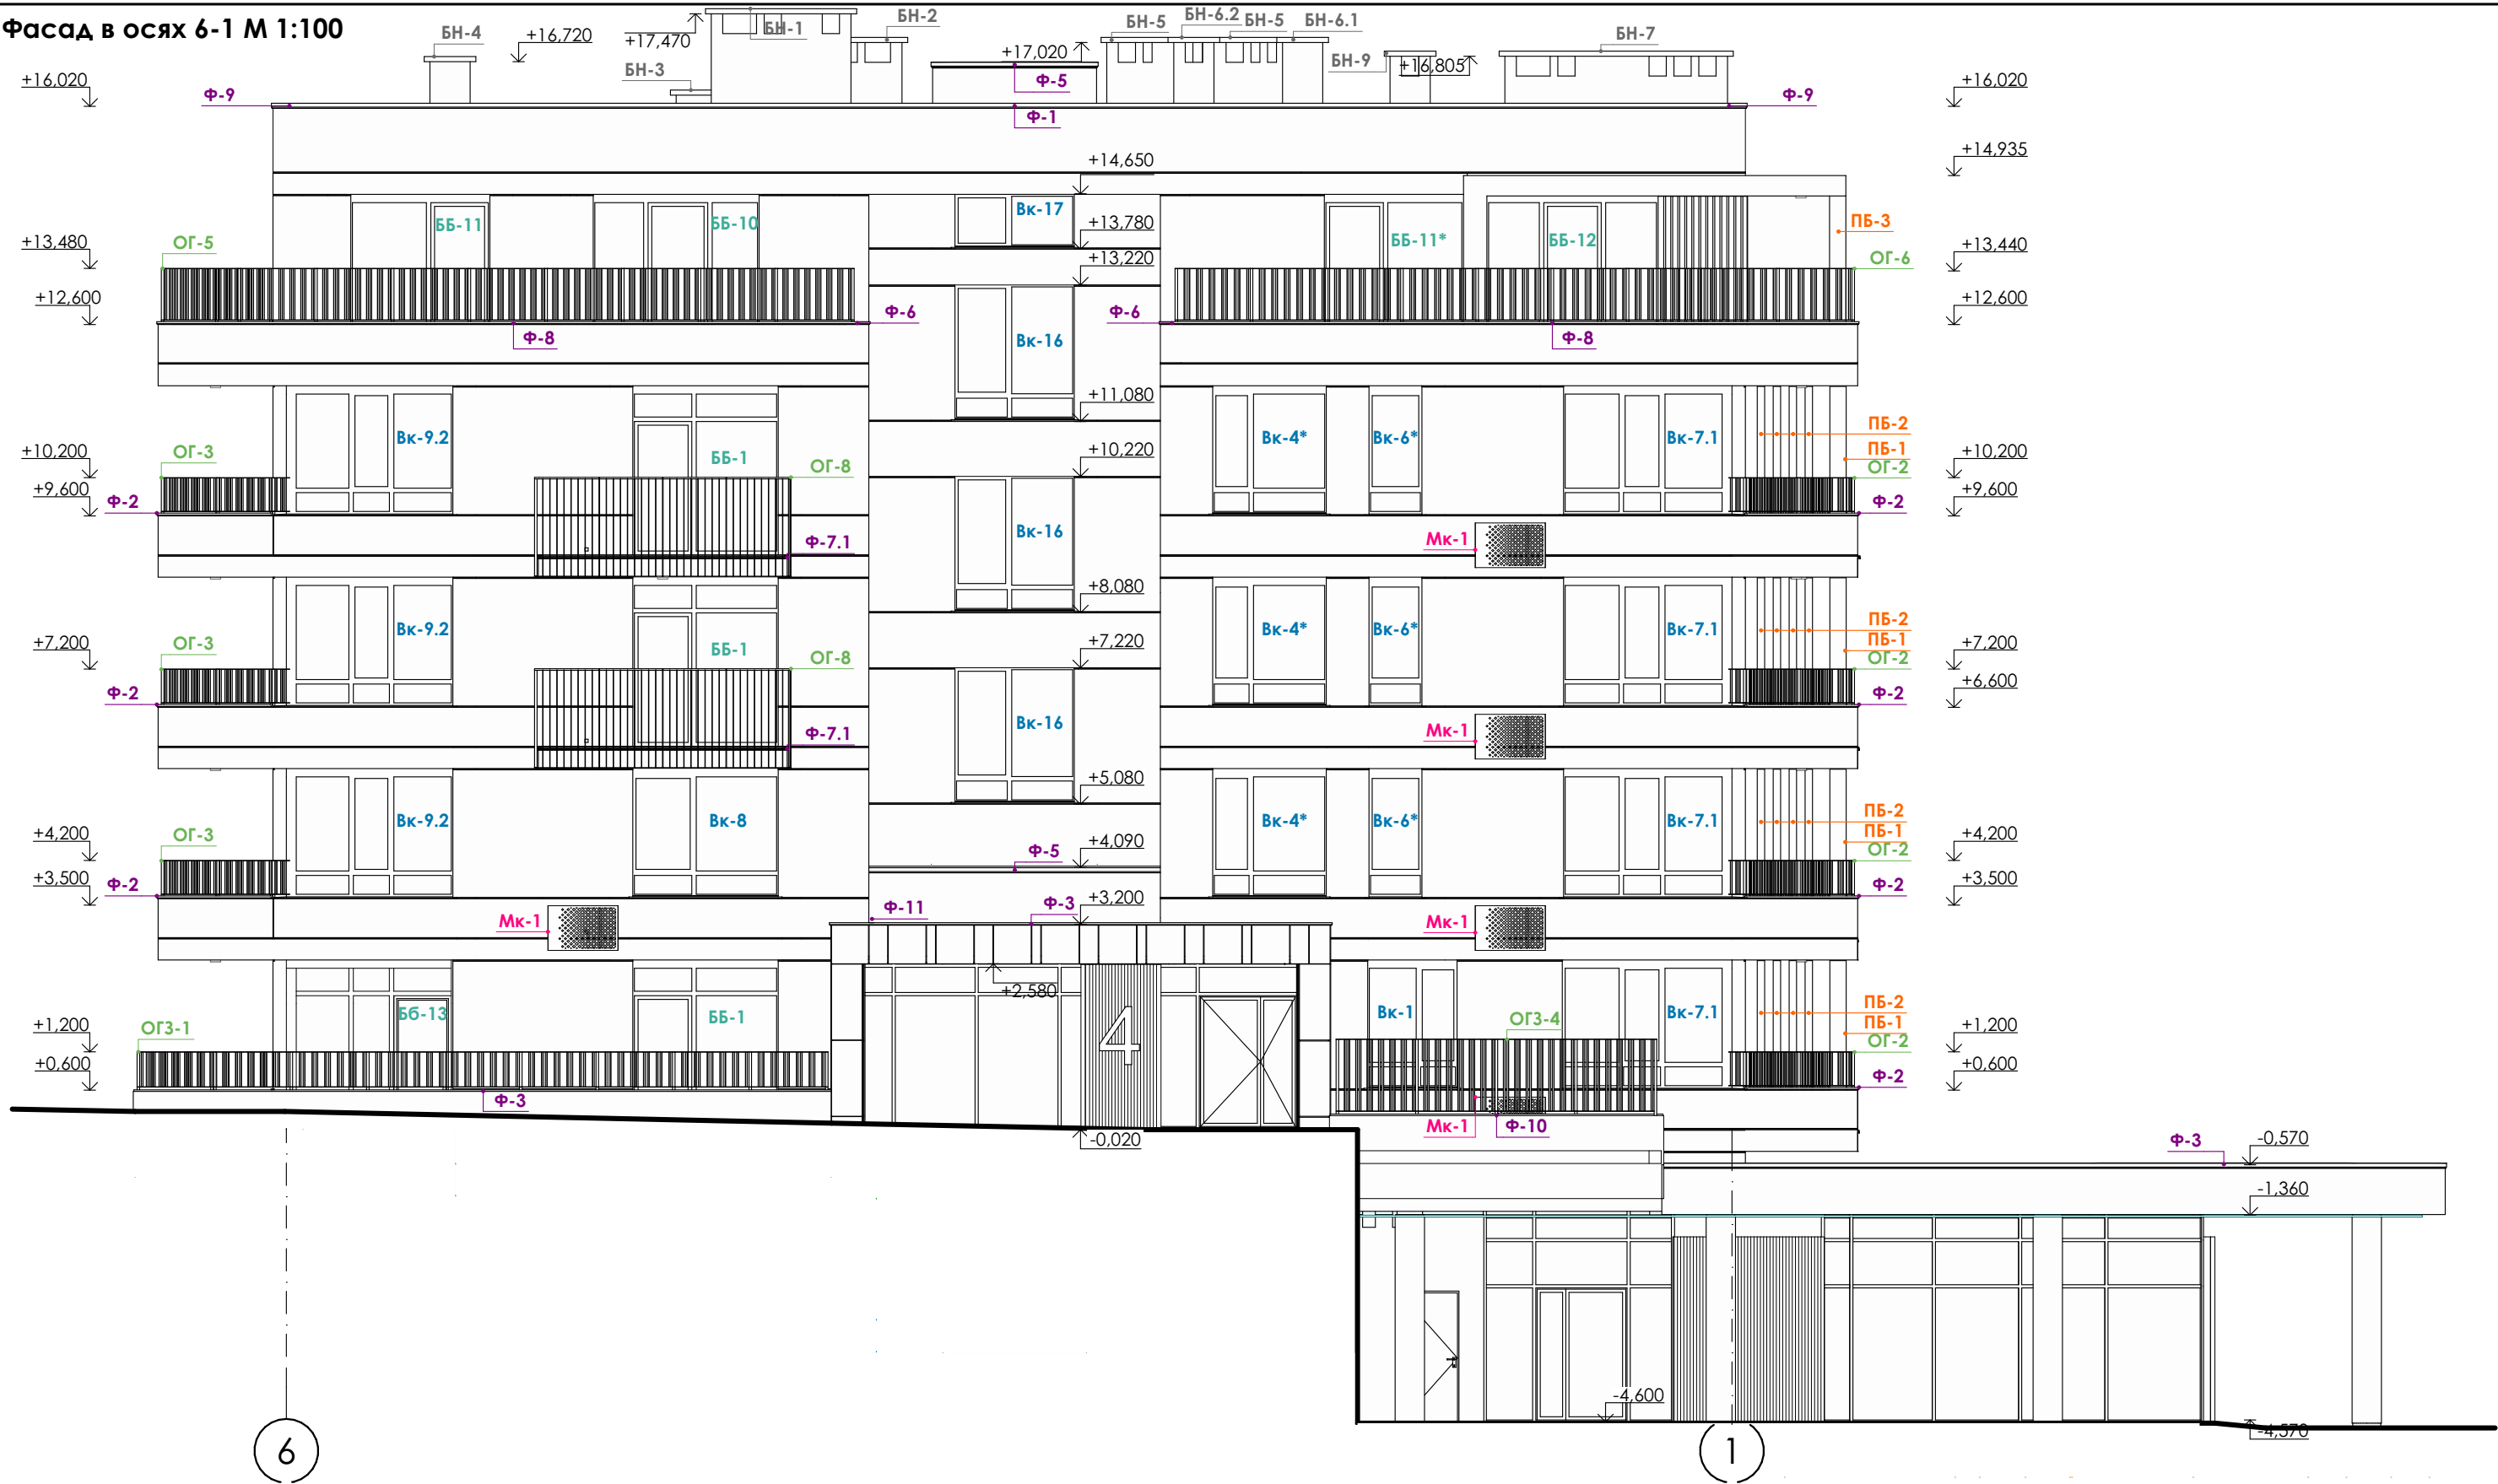Фасад в осях 6-1 М 1:100



- | | | | |
|-------------|---|---------------|--|
| Вк-3 | - Маркування заповнення віконних прорізів | Ог-1 | - Маркування огорожень |
| ББ-1 | - Маркування заповнення балконних прорізів | ПБ-1 | - Маркування перегородок балконних |
| Вт-1 | - Маркування заповнення вітрин | Ф-1 | - Маркування фасонних елементів |
| Мк-1 | - Маркування корзин під зовнішній блок кондиціонера | БН-2 | - Маркування плит накриття вентканалів |
| | | +5,400 | - Відмітки |

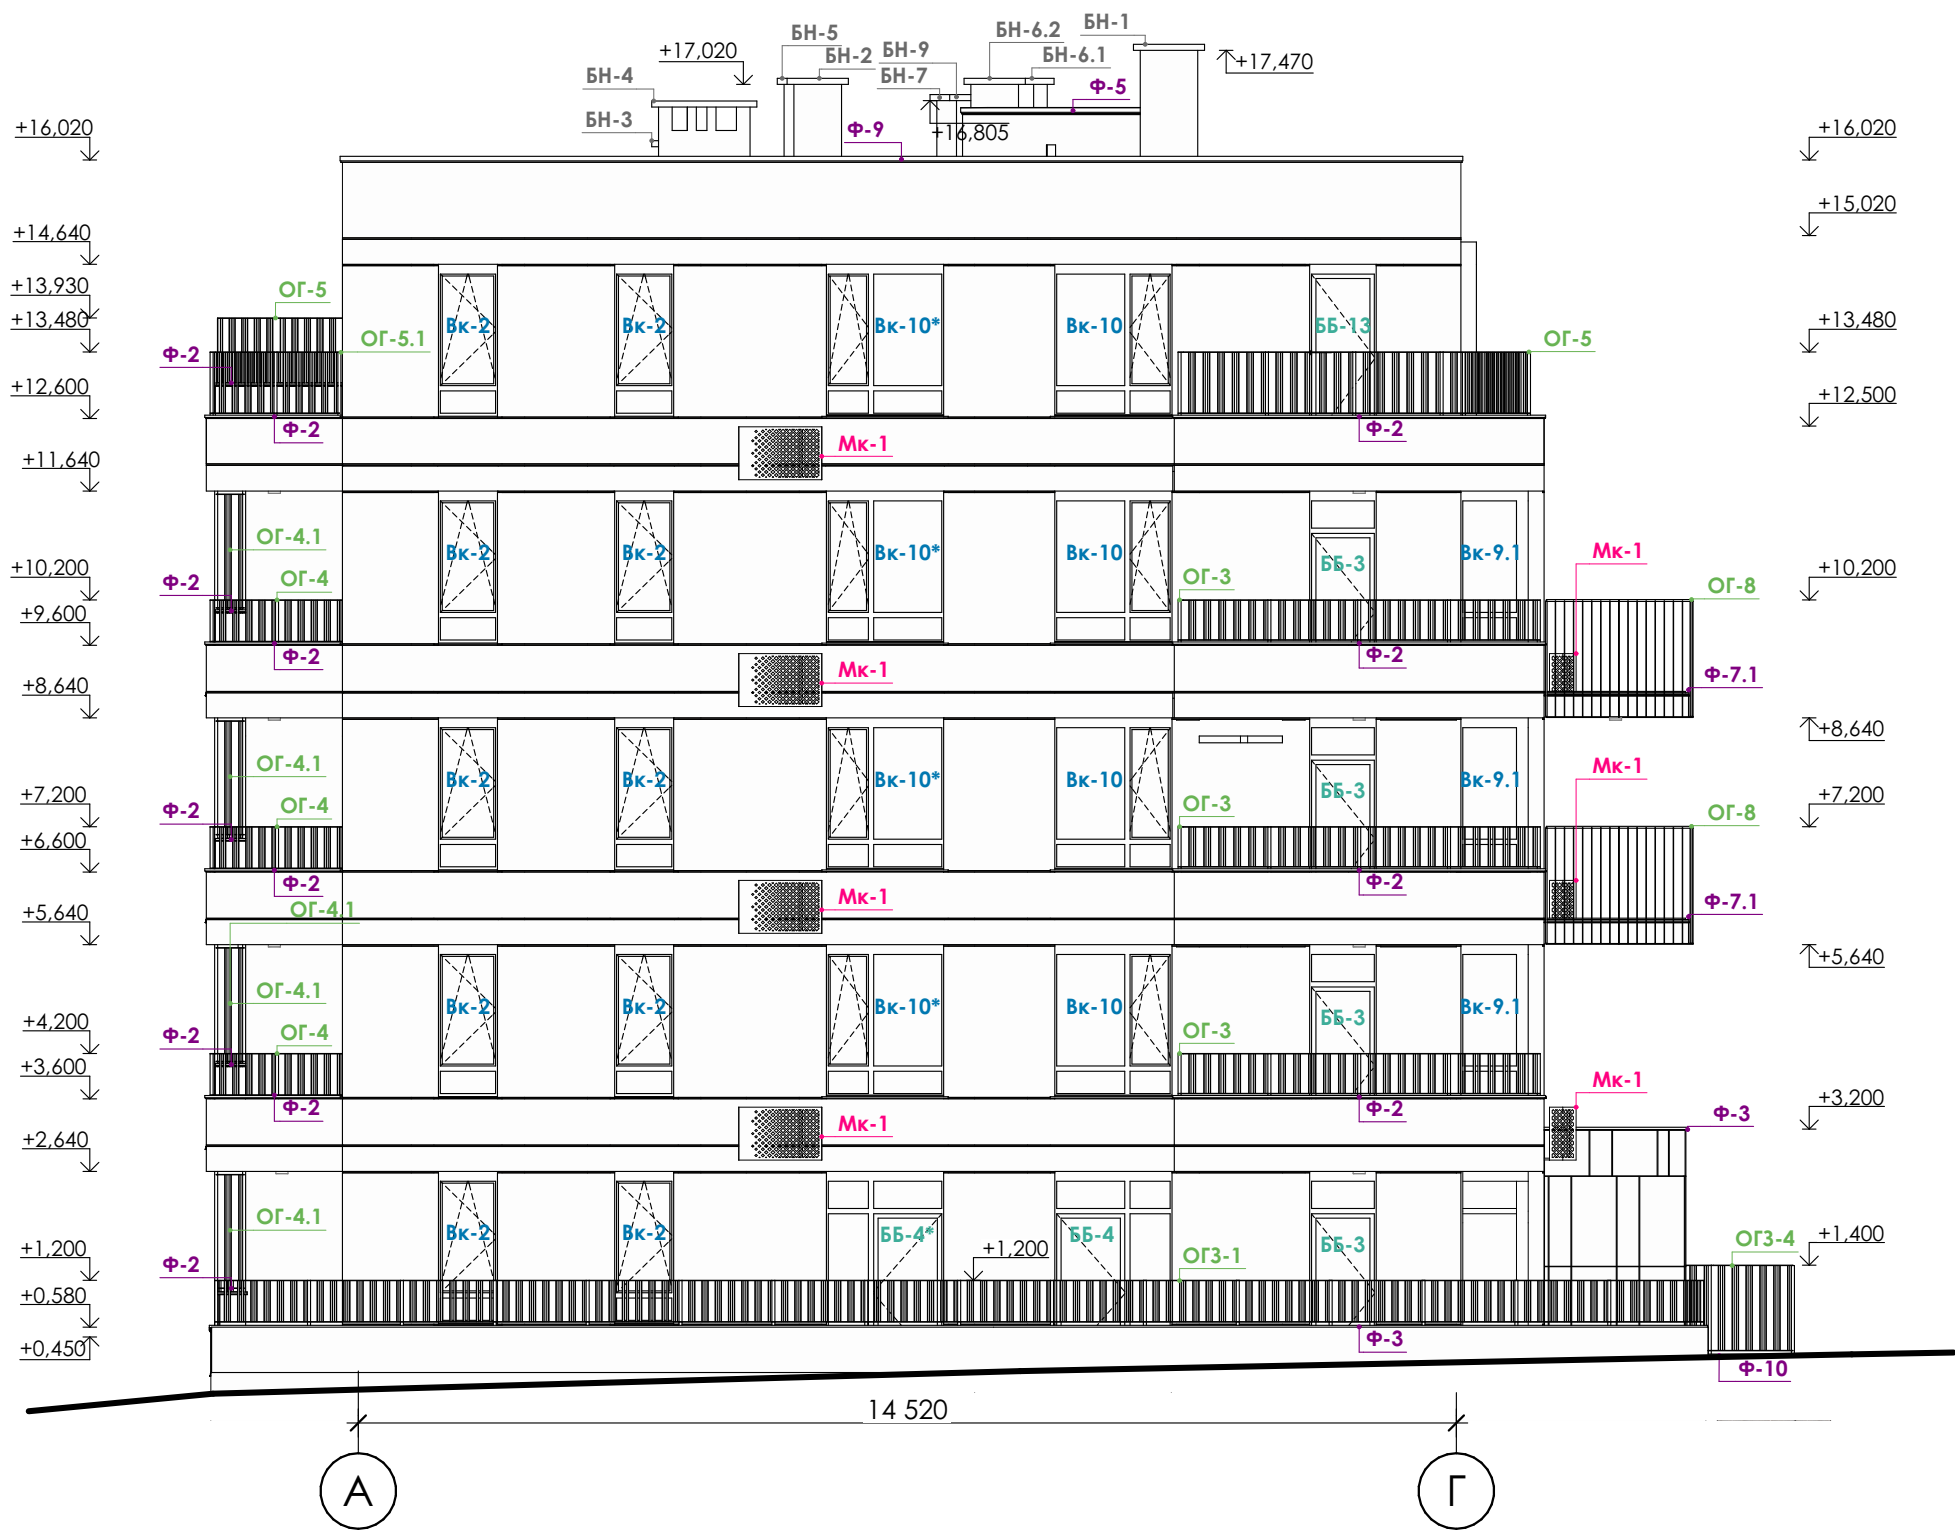
Фасад в осях А-Г М 1:100



Умовні позначення:

- | | | | |
|-------------|---|---------------|--|
| Вк-3 | - Маркування заповнення віконних прорізів | Ог-1 | - Маркування огорожень |
| ББ-1 | - Маркування заповнення балконних прорізів | ПБ-1 | - Маркування перегородок балконних |
| Вт-1 | - Маркування заповнення вітрин | Ф-1 | - Маркування фасонних елементів |
| Мк-1 | - Маркування корзин під зовнішній блок кондиціонера | БН-2 | - Маркування плит накриття вентканалів |
| | | +5.400 | - Відмітки |

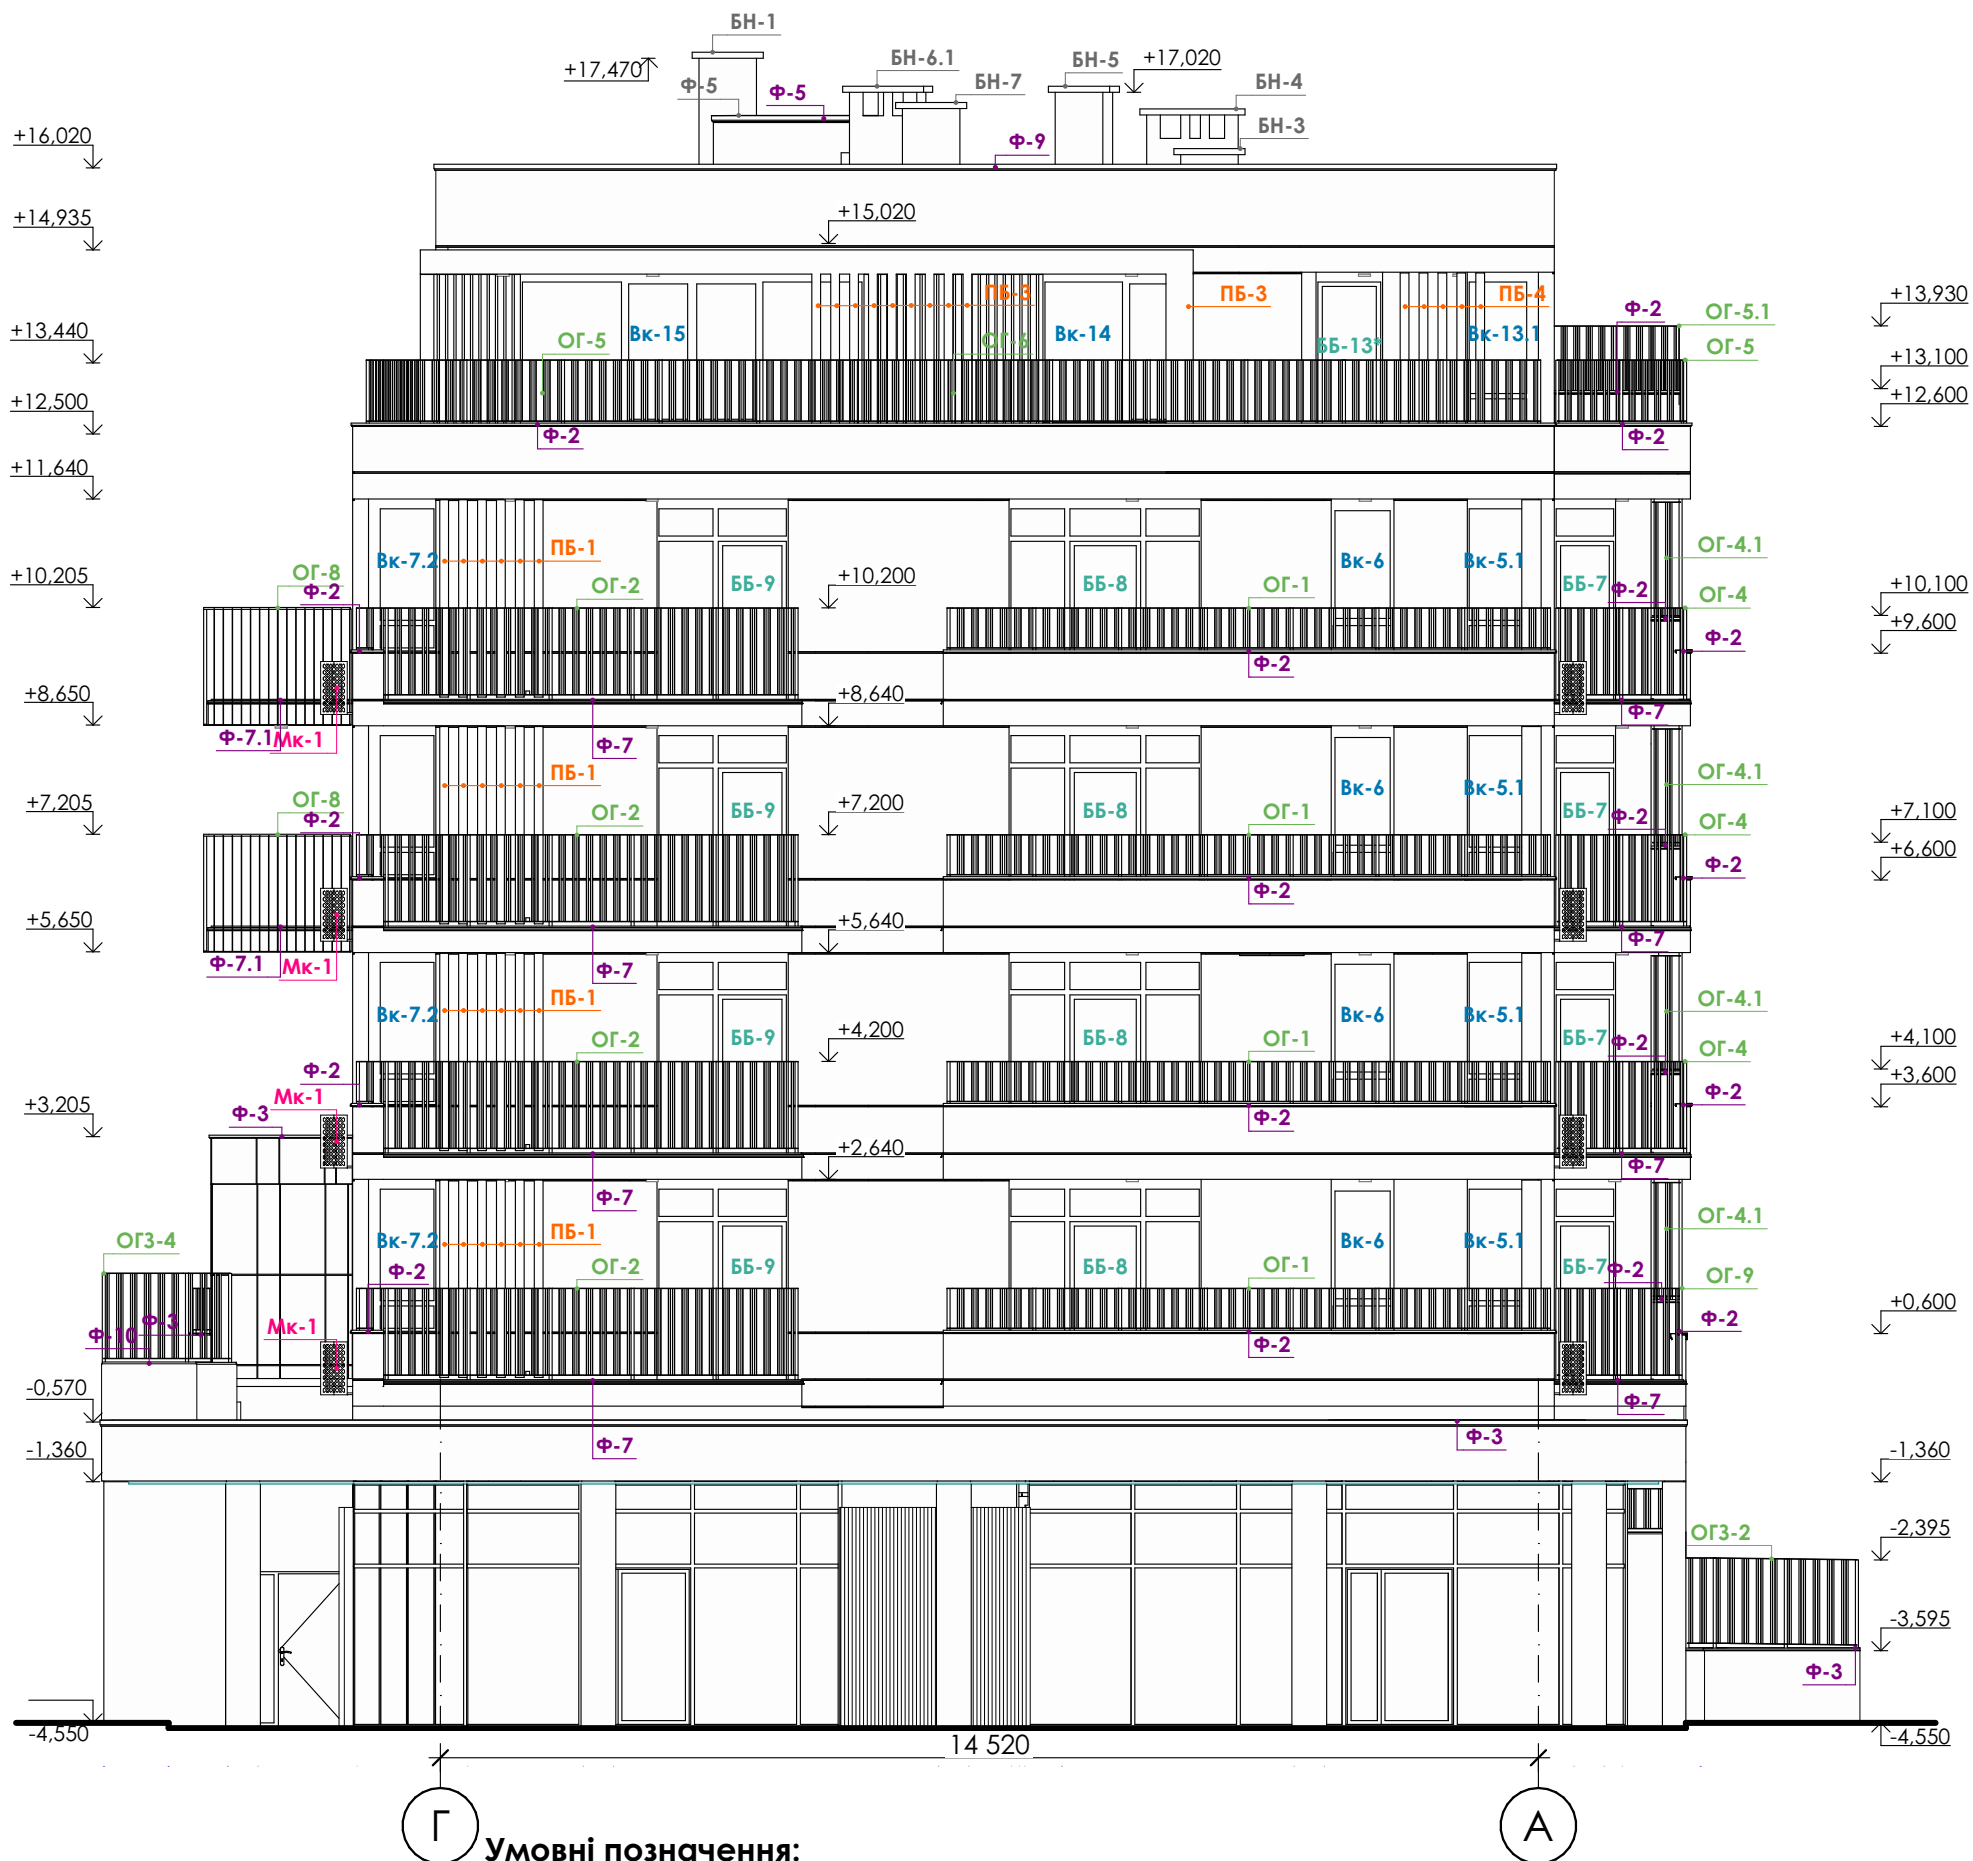Фасад в осях Г-А М 1:100



Умовні позначення:

Вк-3	- Маркування заповнення віконних прорізів	Ог-1	- Маркування огорожень
ББ-1	- Маркування заповнення балконних прорізів	ПБ-1	- Маркування перегородок балконних
ВТ-1	- Маркування заповнення вітрин	Ф-1	- Маркування фасонних елементів
Мк-1	- Маркування корзин під зовнішній блок кондиціонера	БН-2	- Маркування плит накриття вентканалів
		+5.400	- Відмітки

Схема утепления фасаду в осях 1-6 М 1:100

Умовні позначення:

- 1

Плити мінераловатні Технофас Оптіма, 200 мм
- 2

Плити мінераловатні Технофас Оптіма, 150 мм
- 3

Плити мінераловатні Технофас Оптіма, 50 мм
- 4

Плити пінополістерольні ПСБ-25, 200 мм
- 5

Плити пінополістерольні ПСБ-25, 150 мм
- 6

Плити пінополістерольні ПСБ-25, 50 мм
- 7

Плити пінополістерольні ПСБ-25, 20 мм
- 8

Плити мінераловатні Техновент Стандарт, 200 мм
- 9

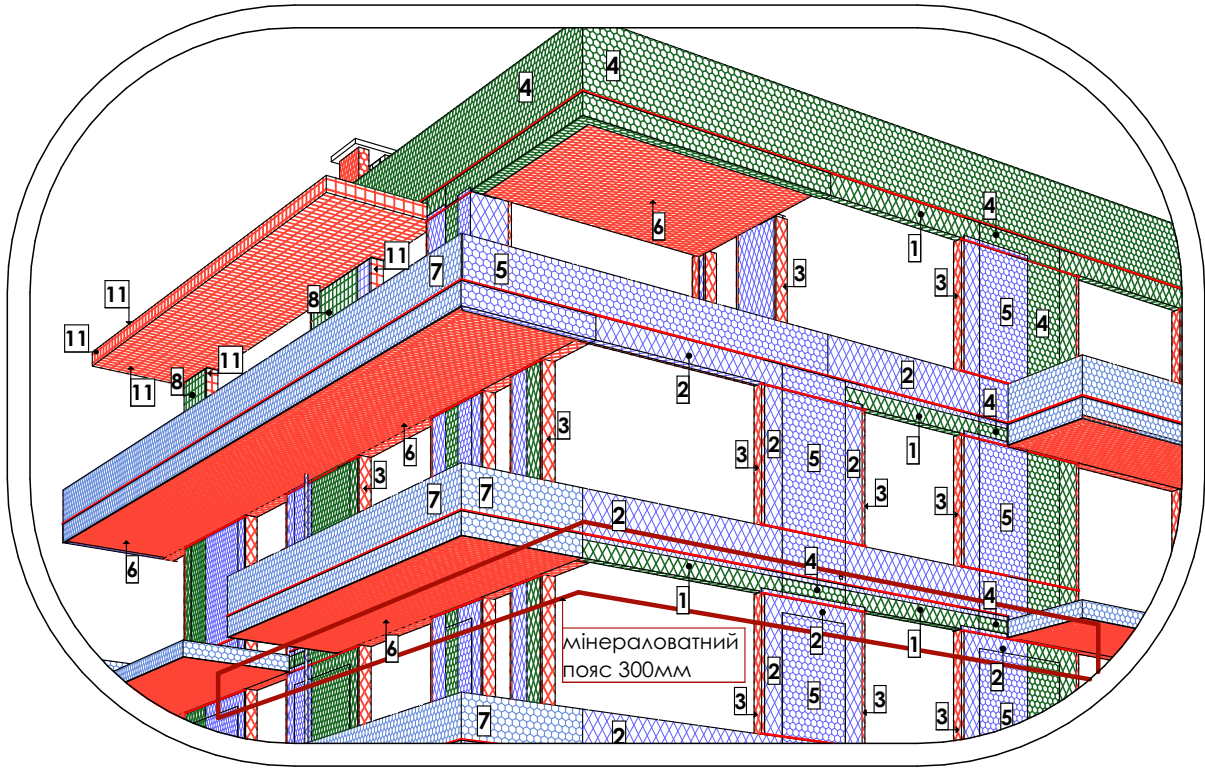
Плити мінераловатні Техновент Стандарт, 150 мм
- 10

Плити мінераловатні Техновент Стандарт, 100 мм
- 11

Плити мінераловатні Техновент Стандарт, 50 мм
- 12


Екструдований пінополістерол, 100 мм
- 13

Стояки K2 для відведення конденсату з зовнішніх блоків кондиціонерів і водовідведення балконів
- Рустовочний профіль 20х20 мм



Позн. маркув.	Найменування	Кіл-сть, м ²	Примітки
1	Плити мінераловатні Технофас Оптіма, 200 мм	76	
2	Плити мінераловатні Технофас Оптіма, 150 мм	210	
3	Плити мінераловатні Технофас Оптіма, 50 мм	108	
4	Плити пінополістерольні ПСБ-25, 200 мм	248	
5	Плити пінополістерольні ПСБ-25, 150 мм	295	
6	Плити пінополістерольні ПСБ-25, 50 мм	681	
7	Плити пінополістерольні ПСБ-25, 20 мм	381	
8	Плити мінераловатні Техновент Стандарт, 200 мм	8	
9	Плити мінераловатні Техновент Стандарт, 150 мм	27	
10	Плити мінераловатні Техновент Стандарт, 100 мм	31	
11	Плити мінераловатні Техновент Стандарт, 50 мм	21	
12	Екструдований пінополістерол, 100 мм	52	
14	Теплоізоляційні плити PIR (Г-1), 50 мм	23	
	Рустовочний профіль 20х20 мм	1 570 м.п	

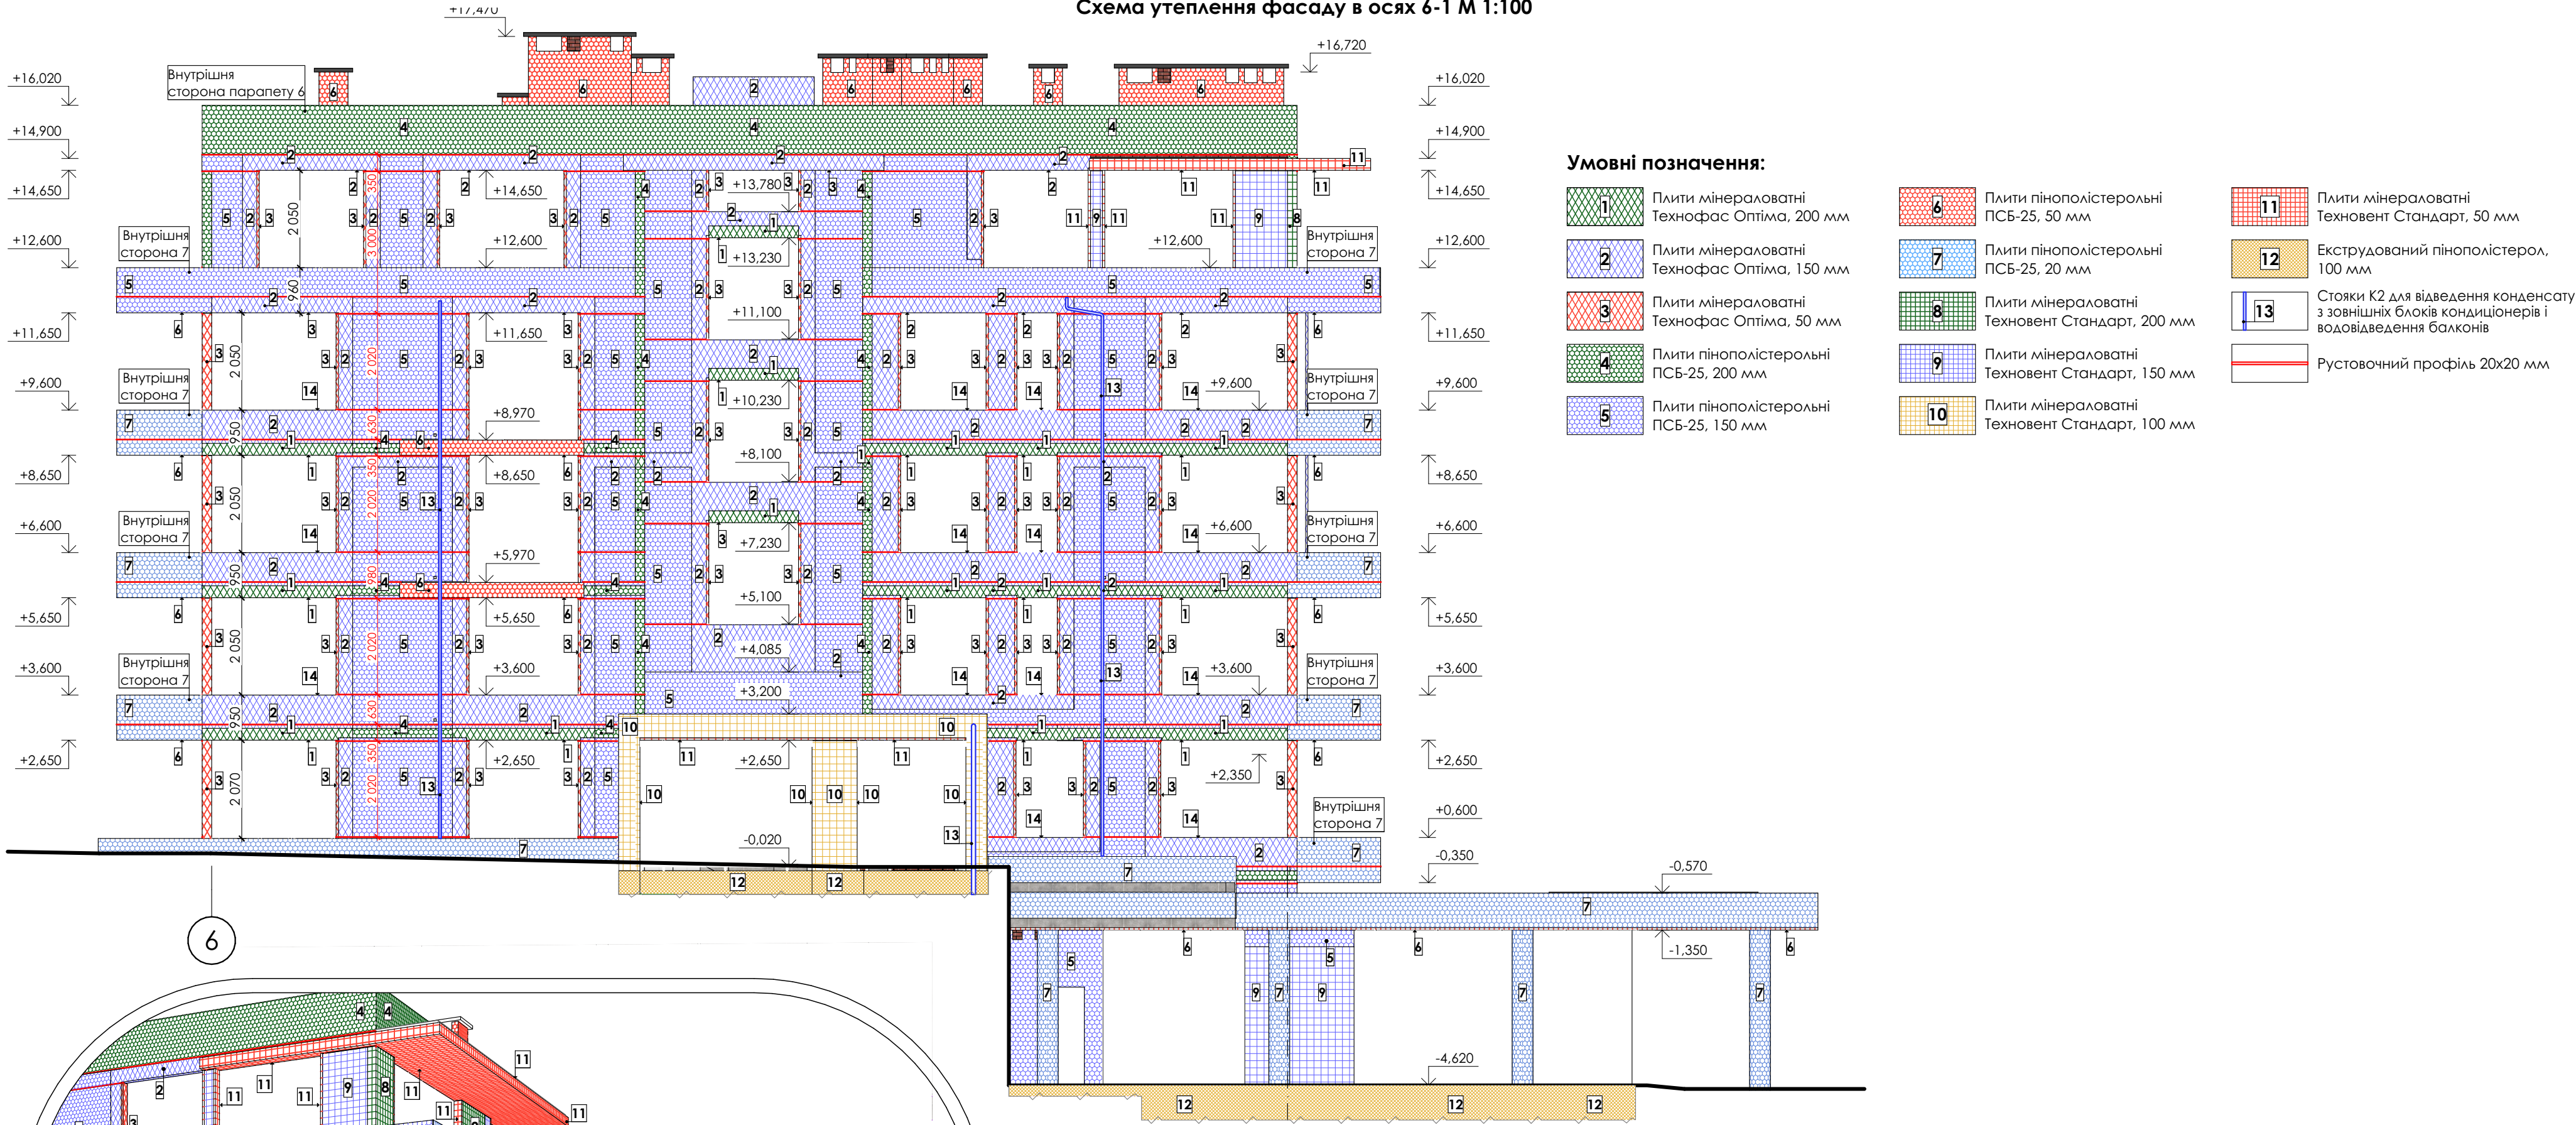Схема утепления фасаду в осях 6-1 М 1:100



Умовні позначення:

- 1

Плити мінераловатні Технофас Оптіма, 200 мм
- 2

Плити мінераловатні Технофас Оптіма, 150 мм
- 3

Плити мінераловатні Технофас Оптіма, 50 мм
- 4

Плити пінополістерольні ПСБ-25, 200 мм
- 5

Плити пінополістерольні ПСБ-25, 150 мм
- 6

Плити пінополістерольні ПСБ-25, 50 мм
- 7

Плити пінополістерольні ПСБ-25, 20 мм
- 8

Плити мінераловатні Техновент Стандарт, 200 мм
- 9

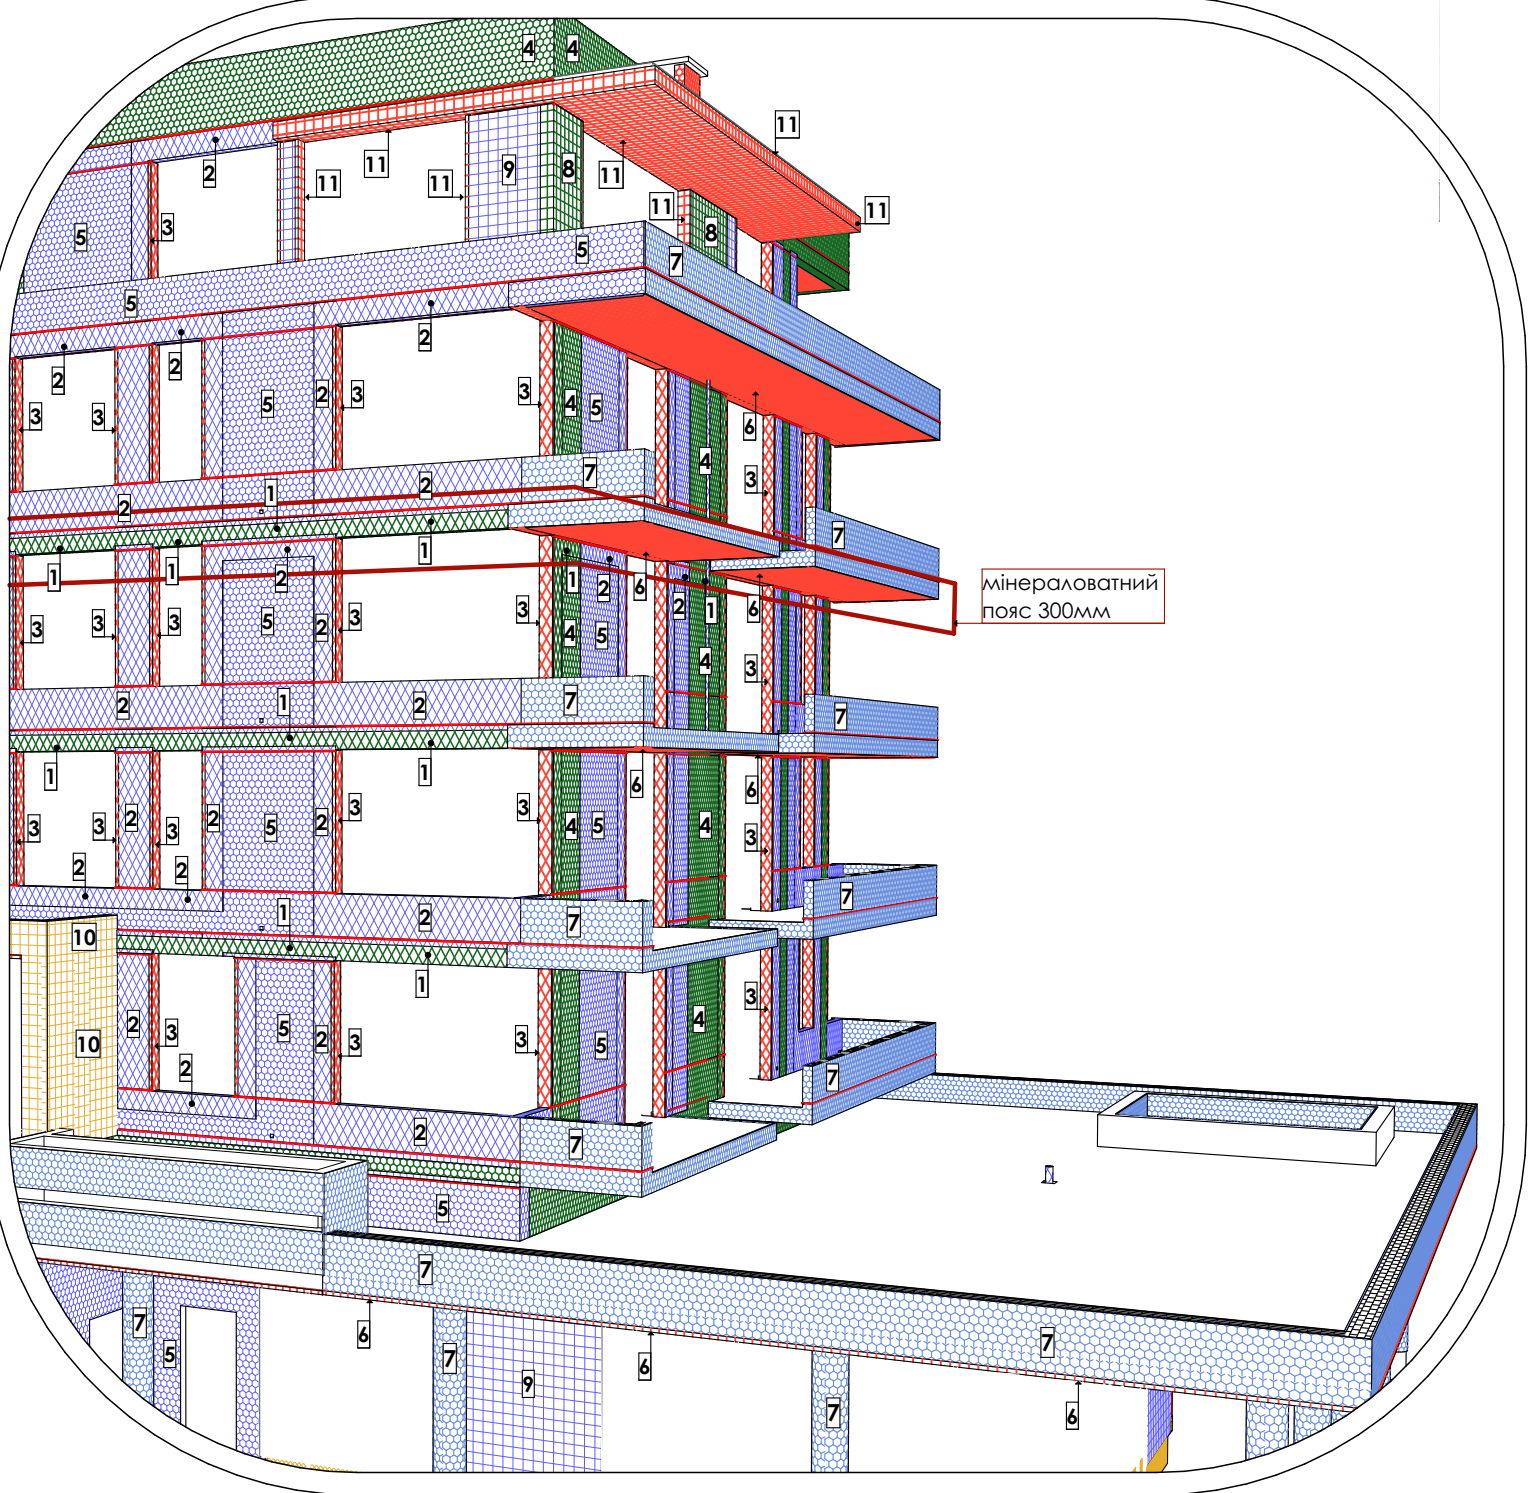
Плити мінераловатні Техновент Стандарт, 150 мм
- 10

Плити мінераловатні Техновент Стандарт, 100 мм
- 11

Плити мінераловатні Техновент Стандарт, 50 мм
- 12

Екструдований пінополістерол, 100 мм
- 13

Стожки К2 для відведення конденсату з зовнішніх блоків кондиціонерів і водовідведення балконів
- Рустовочний профіль 20х20 мм







Позн. маркув.	Найменування	Кіл-сть, м²	Примітки
1	Плити мінераловатні Технофас Оптіма, 200 мм	76	
2	Плити мінераловатні Технофас Оптіма, 150 мм	210	
3	Плити мінераловатні Технофас Оптіма, 50 мм	108	
4	Плити пінополістерольні ПСБ-25, 200 мм	248	
5	Плити пінополістерольні ПСБ-25, 150 мм	295	
6	Плити пінополістерольні ПСБ-25, 50 мм	681	
7	Плити пінополістерольні ПСБ-25, 20 мм	381	
8	Плити мінераловатні Техновент Стандарт, 200 мм	8	
9	Плити мінераловатні Техновент Стандарт, 150 мм	27	
10	Плити мінераловатні Техновент Стандарт, 100 мм	31	
11	Плити мінераловатні Техновент Стандарт, 50 мм	21	
12	Екструдований пінополістерол, 100 мм	52	
14	Теплоізоляційні плити PIR (Г-1), 50 мм	23	
	Рустовочний профіль 20х20 мм	1 570 м.п	


Схема утепления фасаду в осях А-Г М 1:100



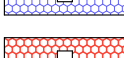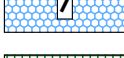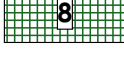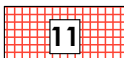Умовні позначення:

	1	Плити мінераловатні Технофас Оптіма, 200 мм
	2	Плити мінераловатні Технофас Оптіма, 150 мм
	3	Плити мінераловатні Технофас Оптіма, 50 мм
	4	Плити пінополістерольні ПСБ-25, 200 мм
	5	Плити пінополістерольні ПСБ-25, 150 мм
	6	Плити пінополістерольні ПСБ-25, 50 мм
	7	Плити пінополістерольні ПСБ-25, 20 мм
	8	Плити мінераловатні Техновент Стандарт, 200 мм
	9	Плити мінераловатні Техновент Стандарт, 150 мм
	10	Плити мінераловатні Техновент Стандарт, 100 мм
	11	Плити мінераловатні Техновент Стандарт, 50 мм
	12	Екструдований пінополістерол, 100 мм
	13	Стояки K2 для відведення конденсату з зовнішніх блоків кондиціонерів і водовідведення балконів
		Рустовочний профіль 20х20 мм

Позн. маркув.	Найменування	Кіл-сть, м²	Примітки
1	Плити мінераловатні Технофас Оптіма, 200 мм	76	
2	Плити мінераловатні Технофас Оптіма, 150 мм	210	
3	Плити мінераловатні Технофас Оптіма, 50 мм	108	
4	Плити пінополістерольні ПСБ-25, 200 мм	248	
5	Плити пінополістерольні ПСБ-25, 150 мм	295	
6	Плити пінополістерольні ПСБ-25, 50 мм	681	
7	Плити пінополістерольні ПСБ-25, 20 мм	381	
8	Плити мінераловатні Техновент Стандарт, 200 мм	8	
9	Плити мінераловатні Техновент Стандарт, 150 мм	27	
10	Плити мінераловатні Техновент Стандарт, 100 мм	31	
11	Плити мінераловатні Техновент Стандарт, 50 мм	21	
12	Екструдований пінополістерол, 100 мм	52	
14	Теплоізоляційні плити PIR (Г-1), 50 мм	23	
	Рустовочний профіль 20х20 мм	1 570 м.п	


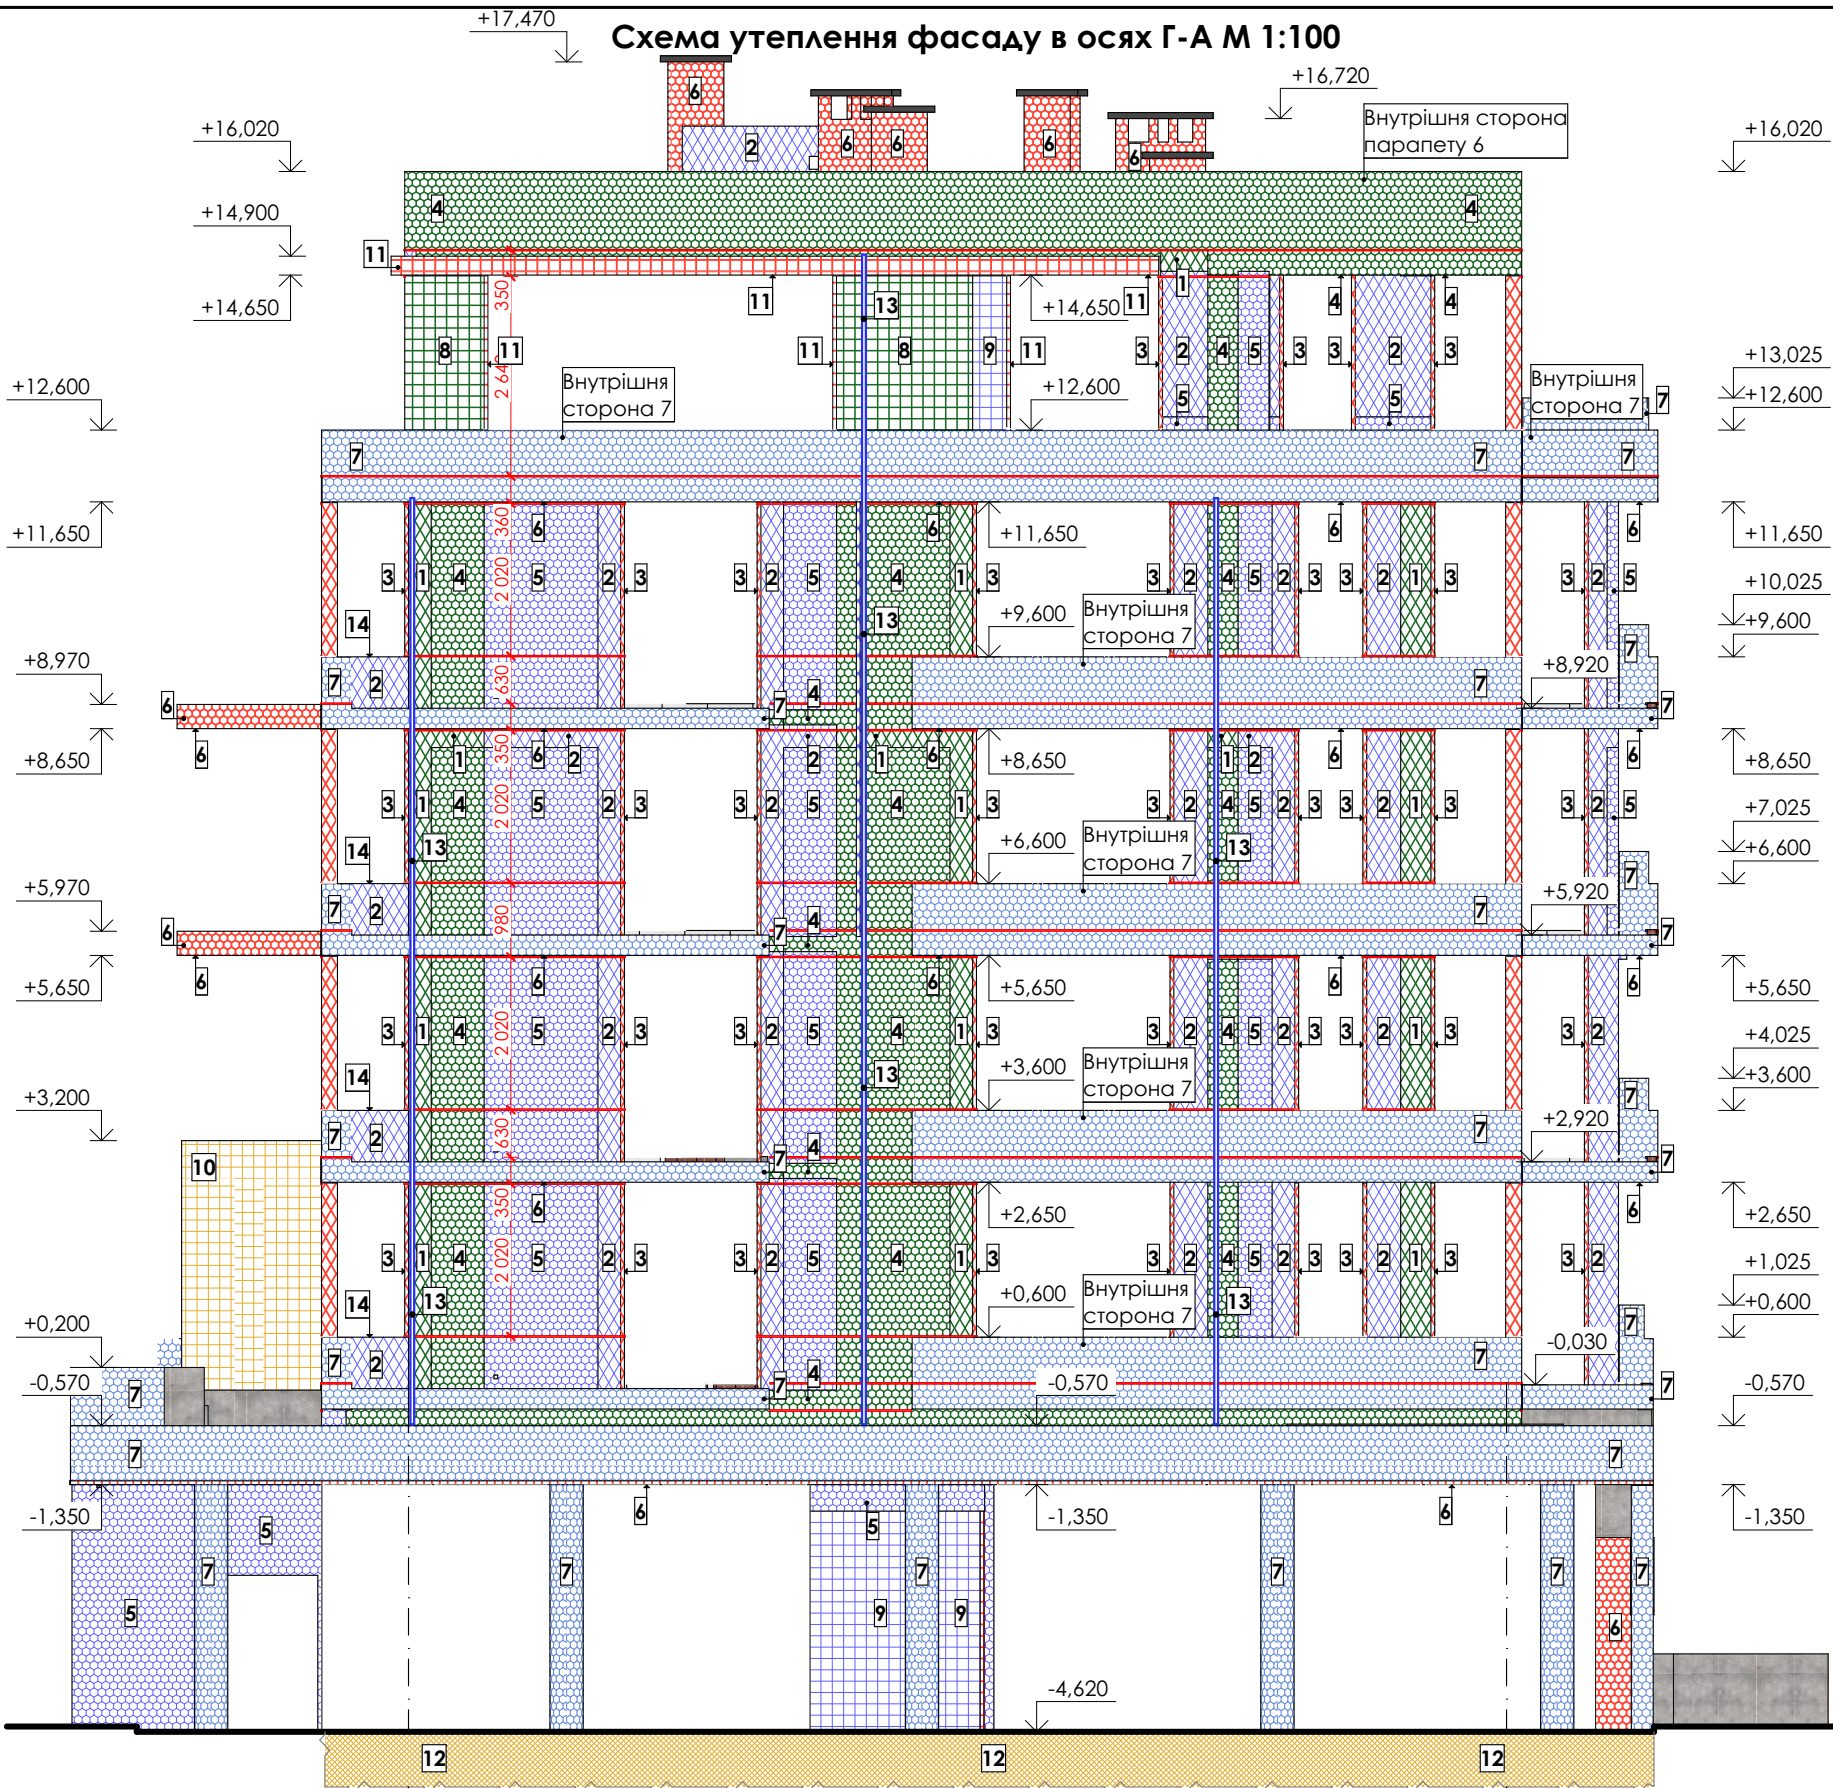



Умовні позначення:

- Плити мінераловатні Технофас Оптіма, 200 мм
- Плити мінераловатні Технофас Оптіма, 150 мм
- Плити мінераловатні Технофас Оптіма, 50 мм
- Плити пінополістерольні ПСБ-25, 200 мм
- Плити пінополістерольні ПСБ-25, 150 мм
- Плити пінополістерольні ПСБ-25, 50 мм
- Плити пінополістерольні ПСБ-25, 20 мм
- Плити мінераловатні Техновент Стандарт, 200 мм
- Плити мінераловатні Техновент Стандарт, 150 мм
- Плити мінераловатні Техновент Стандарт, 100 мм
- Плити мінераловатні Техновент Стандарт, 50 мм
- Екструдований пінополістерол, 100 мм
- Стояки К2 для відведення конденсату з зовнішніх блоків кондиціонерів і водовідведення балконів
- Рустовочний профіль 20х20 мм






Позн. маркув.	Найменування	Кіл-сть, м²	Примітки
1	Плити мінераловатні Технофас Оптіма, 200 мм	76	
2	Плити мінераловатні Технофас Оптіма, 150 мм	210	
3	Плити мінераловатні Технофас Оптіма, 50 мм	108	
4	Плити пінополістерольні ПСБ-25, 200 мм	248	
5	Плити пінополістерольні ПСБ-25, 150 мм	295	
6	Плити пінополістерольні ПСБ-25, 50 мм	681	
7	Плити пінополістерольні ПСБ-25, 20 мм	381	
8	Плити мінераловатні Техновент Стандарт, 200 мм	8	
9	Плити мінераловатні Техновент Стандарт, 150 мм	27	
10	Плити мінераловатні Техновент Стандарт, 100 мм	31	
11	Плити мінераловатні Техновент Стандарт, 50 мм	21	
12	Екструдований пінополістерол, 100 мм	52	
14	Теплоізоляційні плити PIR (Г-1), 50 мм	23	
	Рустовочний профіль 20х20 мм	1 570 м.п	

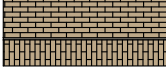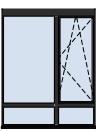Паспорт опорядження фасаду в осях 1-6 М 1:100

Таблиця опорядження фасадів					
Поз. марк.	Елемент фасаду	Матеріал оздоблення	Зразок	№ кольору	Площа м²
1	Зовнішні стіни	Клінкерна фасадна плитка		-	1387
2	Зовнішні стіни	Декоративна фасадна штукатурка		RAL 9003	437
3	Зовнішні стіни	Декоративна фасадна штукатурка		RAL 8025	220
4	Зовнішні стіни	Декоративна фасадна штукатурка		RAL 9011	137
5	Зовнішні стіни	Декоративна фасадна штукатурка		RAL 3016	20
6	Зовнішні стіни	Вентильований фасад з покриттям HPL-панелями Max Compact Exterior		0080 Black	30,3
7	Зовнішні стіни	Вентильований фасад з покриттям HPL-панелями Max Compact Exterior		0923 Enigma	13,7
8	Зовнішні стіни	Профіль опорний HOLZDORF 70X50мм Імпрес		Бук	287 м.п
9	Зовнішні стіни	Вентильований фасад з покриттям композитною панеллю ECOBOND		RAL 3113 (графіт)	27,5
10	Перегородки балконні	Металевий каркас обшитий HPL-панелями Max Compact Exterior		RAL 7016 (антрацит)	105,4
11	Огородження	Пофарбування металевих виробів		RAL 3016	
12	Огородження	Пофарбування металевих виробів		RAL 7016 (антрацит)	
13	Фасонні елементи	Готові фарбовані металеві елементи		RAL 7016 (антрацит)	
14	Фасонні елементи	Готові фарбовані металеві елементи		RAL 3016	
15	Фасонні елементи	Готові фарбовані металеві елементи		RAL 8025	
16	Корзини під кондиціонери	Екран HPL-панель		RAL 9011	
17	Зовнішні стіни	Вентильований фасад з покриттям композитною панеллю ECOBOND		RAL 7016 (антрацит)	58,5
18	Рами віконних, дверних блоків та вітрин	Металопластикові вироби/Алюмінієві вироби		Зовні RAL 7016 Всередині RAL 9003	Алюмінієві вироби RAL 7016



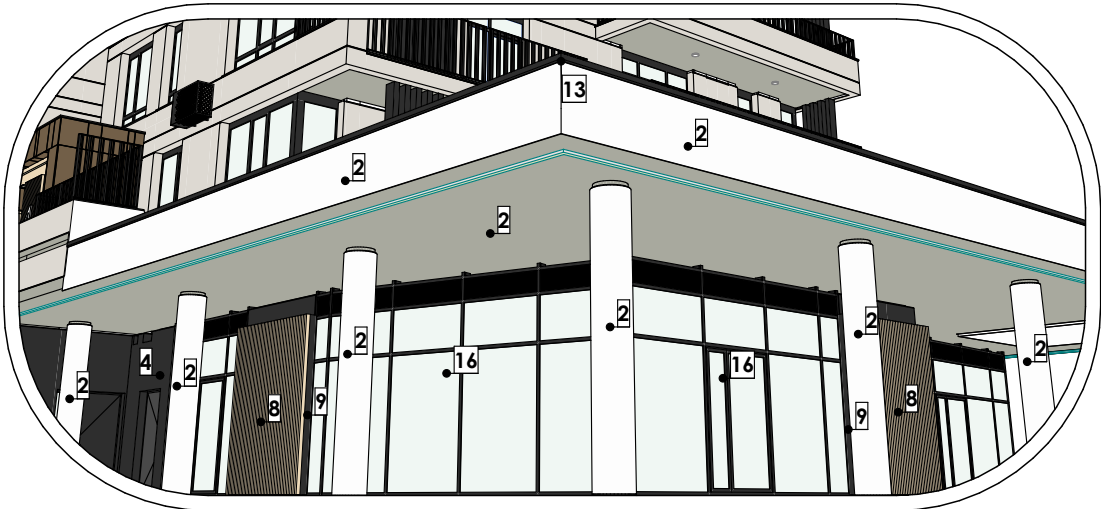


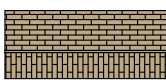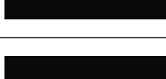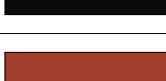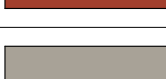
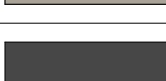
Паспорт опорядження фасаду в осях 6-1 М 1:100

Таблиця опорядження фасадів					
Поз. марк.	Елемент фасаду	Матеріал оздоблення	Зразок	№ кольору	Площа м²
1	Зовнішні стіни	Клінкерна фасадна плитка		-	1387
2	Зовнішні стіни	Декоративна фасадна штукатурка		RAL 9003	437
3	Зовнішні стіни	Декоративна фасадна штукатурка		RAL 8025	220
4	Зовнішні стіни	Декоративна фасадна штукатурка		RAL 9011	137
5	Зовнішні стіни	Декоративна фасадна штукатурка		RAL 3016	20
6	Зовнішні стіни	Вентильований фасад з покриттям HPL-панелями Max Contrast Exterior		0080 Black	30,3
7	Зовнішні стіни	Вентильований фасад з покриттям HPL-панелями Max Contrast Exterior		0923 Enigma	13,7
8	Зовнішні стіни	Профіль опорний HOLZDORF 70X50мм Імпрес		Бук	287 м.п
9	Зовнішні стіни	Вентильований фасад з покриттям композитною панеллю ECOBOND		RAL 3113 (графіт)	27,5
10	Перегородки балконні	Металевий каркас обшитий HPL-панелями Max Contrast Exterior		RAL 7016 (антрацит)	105,4
11	Огородження	Пофарбування металевих виробів		RAL 3016	
12	Огородження	Пофарбування металевих виробів		RAL 7016 (антрацит)	
13	Фасонні елементи	Готові фарбовані металеві елементи		RAL 7016 (антрацит)	
14	Фасонні елементи	Готові фарбовані металеві елементи		RAL 3016	
15	Фасонні елементи	Готові фарбовані металеві елементи		RAL 8025	
16	Корзини під кондиціонери	Екран HPL-панель		RAL 9011	
17	Зовнішні стіни	Вентильований фасад з покриттям композитною панеллю ECOBOND		RAL 7016 (антрацит)	58,5
18	Рами віконних, дверних блоків та вітрин	Металопластикові вироби/Алюмінієві вироби		Ззовні RAL 7016 Всередині RAL 9003	Алюмінієві вироби RAL 7016




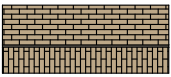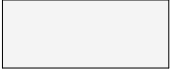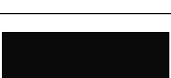
Паспорт опорядження фасаду в осях А-Г М 1:100

Таблиця опорядження фасадів					
Поз. марк.	Елемент фасаду	Матеріал оздоблення	Зразок	№ кольору	Площа м²
1	Зовнішні стіни	Клінкерна фасадна плитка		-	1387
2	Зовнішні стіни	Декоративна фасадна штукатурка		RAL 9003	437
3	Зовнішні стіни	Декоративна фасадна штукатурка		RAL 8025	220
4	Зовнішні стіни	Декоративна фасадна штукатурка		RAL 9011	137
5	Зовнішні стіни	Декоративна фасадна штукатурка		RAL 3016	20
6	Зовнішні стіни	Вентильований фасад з покриттям HPL-панелями Max Compact Exterior		0080 Black	30,3
7	Зовнішні стіни	Вентильований фасад з покриттям HPL-панелями Max Compact Exterior		0923 Enigma	13,7
8	Зовнішні стіни	Профіль опорний HOLZDORF 70X50мм Імпрес		Бук	287 м.п
9	Зовнішні стіни	Вентильований фасад з покриттям композитною панеллю ECOBOND		RAL 3113 (графіт)	27,5
10	Перегородки балконні	Металевий каркас обшитий HPL-панелями Max Compact Exterior		RAL 7016 (антрацит)	105,4
11	Огородження	Пофарбування металевих виробів		RAL 3016	
12	Огородження	Пофарбування металевих виробів		RAL 7016 (антрацит)	
13	Фасонні елементи	Готові фарбовані металеві елементи		RAL 7016 (антрацит)	
14	Фасонні елементи	Готові фарбовані металеві елементи		RAL 3016	
15	Фасонні елементи	Готові фарбовані металеві елементи		RAL 8025	
16	Корзини під кондиціонери	Екран HPL-панель		RAL 9011	
17	Зовнішні стіни	Вентильований фасад з покриттям композитною панеллю ECOBOND		RAL 7016 (антрацит)	58,5
18	Рами віконних, дверних блоків та вітрин	Металопластикові вироби/Алюмінієві вироби		Ззовні RAL 7016 Всередині RAL 9003	Алюмінієві вироби RAL 7016





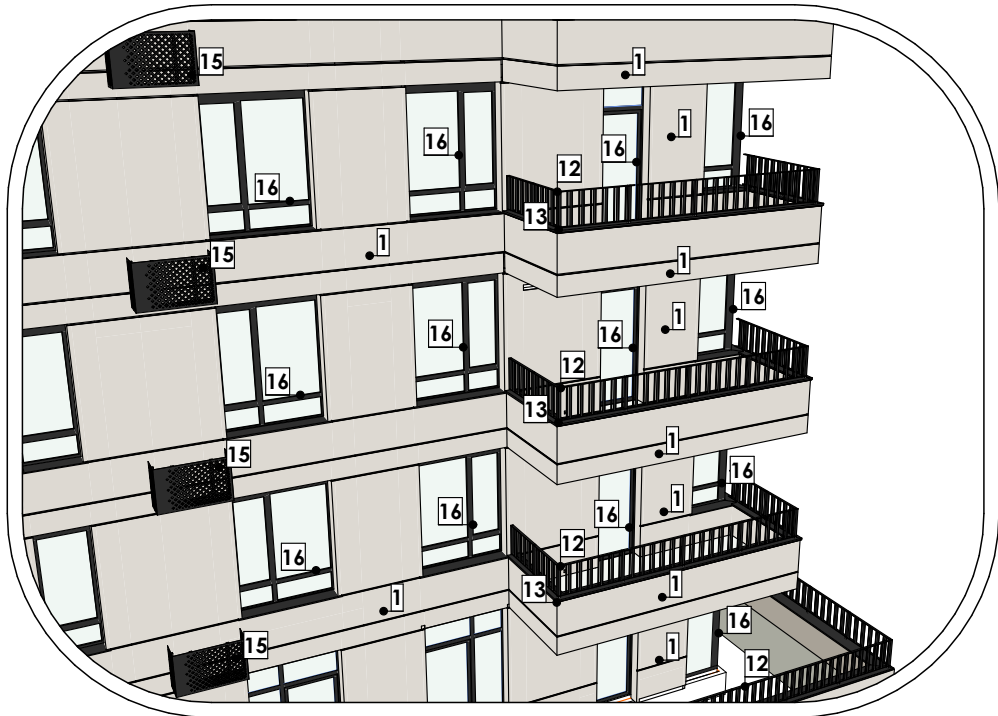
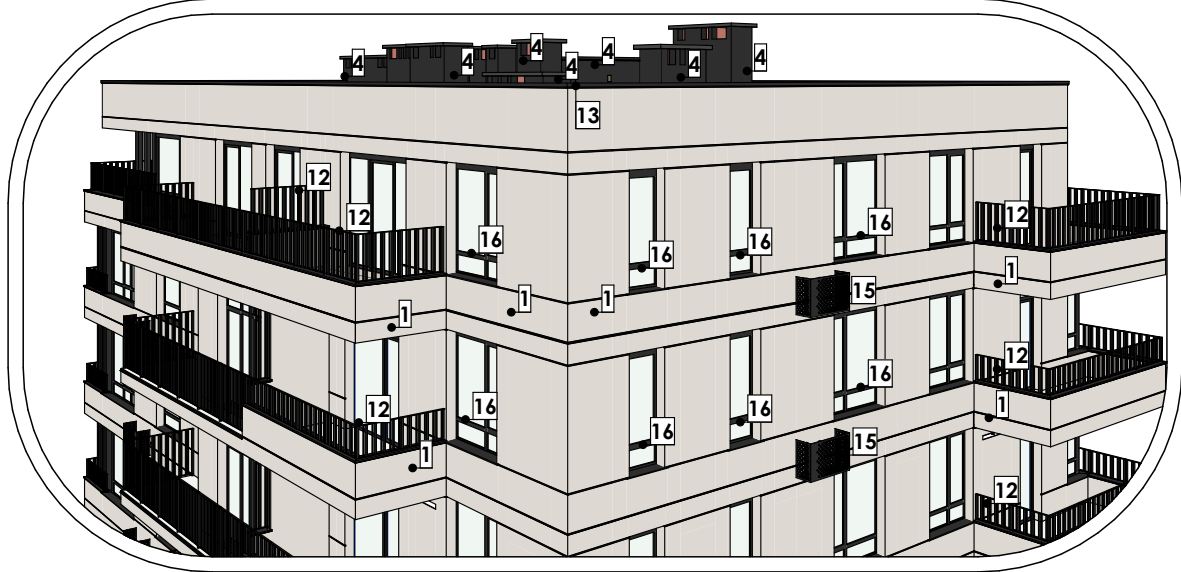


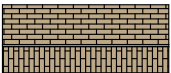Паспорт опорядження фасаду в осях Г-А М 1:100

Таблиця опорядження фасадів					
Поз. марк.	Елемент фасаду	Матеріал оздоблення	Зразок	№ кольору	Площа м²
1	Зовнішні стіни	Клінкерна фасадна плитка		-	1387
2	Зовнішні стіни	Декоративна фасадна штукатурка		RAL 9003	437
3	Зовнішні стіни	Декоративна фасадна штукатурка		RAL 8025	220
4	Зовнішні стіни	Декоративна фасадна штукатурка		RAL 9011	137
5	Зовнішні стіни	Декоративна фасадна штукатурка		RAL 3016	20
6	Зовнішні стіни	Вентилюваний фасад з покриттям HPL-панелями Max Compact Exterior		0080 Black	30,3
7	Зовнішні стіни	Вентилюваний фасад з покриттям HPL-панелями Max Compact Exterior		0923 Enigma	13,7
8	Зовнішні стіни	Профіль опорний HOLZDORF 70X50мм Імпрес		Бук	287 м.п
9	Зовнішні стіни	Вентилюваний фасад з покриттям композитною панеллю ECOBOND		RAL 3113 (графіт)	27,5
10	Перегородки балконні	Металевий каркас обшитий HPL-панелями Max Compact Exterior		RAL 7016 (антрацит)	105,4
11	Огородження	Пофарбування металевих виробів		RAL 3016	
12	Огородження	Пофарбування металевих виробів		RAL 7016 (антрацит)	
13	Фасонні елементи	Готові фарбовані металеві елементи		RAL 7016 (антрацит)	
14	Фасонні елементи	Готові фарбовані металеві елементи		RAL 3016	
15	Фасонні елементи	Готові фарбовані металеві елементи		RAL 8025	
16	Корзини під кондиціонери	Екран HPL-панель		RAL 9011	
17	Зовнішні стіни	Вентилюваний фасад з покриттям композитною панеллю ECOBOND		RAL 7016 (антрацит)	58,5
18	Рами віконних, дверних блоків та вітрин	Металопластикові вироби/Алюмінієві вироби		Ззовні RAL 7016 Всередині RAL 9003	Алюмінієві вироби RAL 7016

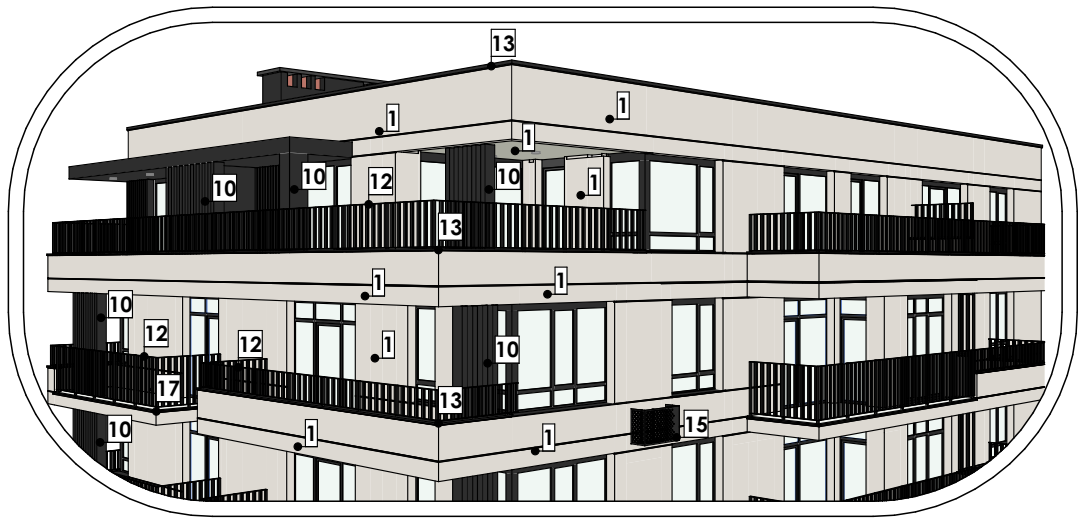

Відомість фасонних елементів

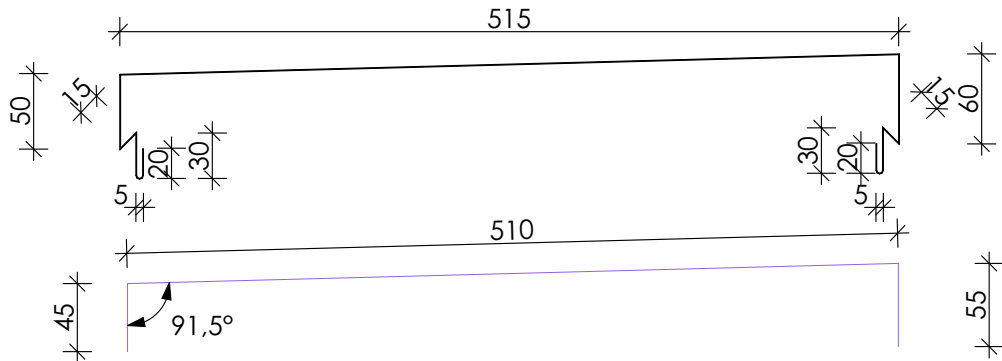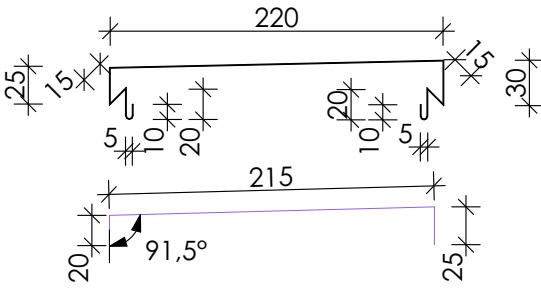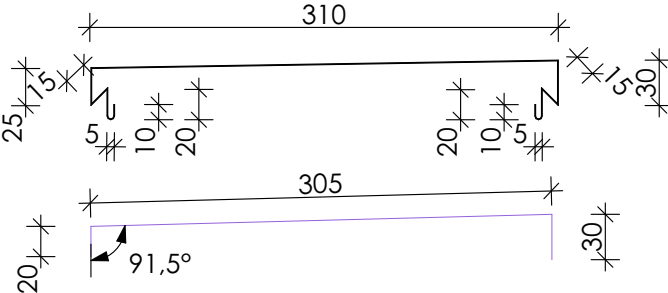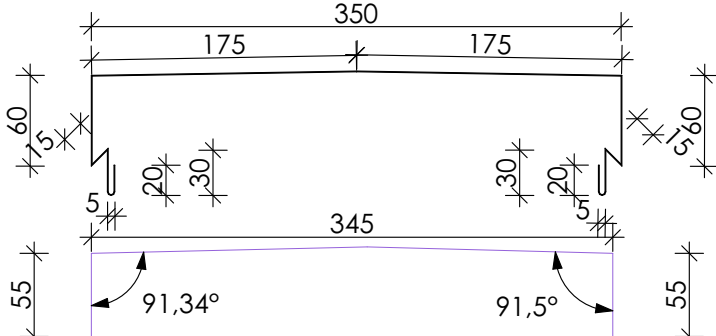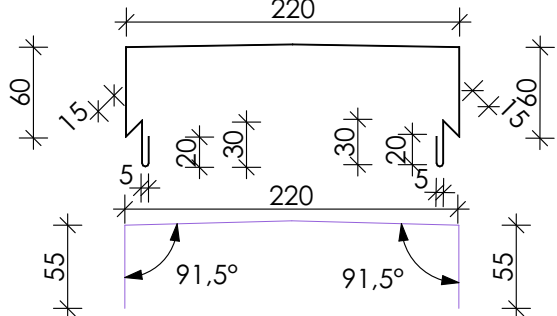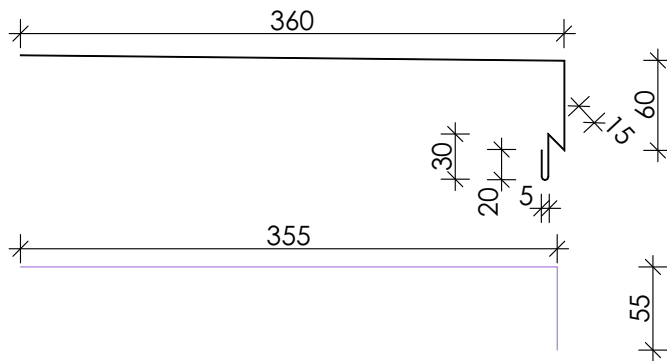Марка	Ескіз	м.п. крапельників / к-сть костилів	Колір	Штрипс, мм	Довжина, мм	Примітки
Ф-1		Крапельник: 23,14; Костиль: 78	RAL 7021	Крапельник: 765; Костиль: 610	23 132	
Ф-2		Крапельник: 136,19; Костиль: 477	RAL 7021	Крапельник: 375; Костиль: 260	135 836	
Ф-3		Крапельник: 72,32; Костиль: 250	RAL 7021	Крапельник: 340; Костиль: 350	75 257	
Ф-4		Крапельник: 55,56; Костиль: 186	RAL 7021	Крапельник: 590; Костиль: 435	55 523	
Ф-4.1		Крапельник: 6,96; Костиль: 24	RAL 7021	Крапельник: 375; Костиль: 260	6 957	
Ф-5		Крапельник: 23,02; Костиль: 80	RAL 7021	Крапельник: 490; Костиль: 410	22 930	

Відомість внутрішнього опорядження

Найменування приміщення згідно експлікації				№ по експлікації	Висота,м	Стеля			Стіни			Низ стін та перегородок				
Відм. поверху						Основа	Вид покриття	Площа, м2	Основа			Площа, м2	Основа	Вид покриття	Висота, м	Площа, м2
1	2	3	4	5	6	7	8	9	10	11	12	13	14			
Поверх на відм. -4,600																
-4,550	Електрощитова	5.2	4,150	Монолітна плита перекриття	1. Затирка бетонної поверхні цементно-піщаним розчином 2. Шпаклювання гіпсовими сумішами 3. Фінішний шар оздоблення згідно дизайн проекту	5,24	3/6 стіни, колони	1. Затирка бетонної поверхні ц/п розчином 2. Фінішний шар оздоблення згідно дизайн проекту	9,84	3/6 стіни, колони	Керамічна плитка на клею	0,1	0,98			
							Стіни, газоблок	1. Шпаклювання сумішшю для газобетону 2. Фінішний шар оздоблення згідно дизайн проекту	20,67	Стіни, газоблок						
							Цегла, стіни і канали	1. Штукатурка ц/п розчином 2. Фінішний шар оздоблення згідно дизайн проекту	12,32	Цегла, стіни і канали						
-4,600	Тамбуру-шлюз 1-го типу, Тамбур (комора для мешканців будинку), Комора для мешканців будинку №2, Комора для мешканців будинку №1, Тамбур, Комора для мешканців будинку №3, Комора для мешканців будинку №4, Коридор, Пожежний пост, Санвузол	0.1; 3.1; 3.2; 3.3; 4.1; 4.2; 4.3; 5.1; 5.4; 5.5	4,300	Монолітна плита перекриття	1. Затирка бетонної поверхні цементно-піщаним розчином 2. Шпаклювання гіпсовими сумішами 3. Фінішний шар оздоблення згідно дизайн проекту	65,65	3/6 стіни, колони	1. Затирка бетонної поверхні ц/п розчином 2. Фінішний шар оздоблення згідно дизайн проекту	184,72	3/6 стіни, колони	Керамічна плитка на клею	0,1	7,97			
							Стіни, газоблок	1. Шпаклювання сумішшю для газобетону 2. Фінішний шар оздоблення згідно дизайн проекту	103,13	Стіни, газоблок						
							Цегла, стіни і канали	1. Штукатурка ц/п розчином 2. Фінішний шар оздоблення згідно дизайн проекту	85,12	Цегла, стіни і канали						
-4,620	Вузол вводу	5.3	4,320	Монолітна плита перекриття	1. Затирка бетонної поверхні цементно-піщаним розчином 2. Шпаклювання гіпсовими сумішами 3. Фінішний шар оздоблення згідно дизайн проекту	7,30	3/6 стіни, колони	1. Затирка бетонної поверхні ц/п розчином 2. Фінішний шар оздоблення згідно дизайн проекту	12,83	3/6 стіни, колони	Керамічна плитка на клею	0,1	1,07			
							Стіни, газоблок	1. Шпаклювання сумішшю для газобетону 2. Фінішний шар оздоблення згідно дизайн проекту	9,42	Стіни, газоблок						
							Цегла, стіни і канали	1. Штукатурка ц/п розчином 2. Фінішний шар оздоблення згідно дизайн проекту	26,44	Цегла, стіни і канали						
Відм. поверху	Найменування приміщення згідно експлікації	№ по експлікації	Висота,м	Стеля			Стіни			Низ стін та перегородок						
1	2	3	4	5	6	7	8	9	10	11	12	13	14			
Поверх на відм. 0,000																
0,000	Тамбур, Сходова клітка СК 1, Коридор	0.1; 0.2; 0.3	2,700	Монолітна плита, низ сходового маршу	1. Затирка бетонної поверхні цементно-піщаним розчином 2. Шпаклювання гіпсовими сумішами 3. Фінішний шар оздоблення згідно дизайн проекту	63,29	3/6 стіни, колони	1. Затирка бетонної поверхні ц/п розчином 2. Фінішний шар оздоблення згідно дизайн проекту	50,79	3/6 стіни, колони	Керамічна плитка на клею	0,1	5,09			
							Стіни, газоблок	1. Шпаклювання сумішшю для газобетону 2. Фінішний шар оздоблення згідно дизайн проекту	50,86	Стіни, газоблок						
							Цегла, стіни і канали	1. Штукатурка ц/п розчином 2. Фінішний шар оздоблення згідно дизайн проекту	9,71	Цегла, стіни і канали						
							Гіпсокартон, стіни	1. Шпаклювання сумішшю для гіпсокартону 2. Фінішний шар оздоблення згідно дизайн проекту	1,92	Гіпсокартон, стіни						
Відм. поверху	Найменування приміщення згідно експлікації	№ по експлікації	Висота,м	Стеля			Стіни			Низ стін та перегородок						
1	2	3	4	5	6	7	8	9	10	11	12	13	14			
Поверх на відм. +3, 000																
3,000	Сходова клітка СК 1, Коридор	0.1; 0.2	2,700	Монолітна плита, низ сходового маршу	1. Затирка бетонної поверхні цементно-піщаним розчином 2. Шпаклювання гіпсовими сумішами 3. Фінішний шар оздоблення згідно дизайн проекту	38,11	3/6 стіни, колони	1. Затирка бетонної поверхні ц/п розчином 2. Фінішний шар оздоблення згідно дизайн проекту	48,65	3/6 стіни, колони	Керамічна плитка на клею	0,1	3,87			
							Стіни, газоблок	1. Шпаклювання сумішшю для газобетону 2. Фінішний шар оздоблення згідно дизайн проекту	39,82	Стіни, газоблок						
							Цегла, стіни і канали	1. Штукатурка ц/п розчином 2. Фінішний шар оздоблення згідно дизайн проекту	15,63	Цегла, стіни і канали						
							Гіпсокартон, стіни	1. Шпаклювання сумішшю для гіпсокартону 2. Фінішний шар оздоблення згідно дизайн проекту	1,92	Гіпсокартон, стіни						
Відм. поверху	Найменування приміщення згідно експлікації	№ по експлікації	Висота,м	Стеля			Стіни			Низ стін та перегородок						
1	2	3	4	5	6	7	8	9	10	11	12	13	14			
Поверх на відм. +6, 000																
+6, 000	Сходова клітка СК 1, Коридор	0.1; 0.2	2,700	Монолітна плита перекриття	1. Затирка бетонної поверхні цементно-піщаним розчином 2. Шпаклювання гіпсовими сумішами 3. Фінішний шар оздоблення згідно дизайн проекту	38,11	3/6 стіни, колони	1. Затирка бетонної поверхні ц/п розчином 2. Фінішний шар оздоблення згідно дизайн проекту	48,65	3/6 стіни, колони	Керамічна плитка на клею	0,1	3,87			
							Стіни, газоблок	1. Шпаклювання сумішшю для газобетону 2. Фінішний шар оздоблення згідно дизайн проекту	39,82	Стіни, газоблок						
							Цегла, стіни і канали	1. Штукатурка ц/п розчином 2. Фінішний шар оздоблення згідно дизайн проекту	15,63	Цегла, стіни і канали						
							Гіпсокартон, стіни	1. Шпаклювання сумішшю для гіпсокартону 2. Фінішний шар оздоблення згідно дизайн проекту	1,92	Гіпсокартон, стіни						
Відм. поверху	Найменування приміщення згідно експлікації	№ по експлікації	Висота,м	Стеля			Стіни			Низ стін та перегородок						
1	2	3	4	5	6	7	8	9	10	11	12	13	14			
Поверх на відм. +9, 000																
+9, 000	Сходова клітка СК 1, Коридор	0.1; 0.2	2,700	Монолітна плита перекриття	1. Затирка бетонної поверхні цементно-піщаним розчином 2. Шпаклювання гіпсовими сумішами 3. Фінішний шар оздоблення згідно дизайн проекту	38,11	3/6 стіни, колони	1. Затирка бетонної поверхні ц/п розчином 2. Фінішний шар оздоблення згідно дизайн проекту	48,65	3/6 стіни, колони	Керамічна плитка на клею	0,1	3,87			
							Стіни, газоблок	1. Шпаклювання сумішшю для газобетону 2. Фінішний шар оздоблення згідно дизайн проекту	39,82	Стіни, газоблок						
							Цегла, стіни і канали	1. Штукатурка ц/п розчином 2. Фінішний шар оздоблення згідно дизайн проекту	15,63	Цегла, стіни і канали						
							Гіпсокартон, стіни	1. Шпаклювання сумішшю для гіпсокартону 2. Фінішний шар оздоблення згідно дизайн проекту	1,92	Гіпсокартон, стіни						
Відм. поверху	Найменування приміщення згідно експлікації	№ по експлікації	Висота,м	Стеля			Стіни			Низ стін та перегородок						
1	2	3	4	5	6	7	8	9	10	11	12	13	14			
Поверх на відм. +12, 000																
+12, 000	Сходова клітка СК 1, Коридор	0.1; 0.2	2,700	Монолітна плита перекриття	1. Затирка бетонної поверхні цементно-піщаним розчином 2. Шпаклювання гіпсовими сумішами 3. Фінішний шар оздоблення згідно дизайн проекту	38,11	3/6 стіни, колони	1. Затирка бетонної поверхні ц/п розчином 2. Фінішний шар оздоблення згідно дизайн проекту	56,41	3/6 стіни, колони	Керамічна плитка на клею	0,1	3,87			
							Стіни, газоблок	1. Шпаклювання сумішшю для газобетону 2. Фінішний шар оздоблення згідно дизайн проекту	45,53	Стіни, газоблок						
							Цегла, стіни і канали	1. Штукатурка ц/п розчином 2. Фінішний шар оздоблення згідно дизайн проекту	15,63	Цегла, стіни і канали						
							Гіпсокартон, стіни	1. Шпаклювання сумішшю для гіпсокартону 2. Фінішний шар оздоблення згідно дизайн проекту	1,92	Гіпсокартон, стіни						